




ŘEZ 1-1 1: 25

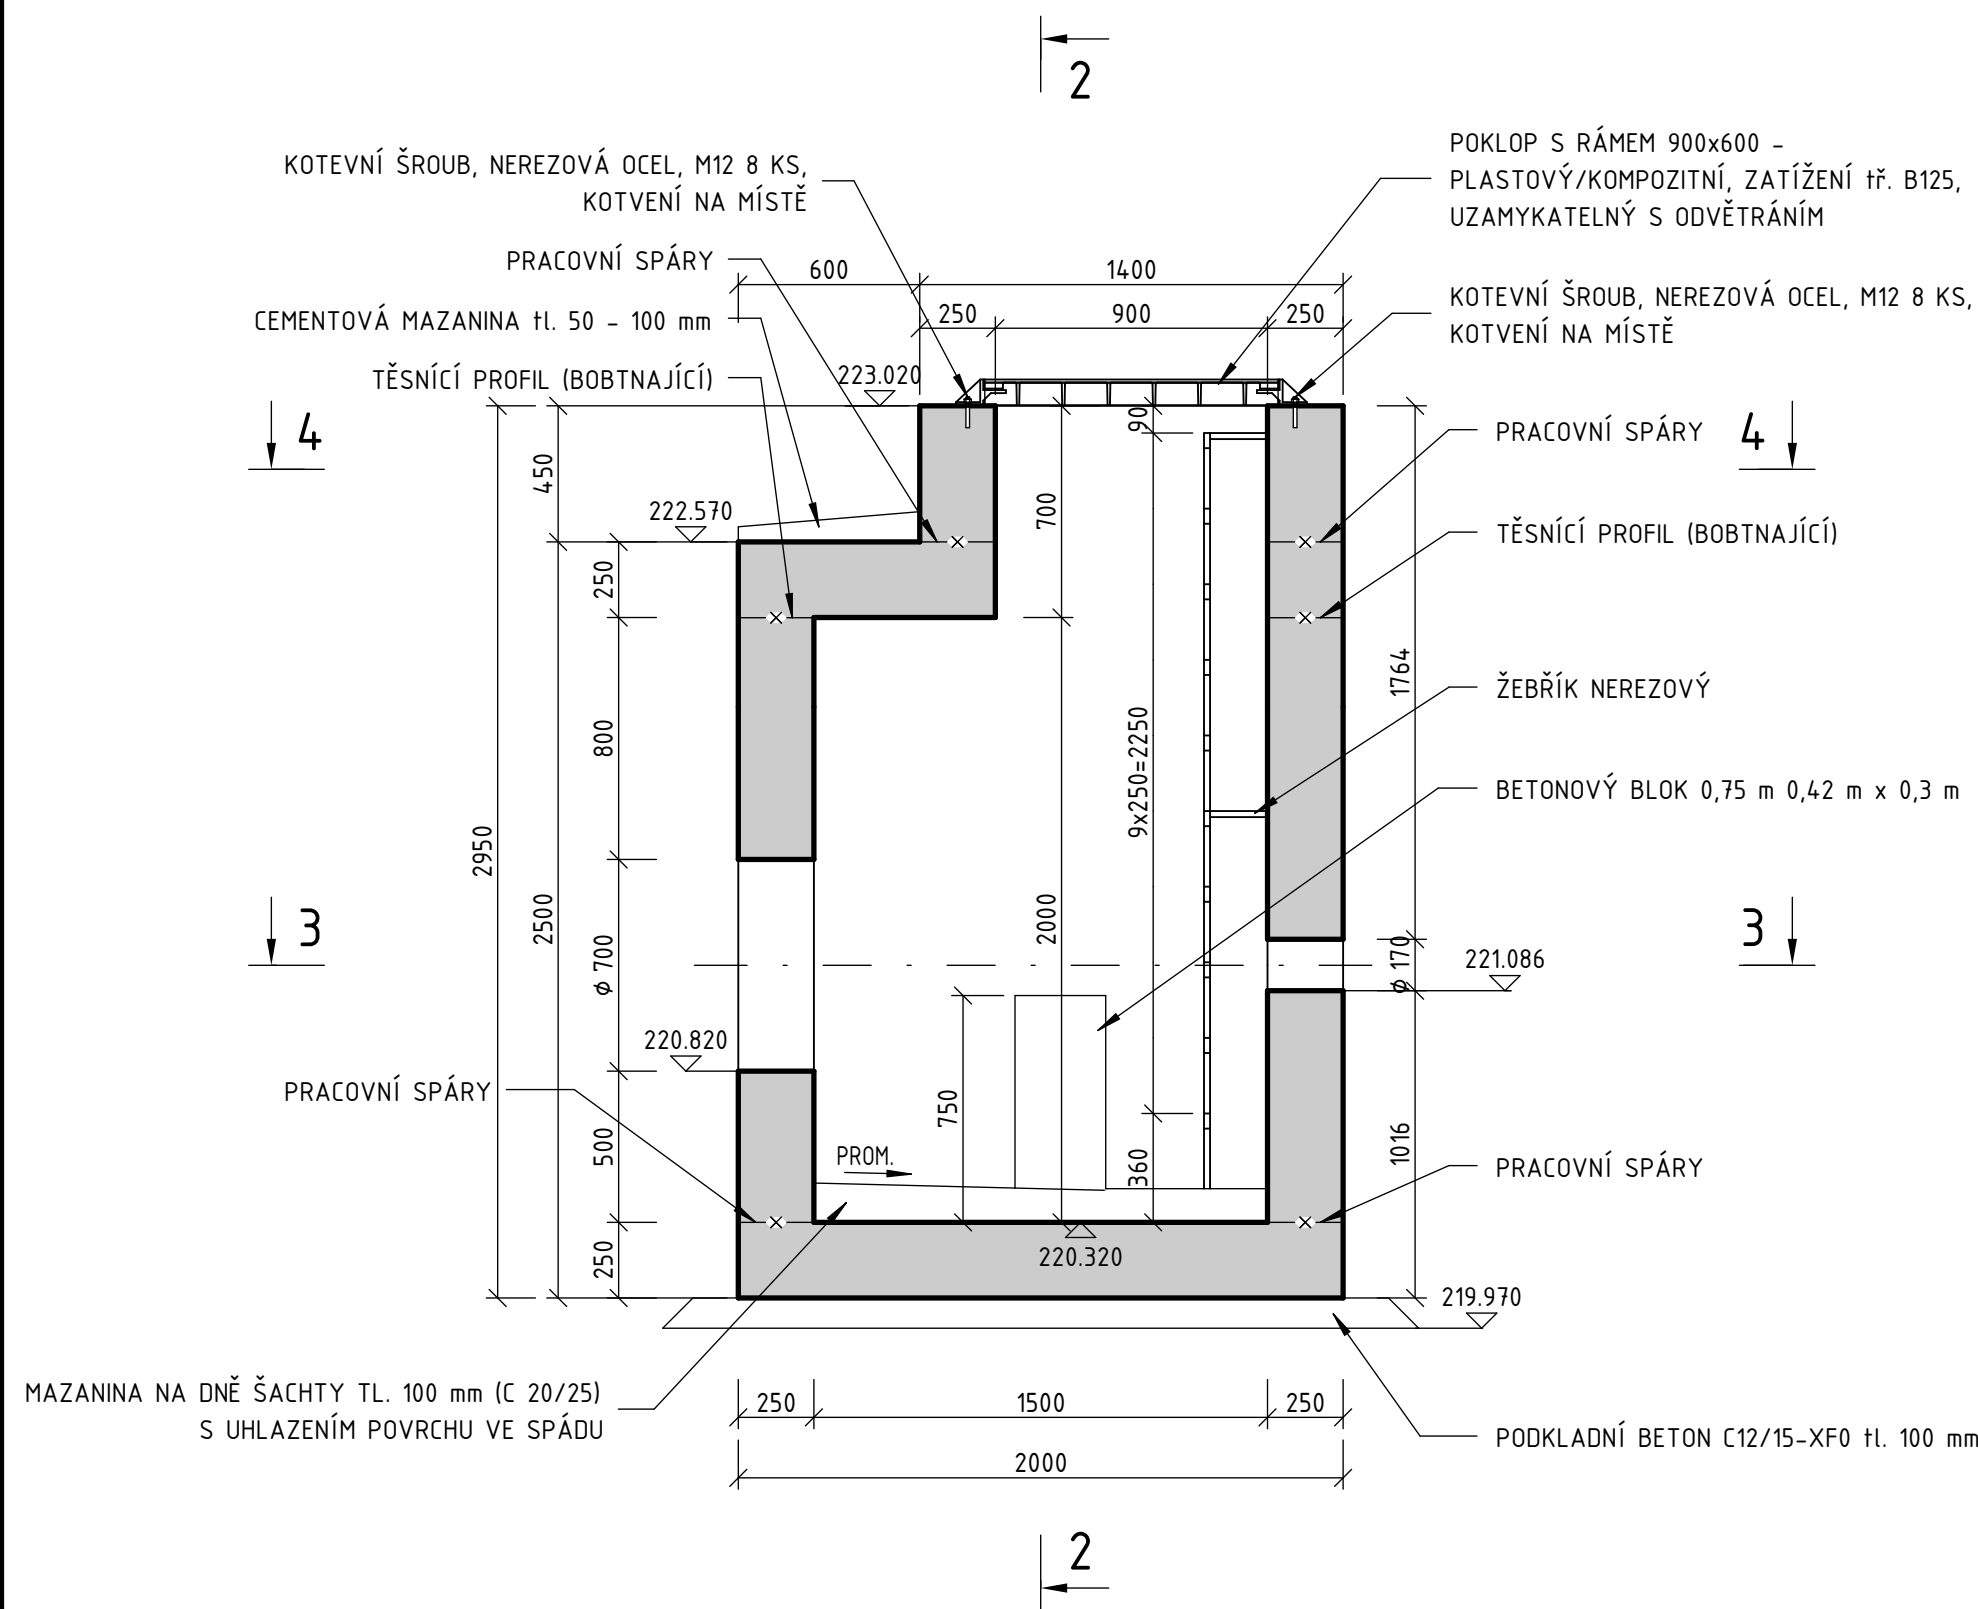


ŘEZ 2-2 1: 25

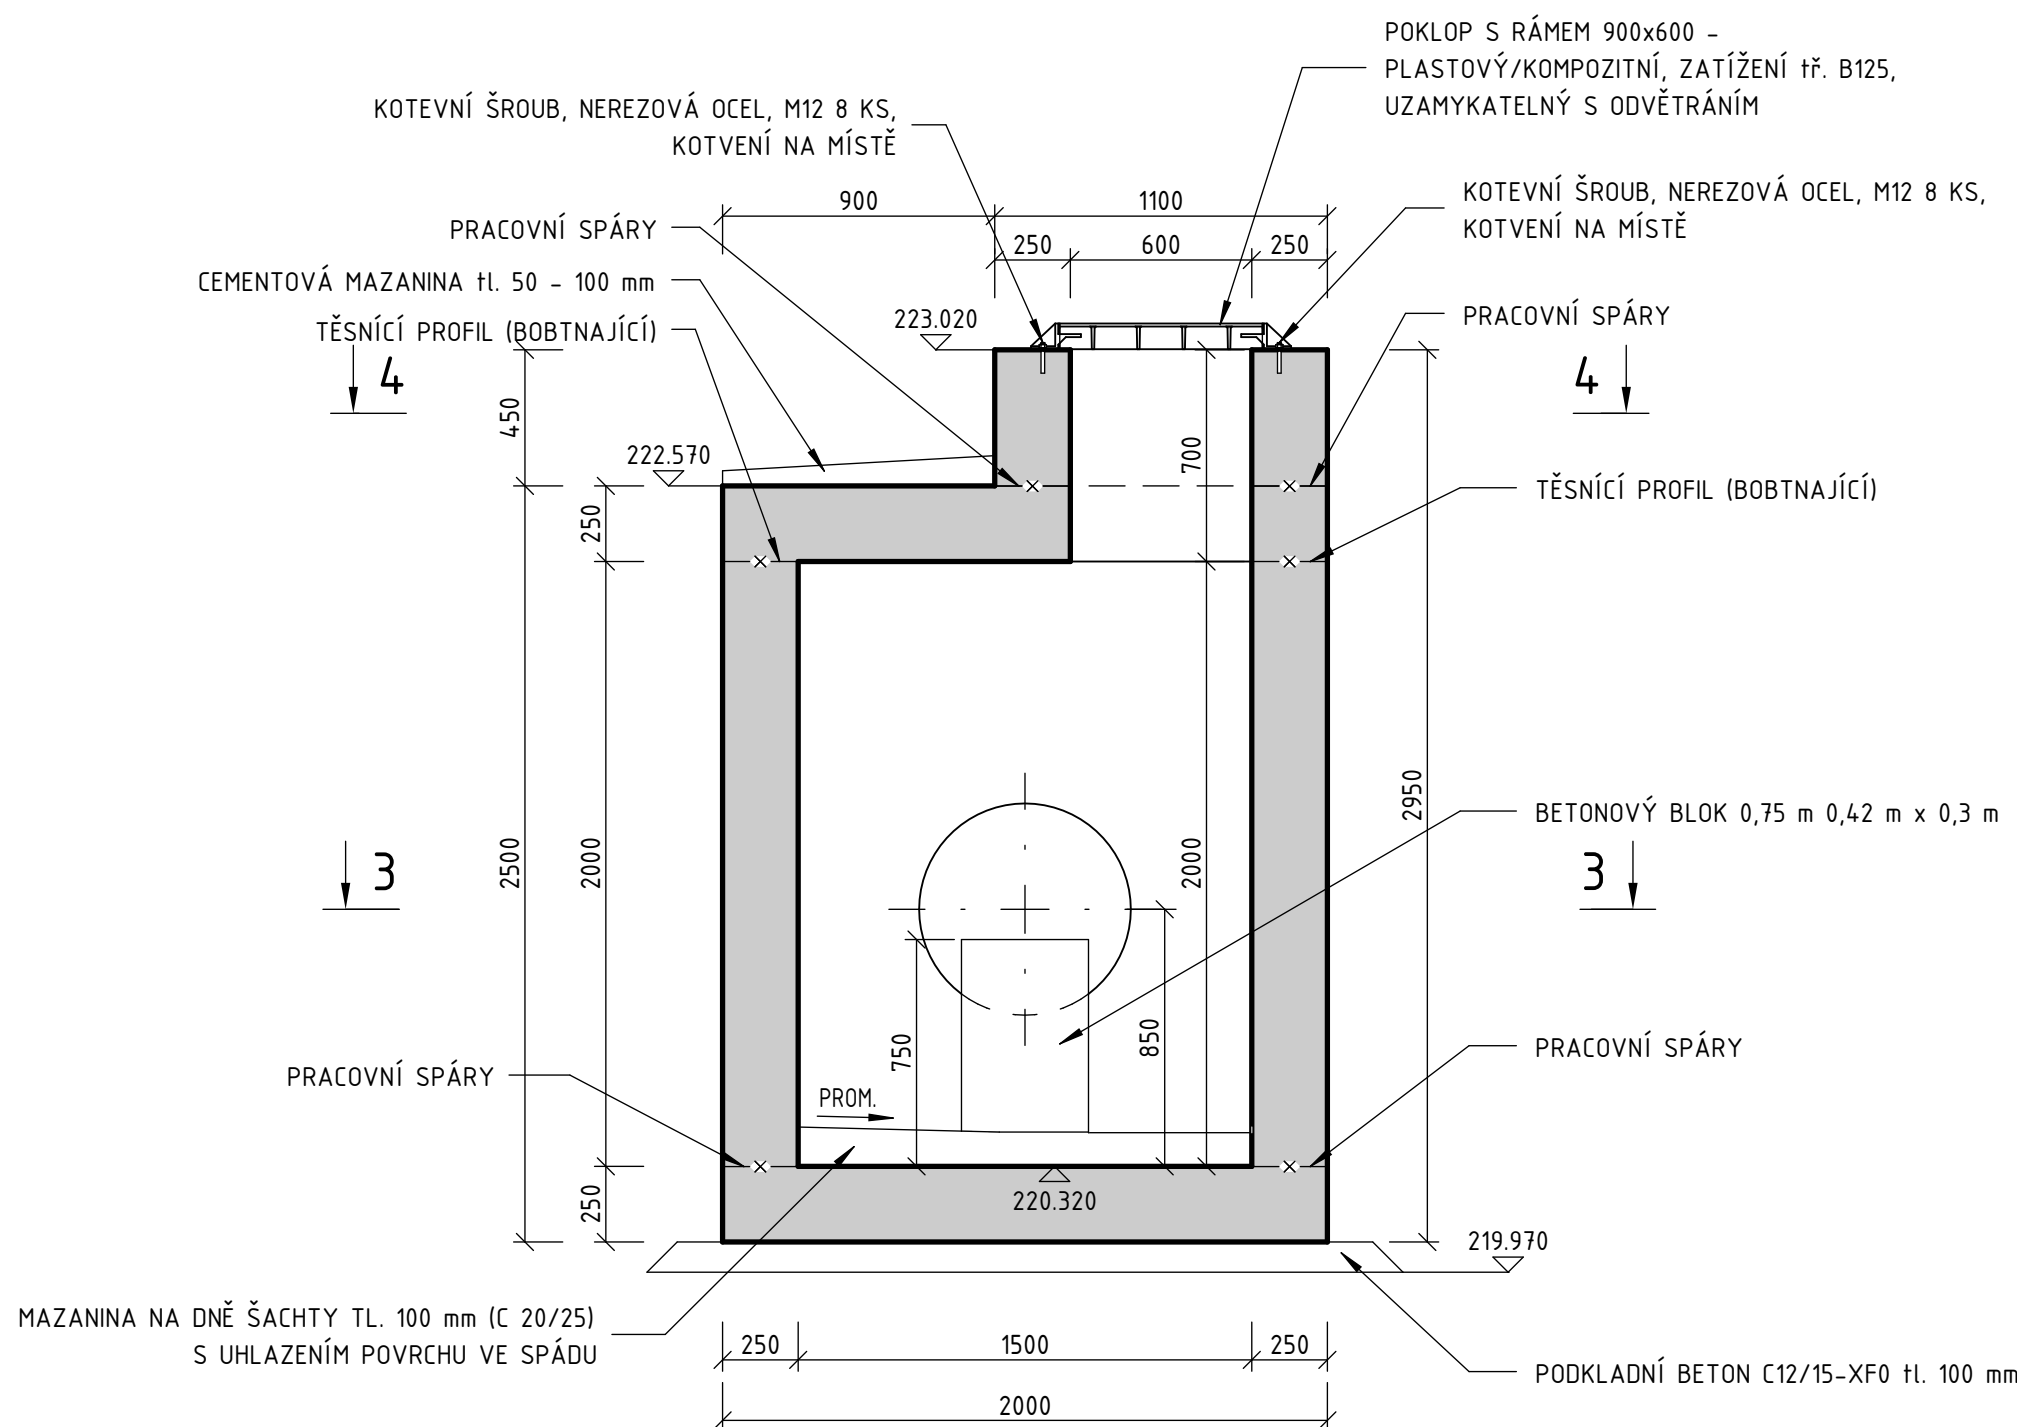

ŘEZ 3-3 1: 25

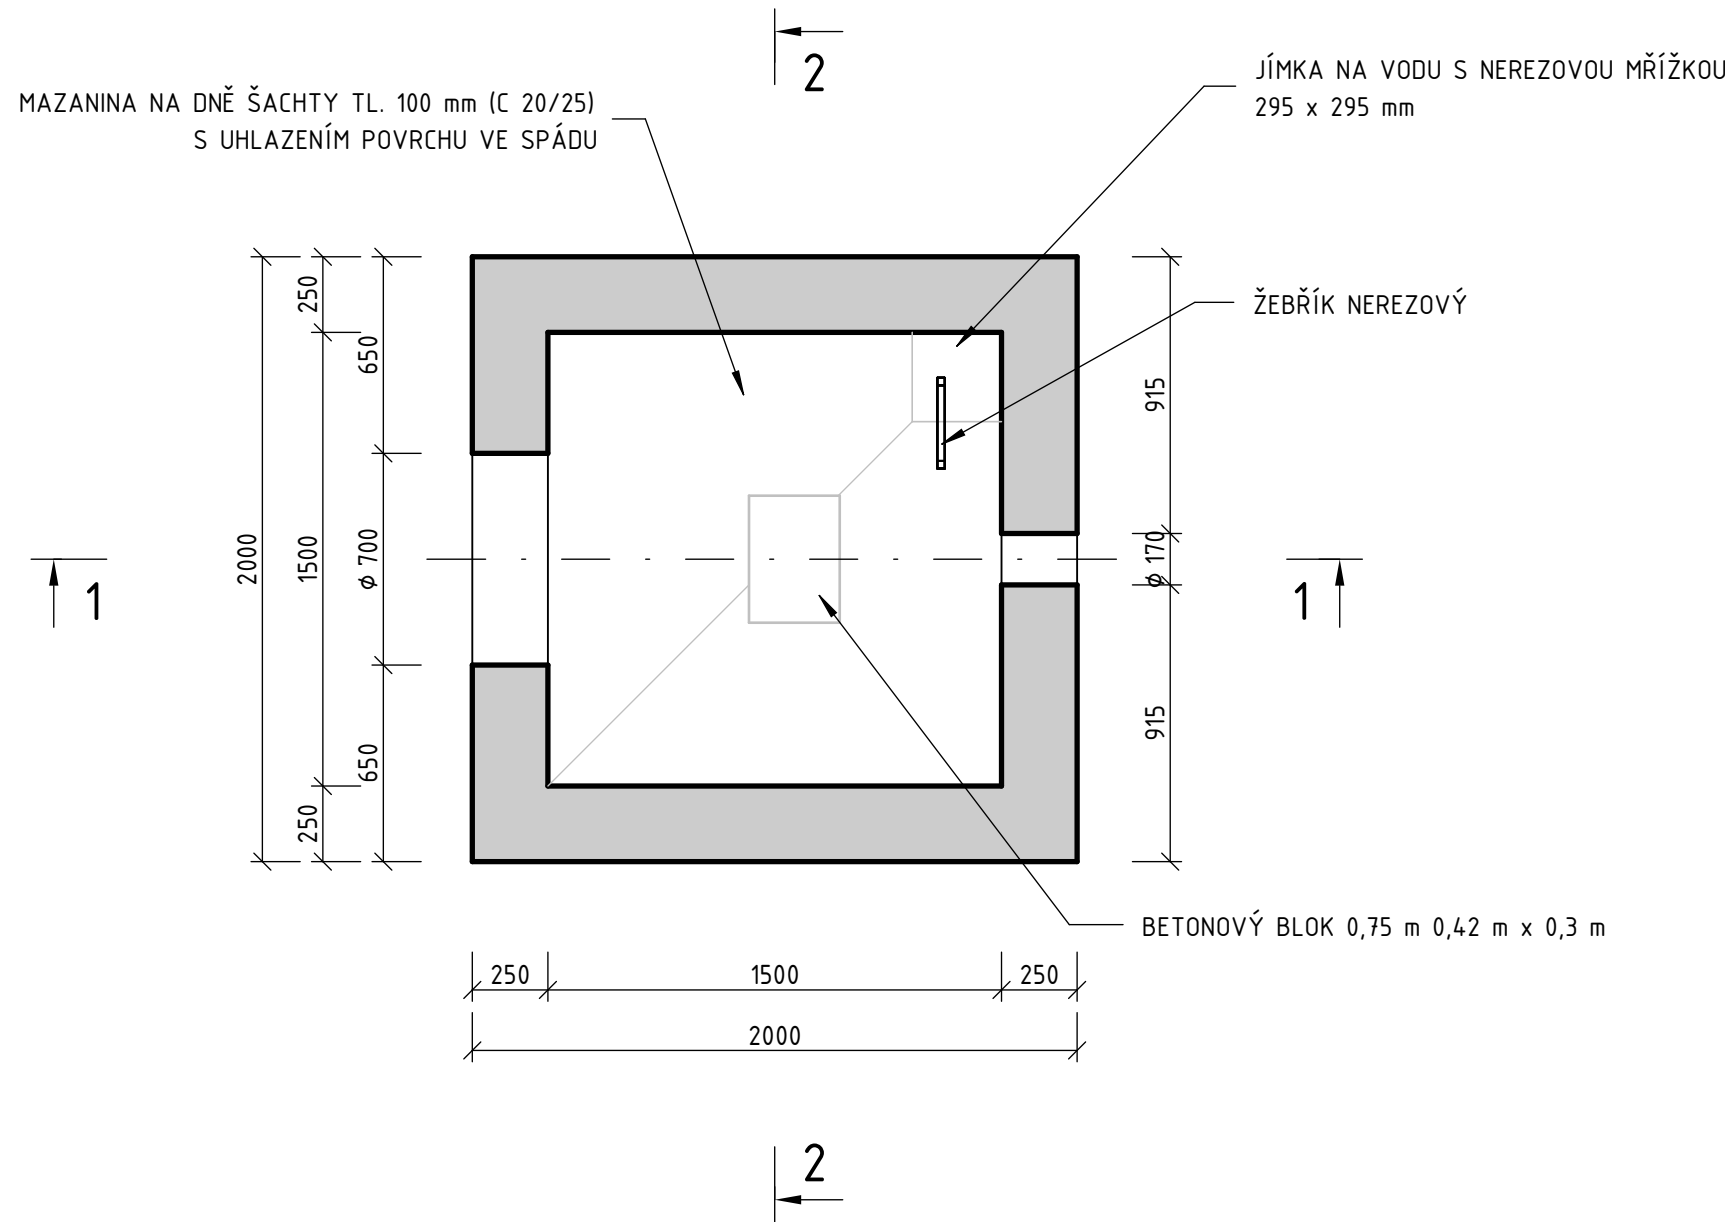

ŘEZ 4-4 1: 25

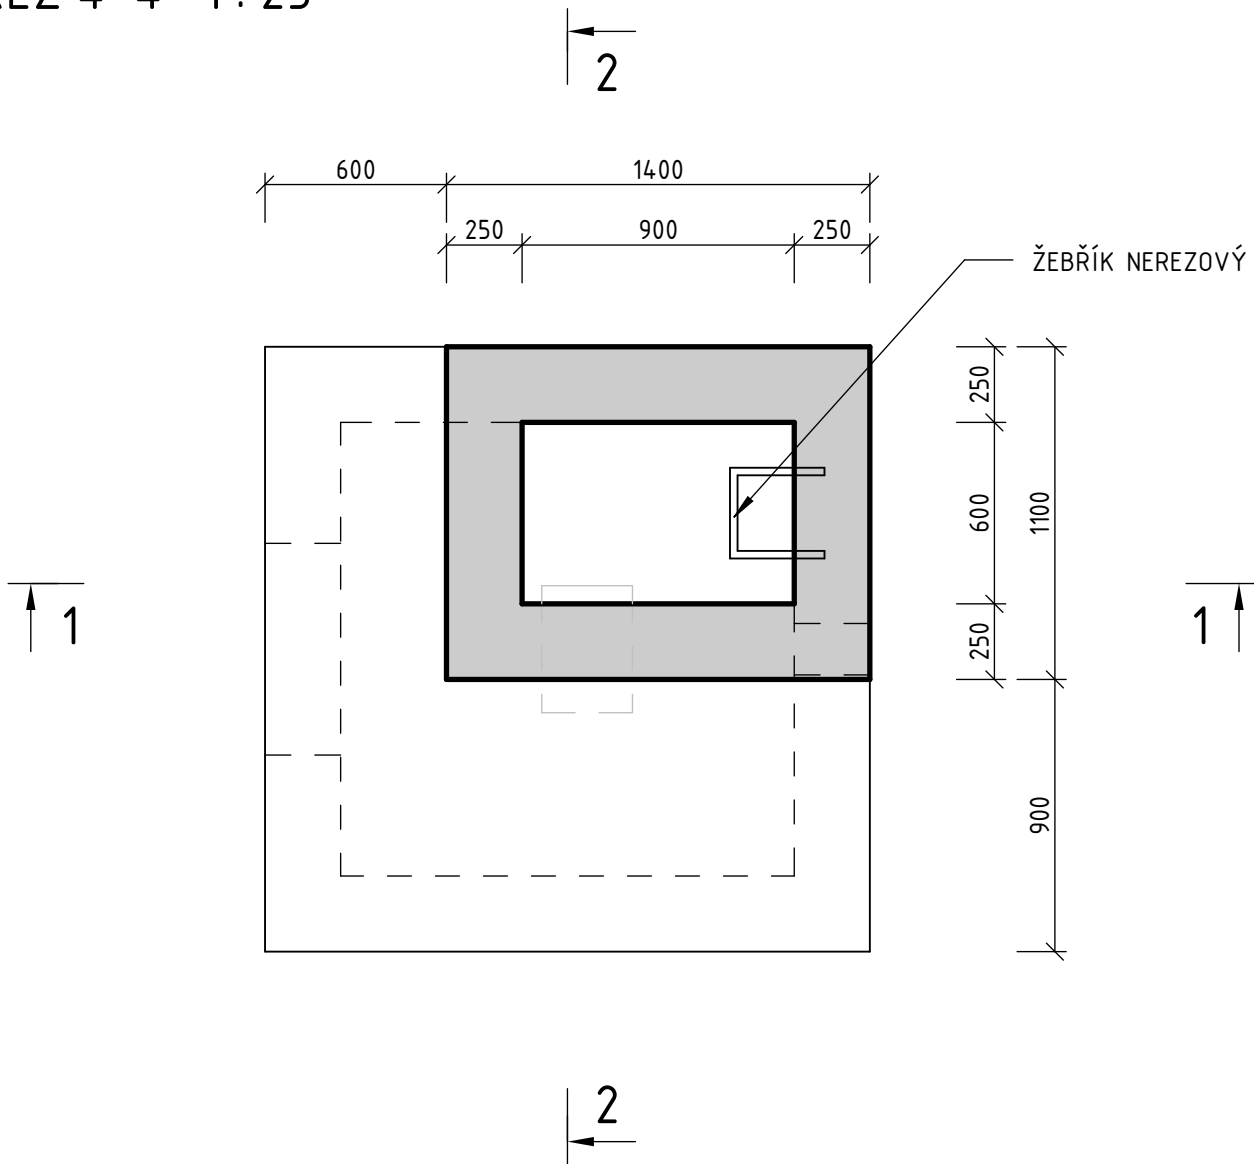

POZNÁMKY:

- VIZ VÝKRES - "6.1 ARMATURNÍ ŠACHTA AŠ3 - VÝKRES VYSTROJENÍ A ZALOŽENÍ"

BETON

JÍMKA

KRYTÍ

VŠECHNY PLOCHY

OCEL

BETONÁŘSKÁ

ČSN EN 206+A2

C30/37-XF3

MINIMÁLNÍ / JMENOVITÉ

45mm / 50 mm

ČSN EN 10027-1

B 500B

Souřadnicový systém: S-JTSK
Výškový systém: Bpv

SO 342 Přeložka vodovodu PVC 225 v MÚK Židněves

Objednatel:
ŘEDITELSTVÍ SILNIC A DÁLNIC
Ředitelství silnic a dálnic s. p.
Čerčanská 2023/12, Krč, 140 00 Praha 4

Zhotovitel:
Valbek, spol. s r.o.
Vaňurova 505/17
460 07 Liberec 3

 Valbek	Vypracoval	ING. ROMAN NAZARCHUK	Zak. číslo	21-L113-001	
	Zodp. projektant	ING. JIŘÍ VANCL	Datum	02/2025	
	Tech. kontrola	ING. DAVID LANDA	Stupeň	PDPS	
	Akce	I/16 MLADÁ BOLESLAV - MARTINOVICE		Počet formátů	8x A4
				Měřítka	1:25
Zhotovitel: Valbek, spol. s r.o. Vaňurova 505/17 460 07 Liberec 3	Příloha	ARMATURNÍ ŠACHTA AŠ3 - VÝKRES TVARU		Č. přílohy	Paré
				6.2	