

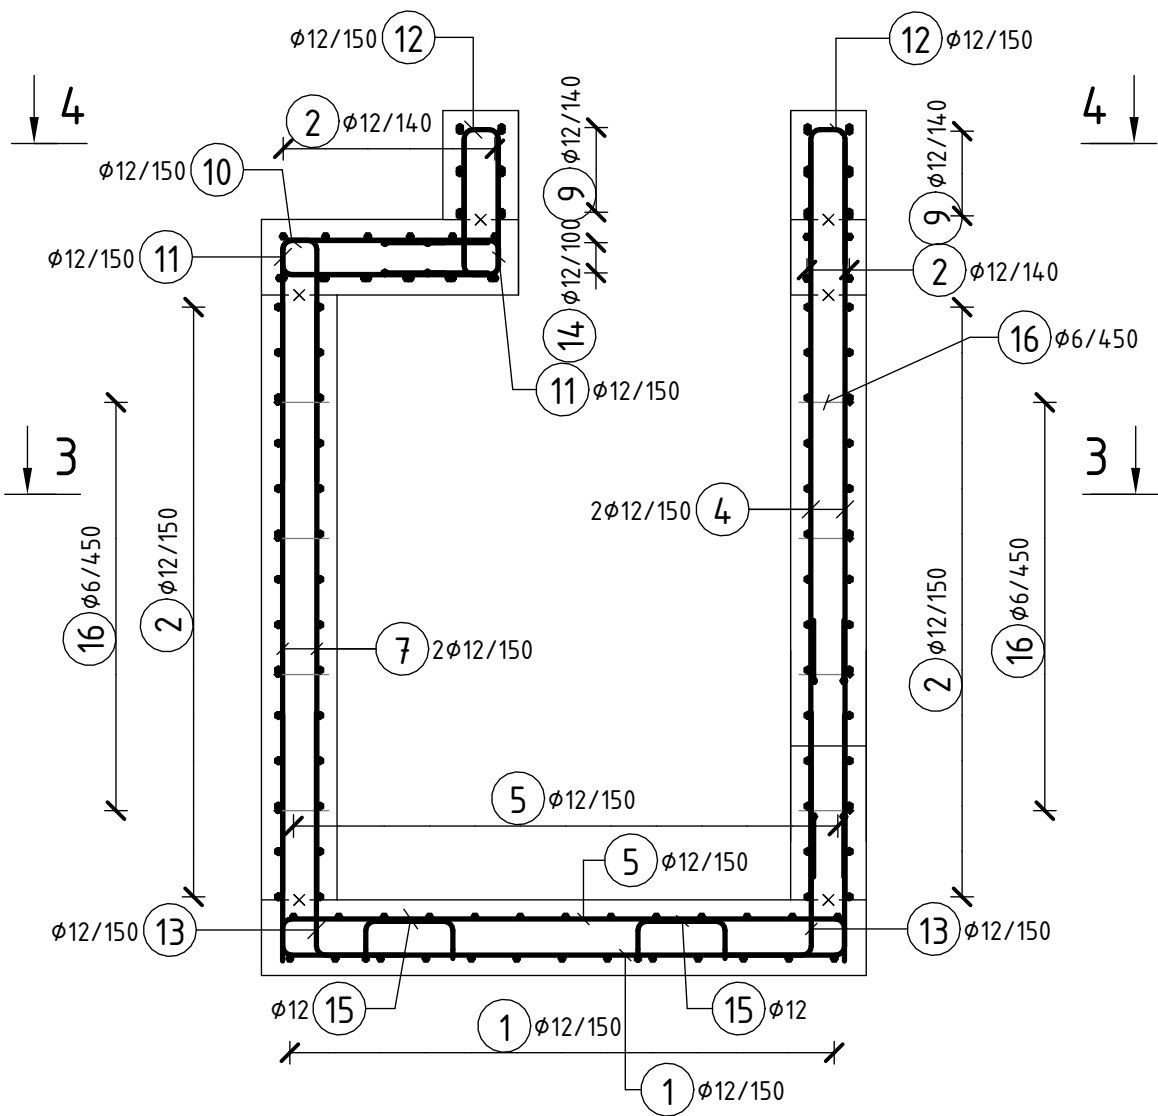


ŘEZ 1-1 1: 25

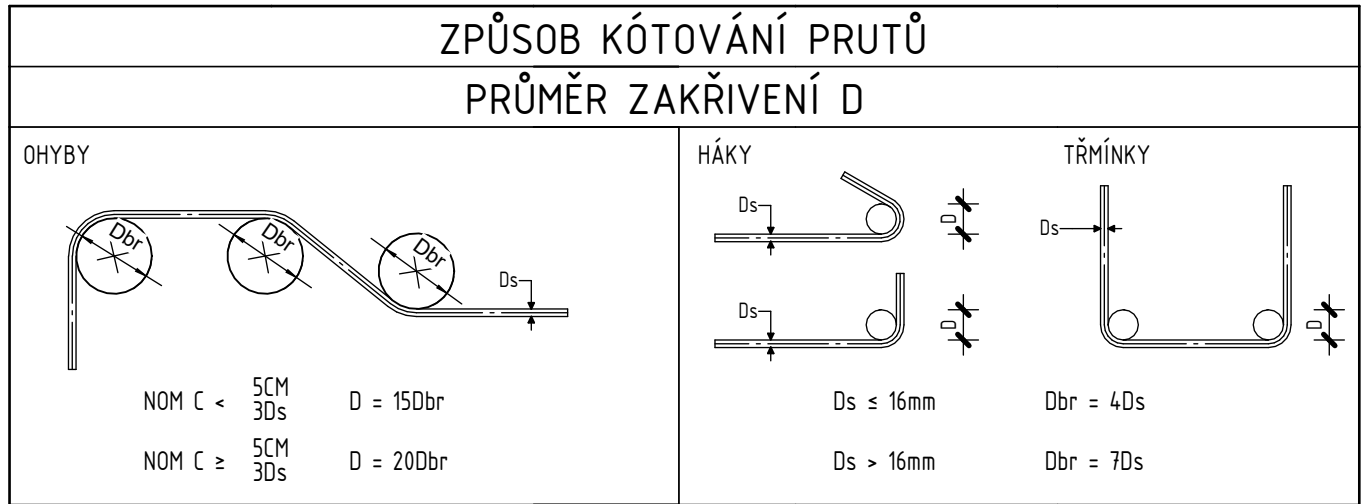

ŘEZ 2-2 1: 25

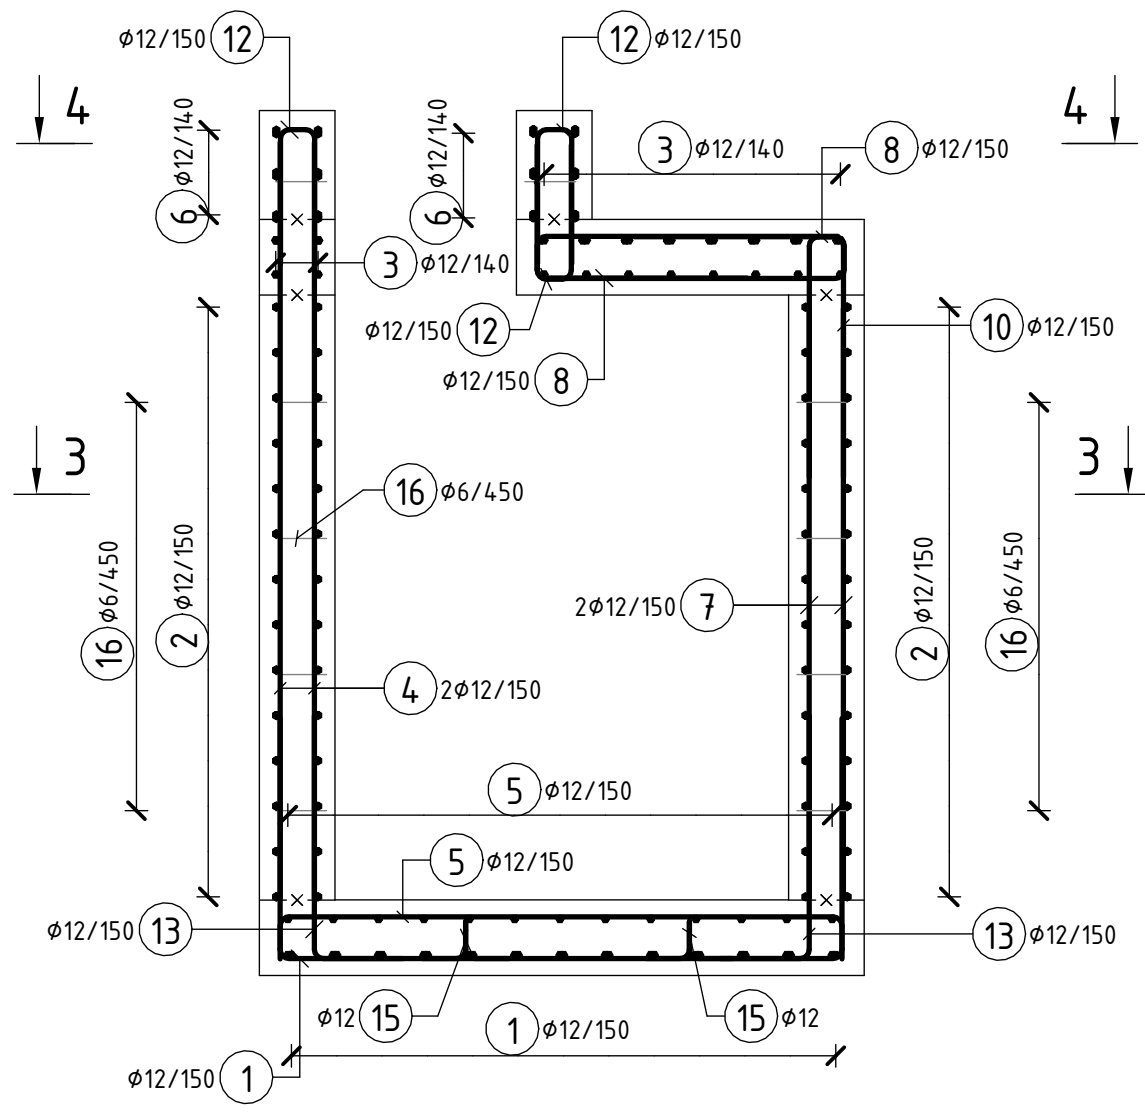

POZNÁMKY:

-V MÍSTĚ POTRUBÍ BUDE VÝZTUŽ OŘÍZNUTA.

BETON

JÍMKÁ

ČSN EN 206+A2

C30/37-XF3

KRYTÍ

VŠECHNY PLOCHY

MINIMÁLNÍ / JMENOVITÉ

45mm / 50 mm

OCEL

BETONÁŘSKÁ

ČSN EN 10027-1


B 500B

ROZMĚRY VÝZTUŽE JSOU KÓTOVÁNY NA VNĚJŠÍ HRANY


VÝKAZ VÝZTUŽE

ČÍSLO POL.	φ [mm]	DĚLKA [mm]	POČET [ks]	DĚLKY PODLE φ [m]	
				d6	d12
1	12	3470	26	0	90.22
2	12	2650	128	0	339.2
3	12	2675	20	0	52.5
4	12	2500	30	0	75
5	12	2160	26	0	56.16
6	12	2050	12	0	24.6
7	12	1950	66	0	128.7
8	12	1850	12	0	22.2
9	12	1750	12	0	21
10	12	1725	33	0	56.94
11	12	1525	8	0	12.2
12	12	1025	41	0	42.04
13	12	1109	48	0	53.24
14	12	1000	12	0	12
15	12	870	4	0	3.48
16	6	305	54	16.5	0
DĚLKA PODLE φ CELKEM			[m]	16.5	989.48
JEDNOTKOVÁ HMOTNOST			[kg/m']	0.222	0.888
HMOTNOST PODLE φ CELKEM			[kg]	3.66	878.64
CELKOVÁ HMOTNOST VÝZTUŽE			[kg]	882.3	


ŘEZ 3-3 1: 25

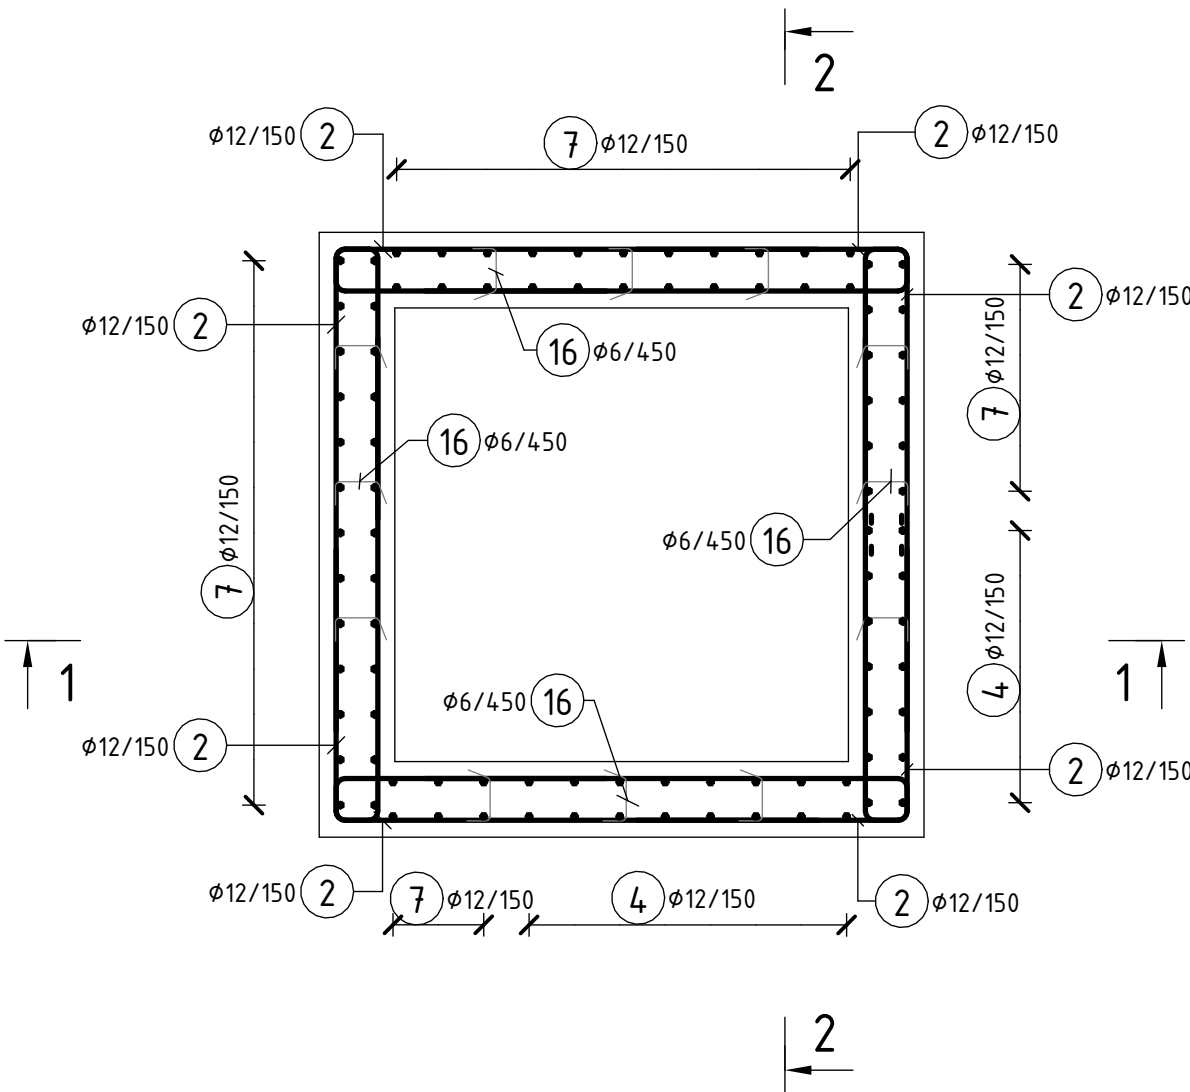

ŘEZ 4-4 1: 25

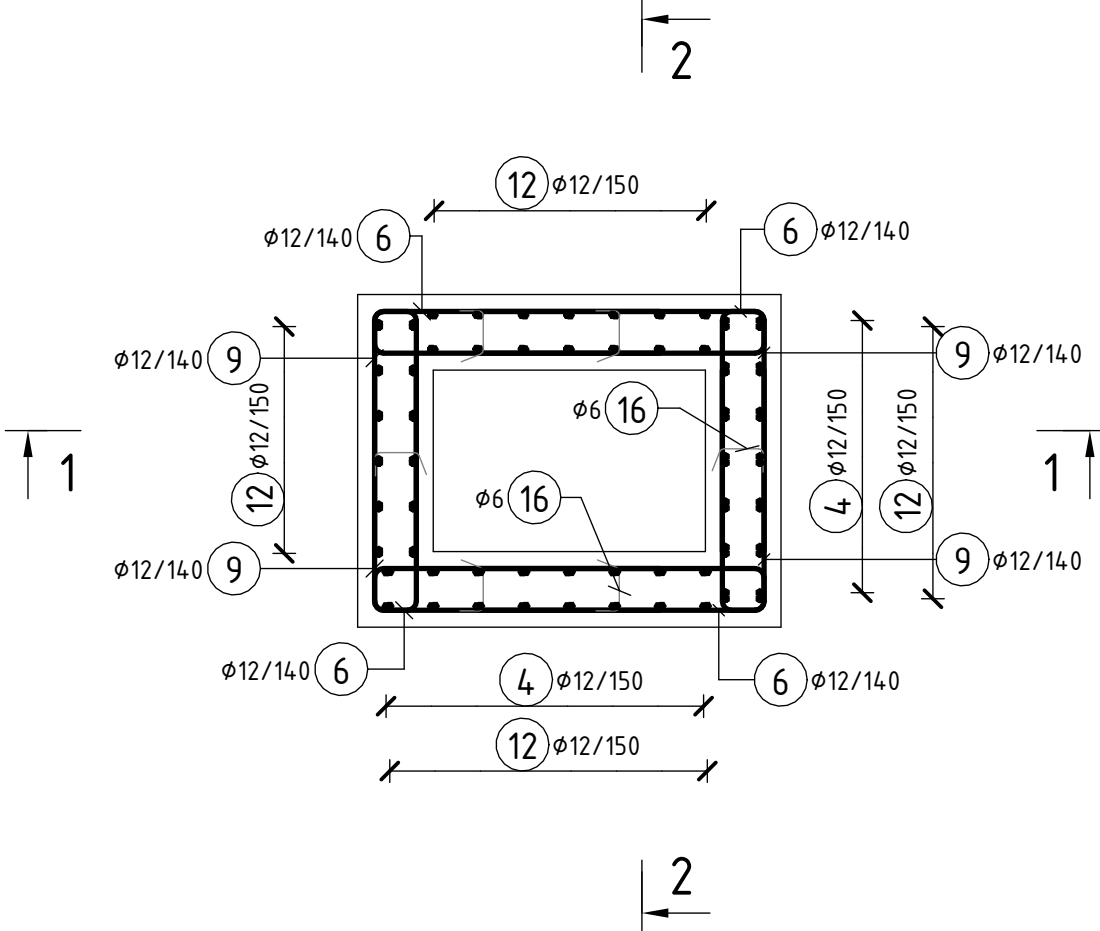

DETAIL 1 1: 25

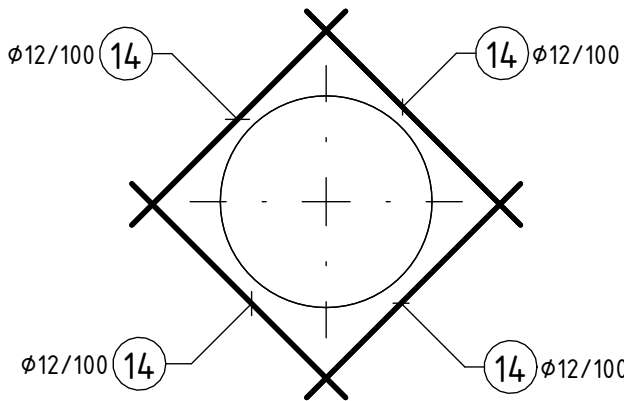

Souřadnicový systém: S-JTSK
Výškový systém: Bpv

SO 342 Přeložka vodovodu PVC 225 v MÚK Židněves



ŘEDITELSTVÍ
SILNIC
A DÁLNIC

Ředitelství silnic a dálnic s. p.

Čerčanská 2023/12, Krč, 140 00 Praha 4



Valbek

Valbek, spol. s r.o.

Vaňurova 505/17
460 07 Liberec 3

 Valbek	Vypracoval	ING. ROMAN NAZARCHUK	Zak. číslo	21-LI13-001
	Zodp. projektant	ING. JIŘÍ VANCL	Datum	02/2025
	Tech. kontrola	ING. DAVID LANDA	Stupeň	PDPS
	Akce	I/16 MLADÁ BOLESLAV - MARTINOVICE		Počet formátů 8x A4
				Měřítko 1:25
Zhotovitel: Valbek, spol. s r.o. Vaňurova 505/17 460 07 Liberec 3	Příloha ARMATURNÍ ŠACHTA AŠ1 - VÝKRES VÝZTUŽE		6.3	
			Č. přílohy	Paré