

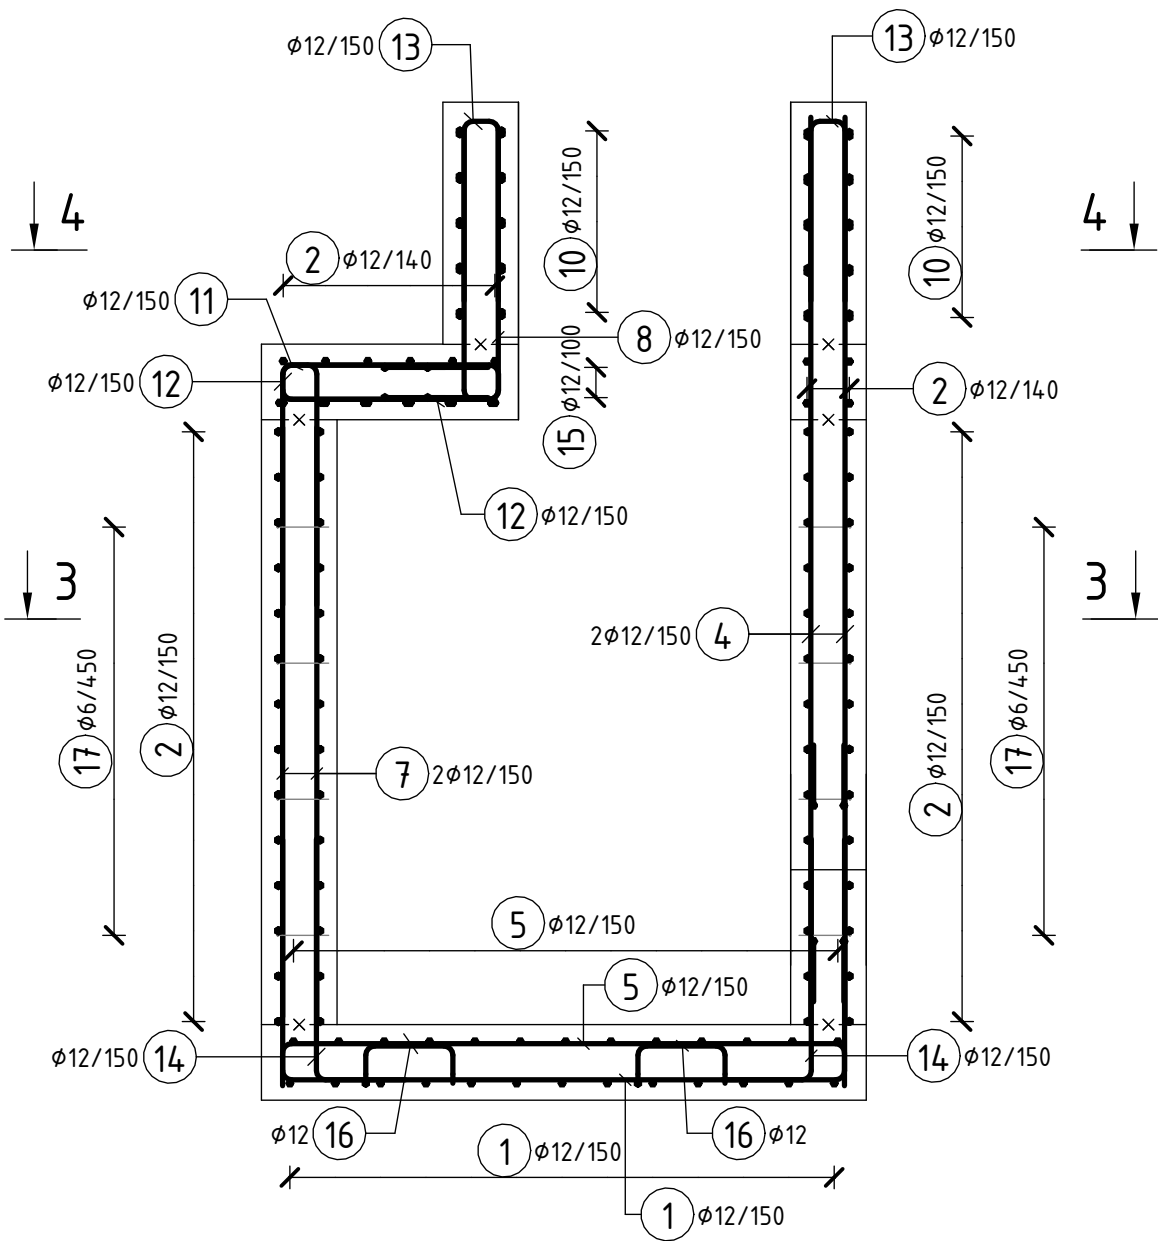


ŘEZ 1-1 1: 25

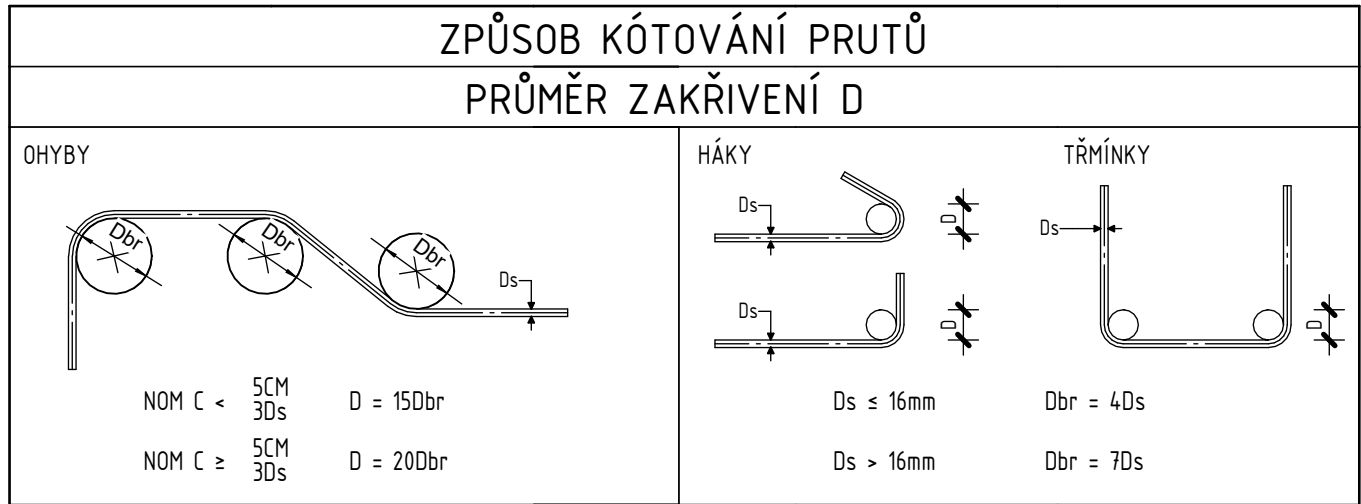

ŘEZ 2-2 1: 25

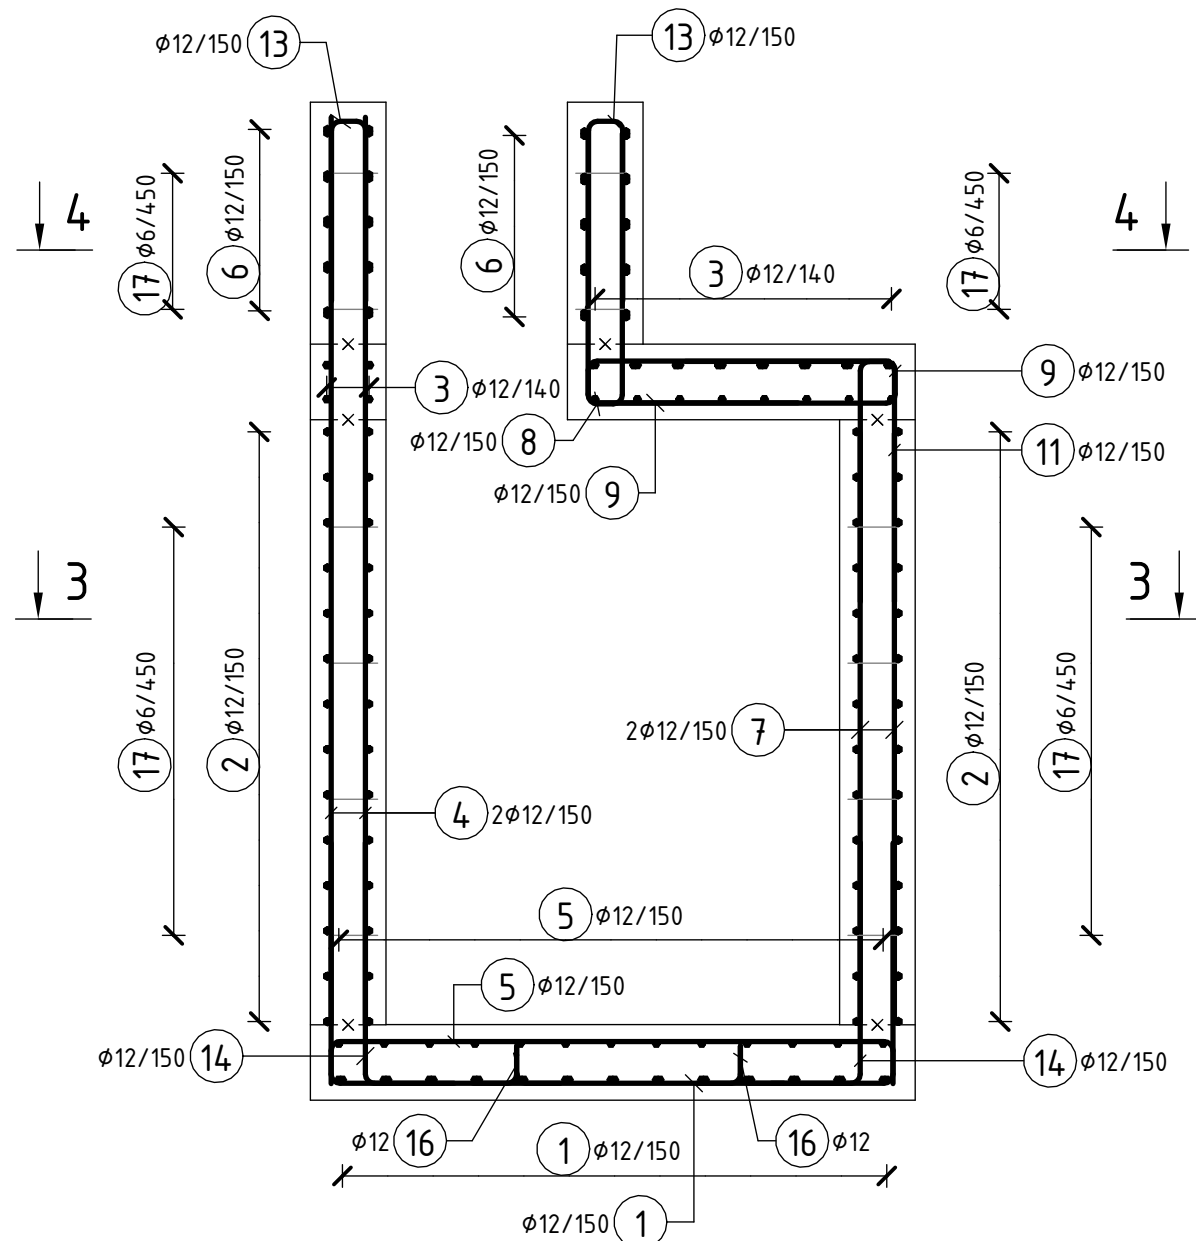

POZNÁMKY:

- V MÍSTĚ POTRUBÍ BUDE VÝZTUŽ OŘÍZNUTA.

BETON

JÍMKÁ

KRYTÍ

VŠECHNY PLOCHY

OCEL

BETONÁŘSKÁ

ČSN EN 206+A2

C30/37-XF3

MINIMÁLNÍ / JMENOVITÉ

45mm / 50 mm

ČSN EN 10027-1


B 500B

ROZMĚRY VÝZTUŽE JSOU KÓTOVÁNY NA VNĚJŠÍ HRANY


VÝKAZ VÝZTUŽE

ČÍSLO POL.	Ø [mm]	DĚLKA [mm]	POČET [ks]	DĚLKY PODLE Ø [m]	
				d6	d12
1	12	3470	26	0	90.22
2	12	2650	128	0	339.2
3	12	2625	20	0	52.5
4	12	3000	30	0	90
5	12	2160	26	0	56.16
6	12	2050	20	0	41
7	12	1950	66	0	128.7
8	12	1925	13	0	25.03
9	12	1850	12	0	22.2
10	12	1750	20	0	35
11	12	1725	33	0	56.94
12	12	1525	8	0	12.2
13	12	1325	28	0	37.11
14	12	1102	48	0	52.9
15	12	1000	12	0	12
16	12	870	4	0	3.48
17	6	305	60	18.3	0
DĚLKA PODLE Ø CELKEM				[m]	18.3
JEDNOTKOVÁ HMOTNOST				[kg/m³]	0.222
HMOTNOST PODLE Ø CELKEM				[kg]	4.08
CELKOVÁ HMOTNOST VÝZTUŽE				[kg]	940.6


ŘEZ 3-3 1: 25

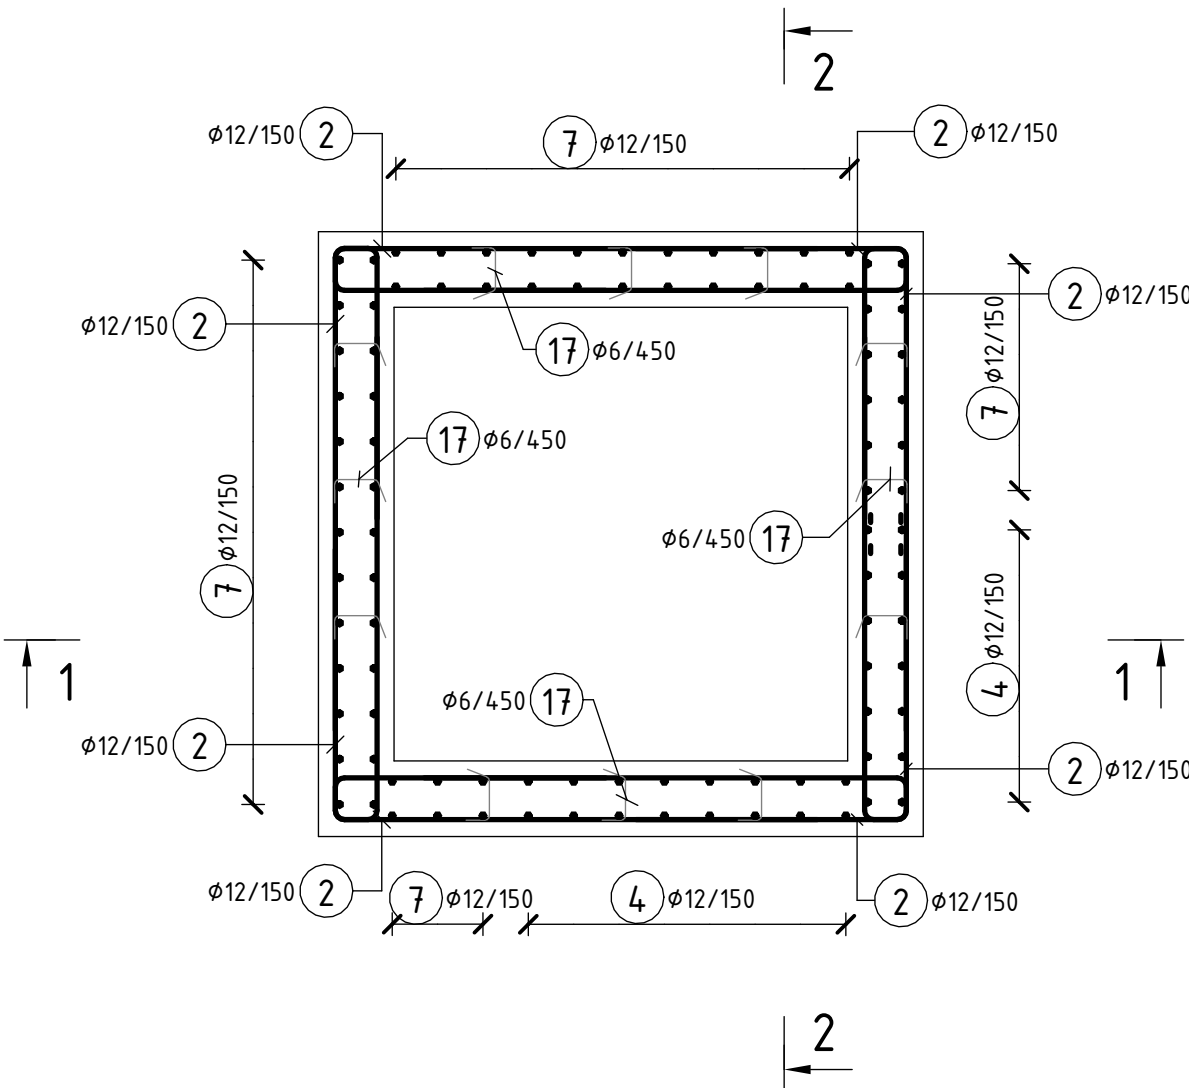

ŘEZ 4-4 1: 25

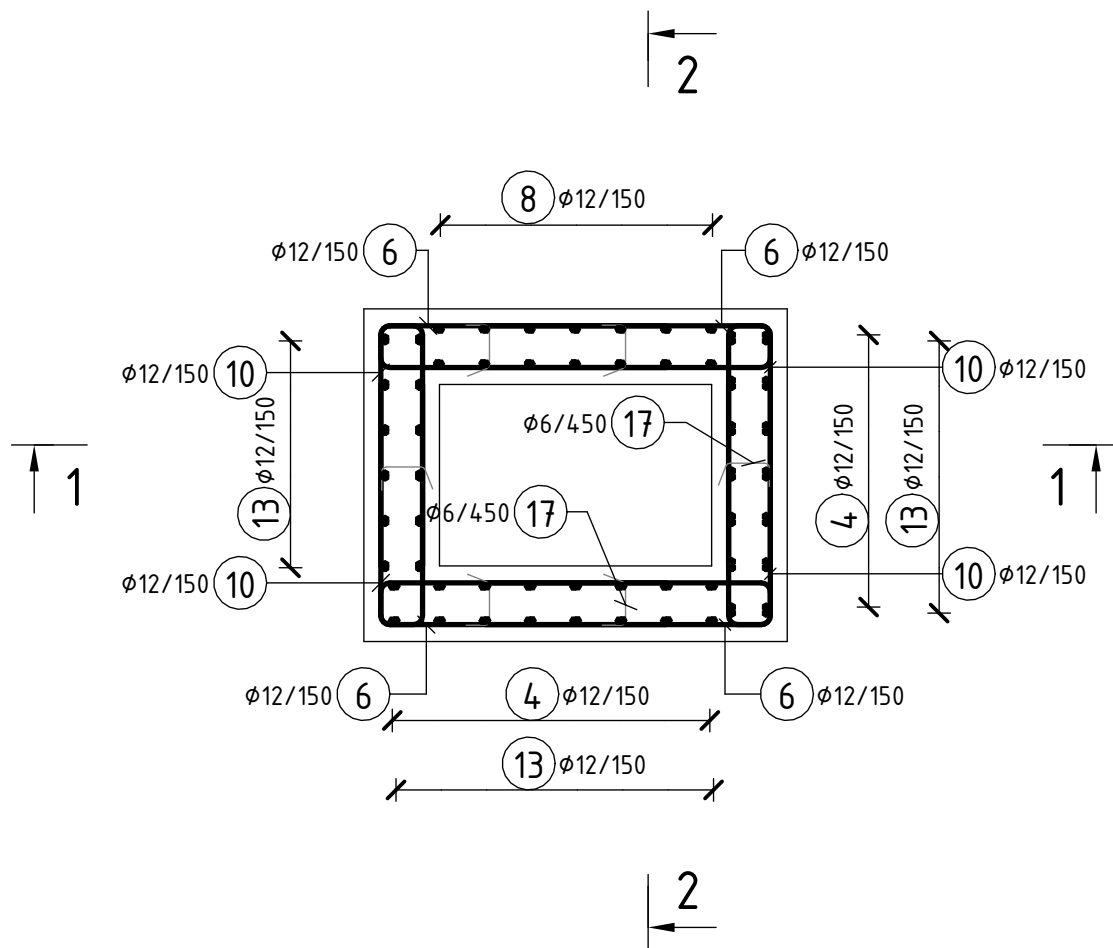

DETAIL 1 1: 25

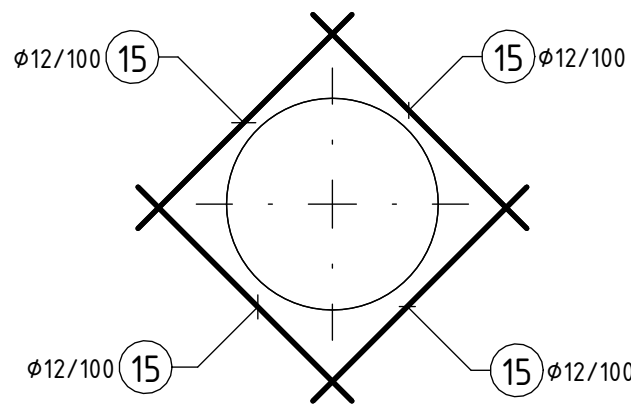

Souřadnicový systém: S-JTSK
Výškový systém: Bpv

SO 342 Přeložka vodovodu PVC 225 v MÚK Židněves

Objednatel:
ŘEDITELSTVÍ SILNIC A DÁLNIC
Ředitelství silnic a dálnic s. p.
Čerčanská 2023/12, Krč, 140 00 Praha 4

Zhotovitel:
Valbek
Valbek, spol. s r.o.
Vaňurova 505/17
460 07 Liberec 3

Vypracoval: ING. ROMAN NAZARCHUK
Zodp. projektant: ING. JIŘÍ VANCL
Tech. kontrola: ING. DAVID LANDA
Akce: I/16 MLADÁ BOLESLAV - MARTINOVICE
Zhotovitel: Valbek, spol. s r.o.
Vaňurova 505/17
460 07 Liberec 3
Příloha: ARMATURNÍ ŠACHTA AŠŽ - VÝKRES VÝZTUŽE
Zak. číslo: 21-LI13-001
Datum: 02/2025
Stupeň: PDPS
Počet formátů: 8x A4
Měřítko: 1:25
Č. přílohy: Paré
6.3