


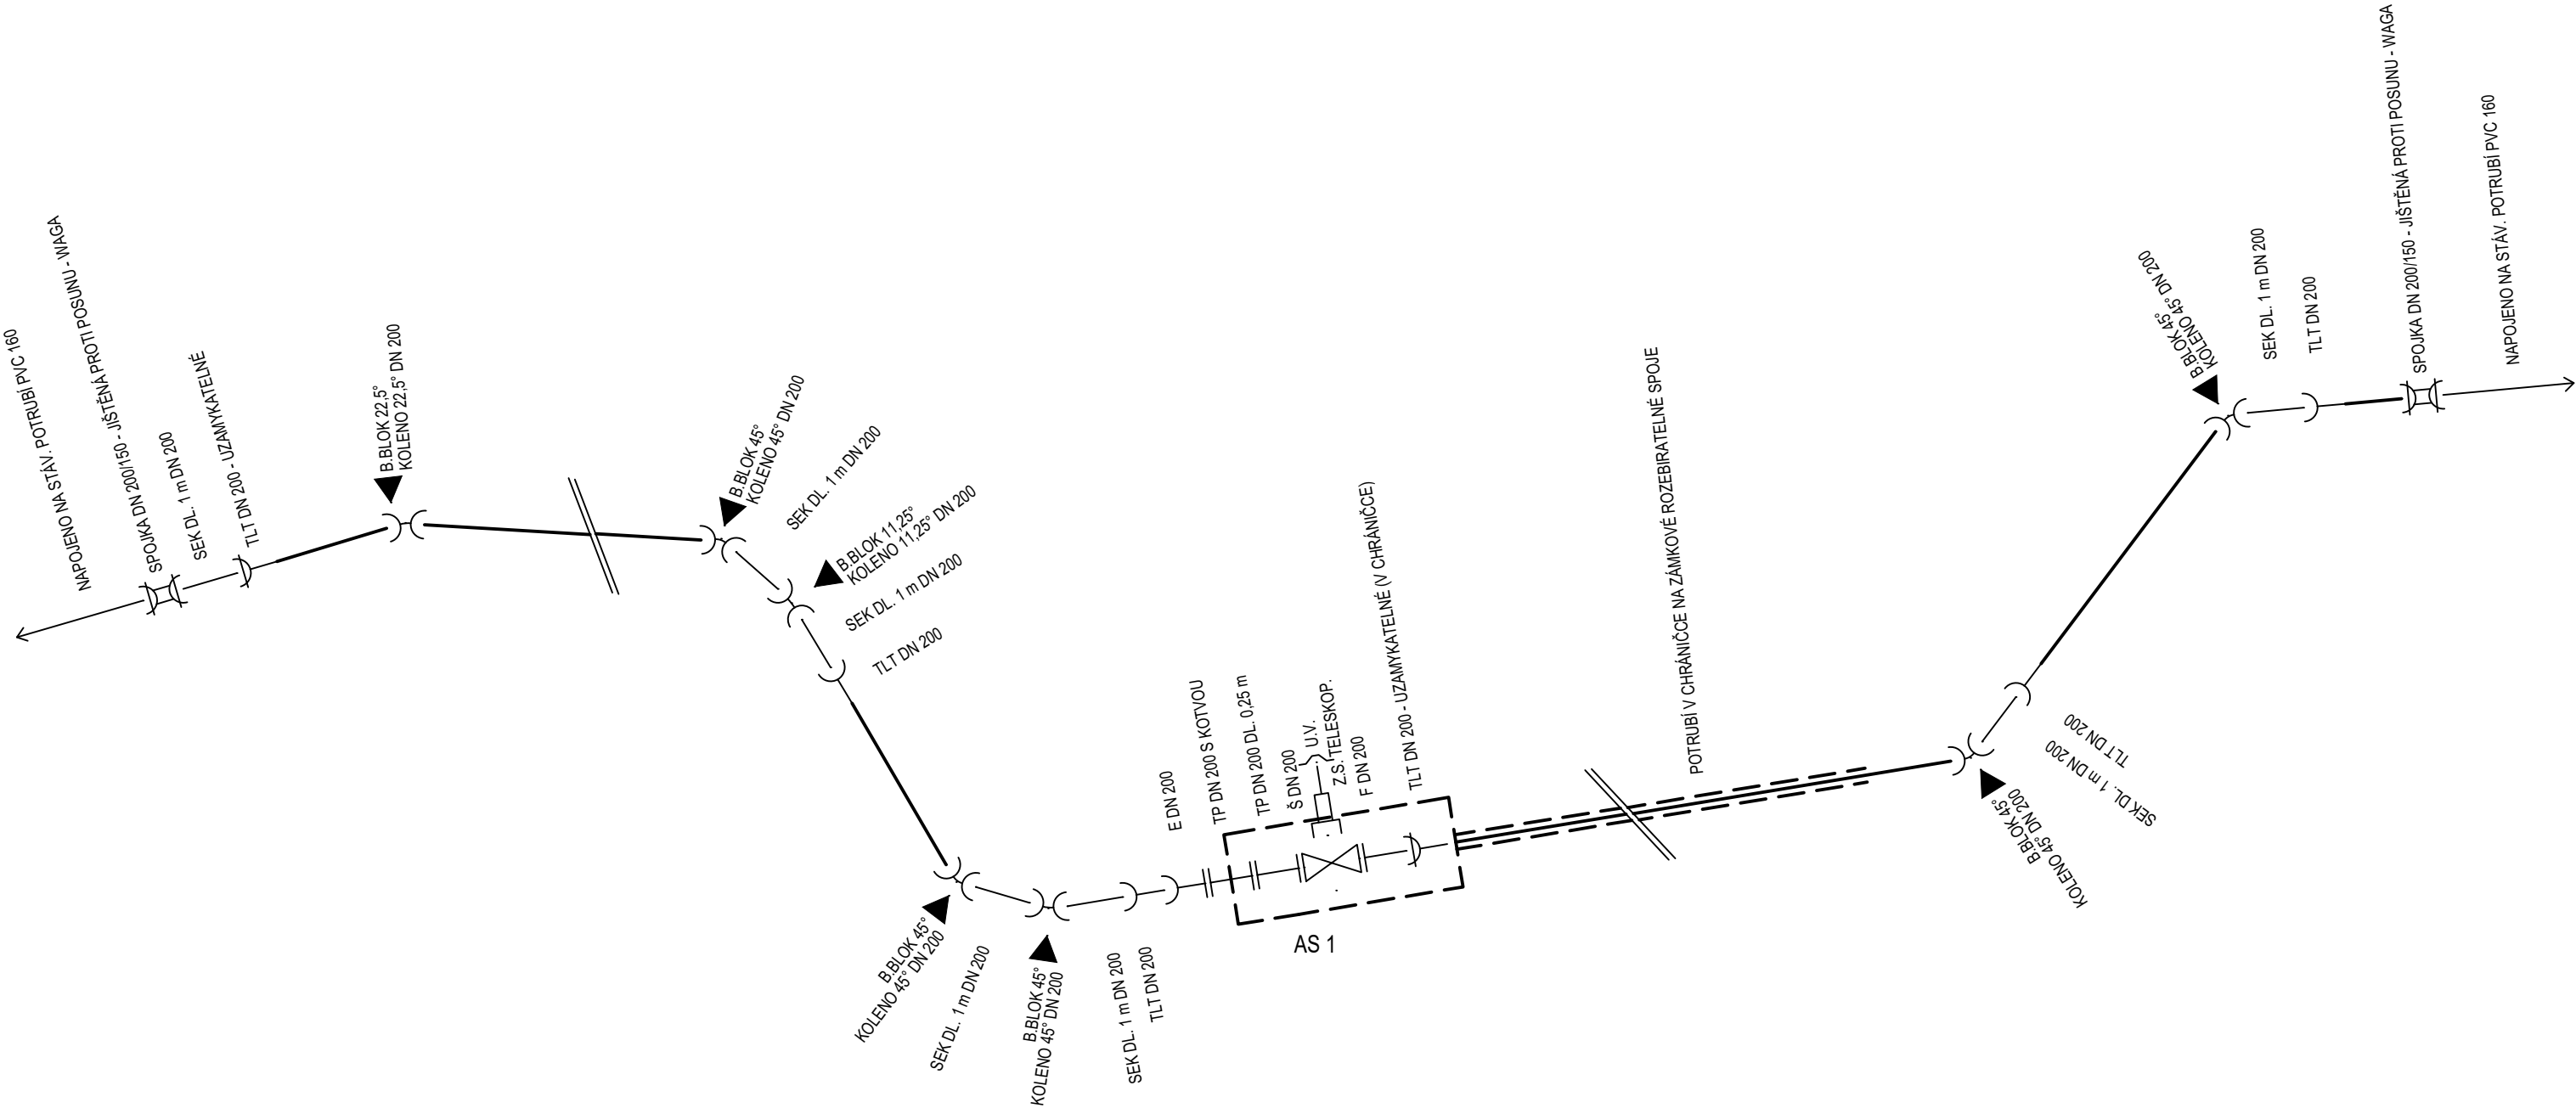

POTRUBÍ, TVAROVKY	Počet	Jednotka
POTRUBÍ		
POTRUBÍ TLT DN 200 min. CLASS 64	247,0	m
CHRÁNIČKA OC DN 500 (tl. stěny 10 mm)	57,0	m
TP DN 200 DL. 0,25 m	1	ks
TVAROVKY		
E DN 200	1	ks
F DN 200	1	ks
KOLENO 11,25° DN 200	1	ks
KOLENO 22,5° DN 200	2	ks
KOLENO 45° DN 200	4	ks
SPOJKA DN 200/150 - JIŠTĚNÁ PROTI POSUNU	2	ks
TLT SEK DN 200 DL. 1 m	7	ks
TP DN 200 S KOTVOU	1	ks
U.V.	1	ks
Z S. TELESKOP.	1	ks
ARMATURY		
Š DN 200	1	ks
JINÉ		
B.BLOK 11,25° - (0,3x0,4x0,75) m	1	ks
B.BLOK 22,5° - (0,56x0,4x0,85) m	1	ks
B.BLOK 45° - (0,87x0,5x0,97) m	5	ks

SPOJKY, TVAROVKY A ARMATURY DLE POŽADAVKU PROVOZOVATELE
LITINOVÉ POTRUBÍ BUDE NA KLUZNÝCH OBJÍMKÁCH PO 1 METRECH
CHRÁNIČKY BUDOU UTĚSNĚNY MANŽETAMI

SO 343

Přeložka vodovodu PVC 160 v km 6,091

Objednatel:



**ŘEDITELSTVÍ
SILNIC
A DÁLNIC**

Ředitelství silnic a dálnic s.p.
Čerčanská 2023/12, Krč, 140 00 Praha 4

Zhotovitel:



Valbek, spol. s r.o.
Vaňurova 505/17
460 07 Liberec 3

HIP:

ING. T. KLIMENT



Vypracoval	BC. ŠTĚPÁN HORECKÝ		Zak. číslo	21-LI13-001	
Zodp. projektant	ING. JIŘÍ VÁNCL		Datum	02/2025	
Tech. kontrola	ING. DAVID LANDA		Stupeň	PDPS	
Akce	I/16 MLADÁ BOLESLAV - MARTINOVICE			Počet formátů	4 x A4
Měřítko				-	
Č. přílohy				Paré	
Zhotovitel: Valbek, spol. s r.o. Vaňurova 505/17 460 07 Liberec 3	Příloha KLADEČSKÝ PLÁN			5	