


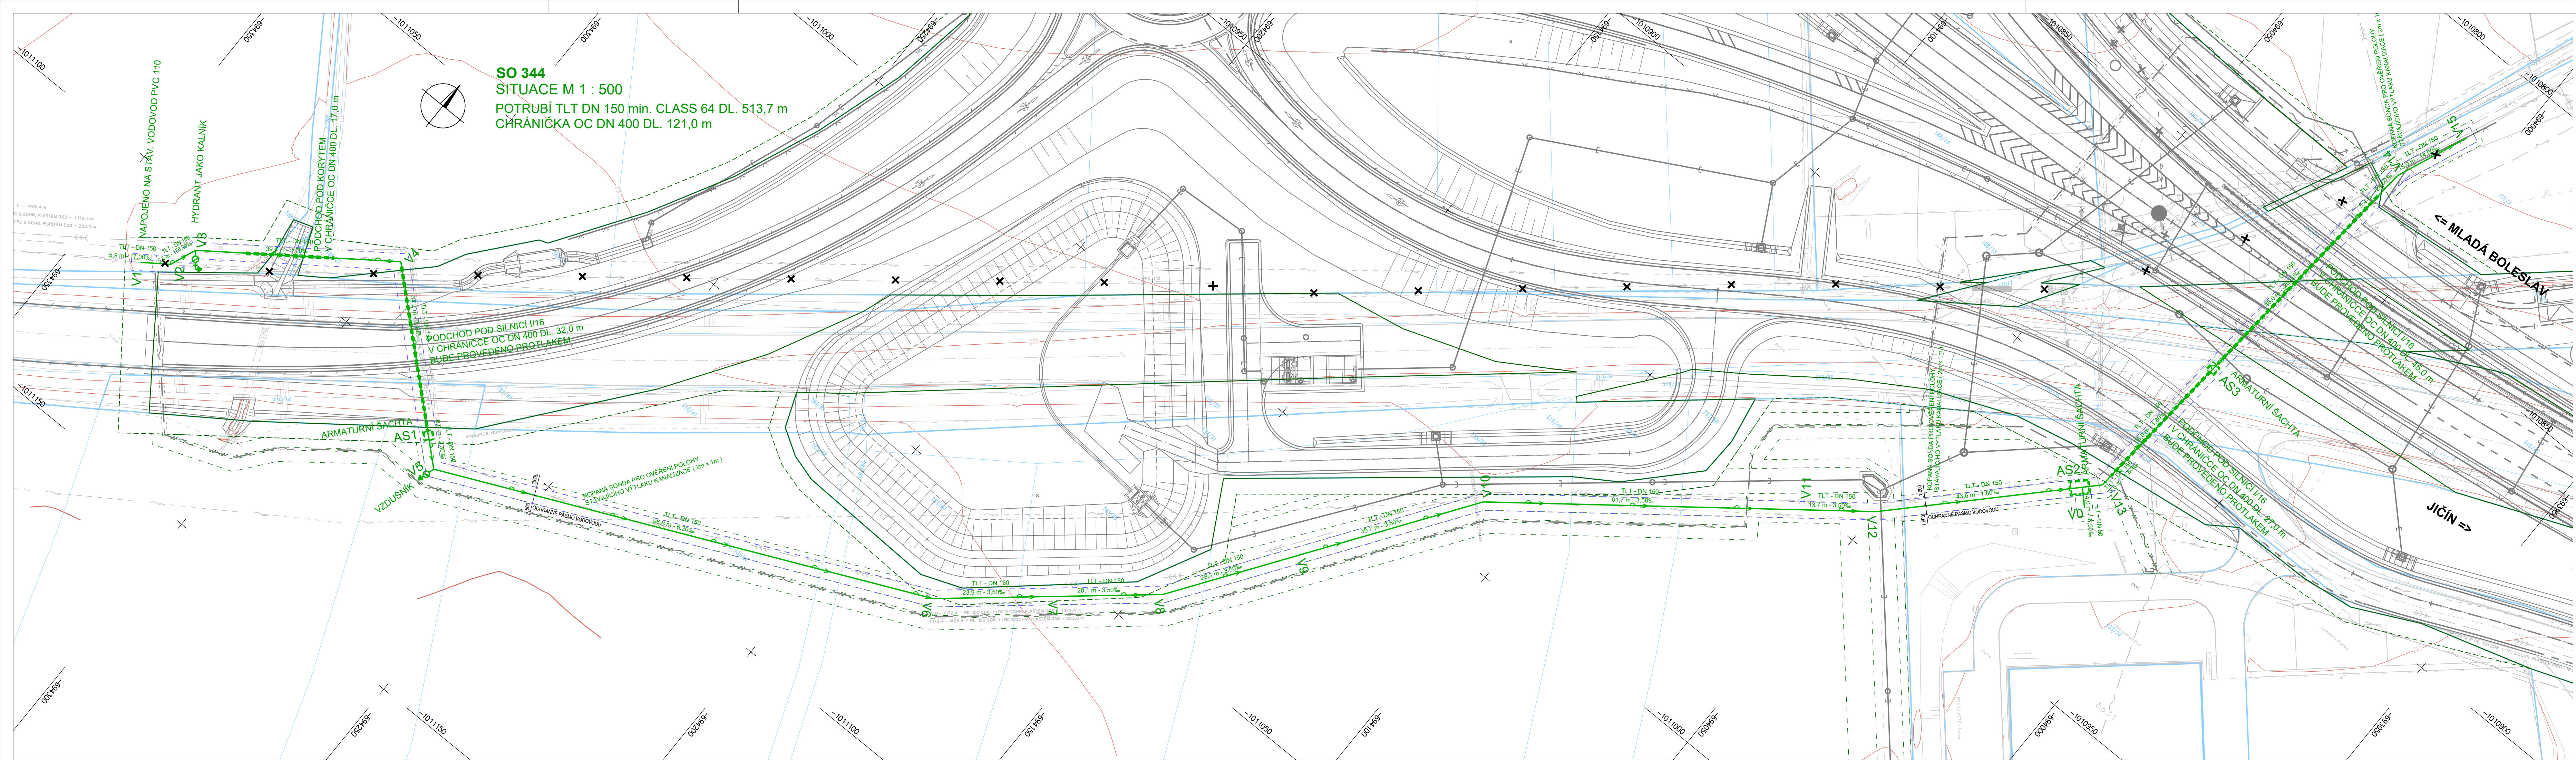

LEGENDA

STÁVAJÍCÍ IS - INFORMATIVNÍ ZÁKRES

- STÁVAJÍCÍ VODOVOD
- STÁVAJÍCÍ TLAKOVÁ KANALIZACE
- STÁVAJÍCÍ KANALIZACE JEDNOTNÁ
- STÁVAJÍCÍ NTL
- PLYNOVOD - STL
- STÁVAJÍCÍ VTL
- PODZEMNÍ VEDENÍ NN
- PODZEMNÍ VEDENÍ VN
- STÁVAJÍCÍ PODZEMNÍ VEDENÍ VVN
- NADZEMNÍ VEDENÍ NN
- NADZEMNÍ VEDENÍ VN
- NADZEMNÍ VEDENÍ VVN
- PODZEMNÍ SDĚLOVACÍ VEDENÍ
- STÁVAJÍCÍ SDĚL. VEDENÍ NADZ.

Souradnicový systém: S-JTSK
Výškový systém: Bpv

SO 344 Přeložka vodovodu v MÚK Martinovice

Objednatel:



Ředitelství silnic a dálnic s. p.
Čerčanská 2023/12, Krč, 140 00 Praha 4

Zhotovitel:



Valbek, spol. s r.o.
Vaňurova 505/17
460 07 Liberec 3



Vypracoval	BC. Š. HORECKÝ		Zak. číslo	21-L113-001	
Zodp. projektant	ING. J. VANCL		Datum	02/2025	
Tech. kontrola	ING. D. LANDA		Stupeň	PDPS	
Akce	I/16 MLADÁ BOLESLAV - MARTINOVICE			Počet formátů	6 x A4
				Měřítko	1 : 500
				Č. přílohy	Paré
Příloha	SITUACE			2	