

VRCHOLOVÝ BOD

344

[1:1000/100]

KÓTA UPRAVENÉHO TERÉNU

HLOUBKA VÝKOPU

HLOUBKA DNA POTRUBÍ

KÓTA DNA POTRUBÍ

KÓTA STÁVAJÍCÍHO TERÉNU

HLOUBKA OD NOVÉHO TERÉNU

STANIČENÍ [km]

STANIČENÍ [m]


SKLON ‰ - DÉLKA v m

DN - MATERIÁL - DÉLKA v m

V 1 V 3 V 2 V 4 AS1 V 5

V 6 V 7 V 8 V 9 V 10 V 11 V 12 AS2 B1 AS3 V 14 V 15

SKLON ‰ - DÉLKA v m	
A1	17, 5,92
A2	156, 5,49
VRCHOLOVÝ BOD	
B1	V
B2	V 13

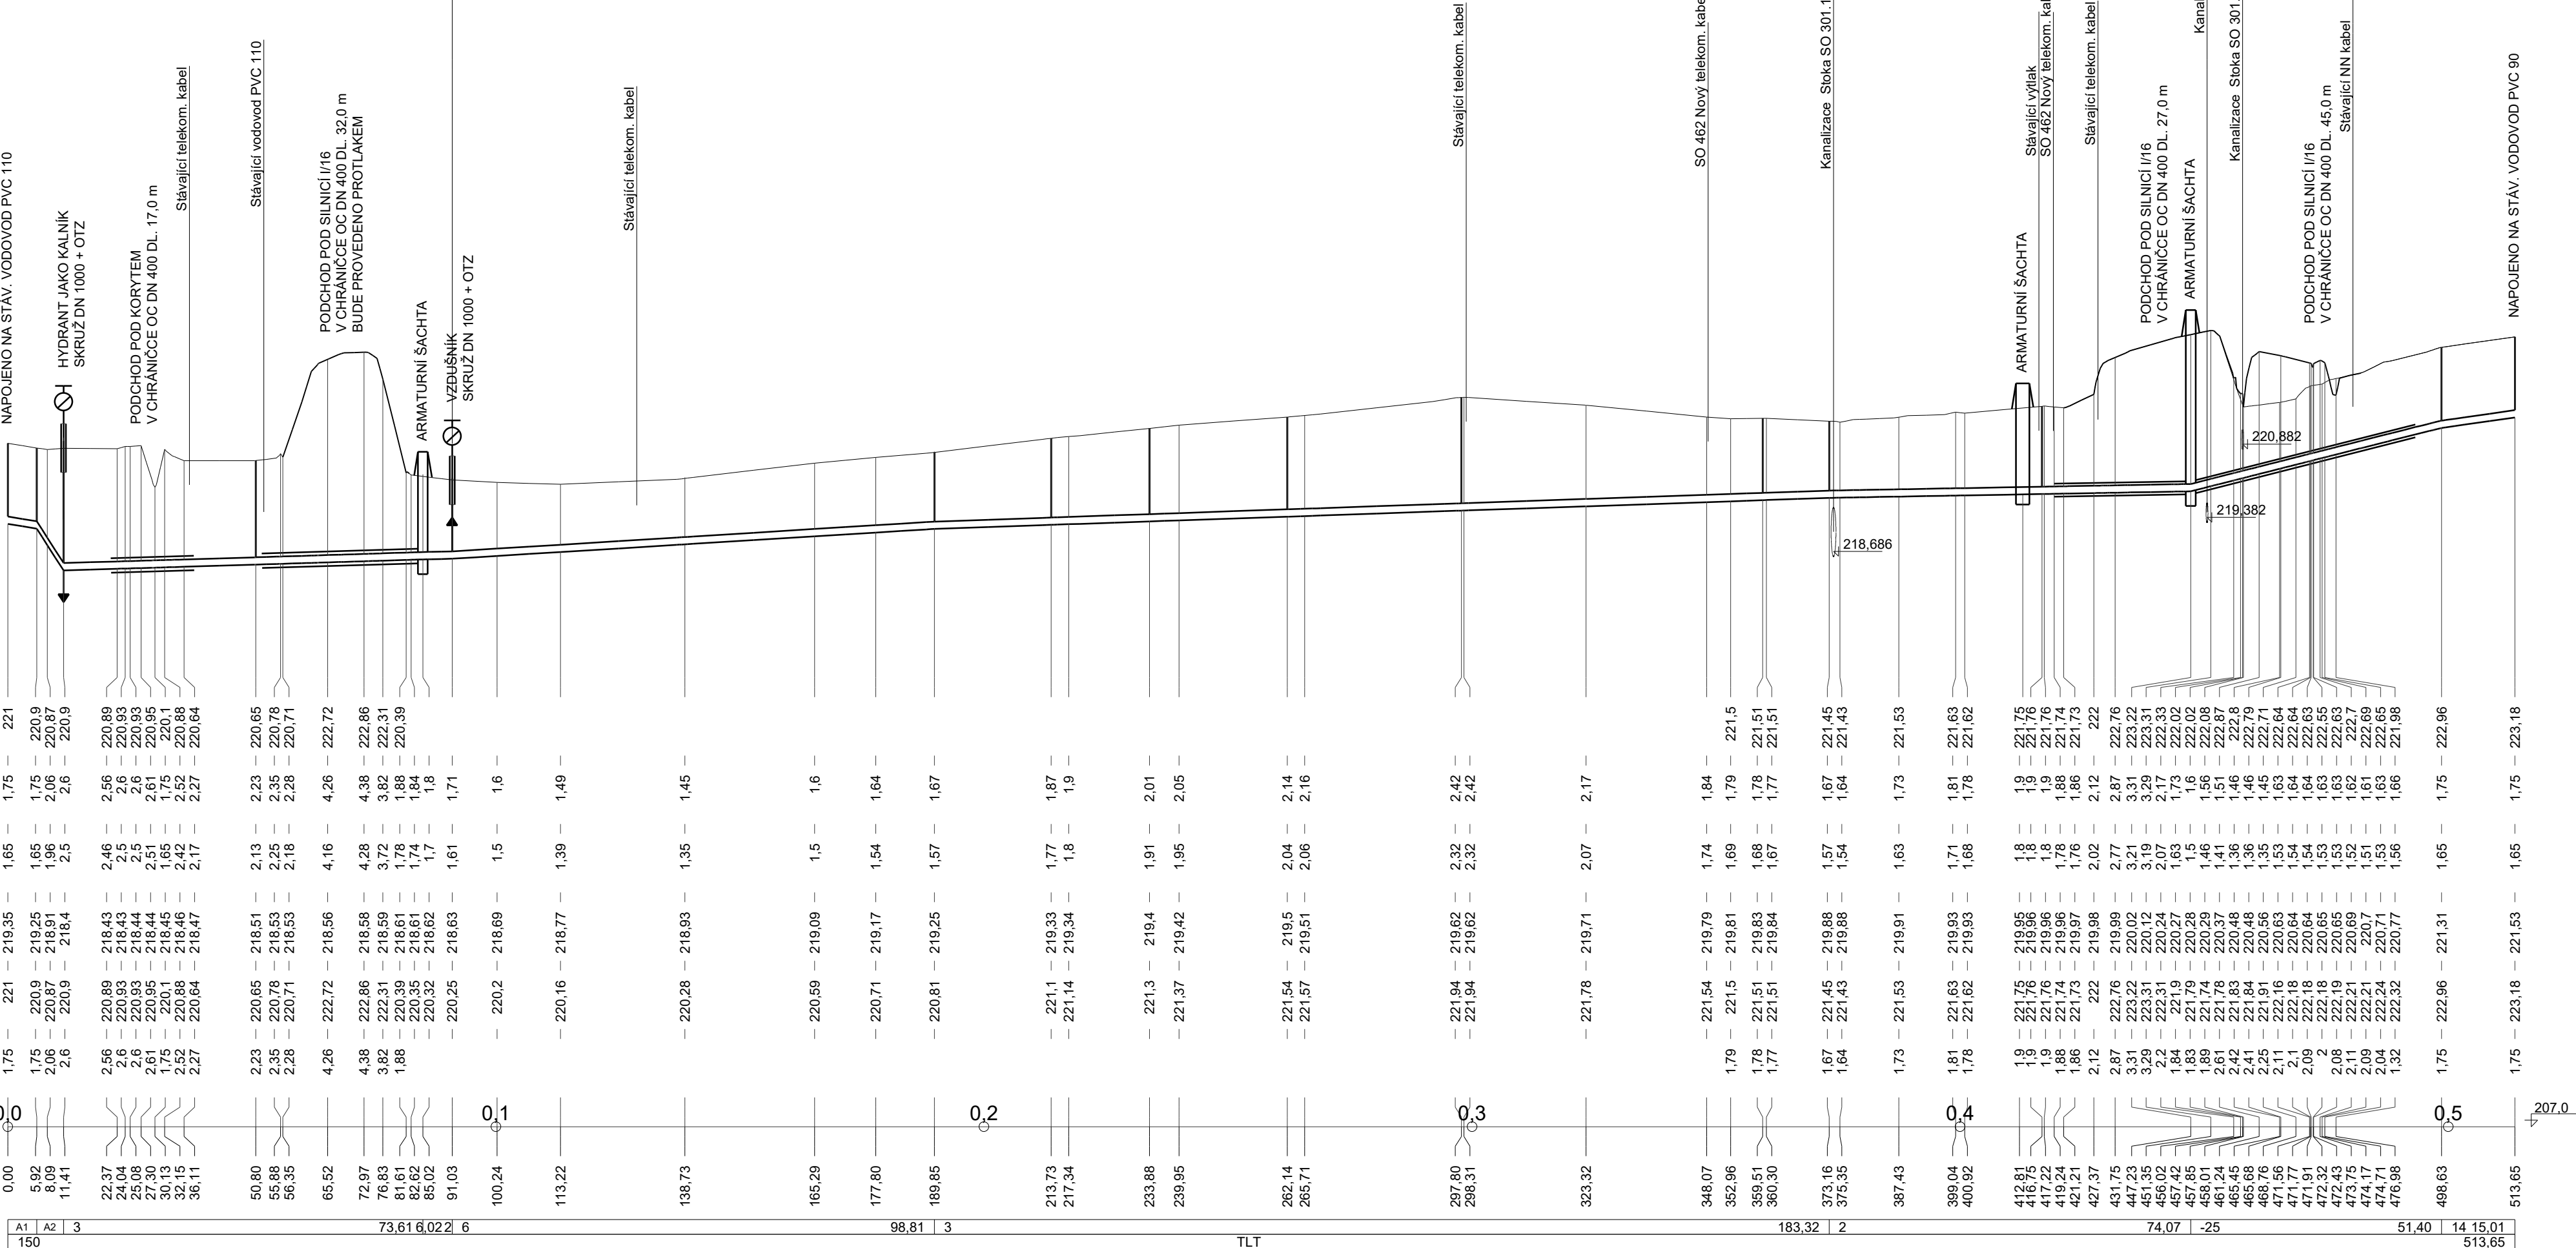

Souřadnicový systém: S-JTSK
Výškový systém: Bpv

SO 344 Přeložka vodovodu v MÚK Martinovice

Objednatel:



ŘEDITELSTVÍ
SILNIC
A DÁLNIC

Ředitelství silnic a dálnic s. p.
Čerčanská 2023/12, Krč, 140 00 Praha 4

Zhotovitel:



Valbek, spol. s r.o.
Vaňurova 505/17
460 07 Liberec 3



Zhotovitel:

Valbek, spol. s r.o.
Vaňurova 505/17
460 07 Liberec 3

Vypracoval	BC. Š. HORECKÝ	Zak. číslo	21-L113-001
Zodp. projektant	ING. J. VANCL	Datum	02/2025
Tech. kontrola	ING. D. LANDA	Stupeň	PDPS
Akce	I/16 MLADÁ BOLESLAV - MARTINOVICE	Počet formátů	4 x A4
		Měřítko	1 : 1000 / 100
		Č. přílohy	Paré
Příloha	PODÉLNÝ PROFIL		3