


POTRUBÍ, TVAROVKY	Počet	Jednotka
POTRUBÍ		
POTRUBÍ TLT DN 150 min. CLASS 64	513,7	m
CHRÁNIČKA OC DN 400 (tl. stěny 10 mm)	121,0	m
TVAROVKY		
TP DN 150 DL. 0,25 m	1	ks
TP DN 150 DL. 1 m	1	ks
TP DN 150 DL. 1,5 m	1	ks
TP DN 50 DL. 0,3 m	2	ks
TP DN 80 DL. 0,25 m	1	ks
A DN 150 / 80	2	ks
E DN 150	4	ks
F DN 150	1	ks
F DN 150 S KOTVOU	1	ks
JISTĚNÁ PŘÍRUBA DN 150	2	ks
K 90° DN 80	6	ks
KOLENO 11,25° DN 150	6	ks
KOLENO 22,5° DN 150	6	ks
KOLENO 45° DN 150	3	ks
KŘÍŽ TLT DN 150/80	1	ks
PPL 90° DN 80	2	ks
R DN 150 / 80	1	ks
R DN 80/50	4	ks
SPOJKA DN 150/100 - JISTĚNÁ PROTI POSUNU - WAGA	1	ks
SPOJKA DN 80 - JISTĚNÁ PROTI POSUNU - WAGA	2	ks
T KUS DN 150/80	2	ks
TLT SEK DN 150 DL. 0,5 m	1	ks
TLT SEK DN 150 DL. 1 m	18	ks
TLT SEK DN 80 DL. 1 m	1	ks
TP DN 150 S KOTVOU	2	ks
TP DN 80 S KOTVOU	1	ks
U.V.	5	ks
Z.S. TELESKOP.	3	ks
ARMATURY		
FILTR DN 80	1	ks
HYDRANT PODZEMNÍ DN 80	1	ks
VODOMĚR PŘÍRUBOVÝ DN 50	2	ks
VZDUŠNÍK DN 80	1	ks
ZA./ODVZDUŠŇOVACÍ SOUPRAVA DN 80	1	ks
ZPĚTNÁ KLAPKA DN 80	1	ks
Š DN 150	2	ks
Š DN 80	6	ks
JINÉ		
B. BLOK "A" - (0,93x0,35x1,1)m	2	ks
B. BLOK 11,25° - (0,28x0,25x0,6)m	6	ks
B. BLOK 22,5° - (0,4x0,36x0,65) m	6	ks
B. BLOK 45° - (0,73x0,35x0,82) m	3	ks
BB	3	ks
R.K. DN 150	1	ks
R.K. DN 80	4	ks

SPOJKY, TVAROVKY A ARMATURY DLE POŽADAVKU PROVOZOVATELE
LITINOVÉ POTRUBÍ BUDE NA KLUZNÝCH OBJÍMKÁCH PO 1 METRECH
CHRÁNIČKY BUDOU UTĚSNĚNY MANŽETAMI

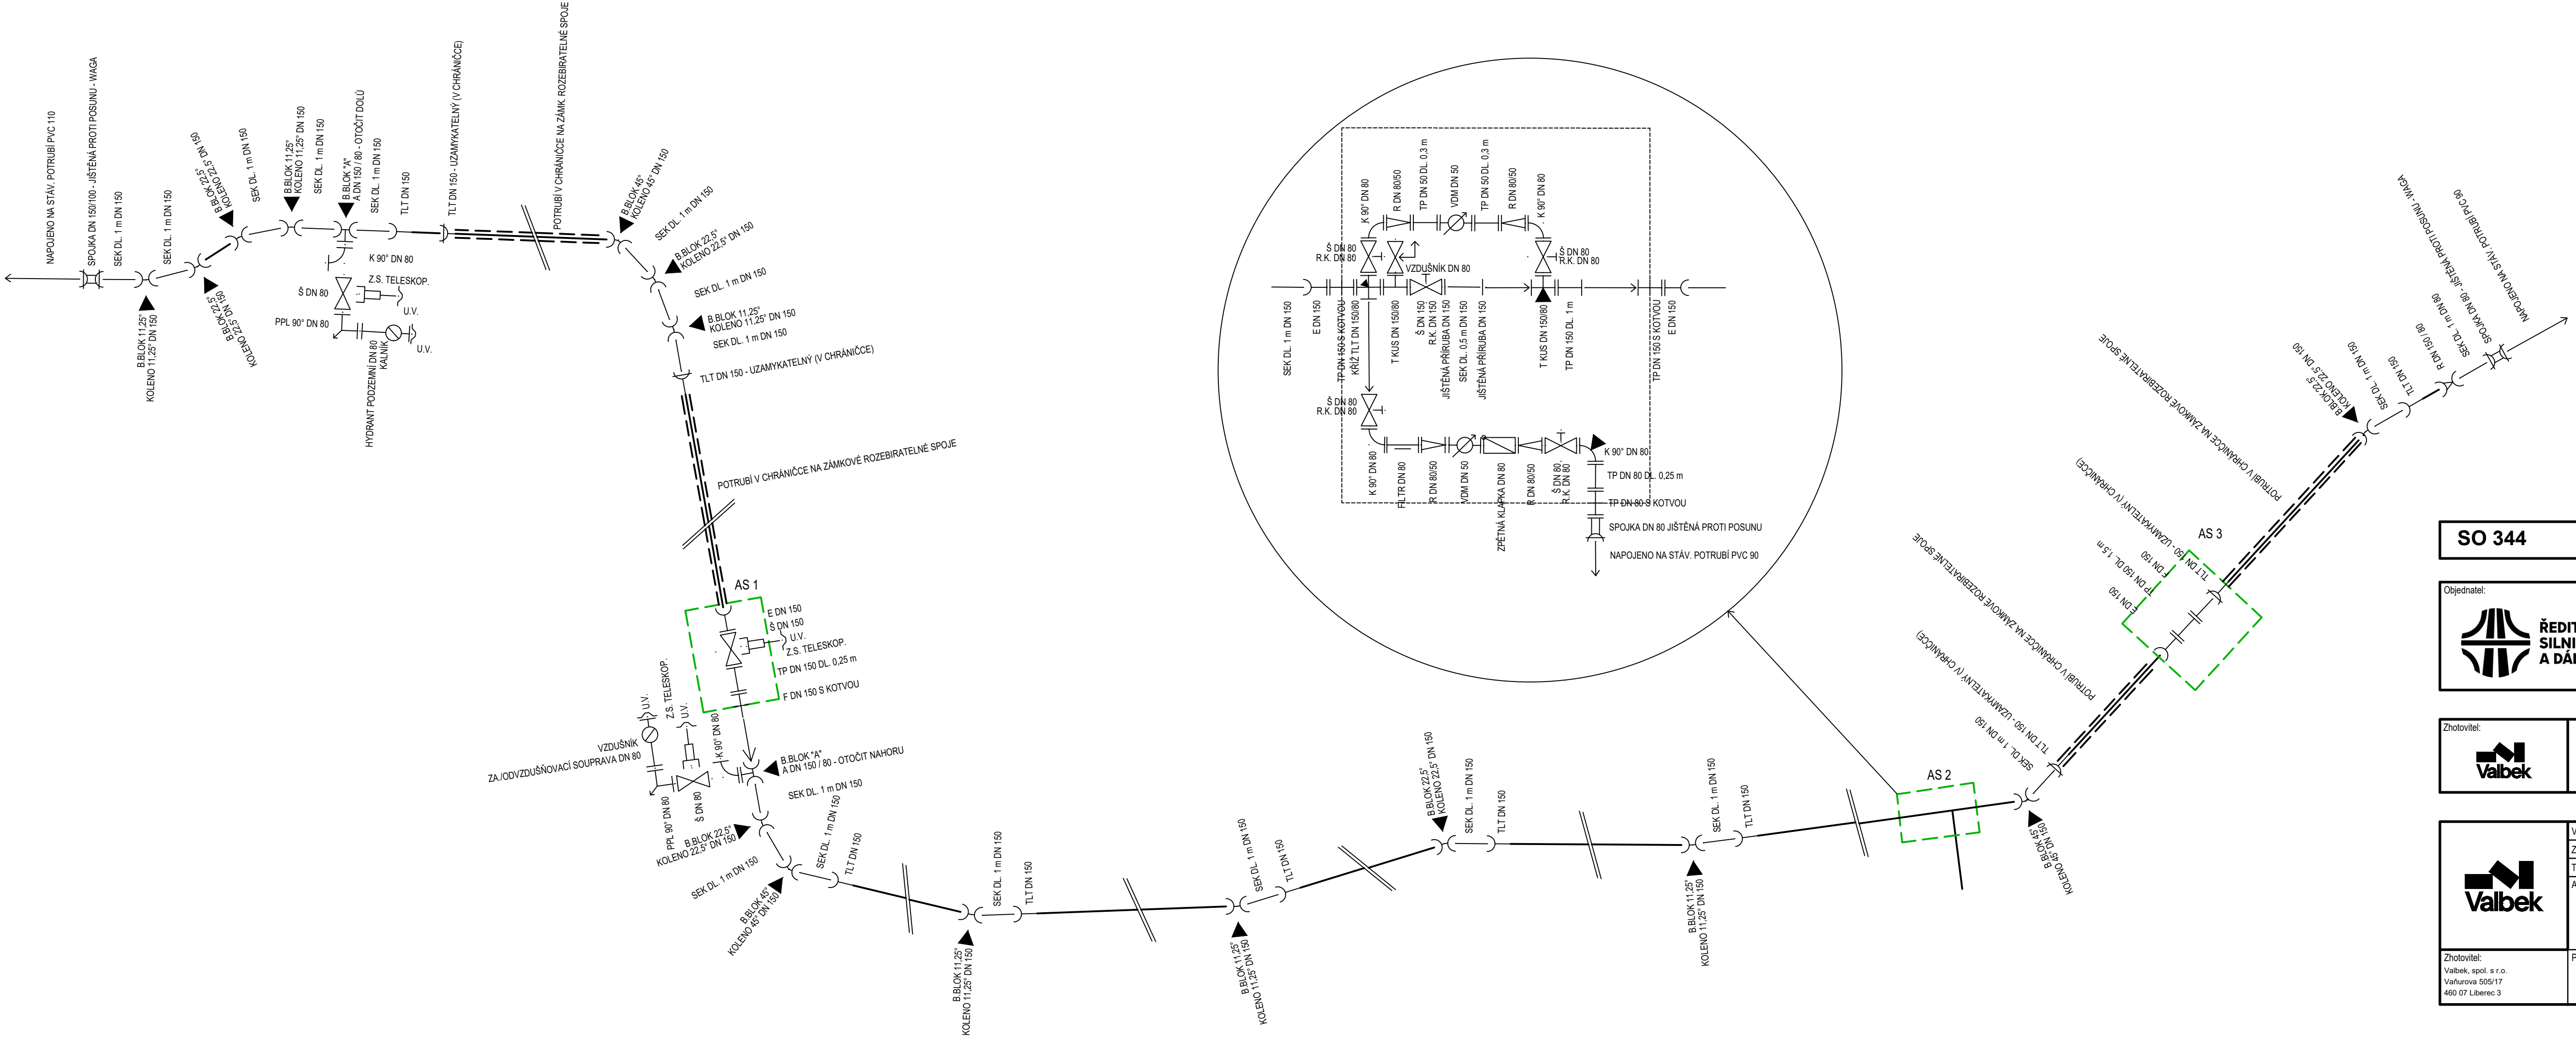

SO 344 Přeložka vodovodu v MÚK Martinovice

Objednatel:



Ředitelství silnic a dálnic
Čerčanská 2023/12, Krč, 140 00 Praha 4

Ředitelství silnic a dálnic s.p.

Zhotovitel:



Valbek, spol. s r.o.
Vaňurova 505/17
460 07 Liberec 3

HIP:

ING. T. KLIMENT

	Vypracoval	BC. ŠTĚPÁN HORECKÝ		Zak. číslo	21-L113-001	
	Zodp. projektant	ING. JIŘÍ VANCL		Datum	02/2025	
	Tech. kontrola	ING. DAVID LANDA		Stupeň	PDPS	
	Akce			Počet formátů	4 x A4	
I/16 MLADÁ BOLESLAV - MARTINOVICE					Měřitko	-
					Č. přílohy	Paré
Zhotovitel:	Příloha			5		
Valbek, spol. s r.o. Vaňurova 505/17 460 07 Liberec 3	KLADÉČSKÝ PLÁN					