



ŘEZ 1-1 1:25

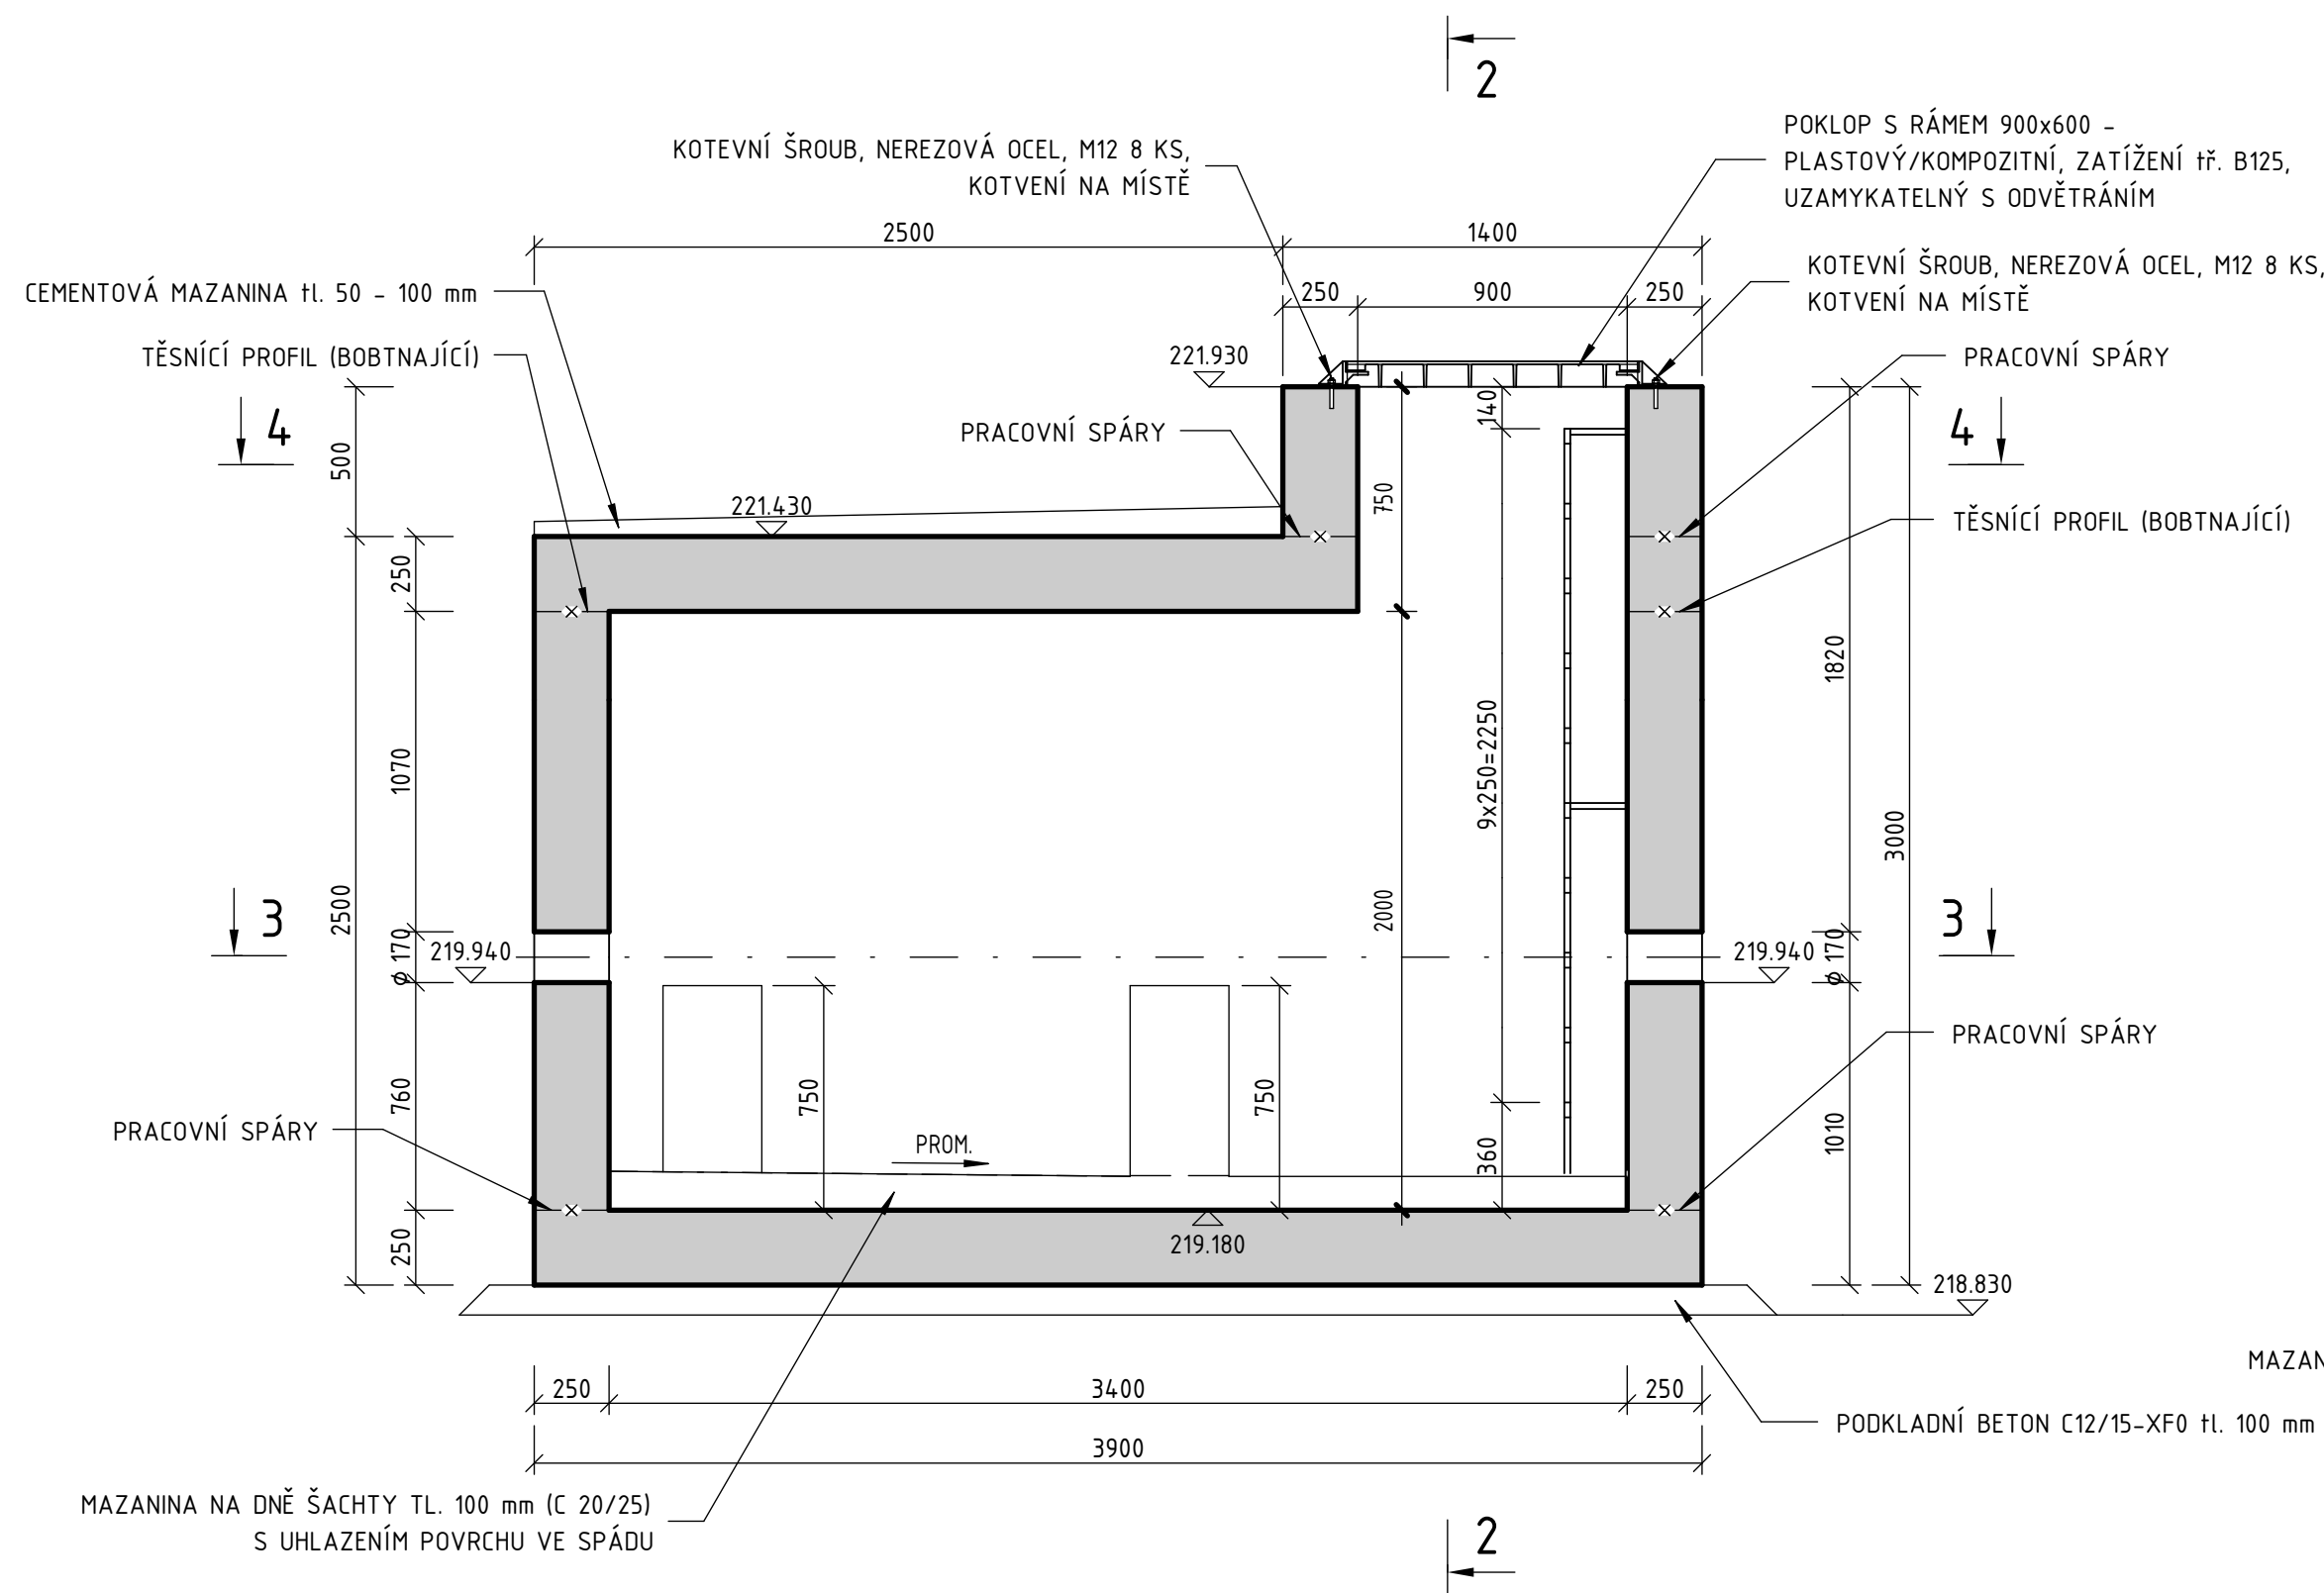

ŘEZ 2-2 1:25

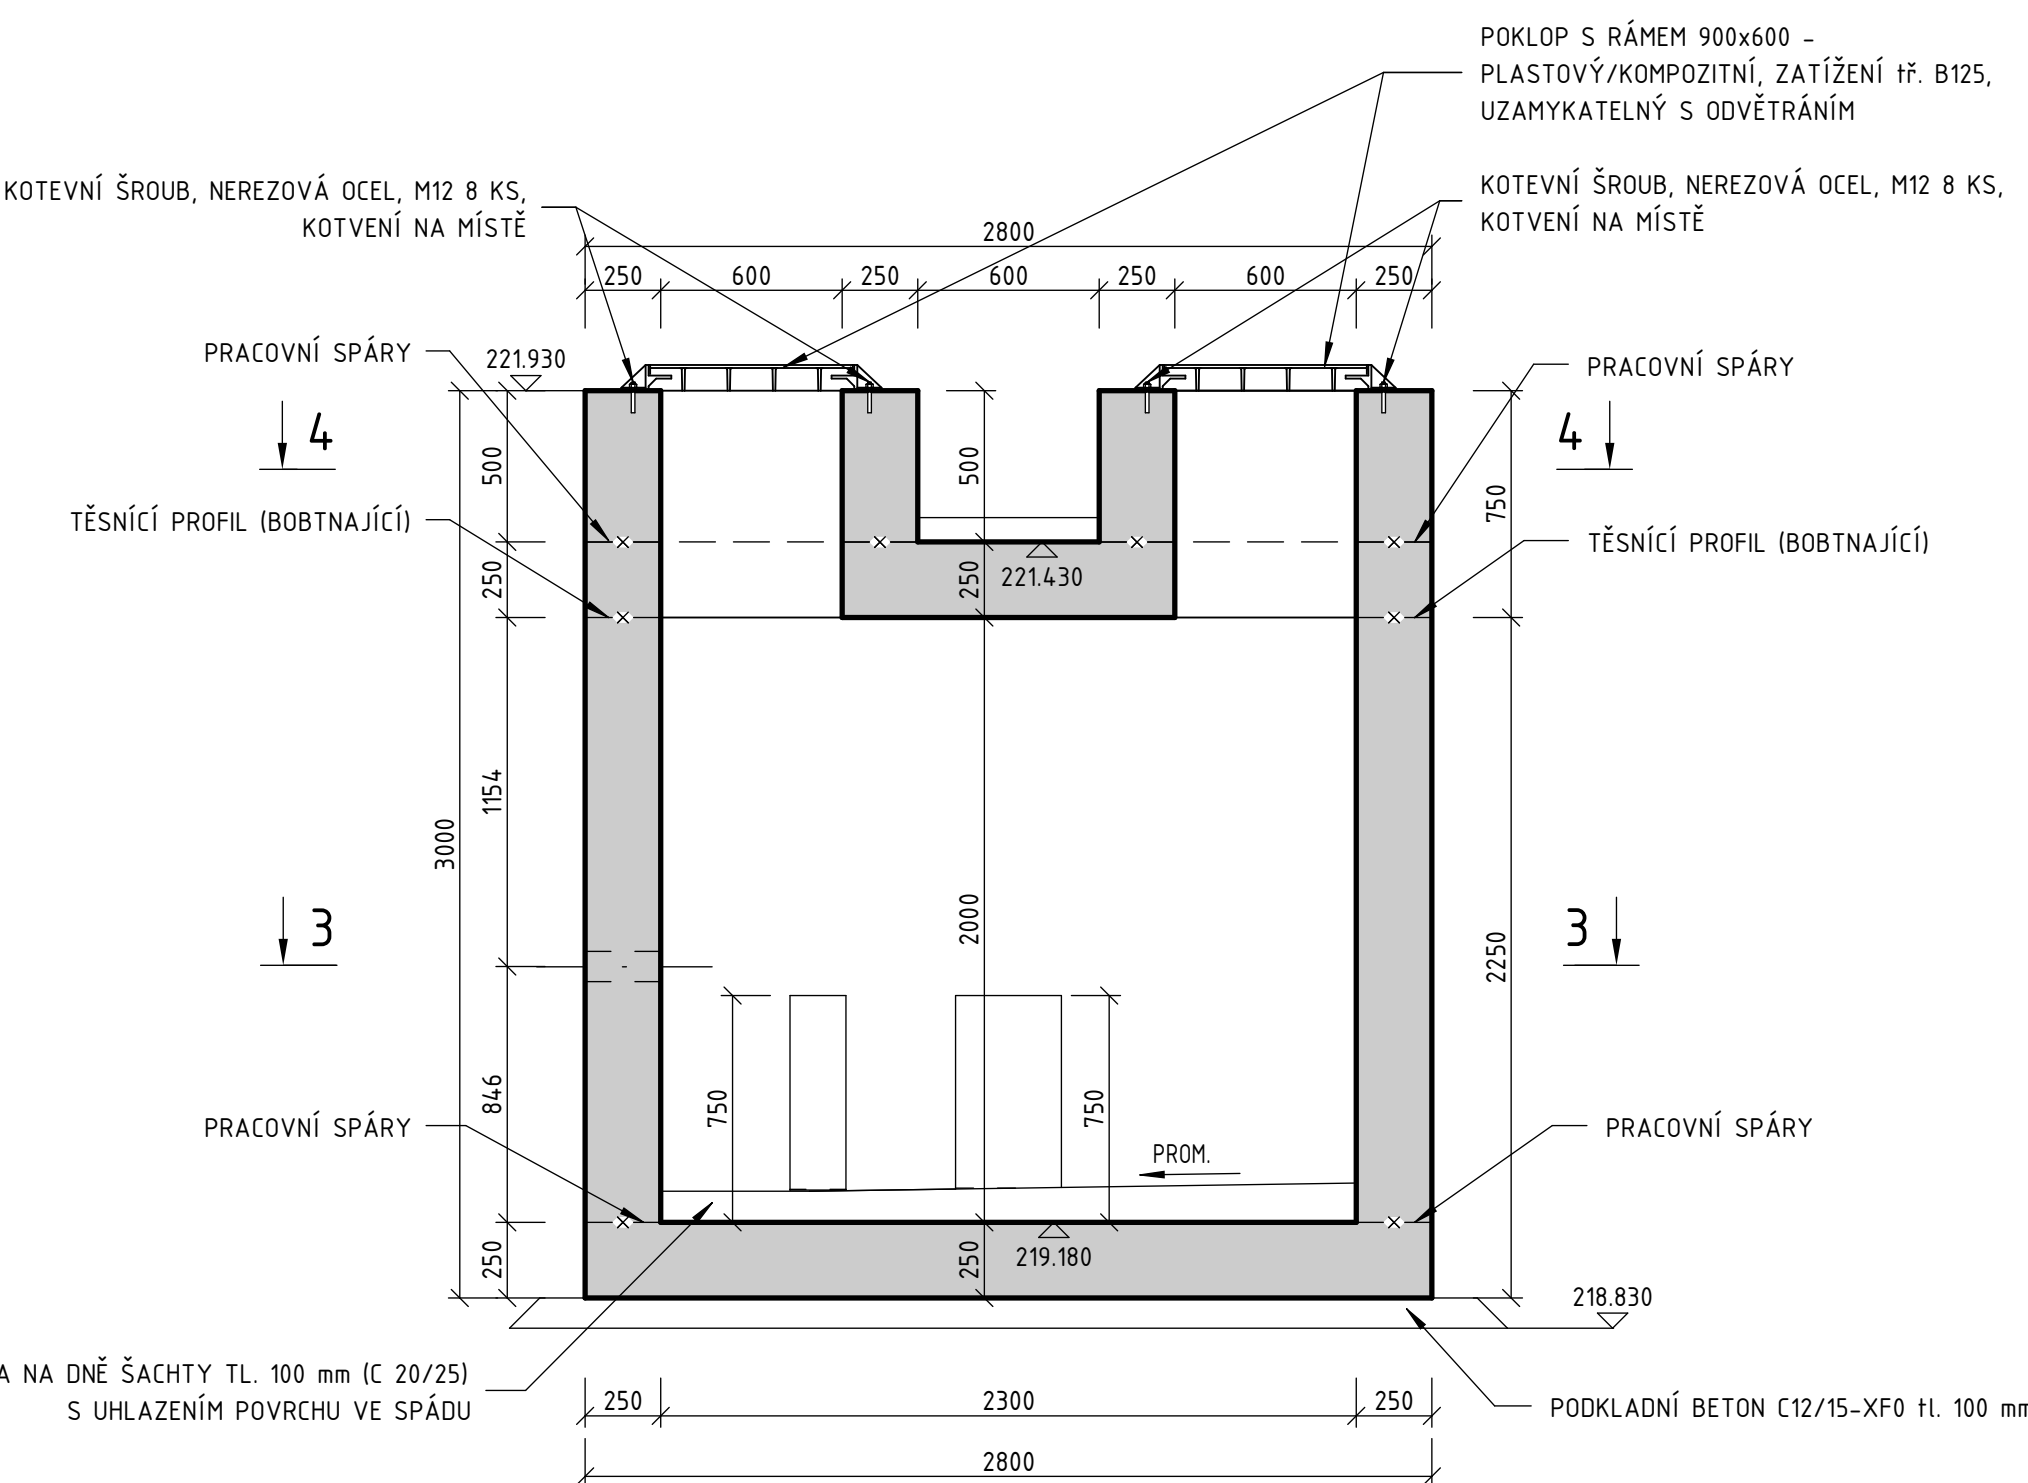

POZNÁMKY:

- VIZ VÝKRES - "6.1 ARMATURNÍ ŠACHTA AŠ2 - VÝKRES VYSTROJENÍ A ZALOŽENÍ"

BETON

JÍMKA

KRYTÍ

VŠECHNY PLOCHY

OCEL

BETONÁŘSKÁ

ČSN EN 206+A2

C30/37-XF3


MINIMÁLNÍ / JMENOVITÉ

45mm / 50 mm


ČSN EN 10027-1

B 500B

ŘEZ 3-3 1:25

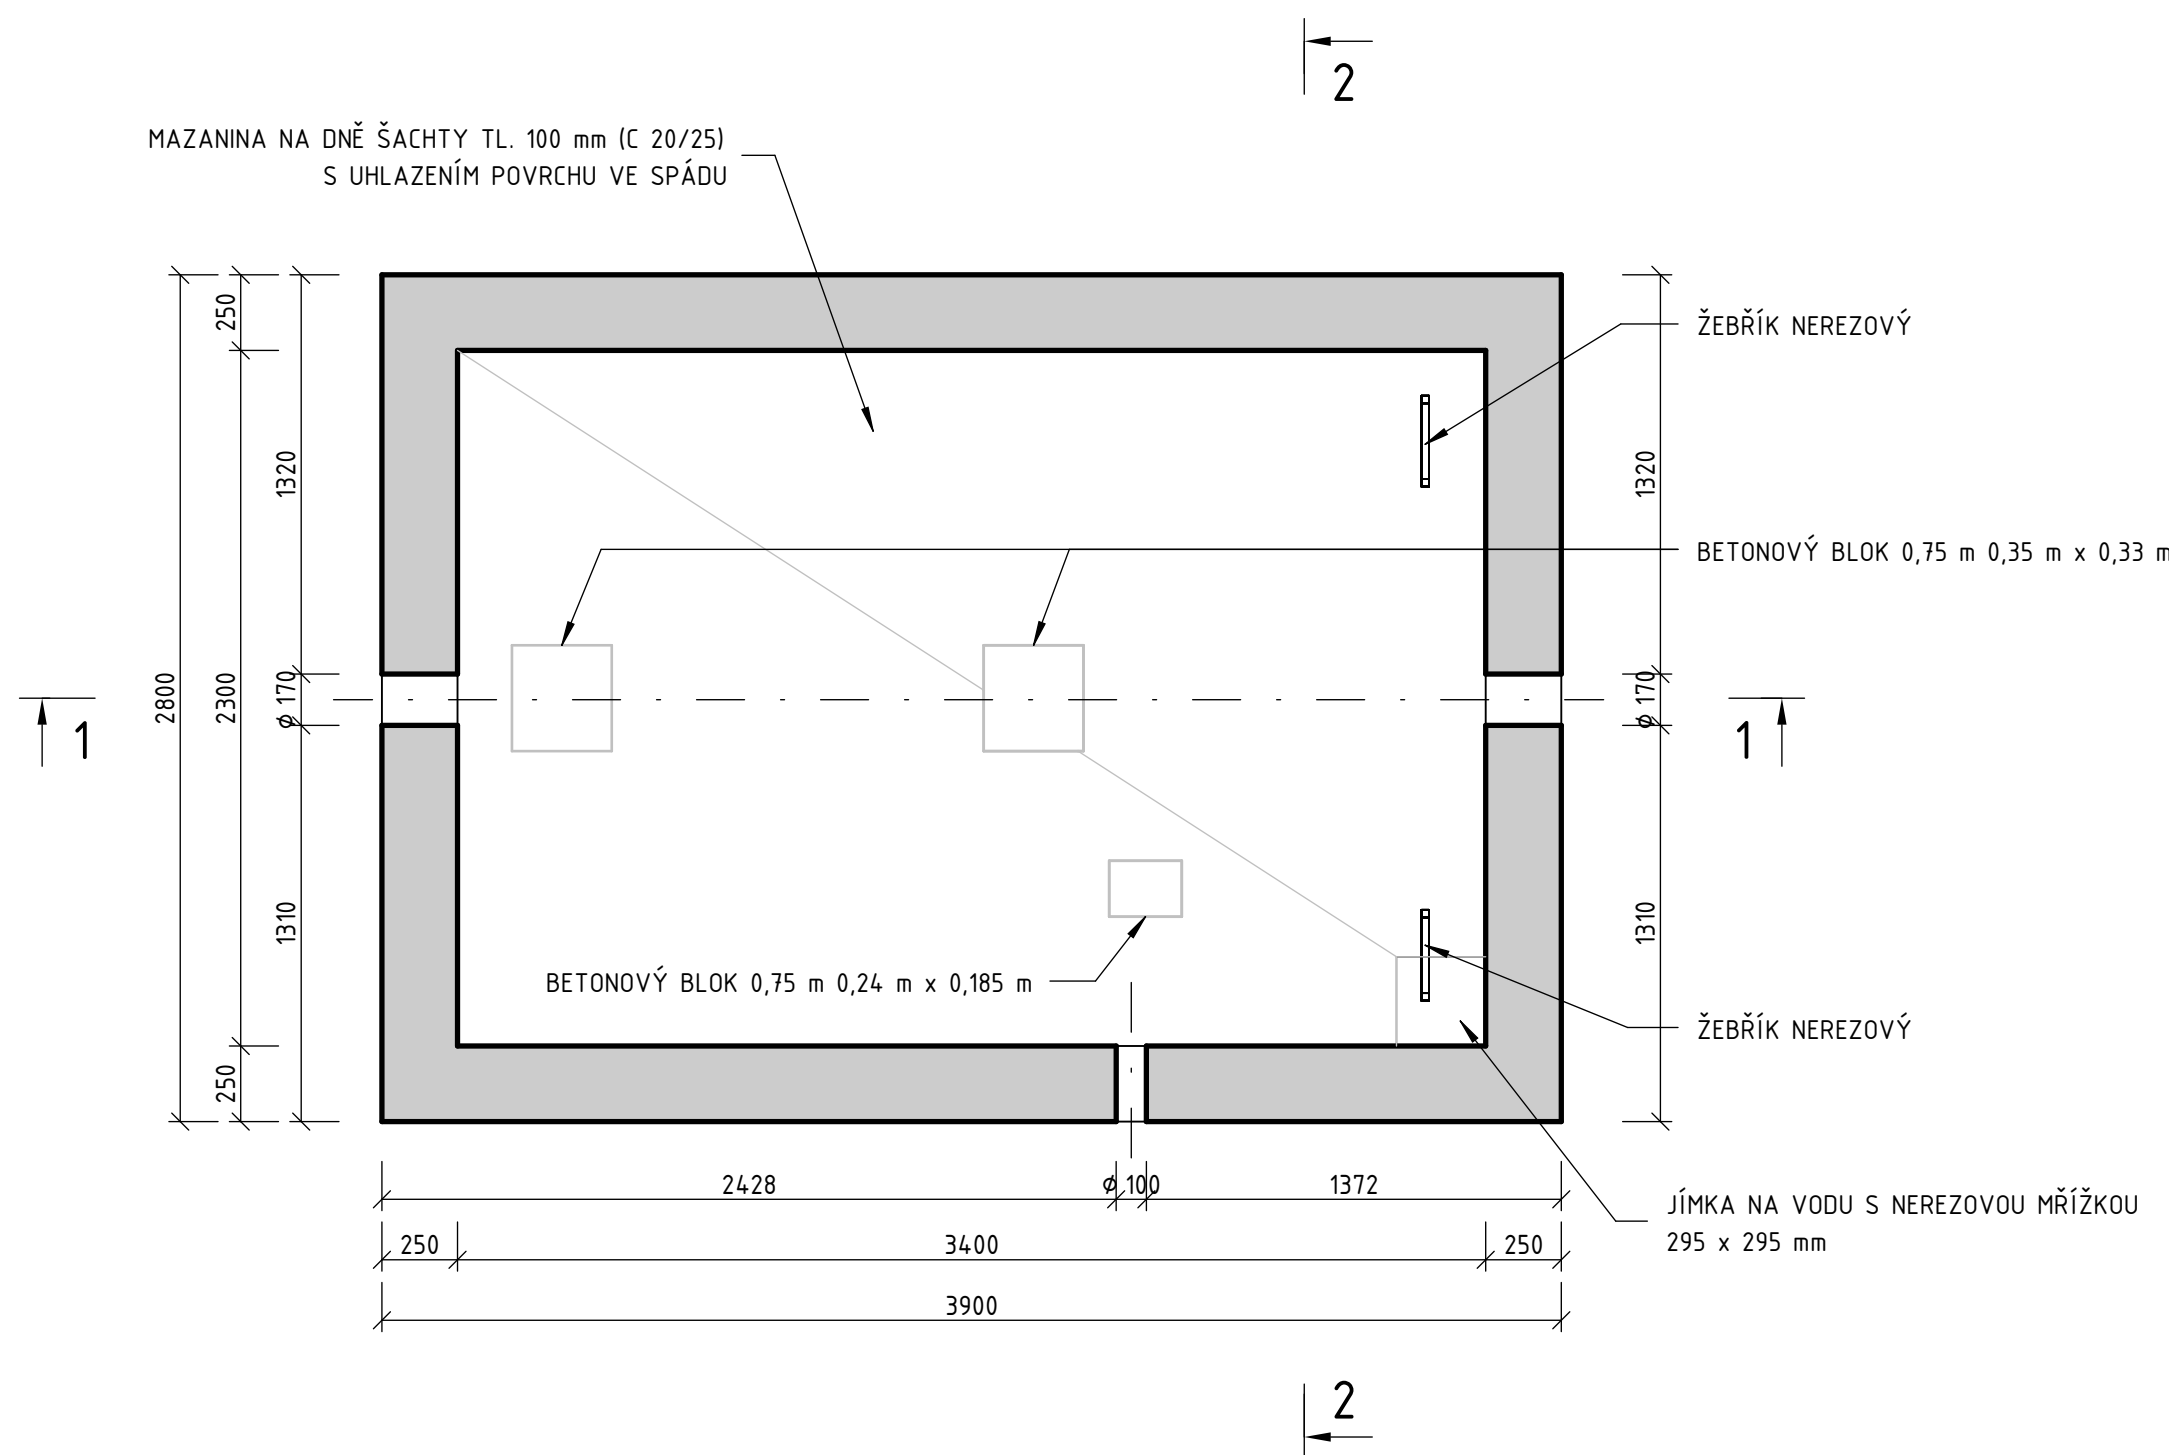

ŘEZ 4-4 1:25

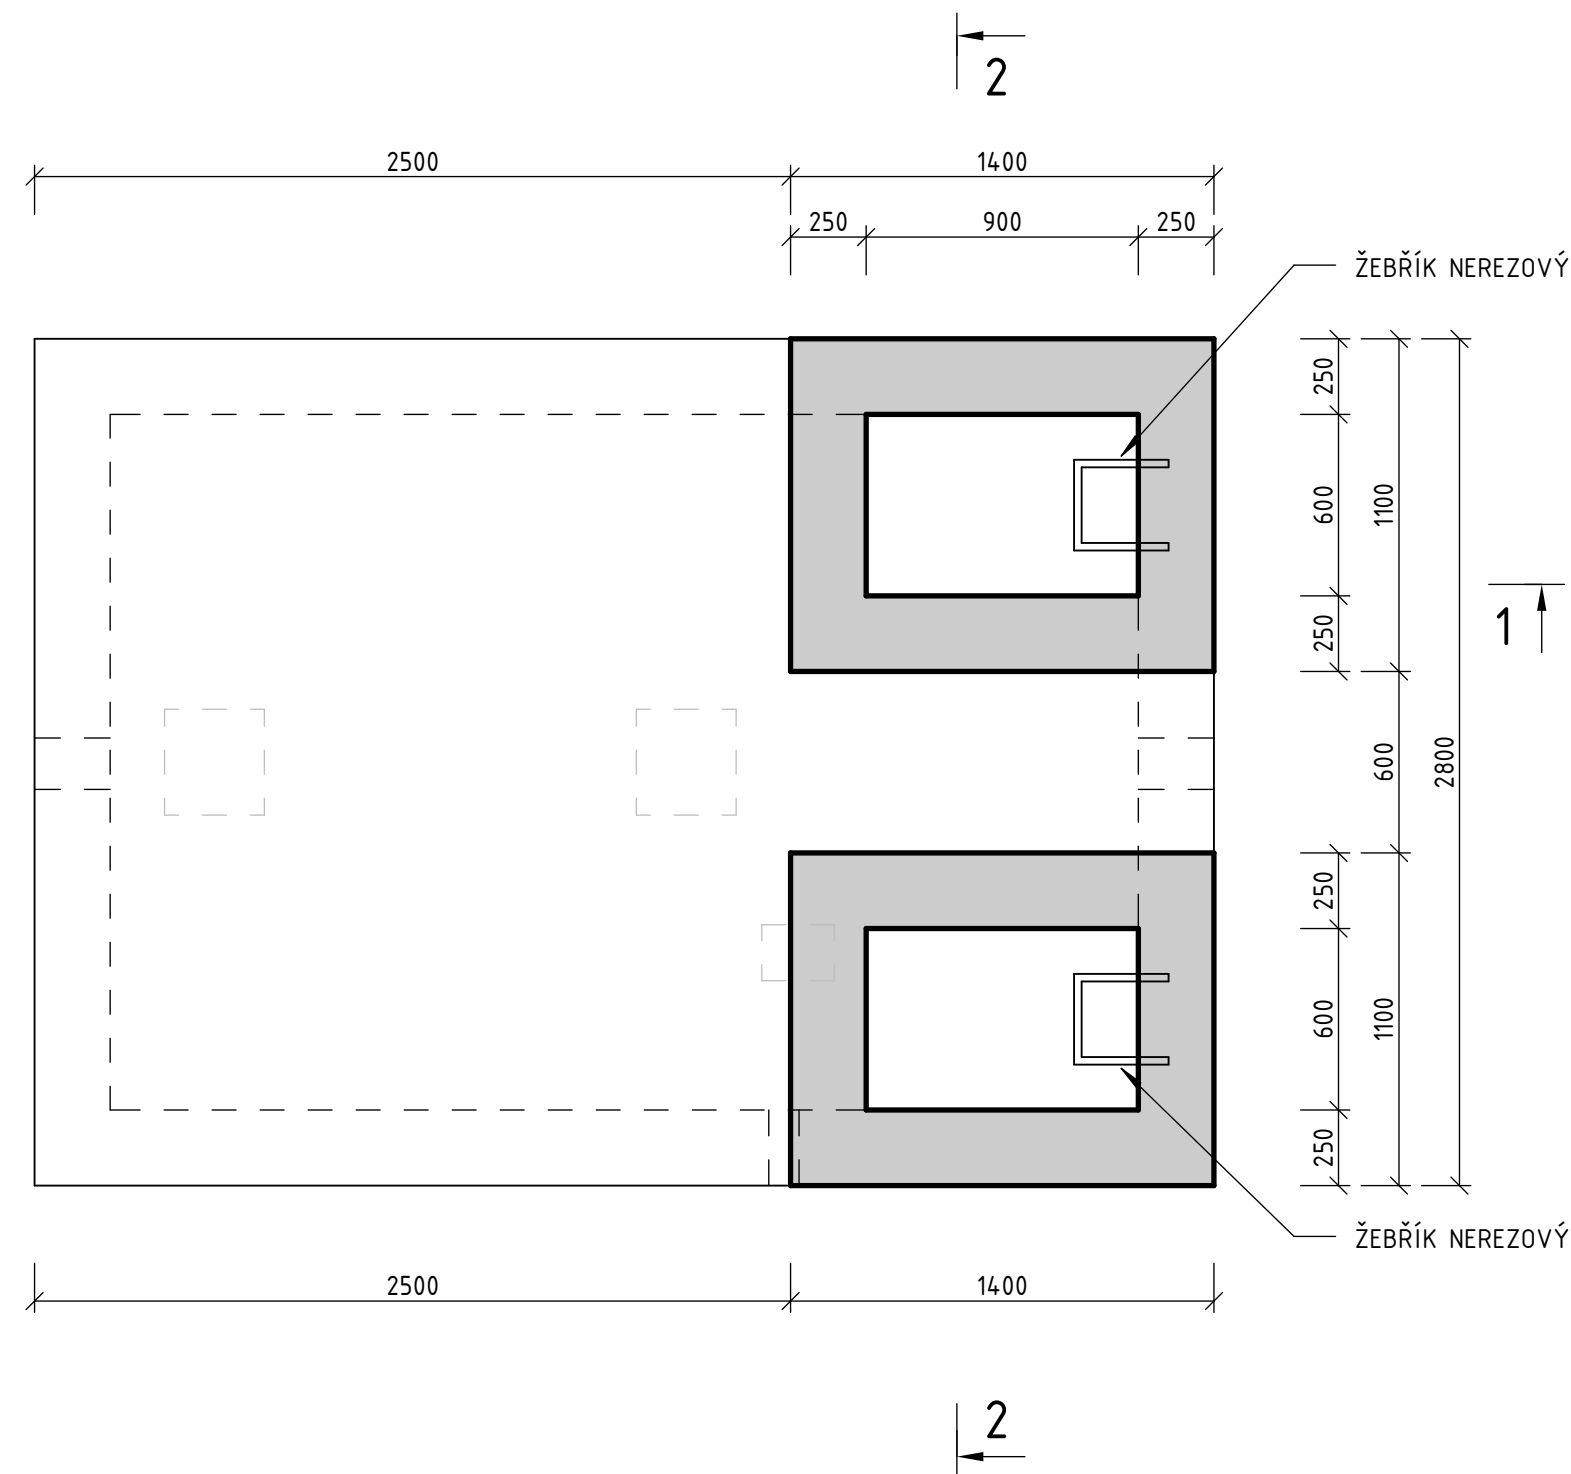

Souřadnicový systém: S-JTSK
Výškový systém: Bpv

SO 344 Přeložka vodovodu v MÚK Martinovice

Objednatel:
ŘEDITELSTVÍ SILNIC A DÁLNIC
Ředitelství silnic a dálnic s. p.
Čerčanská 2023/12, Krč, 140 00 Praha 4

Zhotovitel:
Valbek, spol. s r.o.
Vaňurova 505/17
460 07 Liberec 3

	Vypracoval	ING. ROMAN NAZARCHUK	Zak. číslo	21-L113-001
	Zodp. projektant	ING. JIŘÍ VANCL	Datum	02/2025
	Tech. kontrola	ING. DAVID LANDA	Stupeň	PDPS
	Akce	I/16 MLADÁ BOLESLAV - MARTINOVICE		Počet formátů
Zhotovitel: Valbek, spol. s r.o. Vaňurova 505/17 460 07 Liberec 3	Příloha ARMATURNÍ ŠACHTA AŠ2 - VÝKRES TVARU		Měřítko	1:25
			Č. přílohy	Paré
			6.3	