



ŘEZ 1-1 1: 25

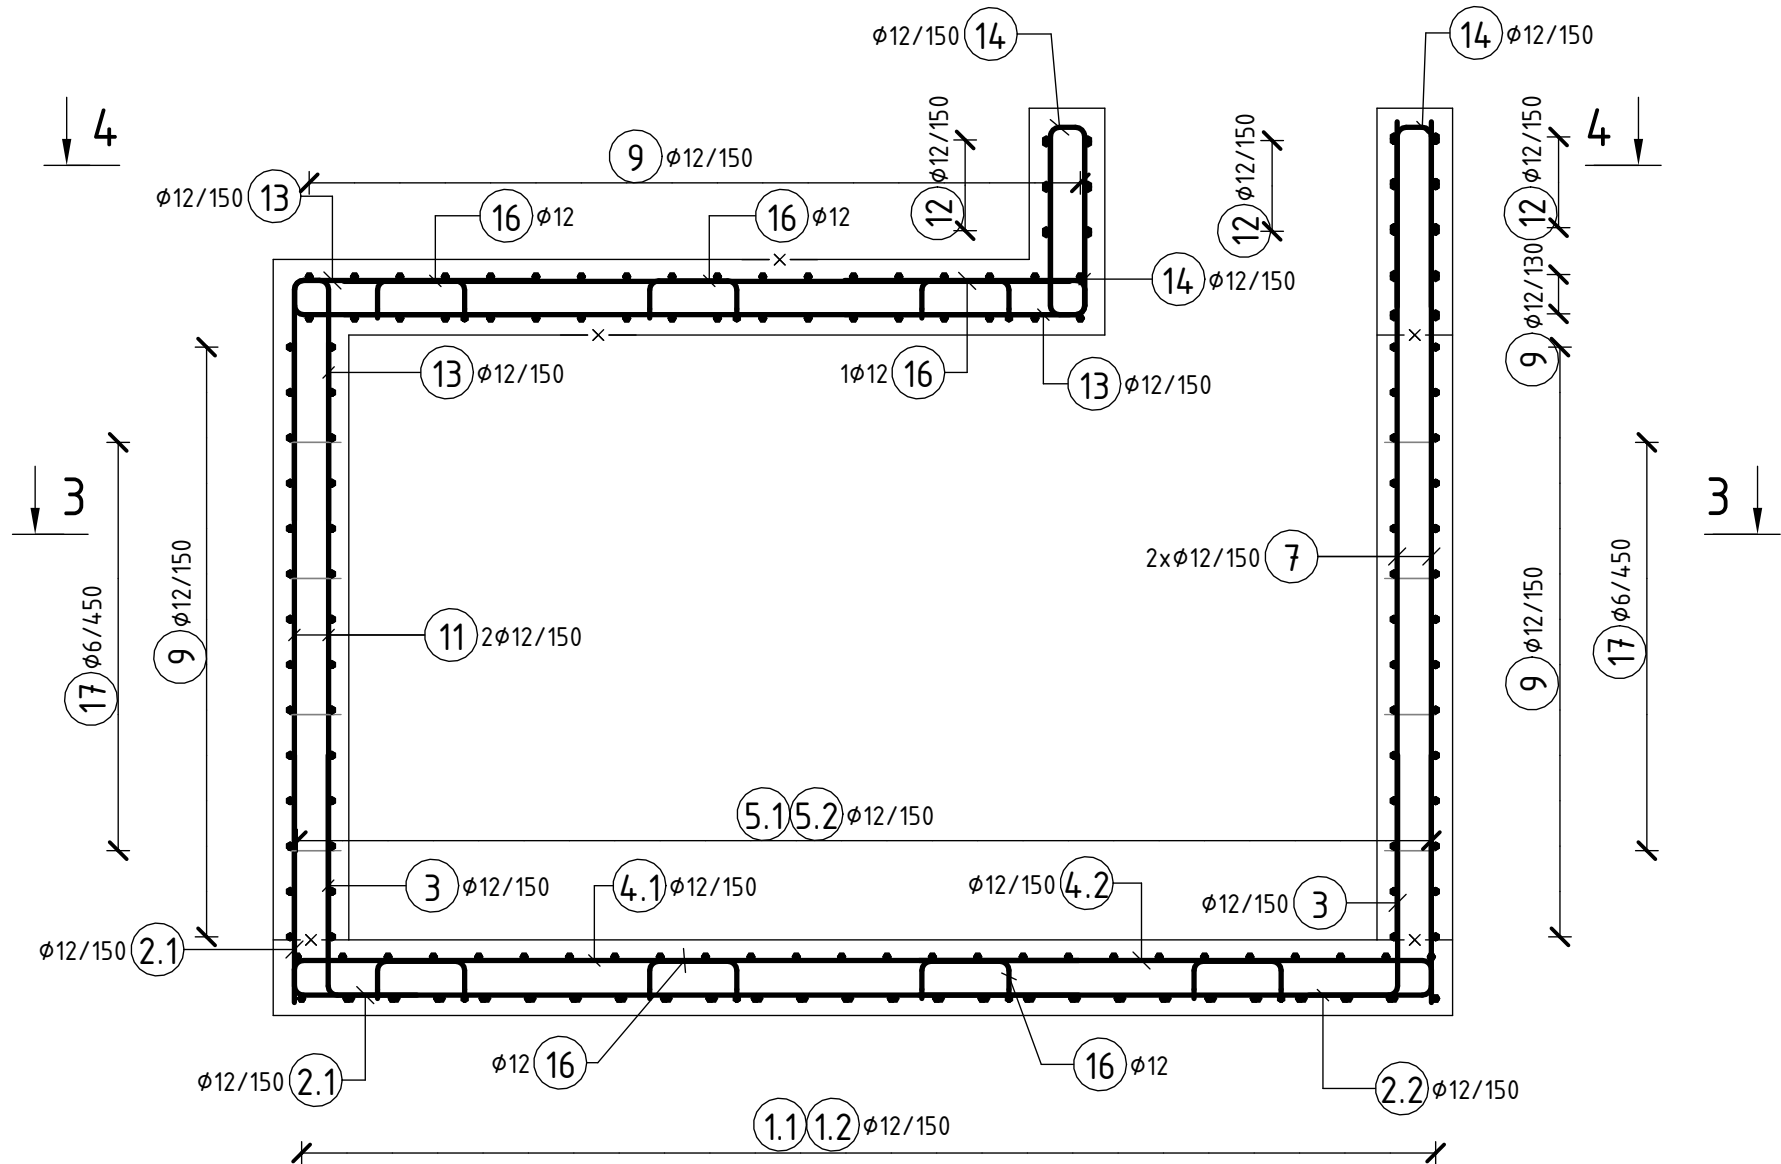

ŘEZ 2-2 1: 25

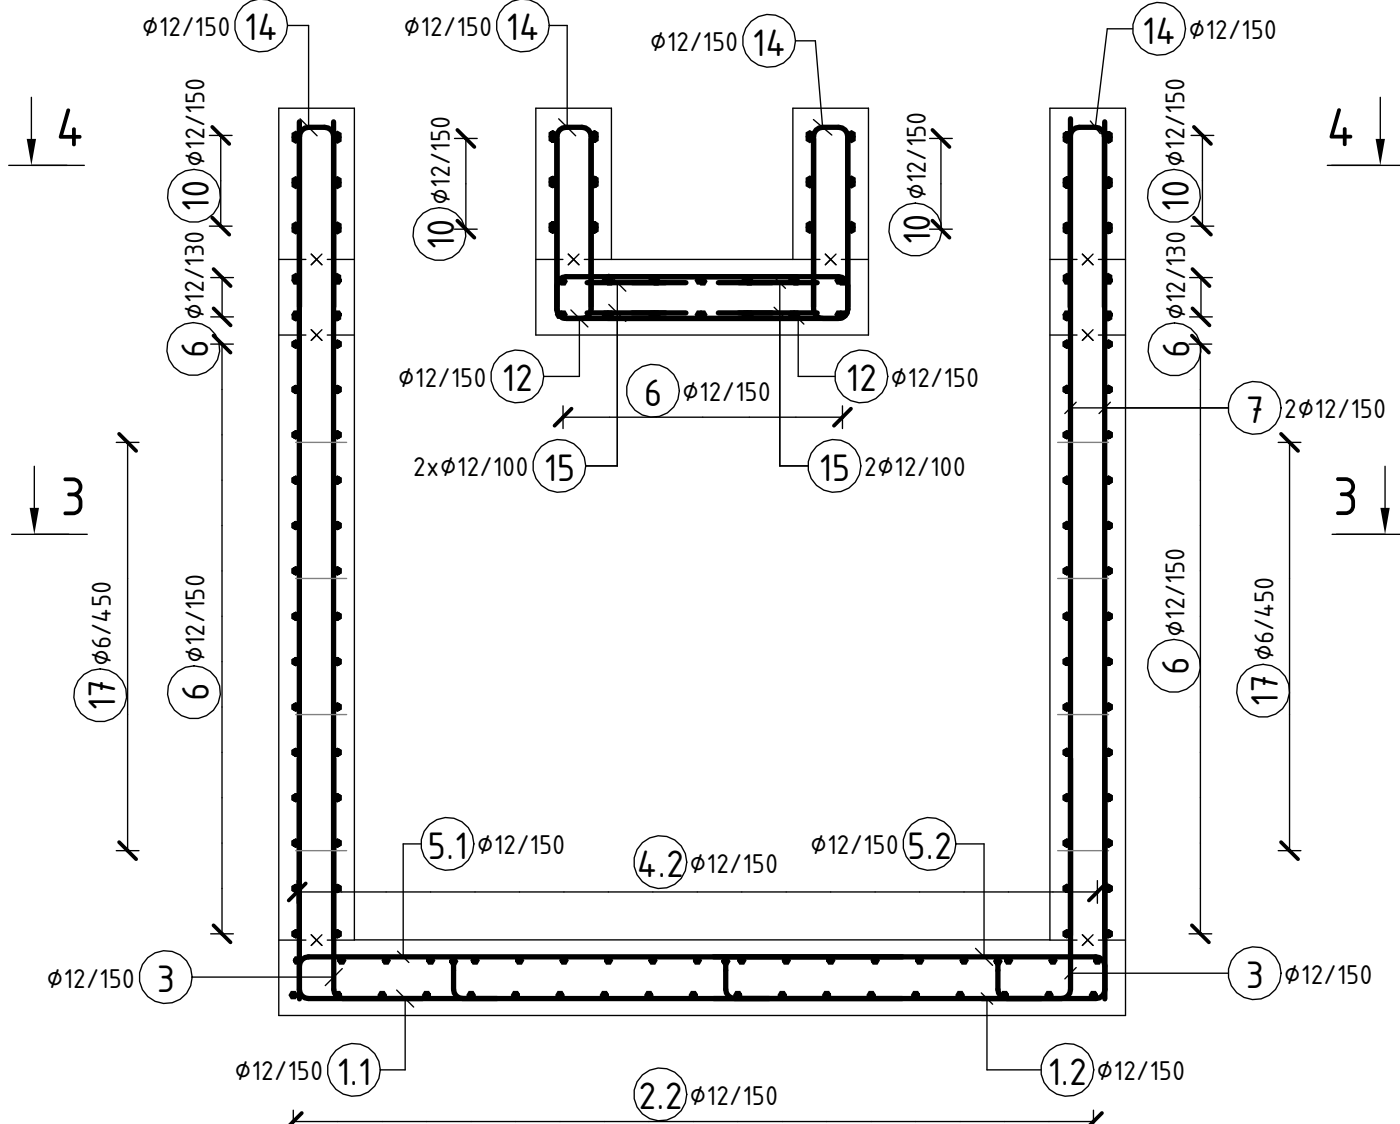

VÝKAZ VÝZTUŽE

ČÍSLO POL.	Ø [mm]	DÉLKA [mm]	POČET [ks]	DÉLKY PODLE Ø [m]	
				d6	d12
1.1	12	2800	26	0	72.8
1.2	12	2100	26	0	54.6
2.1	12	3400	19	0	64.6
2.2	12	2500	19	0	47.5
3	12	1100	86	0	94.6
4.1	12	2745	19	0	52.16
4.2	12	1845	19	0	35.06
5.1	12	2145	26	0	55.77
5.2	12	1445	26	0	37.57
6	12	3400	78	0	265.2
7	12	2700	60	0	162
8	12	2400	22	0	52.8
9	12	2300	96	0	220.8
10	12	2050	24	0	49.2
11	12	1950	108	0	210.6
12	12	1750	190	0	332.5
13	12	1725	89	0	153.56
14	12	1325	82	0	108.68
15	12	1000	8	0	8
16	12	870	21	0	18.27
17	6	305	96	29.28	0
DÉLKA PODLE Ø CELKEM				[m]	29.28
JEDNOTKOVÁ HMOTNOST				[kg/m³]	0.222
HMOTNOST PODLE Ø CELKEM				[kg]	6.48
CELKOVÁ HMOTNOST VÝZTUŽE				[kg]	1867.86

POZNÁMKY:

- V MÍSTĚ POTRUBÍ BUDE VÝZTUŽ OŘÍZNUTA.

BETON

JÍMKY

KRYTÍ

VŠECHNY PLOCHY

OCEL

BETONÁŘSKÁ

ČSN EN 206+A2

C30/37-XF3


MINIMÁLNÍ / JMENOVITÉ

45mm / 50 mm


ČSN EN 10027-1

B 500B


ROZMĚRY VÝZTUŽE JSOU KÓTOVÁNY NA VNĚJŠÍ HRANY

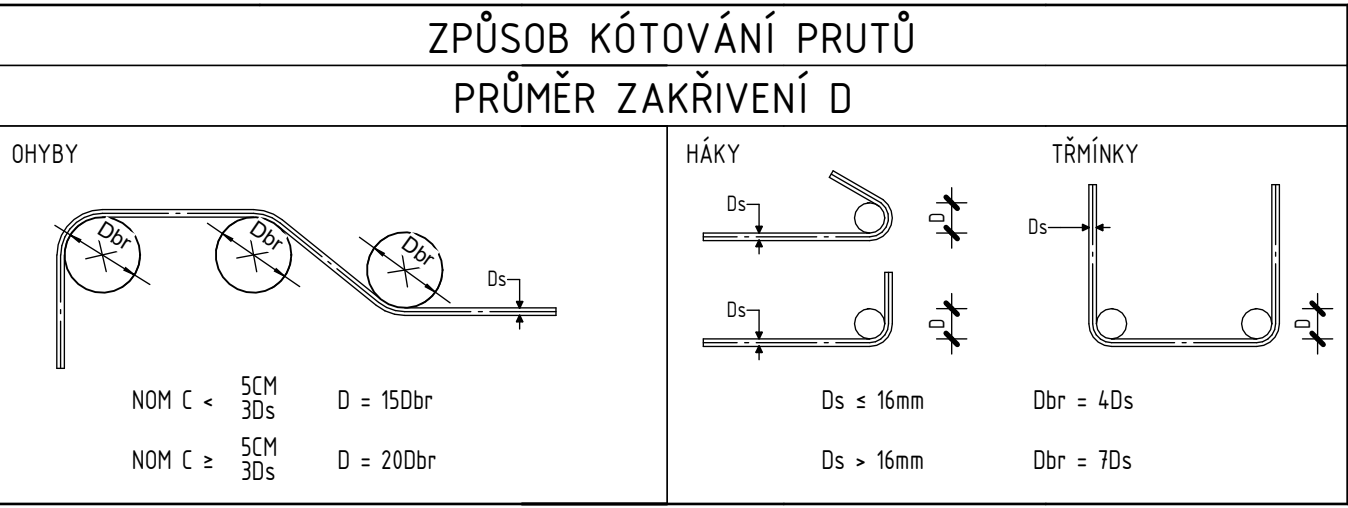

ŘEZ 3-3 1: 25

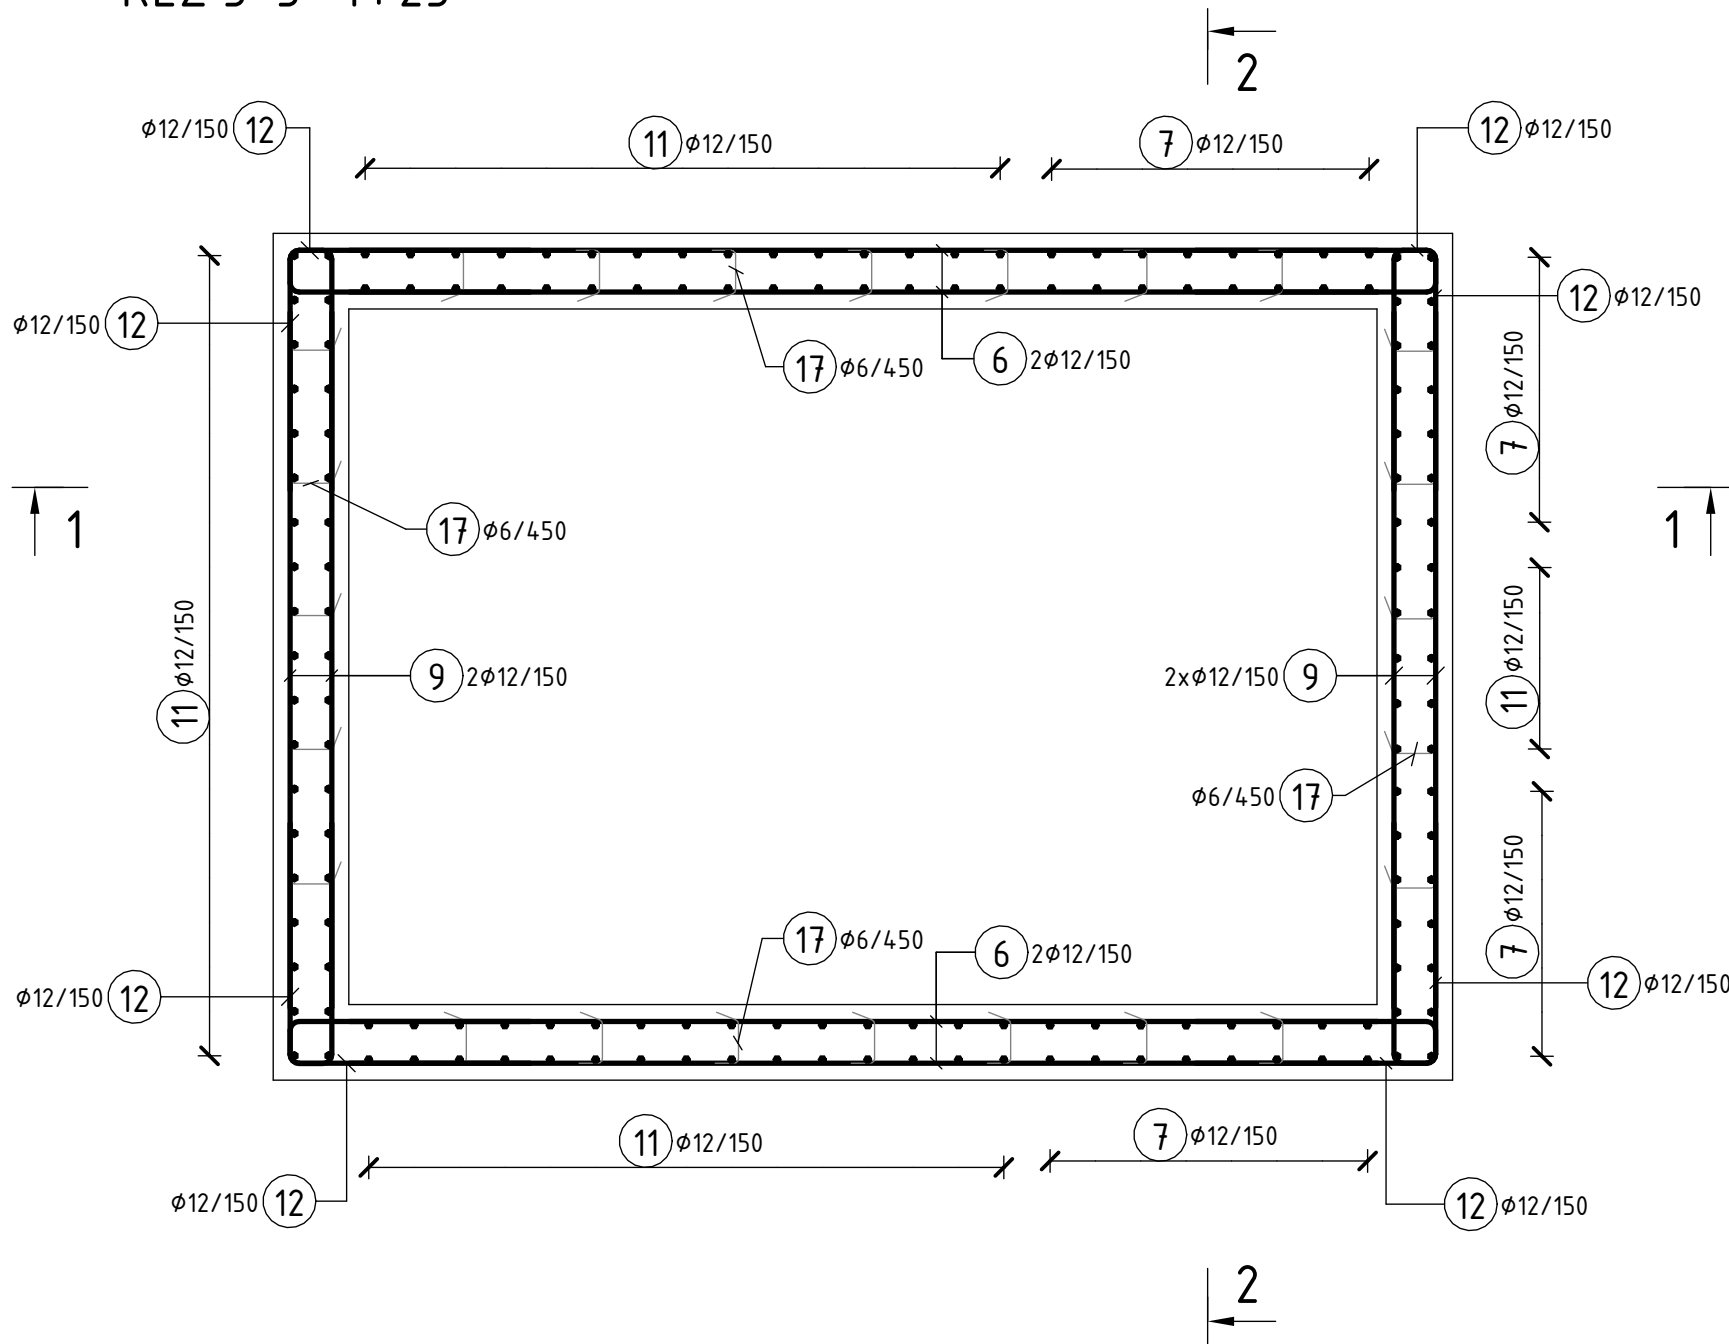

ŘEZ 4-4 1: 25

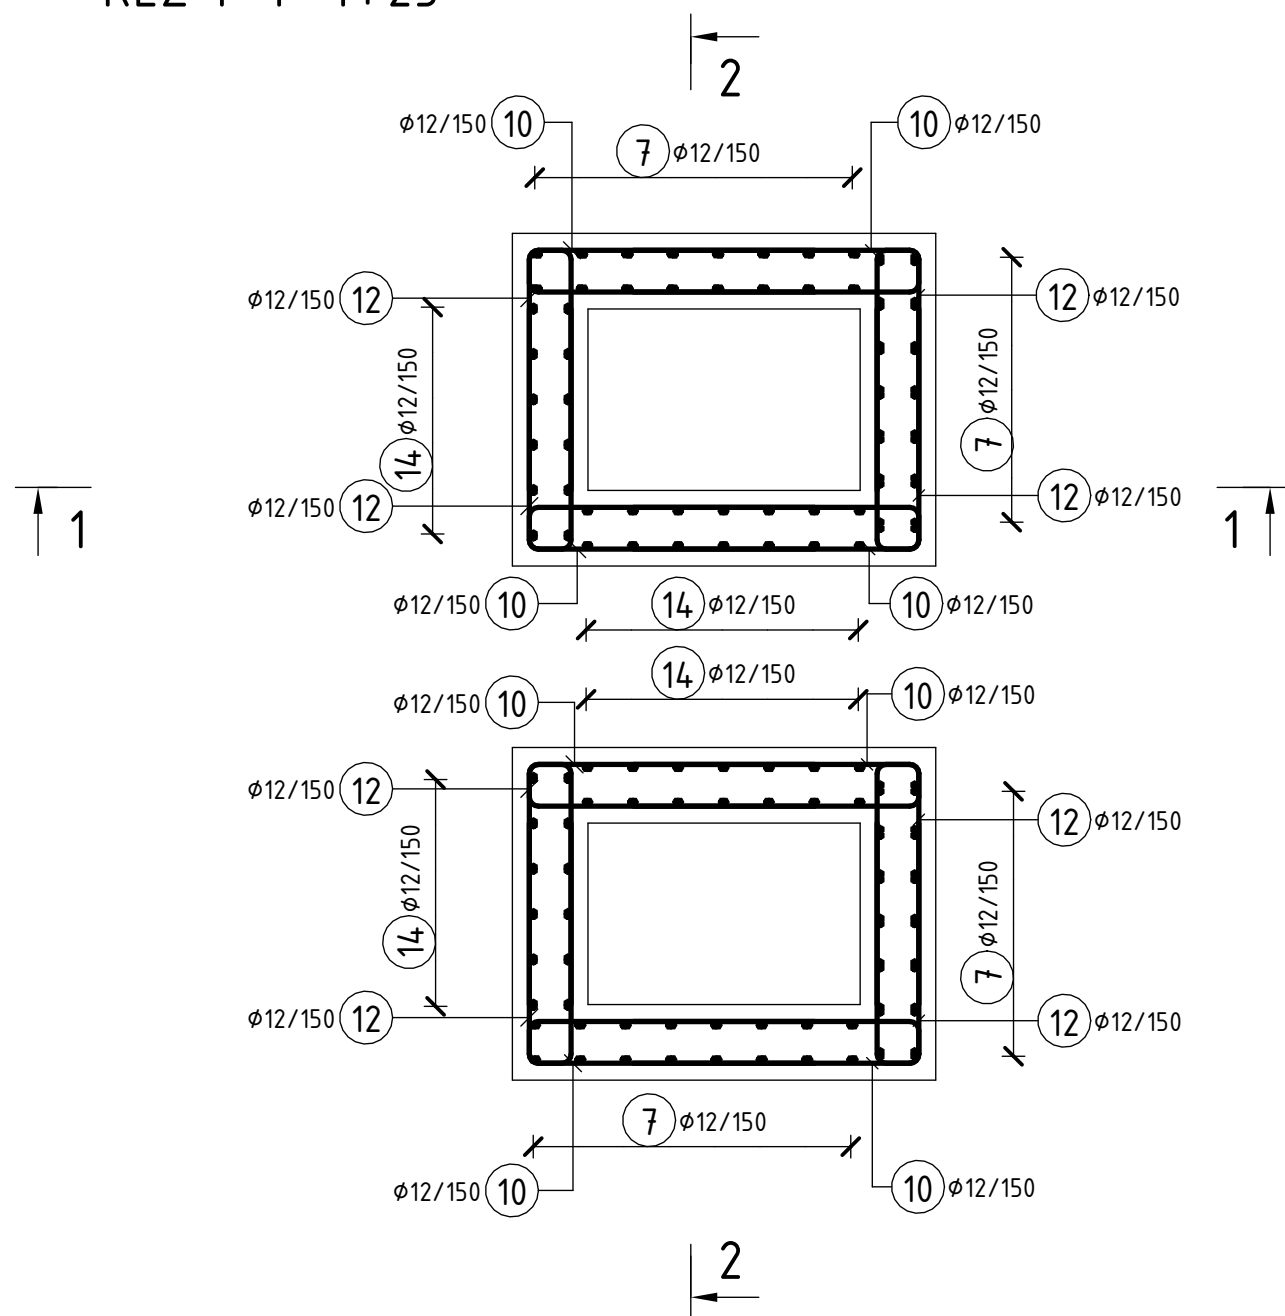

Souřadnicový systém: S-JTSK
Výškový systém: Bpv

SO 344 Přeložka vodovodu v MÚK Martinovice

Objednatel: Ředitelství silnic a dálnic s. p.
Čerčanská 2023/12, Krč, 140 00 Praha 4

Zhotovitel: Valbek, spol. s r.o.
Vaňurova 505/17
460 07 Liberec 3

Vypracoval: ING. ROMAN NAZARCHUK
Zodp. projektant: ING. JIŘÍ VANCL
Tech. kontrola: ING. DAVID LANDA
Akce: I/16 MLADÁ BOLESLAV - MARTINOVICE
Zhotovitel: Valbek, spol. s r.o.
Vaňurova 505/17
460 07 Liberec 3
Příloha: ARMATURNÍ ŠACHTA AŠ2 - VÝKRES VÝZTUŽE
Zak. číslo: 21-LI13-001
Datum: 02/2025
Stupeň: PDPS
Počet formátů: 8x A4
Měřítko: 1:25
Č. přílohy: Paré
6.6