

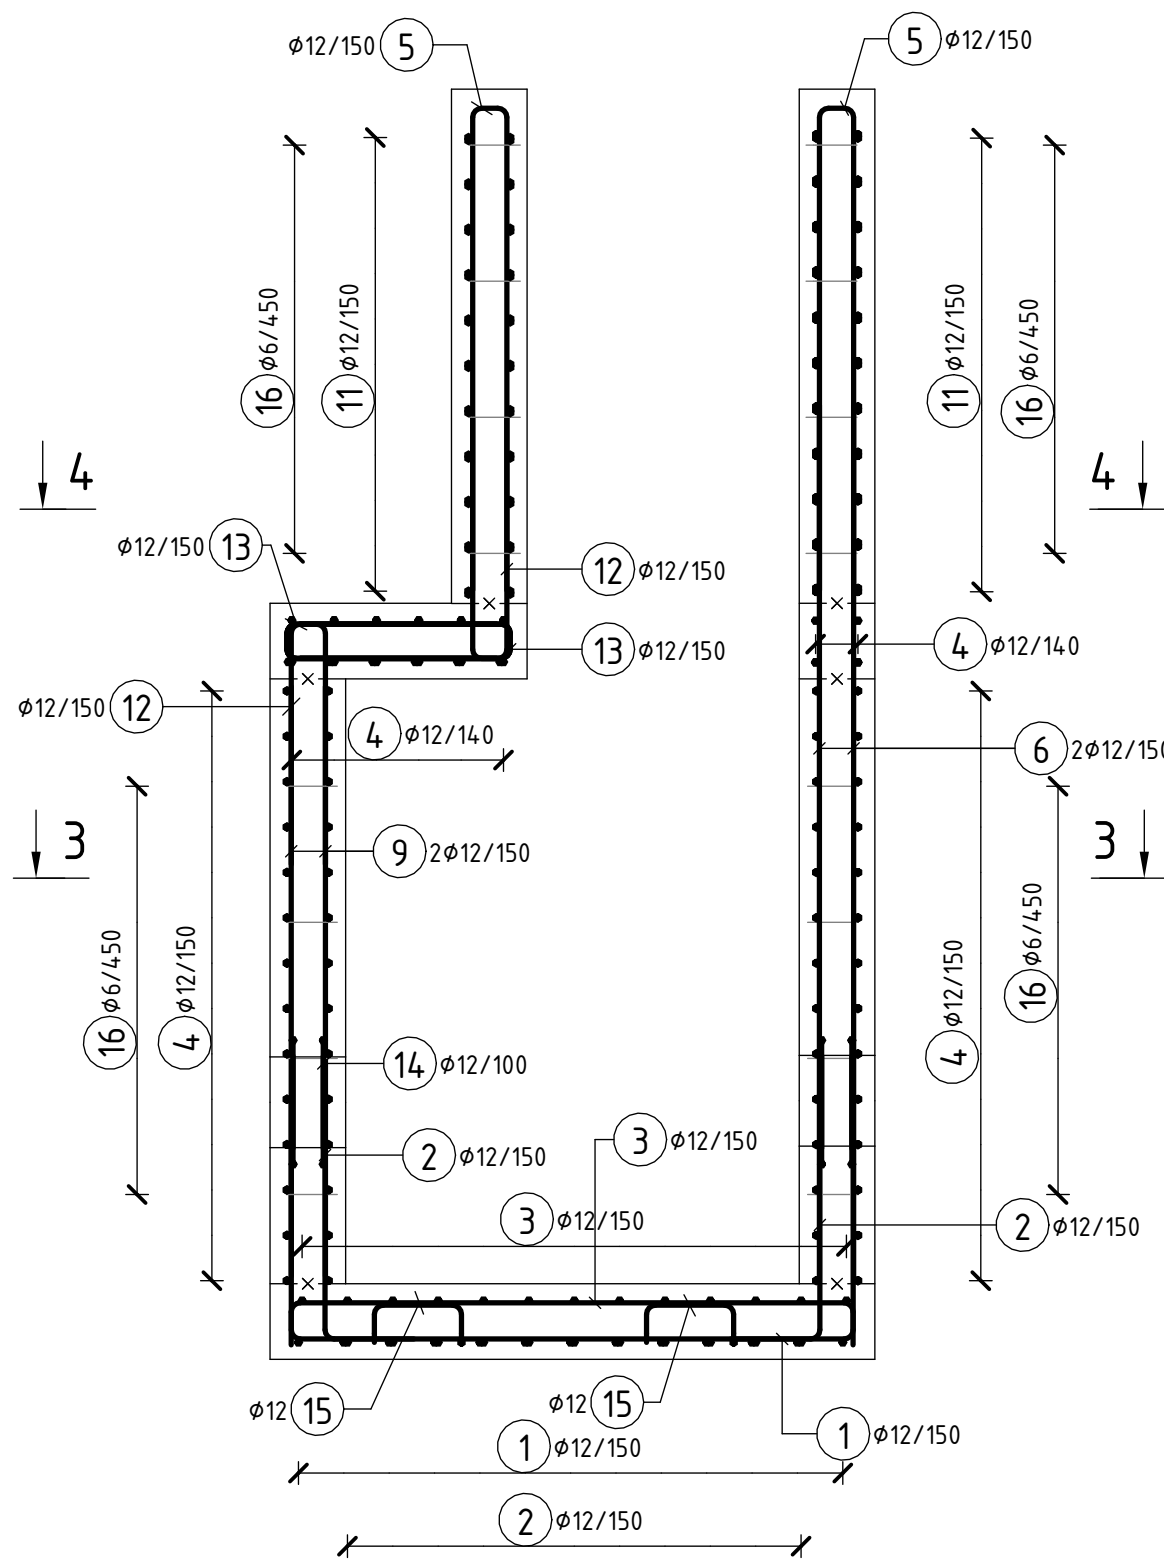


ŘEZ 1-1 1: 25

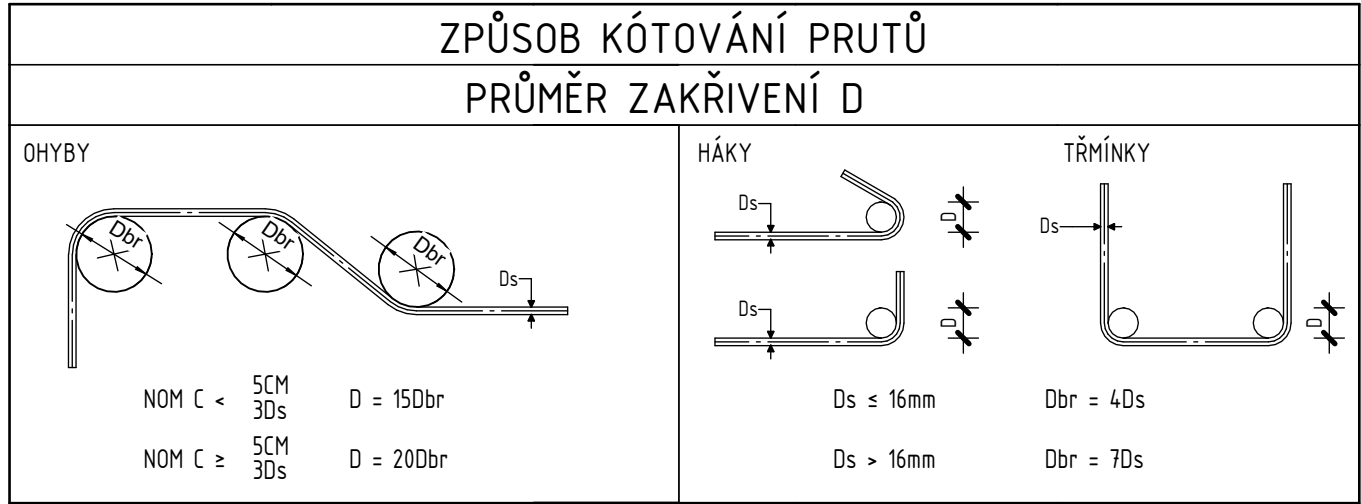

ŘEZ 2-2 1: 25

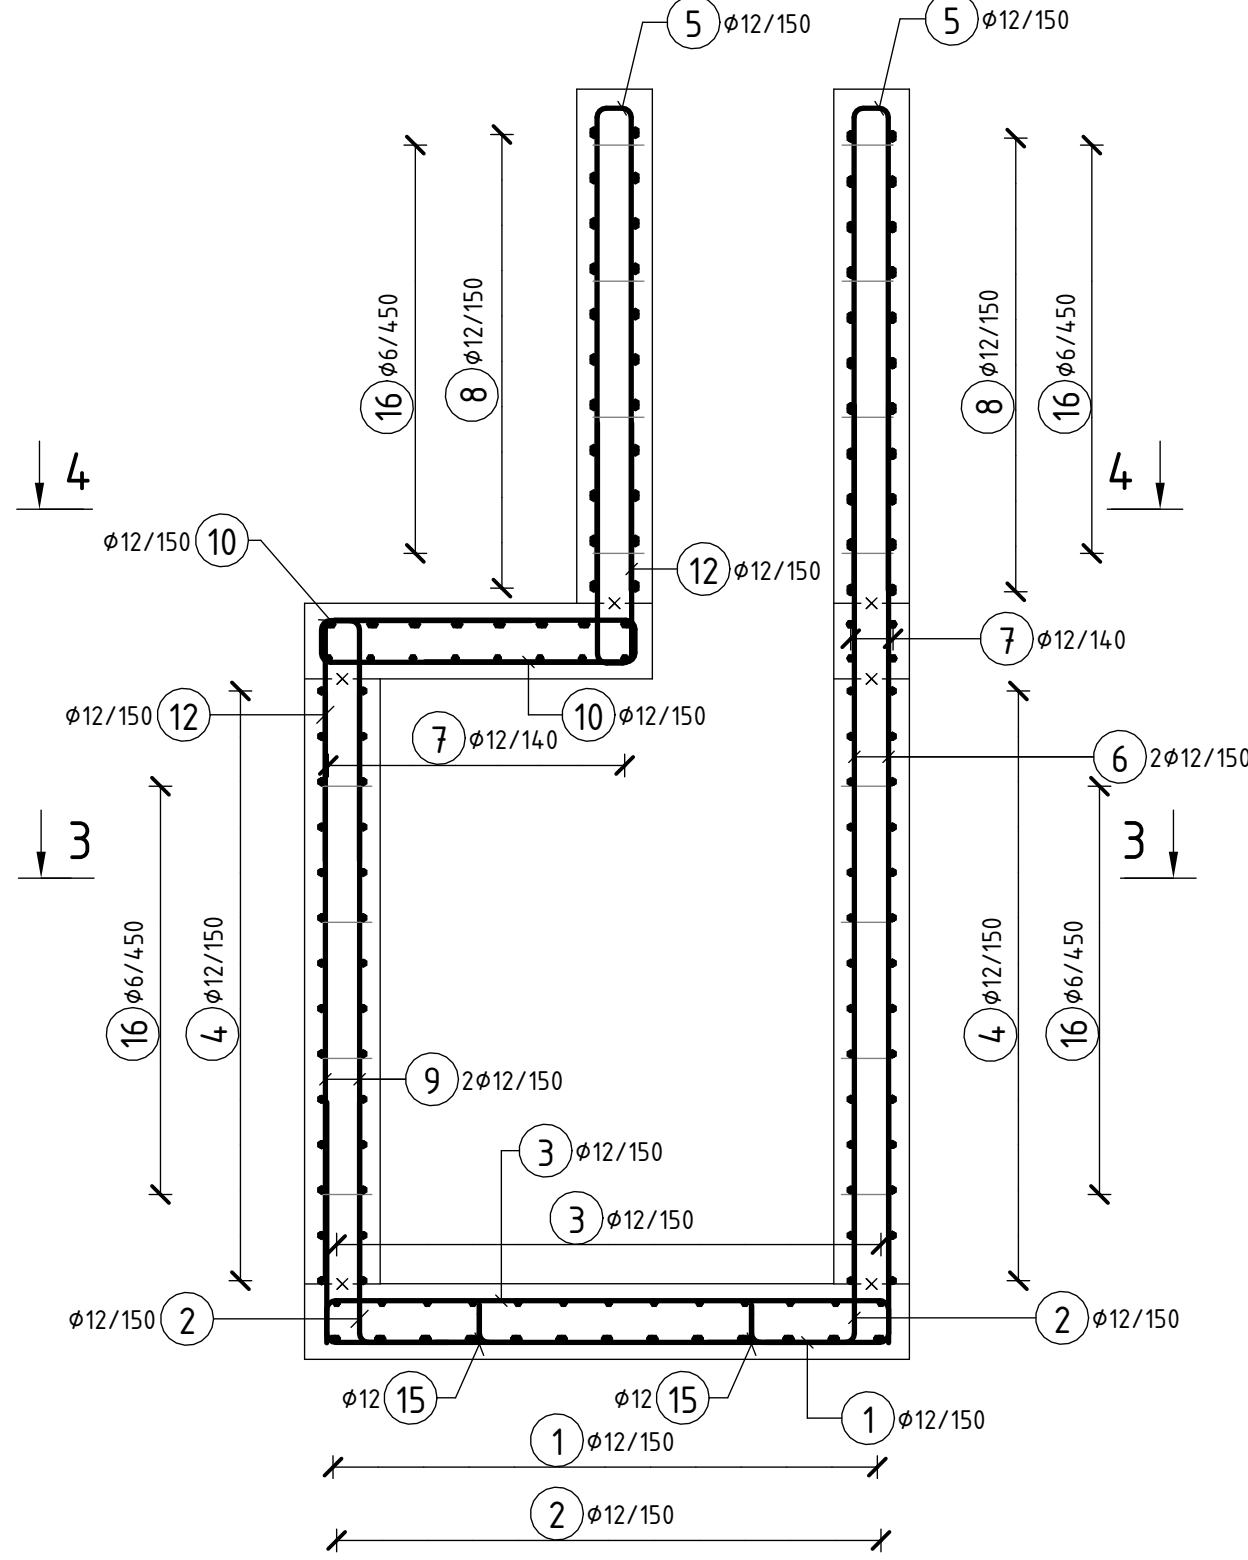

POZNÁMKY:

- V MÍSTĚ POTRUBÍ BUDE VÝZTUŽ OŘÍZNUTA.

BETON

JÍMKÁ

ČSN EN 206+A2

C30/37-XF3

KRYTÍ

VŠECHNY PLOCHY

MINIMÁLNÍ / JMENOVITÉ

45mm / 50 mm

OCEL

BETONÁŘSKÁ

ČSN EN 10027-1


B 500B

ROZMĚRY VÝZTUŽE JSOU KÓTOVÁNY NA VNĚJŠÍ HRANY


VÝKAZ VÝZTUŽE

| ČÍSLO<br>POL.            | Ø<br>[mm] | DĚLKA<br>[mm] | POČET<br>[ks] | DĚLKY PODLE Ø [m] |         |
|--------------------------|-----------|---------------|---------------|-------------------|---------|
|                          |           |               |               | d6                | d12     |
| 1                        | 12        | 3470          | 26            | 0                 | 90.22   |
| 2                        | 12        | 1100          | 48            | 0                 | 52.8    |
| 3                        | 12        | 2160          | 26            | 0                 | 56.16   |
| 4                        | 12        | 2650          | 128           | 0                 | 339.2   |
| 5                        | 12        | 3325          | 28            | 0                 | 93.11   |
| 6                        | 12        | 2900          | 30            | 0                 | 87      |
| 7                        | 12        | 2625          | 20            | 0                 | 52.5    |
| 8                        | 12        | 2050          | 44            | 0                 | 90.2    |
| 9                        | 12        | 1950          | 66            | 0                 | 128.7   |
| 10                       | 12        | 1850          | 12            | 0                 | 22.2    |
| 11                       | 12        | 1750          | 44            | 0                 | 77      |
| 12                       | 12        | 1725          | 46            | 0                 | 79.37   |
| 13                       | 12        | 1525          | 8             | 0                 | 12.2    |
| 14                       | 12        | 1000          | 20            | 0                 | 20      |
| 15                       | 12        | 870           | 4             | 0                 | 3.48    |
| 16                       | 6         | 305           | 72            | 21.96             | 0       |
| DĚLKA PODLE Ø CELKEM     |           |               | [m]           | 21.96             | 1204.14 |
| JEDNOTKOVÁ HMOTNOST      |           |               | [kg/m']       | 0.222             | 0.888   |
| HMOTNOST PODLE Ø CELKEM  |           |               | [kg]          | 4.86              | 1069.26 |
| CELKOVÁ HMOTNOST VÝZTUŽE |           |               | [kg]          | 1074.12           |         |


ŘEZ 3-3 1: 25

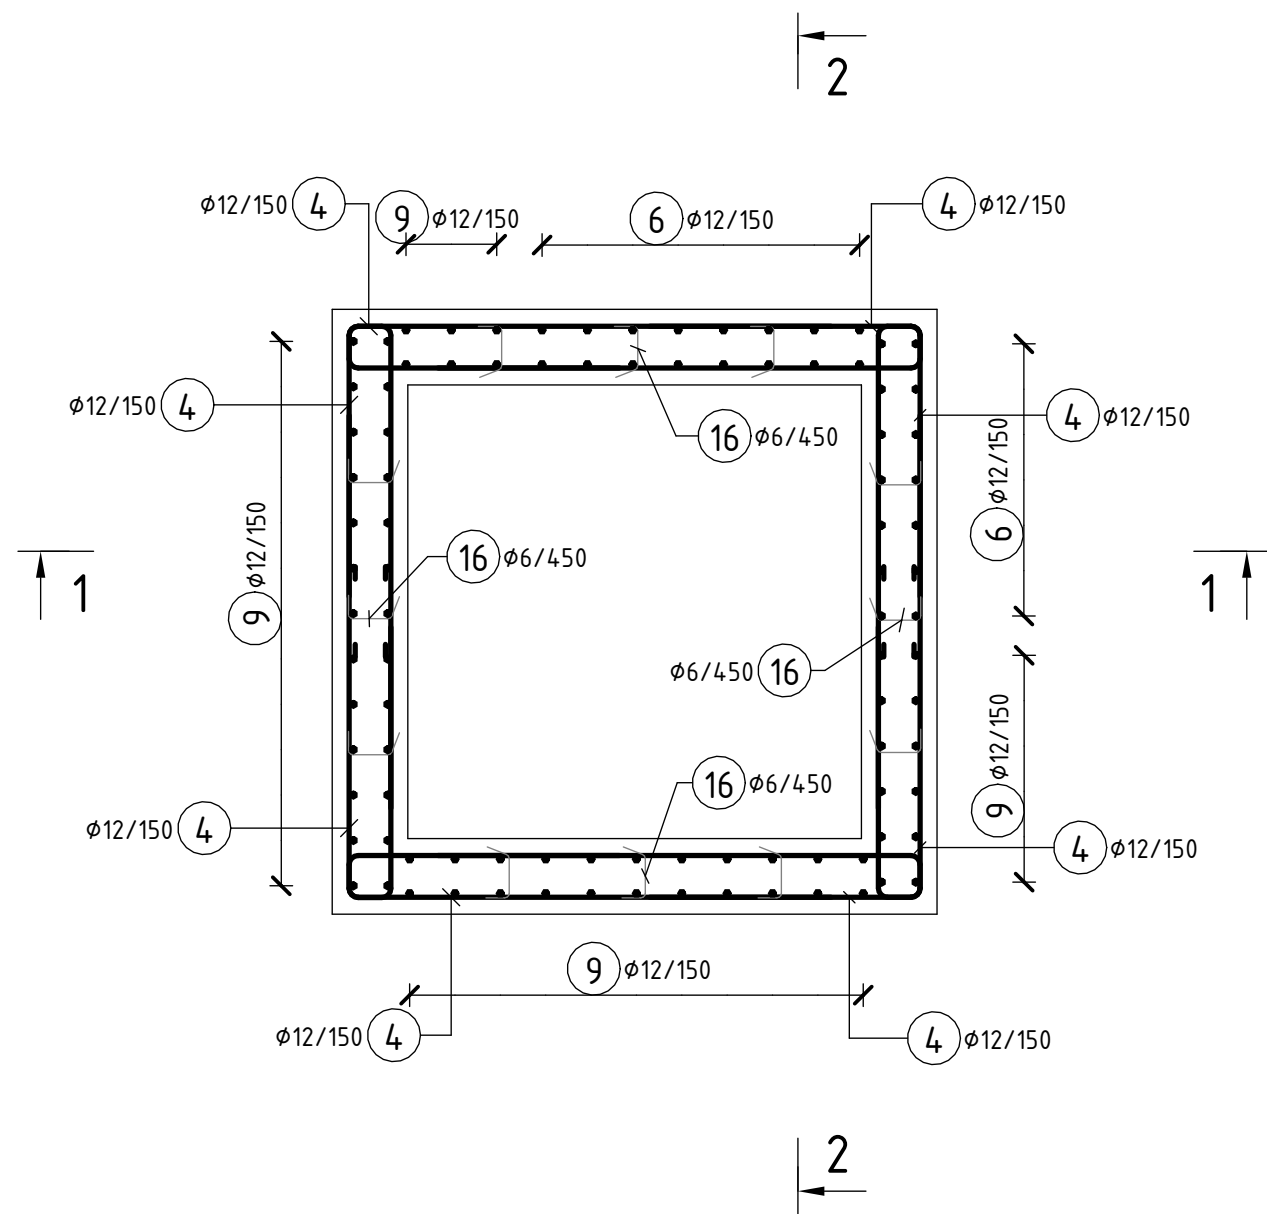

ŘEZ 4-4 1: 25

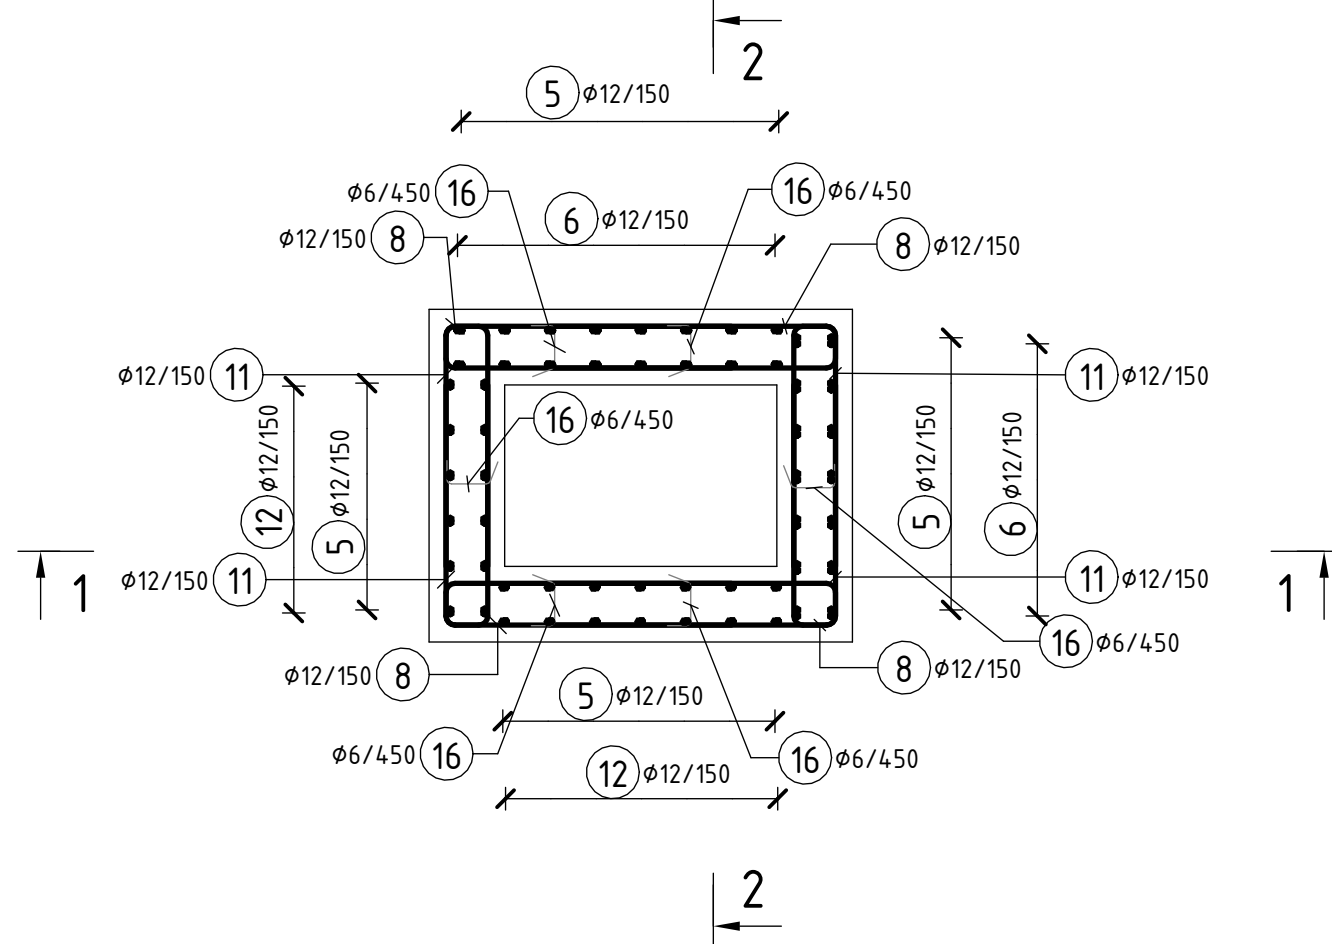

DETAIL 1 1: 25

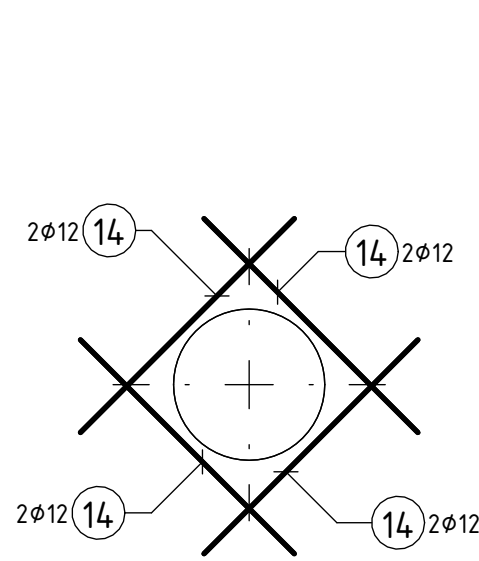

Souřadnicový systém: S-JTSK  
Výškový systém: Bpv

SO 344 Přeložka vodovodu v MÚK Martinovice

Objednatel:  
**ŘEDITELSTVÍ SILNIC A DÁLNIC**  
**Ředitelství silnic a dálnic s. p.**  
Čerčanská 2023/12, Krč, 140 00 Praha 4

Zhotovitel:  
**Valbek, spol. s r.o.**  
Vaňurova 505/17  
460 07 Liberec 3

|                                                                            |                                   |                                                  |               |             |
|----------------------------------------------------------------------------|-----------------------------------|--------------------------------------------------|---------------|-------------|
|                                                                            | Vypracoval                        | ING. ROMAN NAZARCHUK                             | Zak. číslo    | 21-LI13-001 |
|                                                                            | Zodp. projektant                  | ING. JIŘÍ VANCL                                  | Datum         | 02/2025     |
|                                                                            | Tech. kontrola                    | ING. DAVID LANDA                                 | Stupeň        | PDPS        |
|                                                                            | I/16 MLADÁ BOLESLAV - MARTINOVICE |                                                  | Počet formátů | 8x A4       |
|                                                                            |                                   |                                                  | Měřítko       | 1:25        |
| Zhotovitel:<br>Valbek, spol. s r.o.<br>Vaňurova 505/17<br>460 07 Liberec 3 |                                   | Příloha<br>ARMATURNÍ ŠACHTA AŠ3 - VÝKRES VÝZTUŽE |               | 6.7         |