


SO 360.1 DISPOZIČNÍ VÝKRES OLK M 1:100

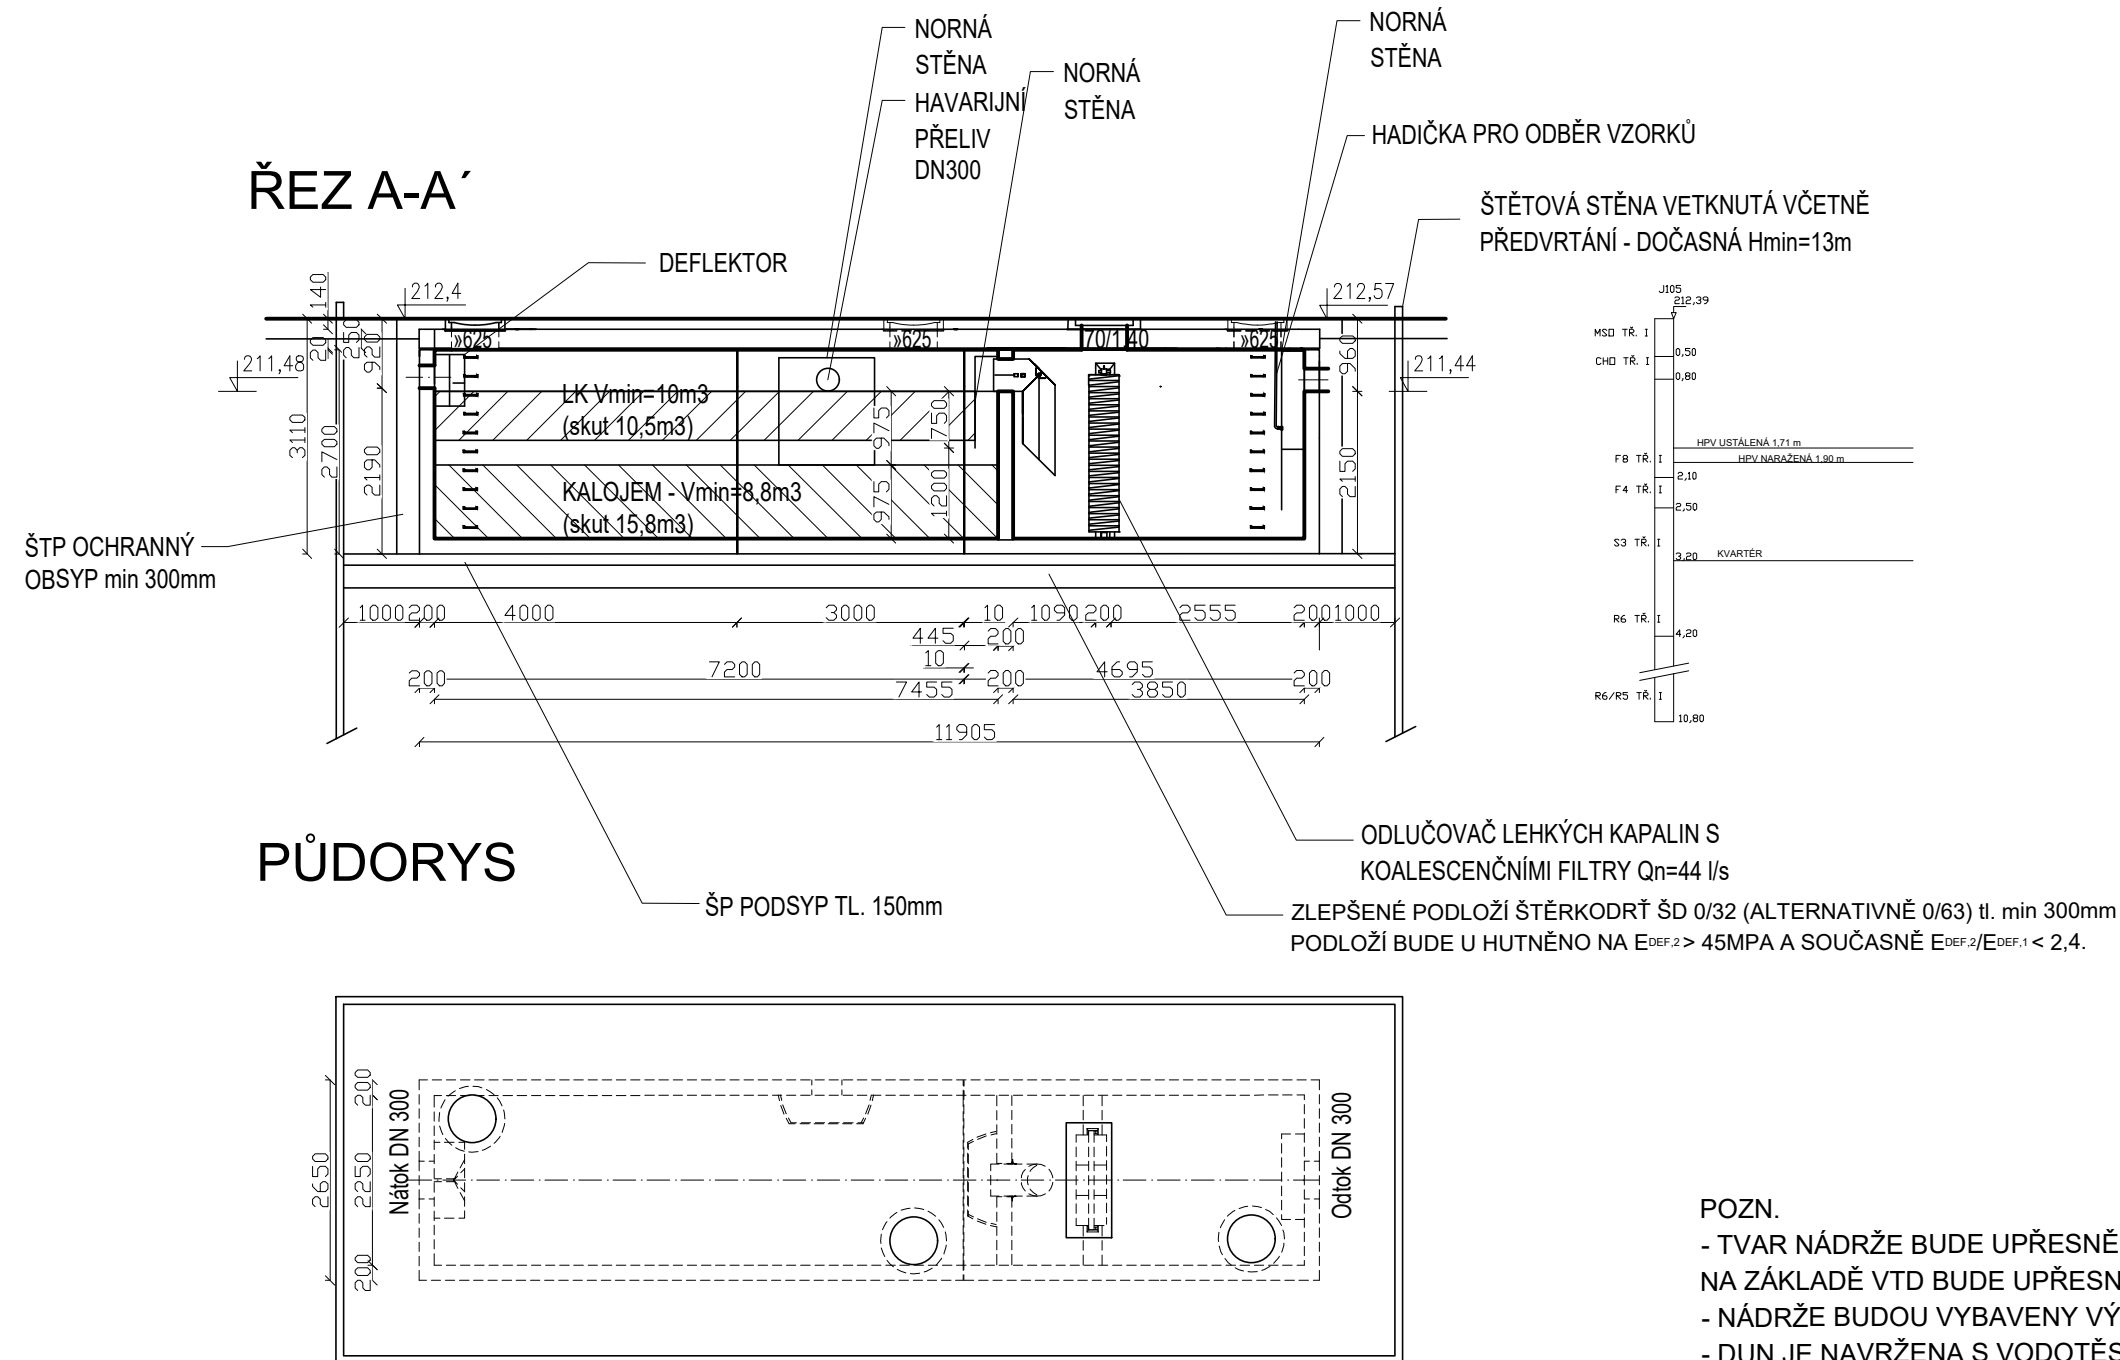

POZN.

- TVAR NÁDRŽE BUDE UPŘESNĚN V DALŠÍM STUPNI PD DLE KONKRÉTNÍHO DODAVATELE NA ZÁKLADĚ VTD BUDE UPŘESNĚN ZPŮSOB ZALOŽENÍ POMOCÍ ŠTĚTOVNIC
- NÁDRŽE BUDOU VYBAVENY VÝSTUPY PRO OBOŽIVELNÍKY
- DUN JE NAVRŽENA S VODOTĚSNÝMI SYSTÉMEM SEŠROUBOVÁNÍM PŘES TĚSNĚNÍ, ŠACHTOVÉ NÁSTAVBY POUŽÍVAJÍ STANDARDNÍ JAZÝČKOVÉ TĚSNĚNÍ. NA STROPNÍ DESCE NÁDRŽE BUDOU ZABETONOVÁNY PROFILY SPOJE PRO TOTO TĚSNĚNÍ.
- DO KAŽDÉ ČÁSTI DUN MUSÍ BÝT UMOŽNĚN VSTUP PŘES VSTUPNÍ KOMÍN (STUPADLA / ŽEBŘÍK)
- VE DNĚ BUDE ZŘÍZENÁ ČERPACÍ JÍMKA PRO ČERPÁNÍ PŘÍPADNÉ PRŮSAKOVÉ VODY
- VNĚJŠÍ POVRCH STROPU OPATŘEN PENETRAČNÍM ASFALTOVÝM NÁTĚREM, SPOJE STROPNÍCH DÍLŮ NÁSLEDNĚ PŘEKRYT NATAVITELNÝMI ASFALTOVÝMI PÁSY

Souřadnicový systém: S-JTSK
Výškový systém: Bpv

SO 360.1 DUN a retenční nádrže na I/16

Objednatel:



ŘEDITELSTVÍ SILNIC A DÁLNIC


Ředitelství silnic a dálnic s. p.

Čerčanská 2023/12, Krč, 140 00 Praha 4

Zhotovitel:

**Valbek, spol. s r.o.**

Vaňurova 505/17
460 07 Liberec 3

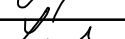	Vypracoval	ING. J. VANCL		Zak. číslo	21-LI13-001
	Zodp. projektant	ING. J. VANCL		Datum	02/2025
	Tech. kontrola	ING. D. LANDA		Stupeň	PDPS
	Akce			Počet formátů	3 x A4
I/16 MLADÁ BOLESLAV - MARTINOVICE				Měřítko	1 : 100
				Č. přílohy	Paré
				2	
Zhotovitel: Valbek, spol. s r.o. Vaňurova 505/17 460 07 Liberec 3	Příloha DISPOZIČNÍ VÝKRES OLK				