


PODÉLNÝ PROFIL HRÁZÍ RETENČNÍ NÁDRŽE

M 1 : 500

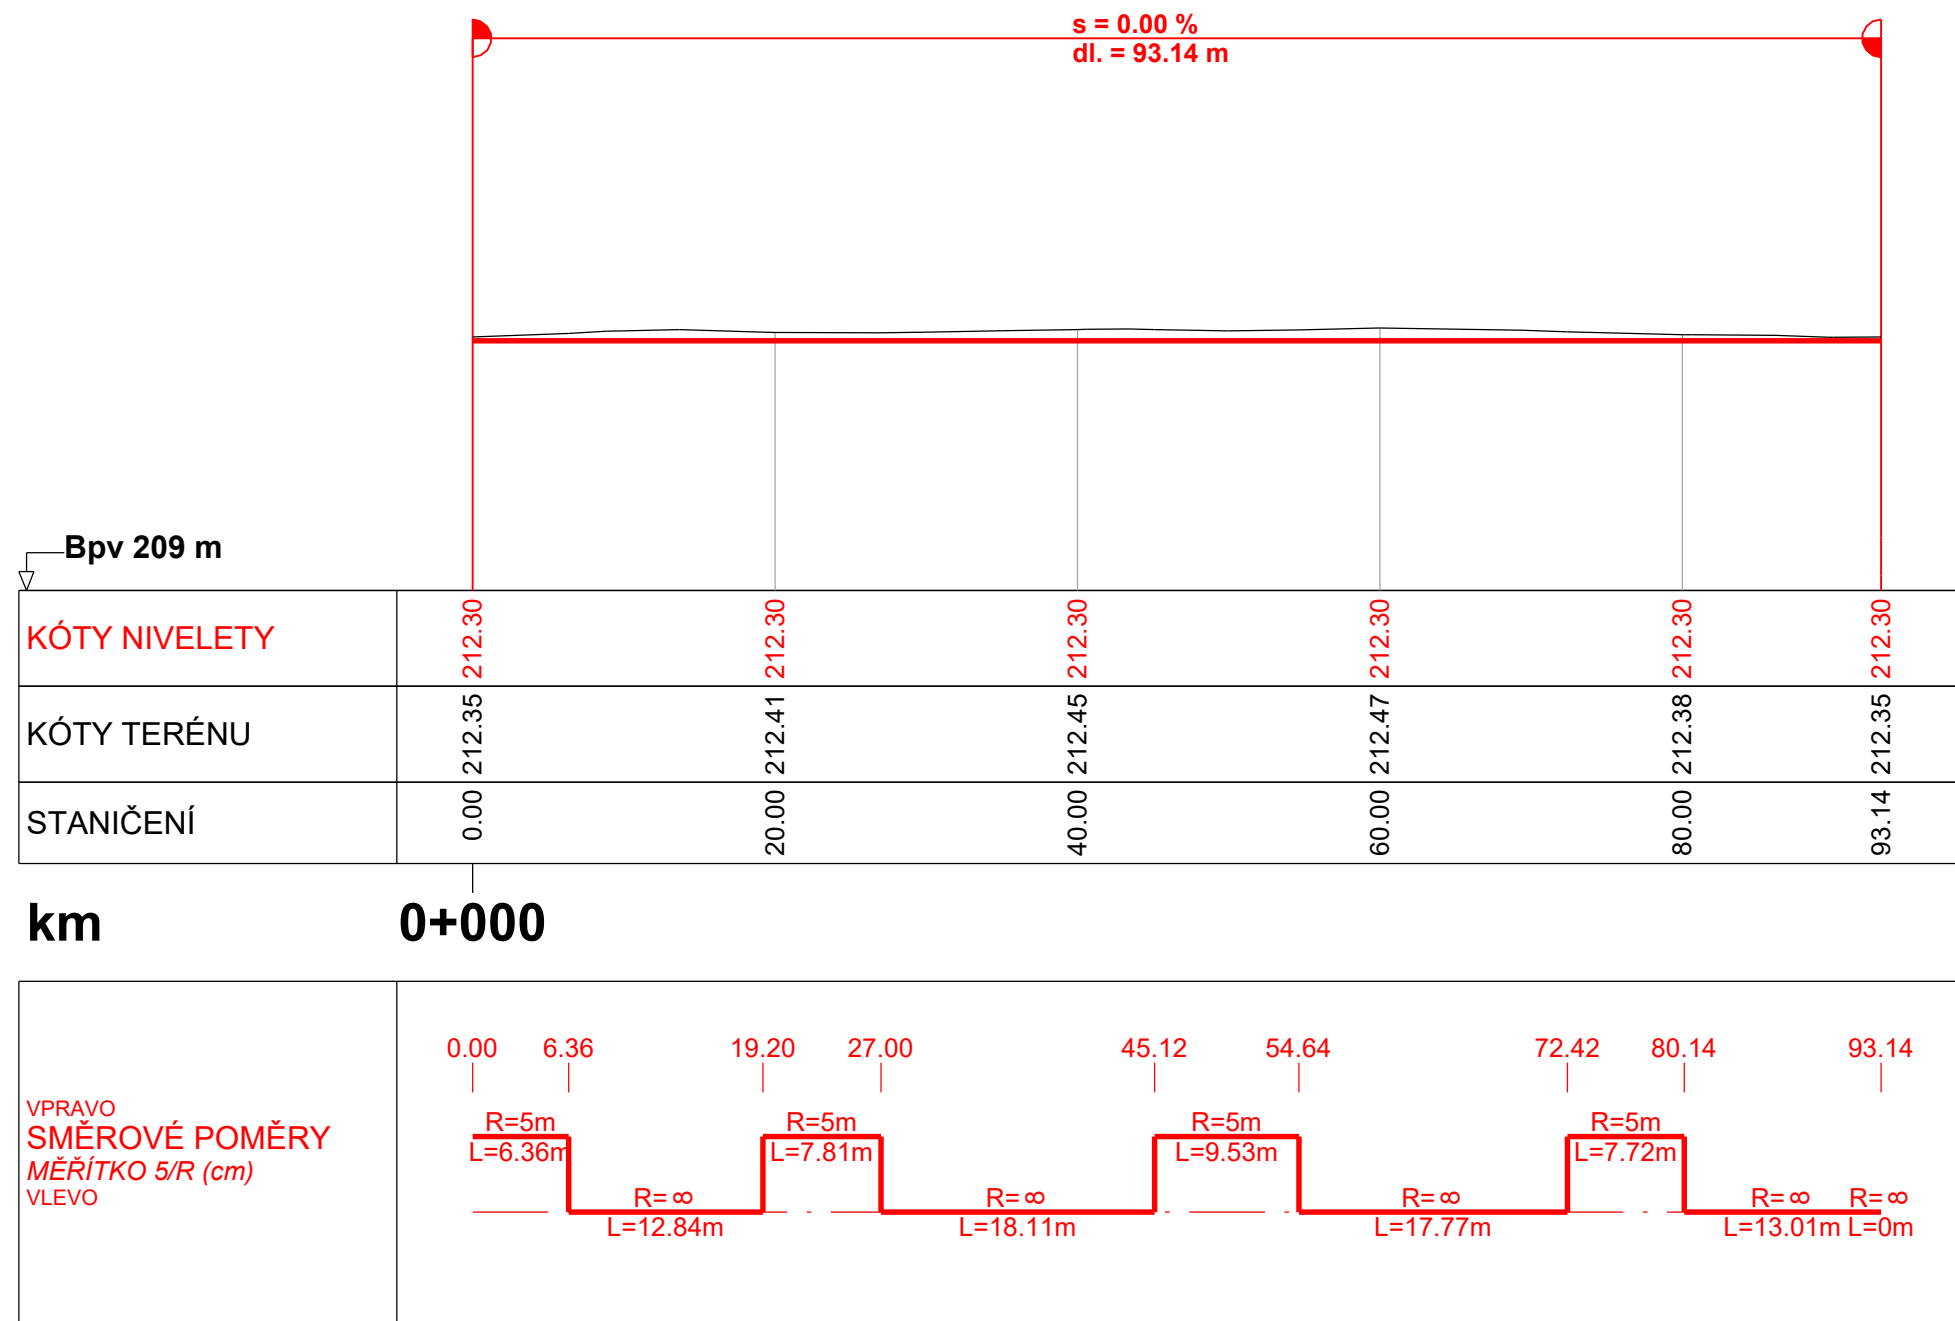

Souřadnicový systém: S-JTSK
Výškový systém: Bpv

SO 360.1 DUN a retenční nádrže na I/16

Objednatel:	 ŘEDITELSTVÍ SILNIC A DÁLNIC	Ředitelství silnic a dálnic s. p. Čerčanská 2023/12, Krč, 140 00 Praha 4
-------------	--	--

Zhotovitel: 	Valbek, spol. s r.o. Vaňurova 505/17 460 07 Liberec 3	
--	--	--

	Vypracoval ING. J. VANCL		Zak. číslo 21-LI13-001
	Zodp. projektant ING. J. VANCL		Datum 02/2025
	Tech. kontrola ING. D. LANDA		Stupeň PDPS
	Akce I/16 MLADÁ BOLESLAV - MARTINOVICE		Počet formátů 3 x A4
Zhotovitel: Valbek, spol. s r.o. Vaňurova 505/17 460 07 Liberec 3	Příloha PODÉLNÝ PROFIL HRÁZÍ RETENČNÍ NÁDRŽE	Měřítko 1 : 500/100	Č. přílohy Paré
		3	