


PODÉLNÝ ŘEZ RETENČNÍ NÁDRŽÍ  
M 1:100

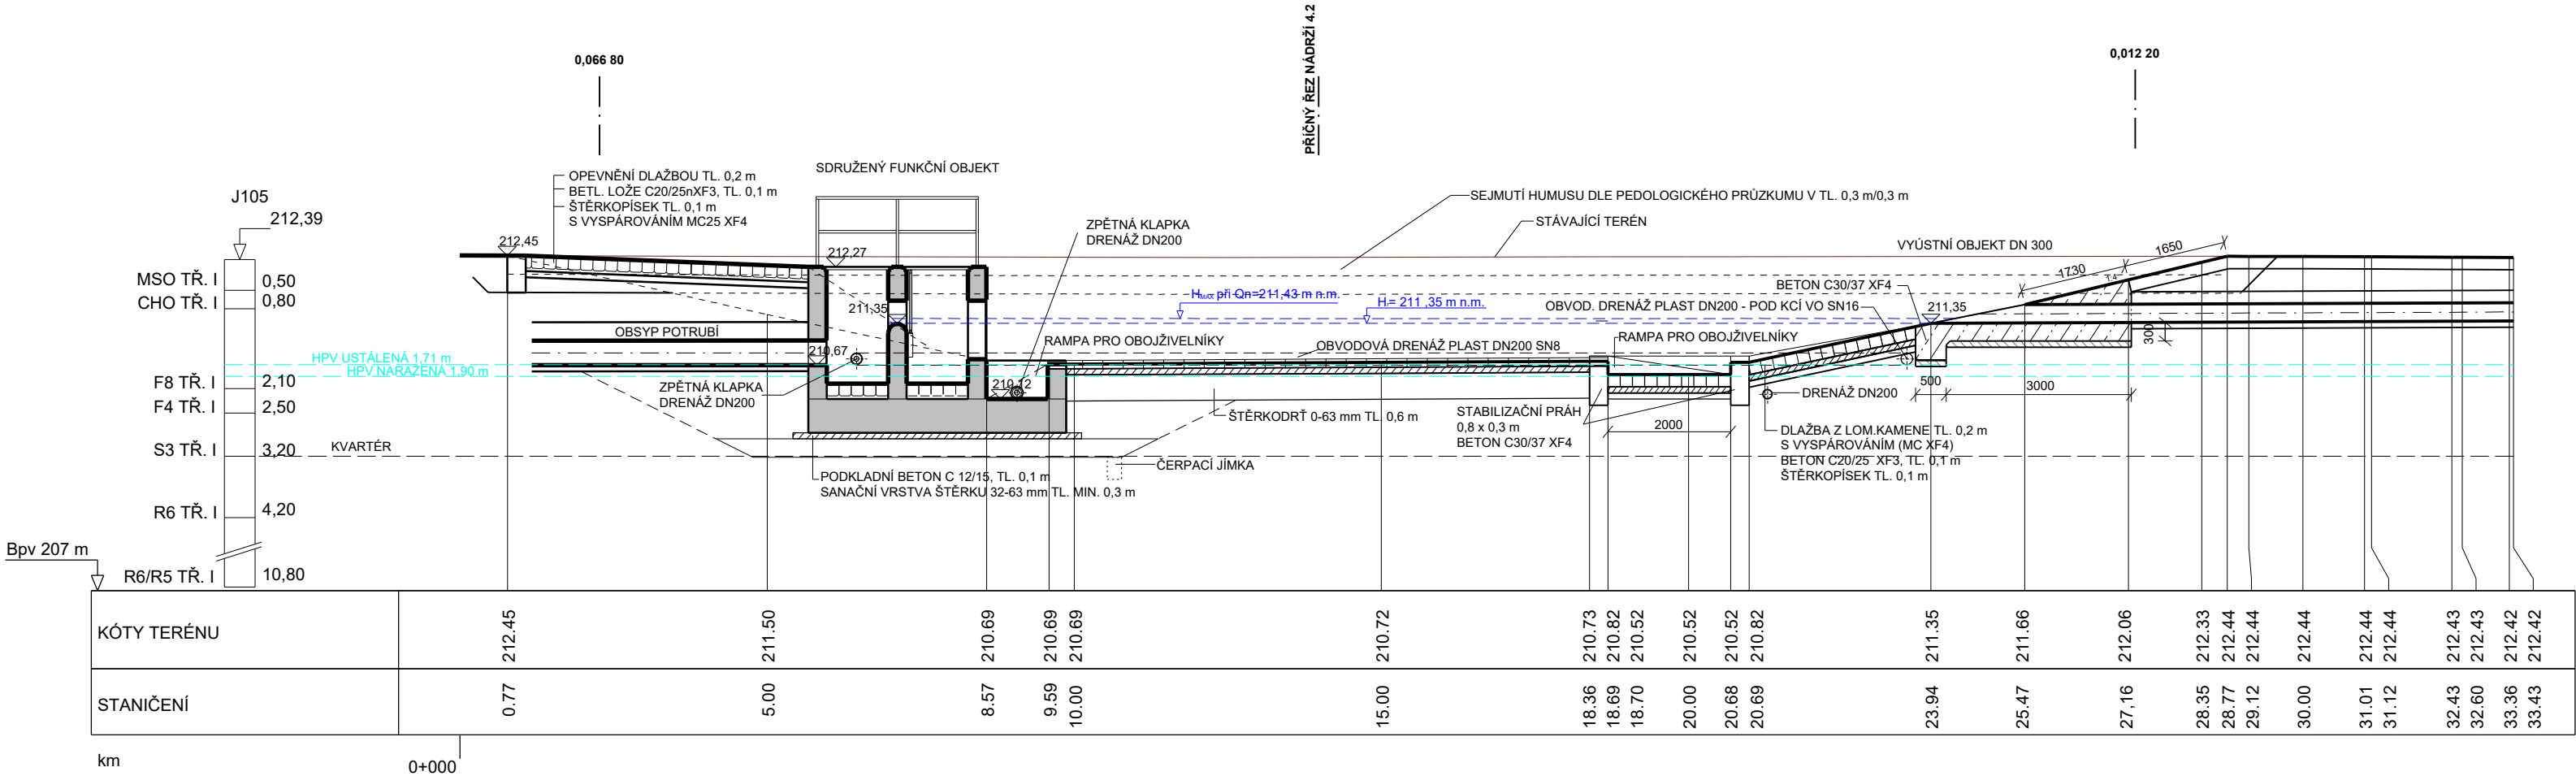

Souřadnicový systém: S-JTSK  
Výškový systém: Bpv

SO 360.1 DUN a retenční nádrže na I/16

Objednatel:



ŘEDITELSTVÍ  
SILNIC  
A DÁLNIC

Ředitelství silnic a dálnic s. p.  
Čerčanská 2023/12, Krč, 140 00 Praha 4

Zhotovitel:



Valbek, spol. s r.o.  
Vaňurova 505/17  
460 07 Liberec 3



Vypracoval  
Zodp. projektant  
Tech. kontrola

ING. V. JURÁNEK  
ING. J. VANCL  
ING. D. LANDA

Zak. číslo  
Datum  
Stupeň

21-LI13-001  
02/2025  
PDPS

Akce  
I/16 MLADÁ BOLESLAV - MARTINOVICE

Počet formátů  
Měřítko  
Č. přílohy

4 x A4  
1:100  
Paré

Zhotovitel:  
Valbek, spol. s r.o.  
Vaňurova 505/17  
460 07 Liberec 3

Příloha  
PODÉLNÝ ŘEZ RETENČNÍ NÁDRŽÍ

4.1