


PŘÍČNÝ ŘEZ RETENČNÍ NÁDRŽÍ  
M 1:100

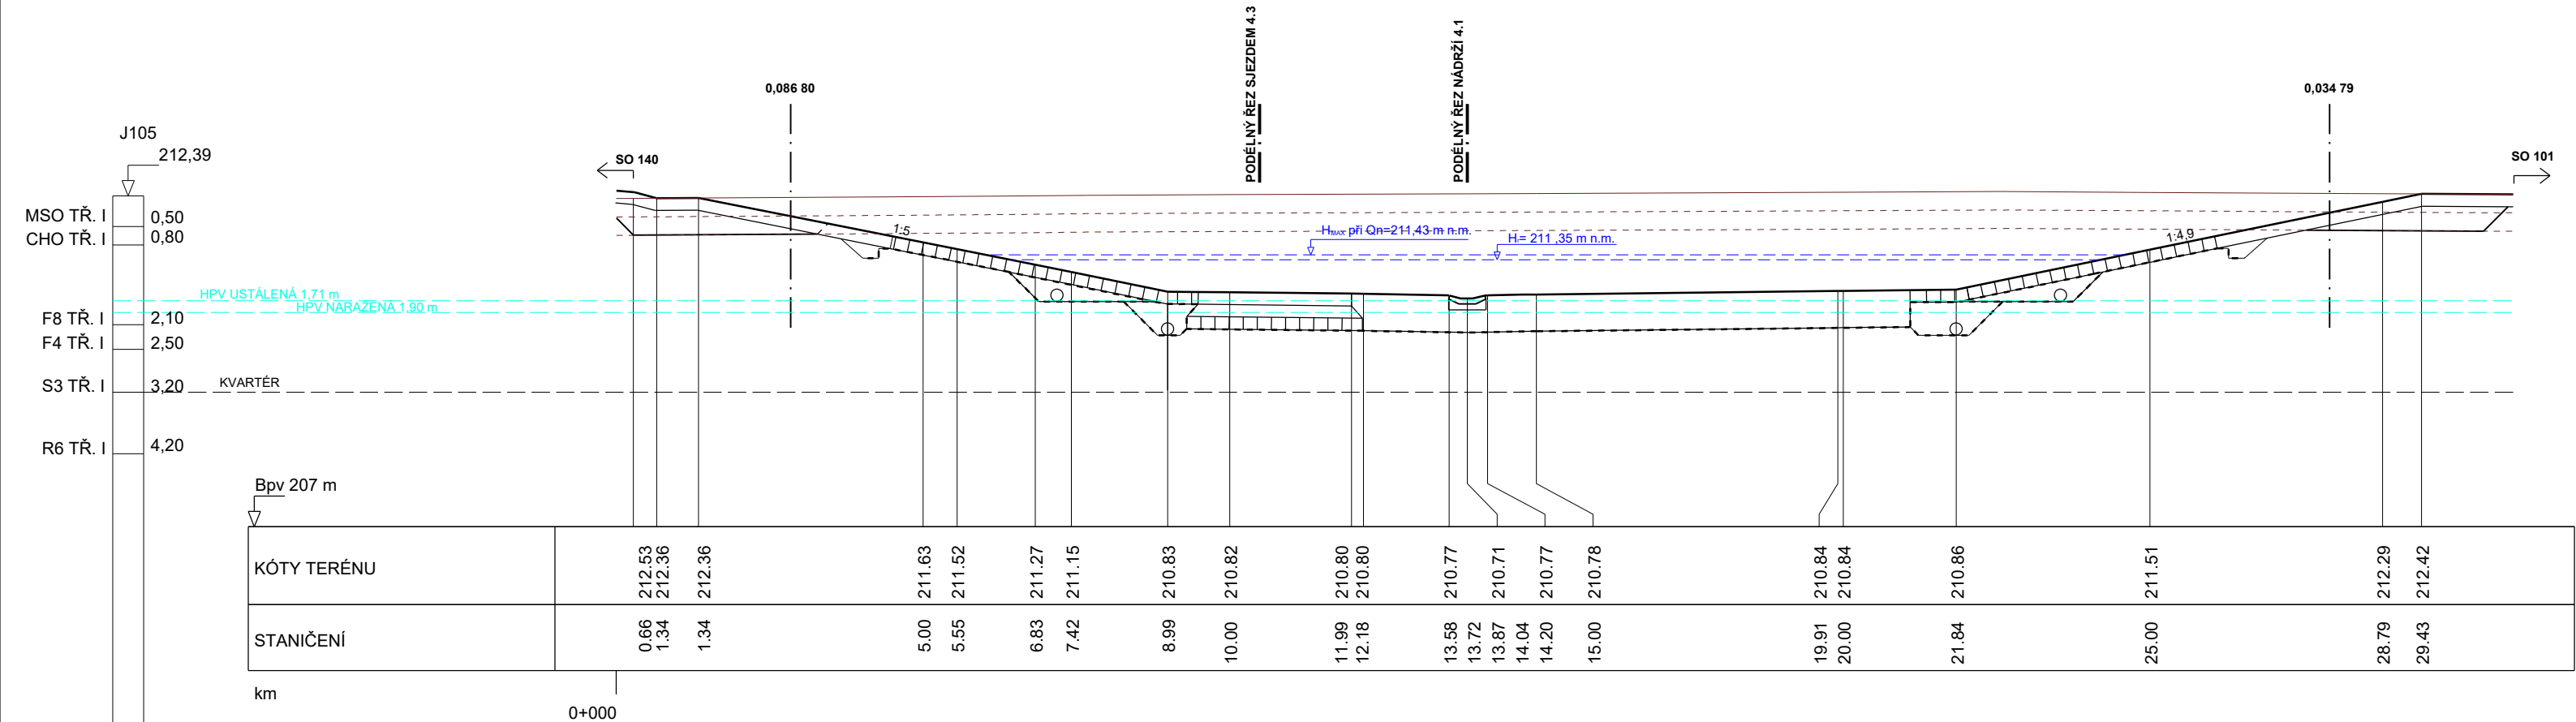

Souřadnicový systém: S-JTSK  
Výškový systém: Bpv

SO 360.1 DUN a retenční nádrže na I/16

Objednatel:



ŘEDITELSTVÍ  
SILNIC  
A DÁLNIC

Ředitelství silnic a dálnic s. p.  
Čerčanská 2023/12, Krč, 140 00 Praha 4

Zhotovitel:



Valbek, spol. s r.o.  
Vaňurova 505/17  
460 07 Liberec 3



Ing. V. JURÁNEK  
Ing. J. VANCL  
Ing. D. LANDA

Zak. číslo  
Datum  
Stupeň  
Počet formátů  
Měřítko  
Č. přílohy

I/16 MLADÁ BOLESLAV - MARTINOVICE

Zhotovitel:  
Valbek, spol. s r.o.  
Vaňurova 505/17  
460 07 Liberec 3

Příloha  
PŘÍČNÝ ŘEZ RETENČNÍ NÁDRŽÍ

4.2