




SO 360.1 - SFO
M 1:50

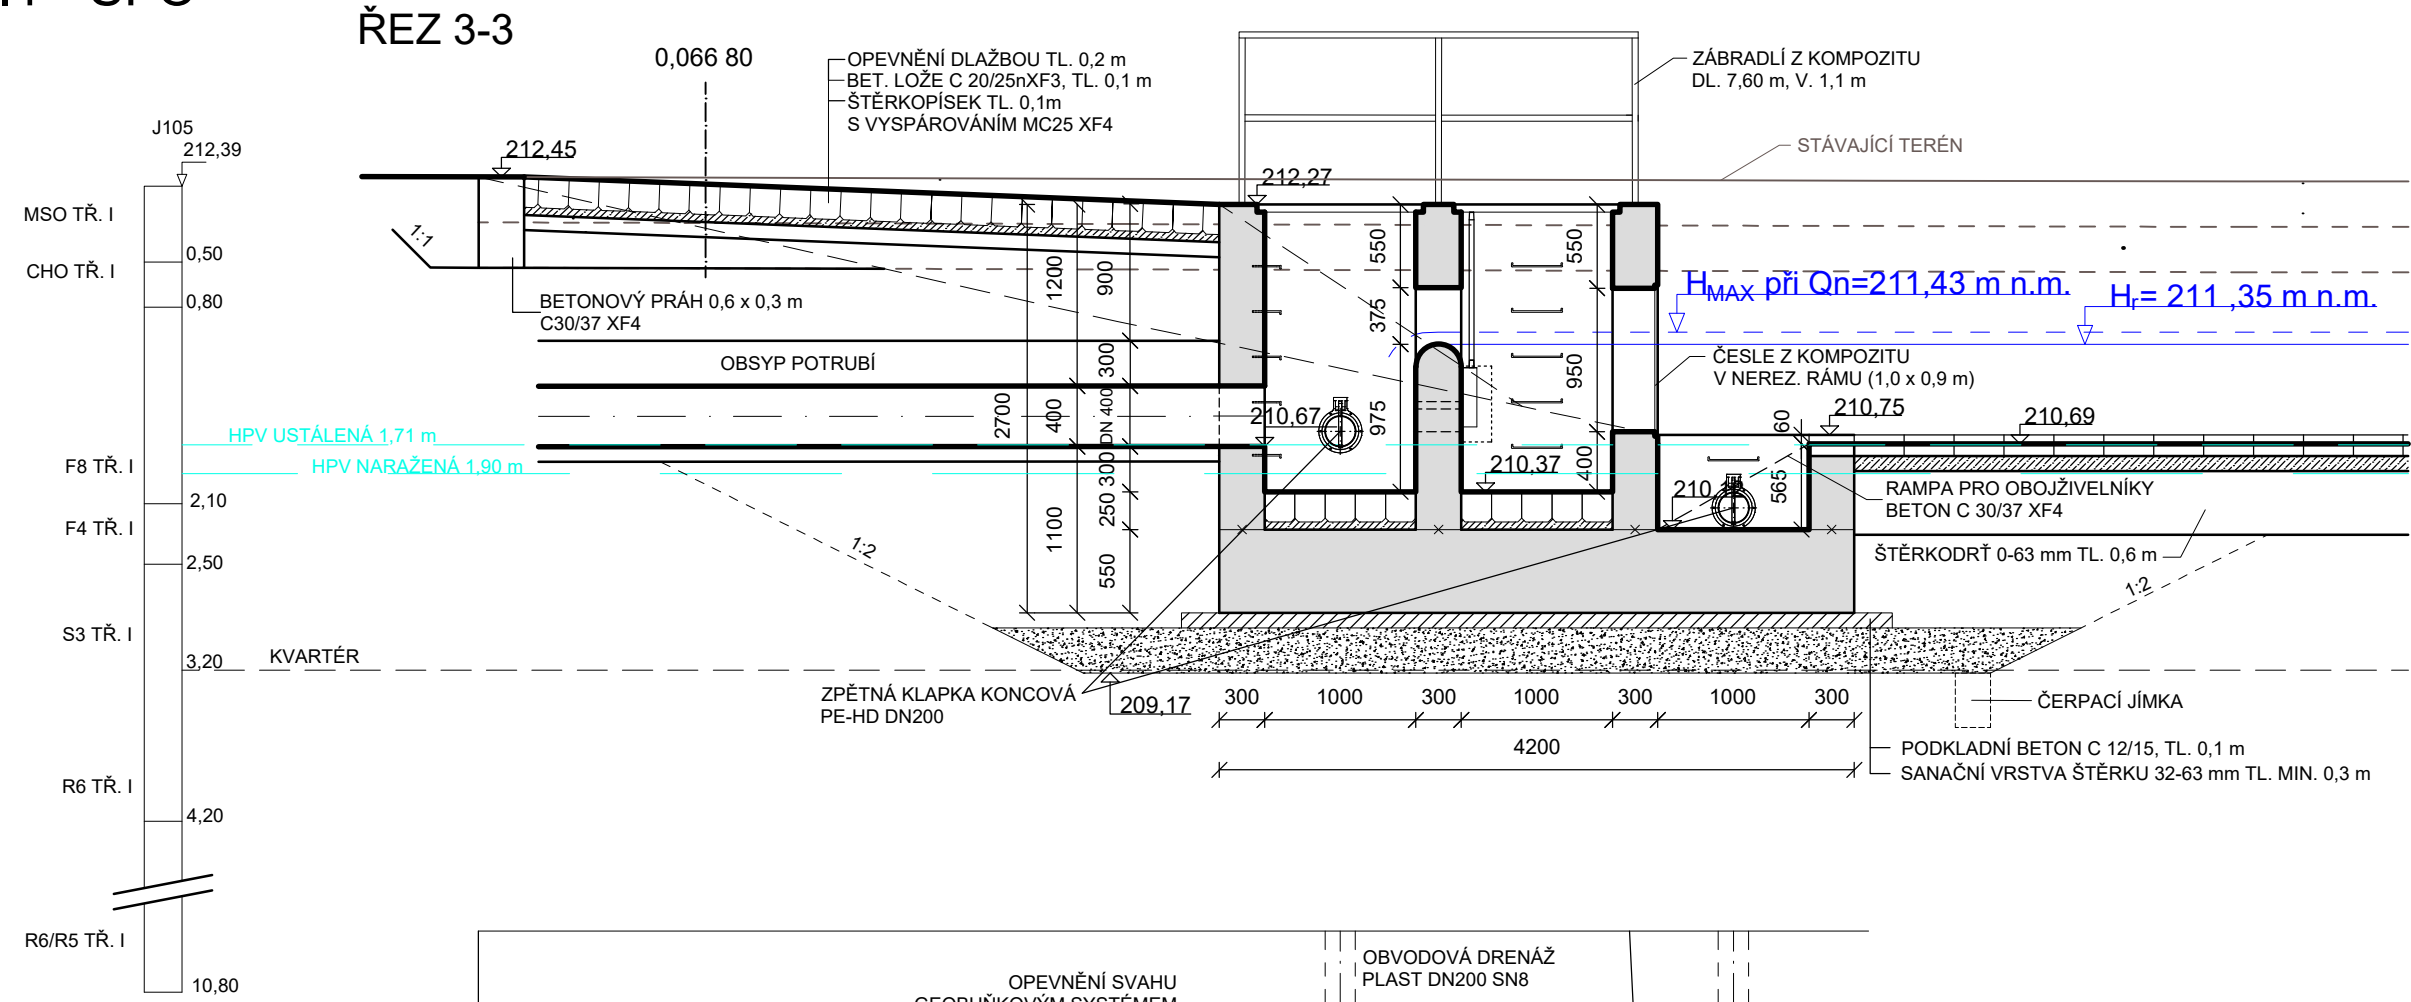


PŮDORYS

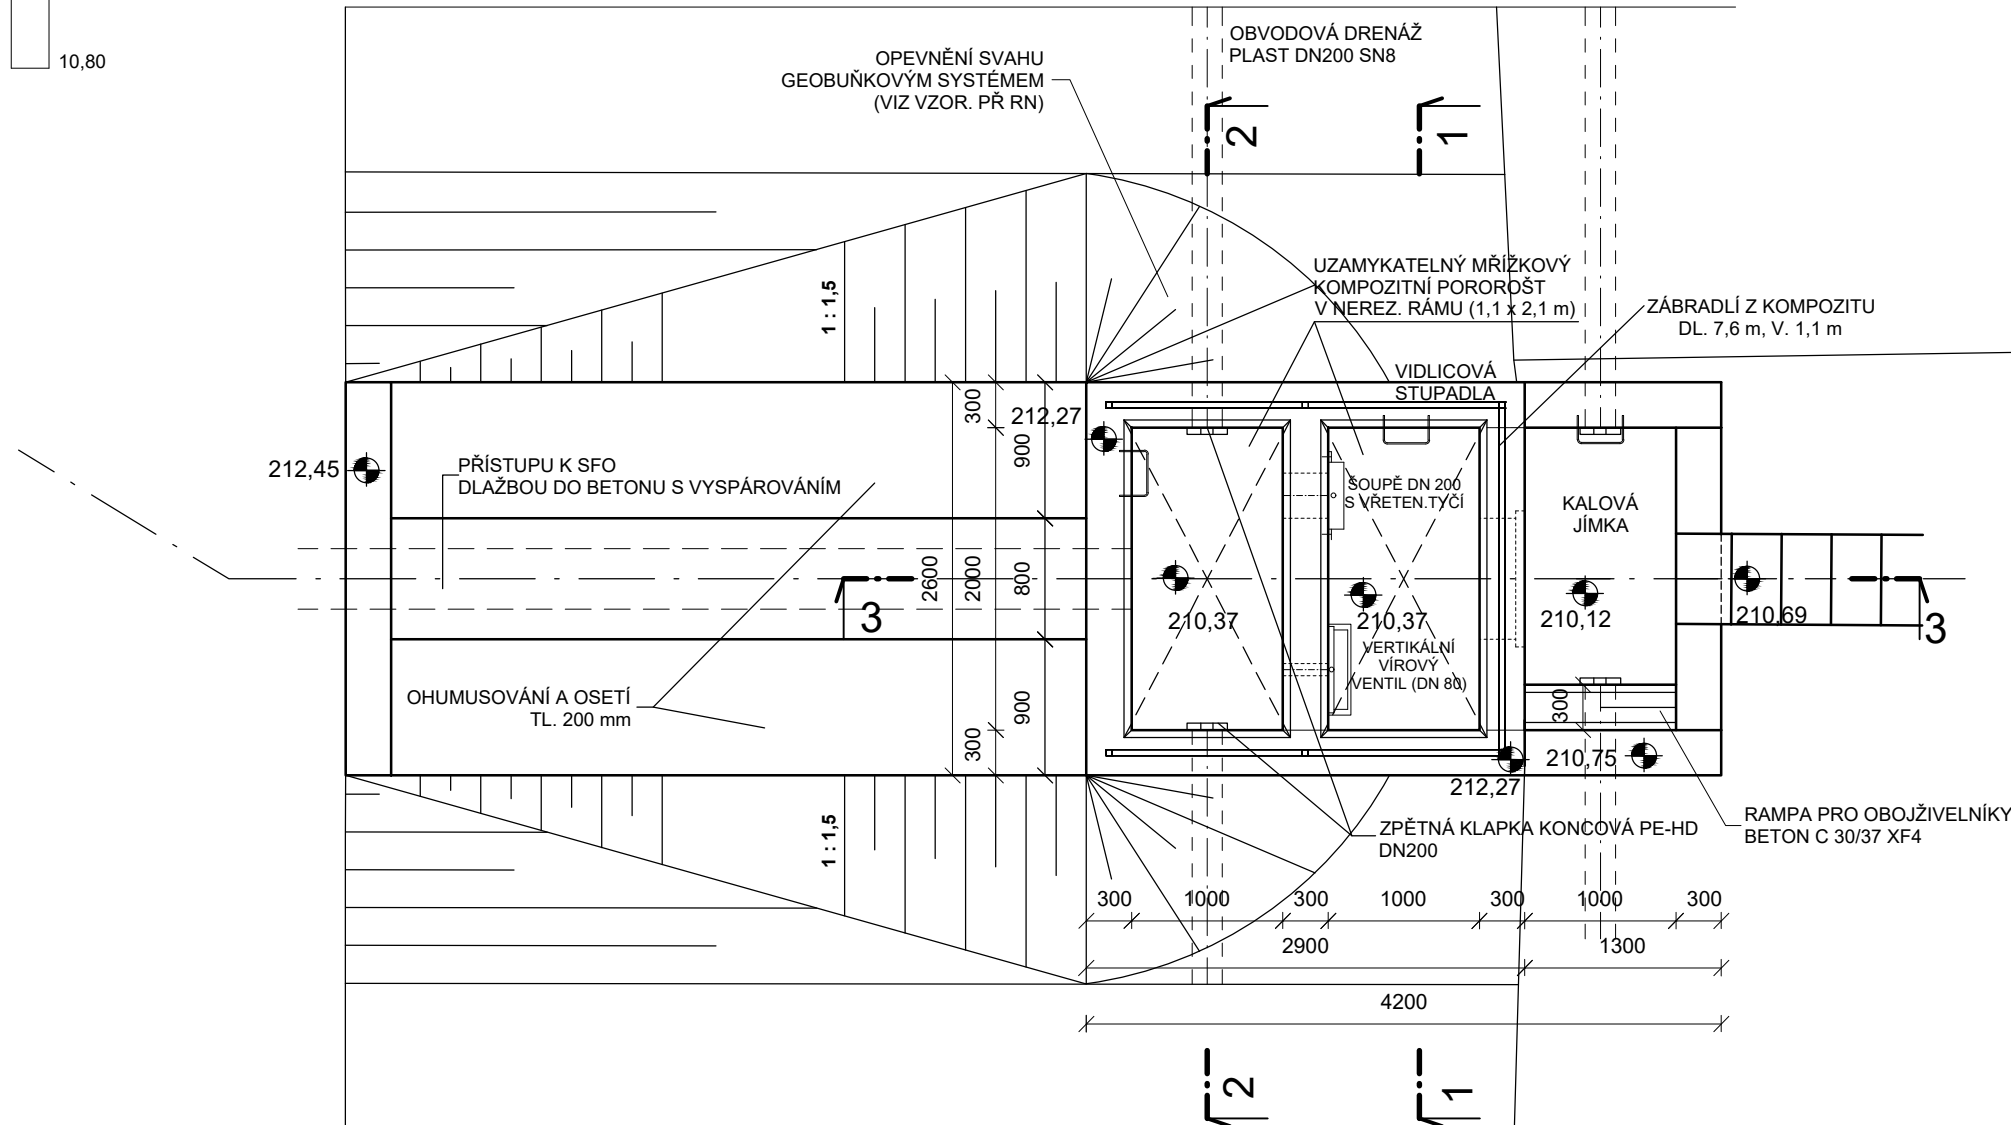

ŘEZ 2-2

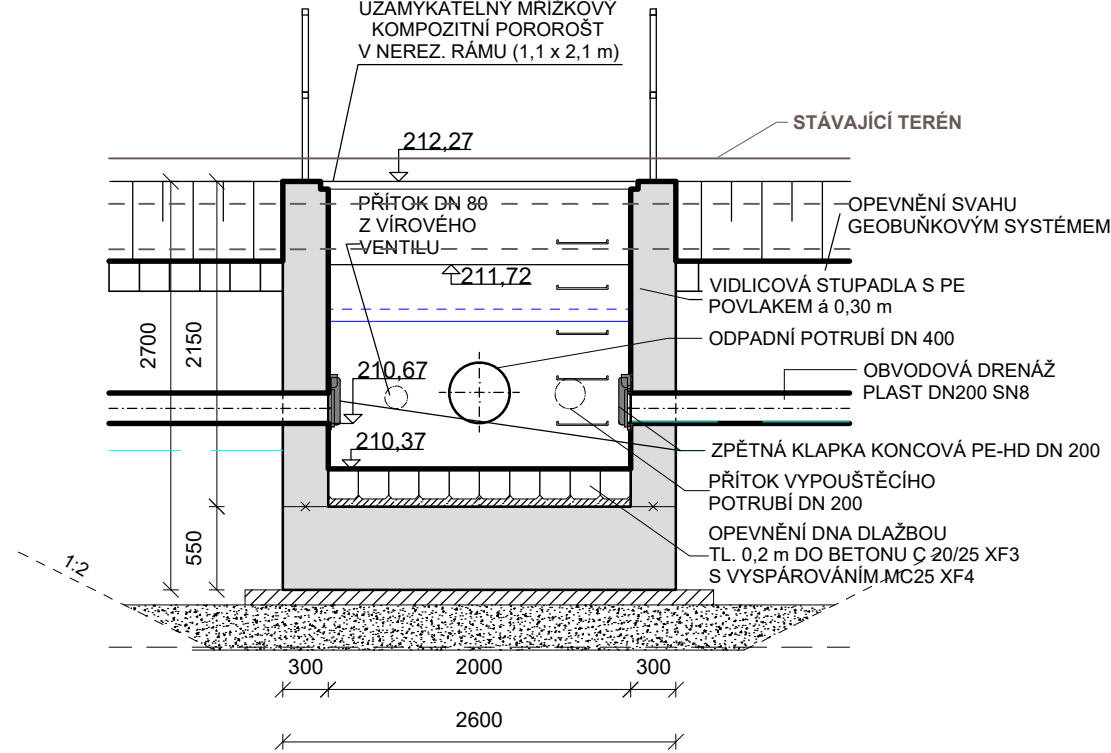

ŘEZ 1-1

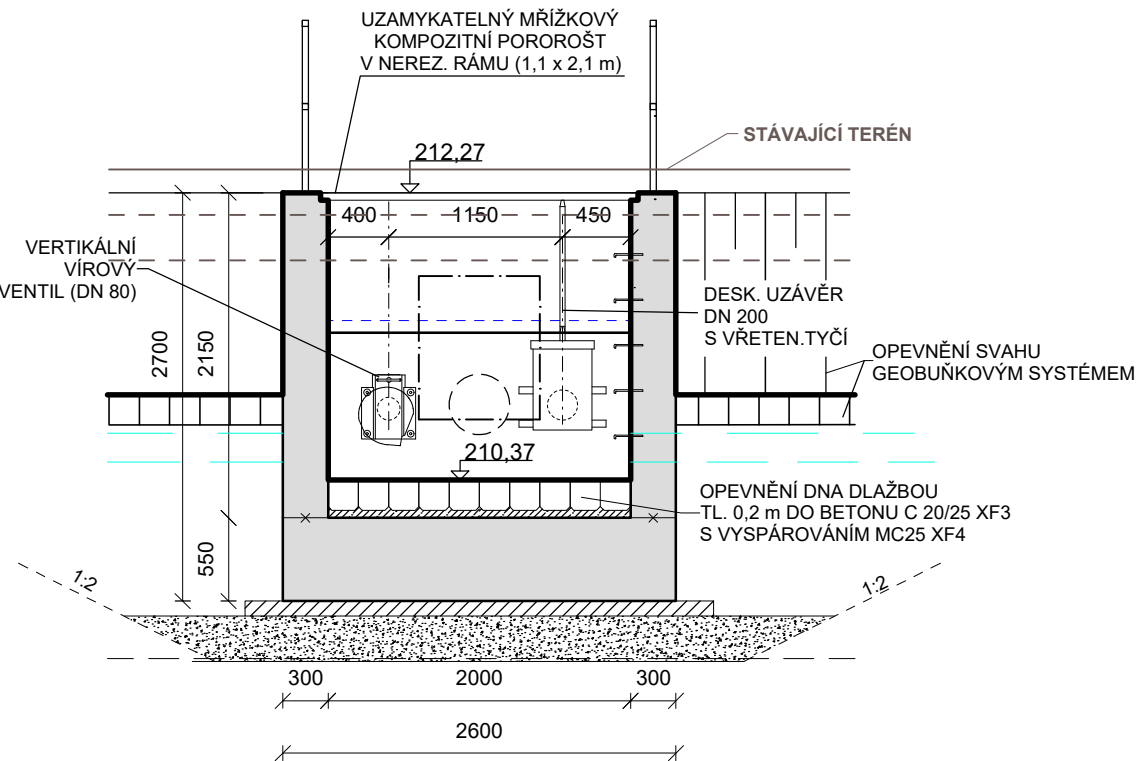

POZNÁMKA:
POŽADAVKY NA POHLEDOVÝ BETON KONSTRUKCE SFO Z HLEDISKA SMĚSI KAMENIVA, HUTNOSTI POVRCHU, BARVY, ODSŤÍNU, STEJNORODOSTI A ZPŮSOBU BEDNĚNÍ DLE TKP 18 HRANY ŽB KONSTRUKCE BUDOU ZKOSENY 30/30 mm
PROSTUPY VE STĚNÁCH A PRACOVNÍ SPÁRY BUDOU TĚSNĚNY TĚSNÍCÍ PÁSKOU
PRACOVNÍ A DILATAČNÍ SPÁRY V POHLEDOVÉM BETONU ZKOSENY DLE TKP 18
OPEVNĚNÍ PŘÍSTUPU K SFO BUDE PROVEDENO DLAŽBOU Z LOMOVÉHO KAMENE TL. 0,2 m DO BETONU C 20/25nXF3, S VYSPÁROVÁNÍM MC (XF4) (DLAŽBA Z KAMENE viz ČSN EN 13383-1 KÁMEN PRO VODNÍ STAVBY)

Souřadnicový systém: S-JTSK
Výškový systém: Bpv

SO 360.1

DUN a retenční nádrže na I/16

Objednatel:



ŘEDITELSTVÍ
SILNIC
A DÁLNIC

Ředitelství silnic a dálnic s. p.

Čerčanská 2023/12, Krč, 140 00 Praha 4



Valbek

Valbek, spol. s r.o.

Vaňurova 505/17
460 07 Liberec 3




Valbek

Zhotovitel:

Valbek, spol. s r.o.
Vaňurova 505/17
460 07 Liberec 3


Vypracoval

ING. V. JURÁNEK

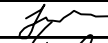

Zodp. projektant

ING. J. VANCL

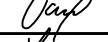

Tech. kontrola

ING. D. LANDA



Akce

I/16 MLADÁ BOLESLAV - MARTINOVICE

Příloha

SDRUŽENÝ FUNKČNÍ OBJEKT

Zak. číslo

21-LI13-001

Datum

02/2025

Stupeň

PDPS

Počet formátů

4 x A4

Měřítka

1 : 50

Č. přílohy

Paré

5