

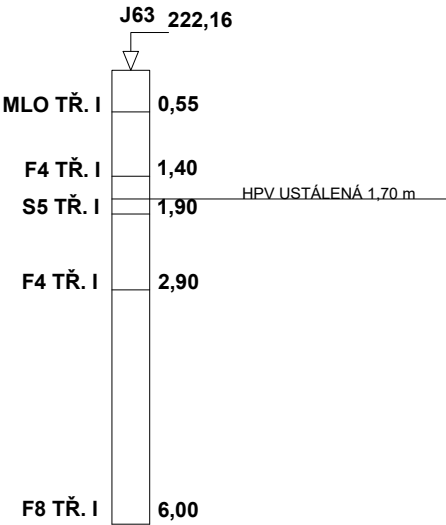


SO 360.10 DISPOZIČNÍ VÝKRES OLK
M 1:100

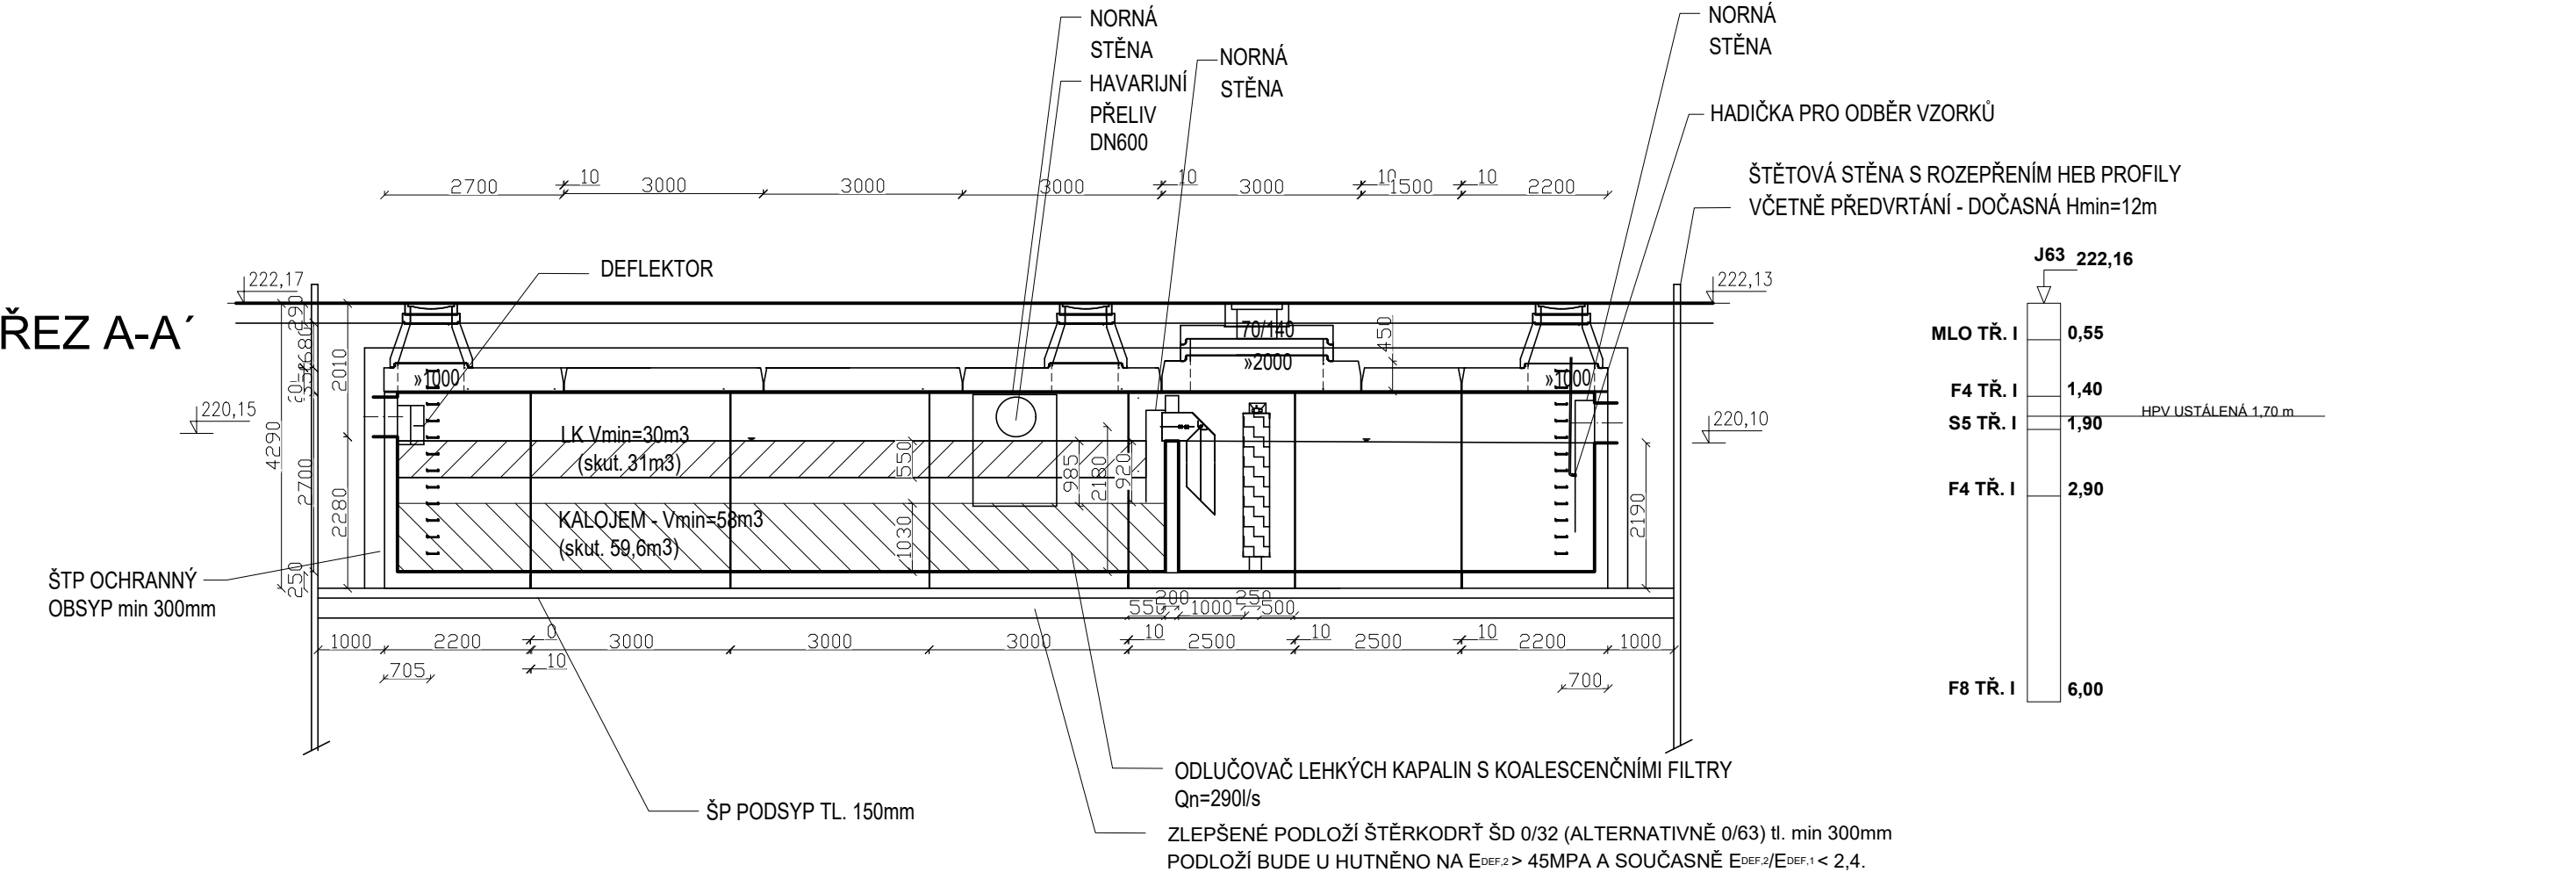

PŮDORYS

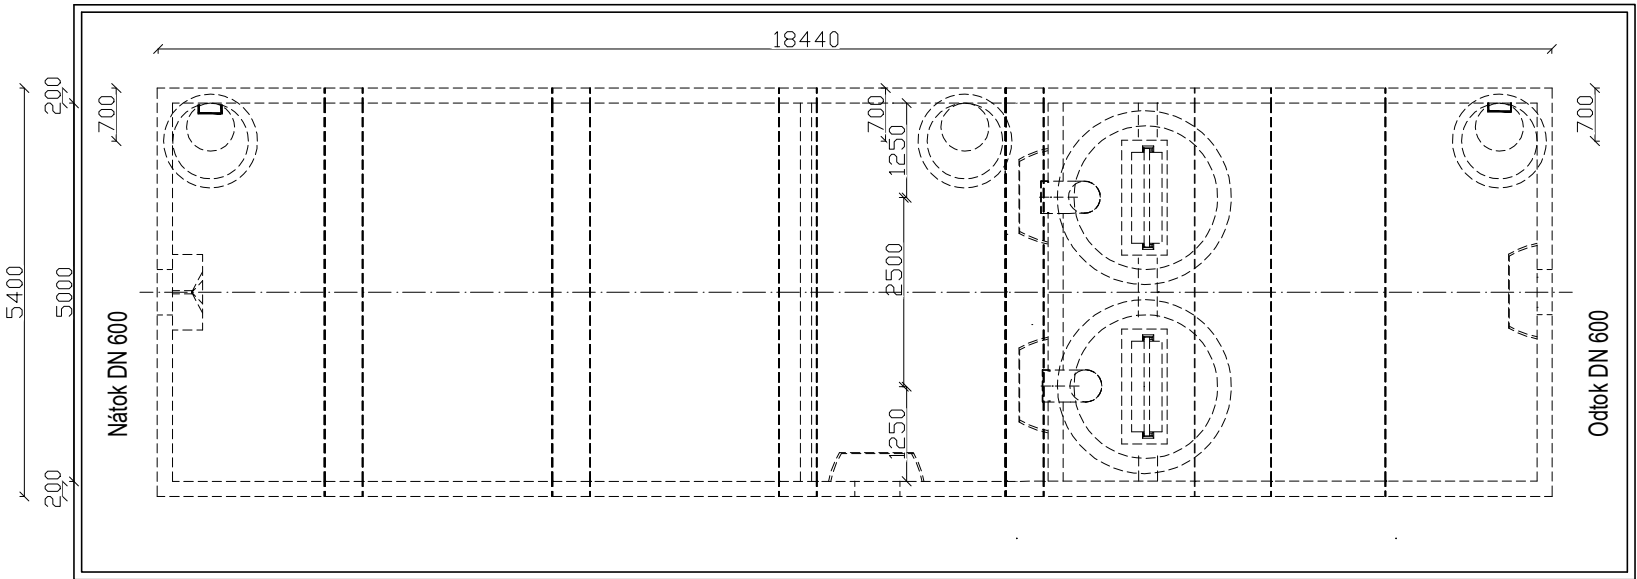

POZN.
- TVAR NÁDRŽE BUDE UPŘESNĚN V DALŠÍM STUPNI PD DLE KONKRÉTNÍHO DODAVATELE
NA ZÁKLADĚ VTD BUDE UPŘESNĚN ZPŮSOB ZALOŽENÍ POMOCÍ ŠTĚTOVNIC
- NÁDRŽE BUDOU VYBAVENY VÝSTUPY PRO OBOJŽIVELNÍKY
- DUN JE NAVRŽENA S VODOTĚSNÝMI SYSTÉMEM SEŠROUBOVÁNÍM PŘES TĚSNĚNÍ, ŠACHTOVÉ NÁSTAVBY POUŽÍVAJÍ STANDARDNÍ JAZYČKOVÉ TĚSNĚNÍ. NA STROPNÍ DESCE NÁDRŽE BUDOU ZABETONOVÁNY PROFILY SPOJE PRO TOTO TĚSNĚNÍ.
- DO KAŽDÉ ČÁSTI DUN MUSÍ BÝT UMOŽNĚN VSTUP PŘES VSTUPNÍ KOMÍN (STUPADLA / ŽEBŘÍK)
-VE DNĚ BUDE ZŘÍZENA ČERPACÍ JÍMKA PRO ČERPÁNÍ PŘÍPADNÉ PRŮSAKOVÉ VODY
-VNĚJŠÍ POVRCH STROPU OPATŘEN PENETRAČNÍM ASFALTOVÝM NÁTĚREM, SPOJE STROPNÍCH DÍLŮ NÁSLEDNĚ PŘEKRYT NATAVITELNÝMI ASFALTOVÝMI PÁSY

SO 360.10 DUN a retenční nádrže na I/16

Objednatel:



ŘEDITELSTVÍ
SILNIC
A DÁLNIC


Ředitelství silnic a dálnic s. p.
Čerčanská 2023/12, Krč, 140 00 Praha 4

Zhotovitel:



Valbek

Valbek, spol. s r.o.
Vaňurova 505/17
460 07 Liberec 3

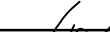	Vypracoval	ING. J. VANCL		Zak. číslo	21-LI13-001
	Zodp. projektant	ING. J. VANCL		Datum	02/2025
	Tech. kontrola	ING. D. LANDA		Stupeň	PDPS
	Akce			Počet formátů	3 x A4
	I/16 MLADÁ BOLESLAV - MARTINOVICE			Měřítko	1 : 100
Zhotovitel: Valbek, spol. s r.o. Vaňurova 505/17 460 07 Liberec 3	Příloha DISPOZIČNÍ VÝKRES OLK			Č. přílohy	Paré
				2	