


PODÉLNÝ PROFIL HRÁZÍ RETENČNÍ NÁDRŽE

M 1 : 500

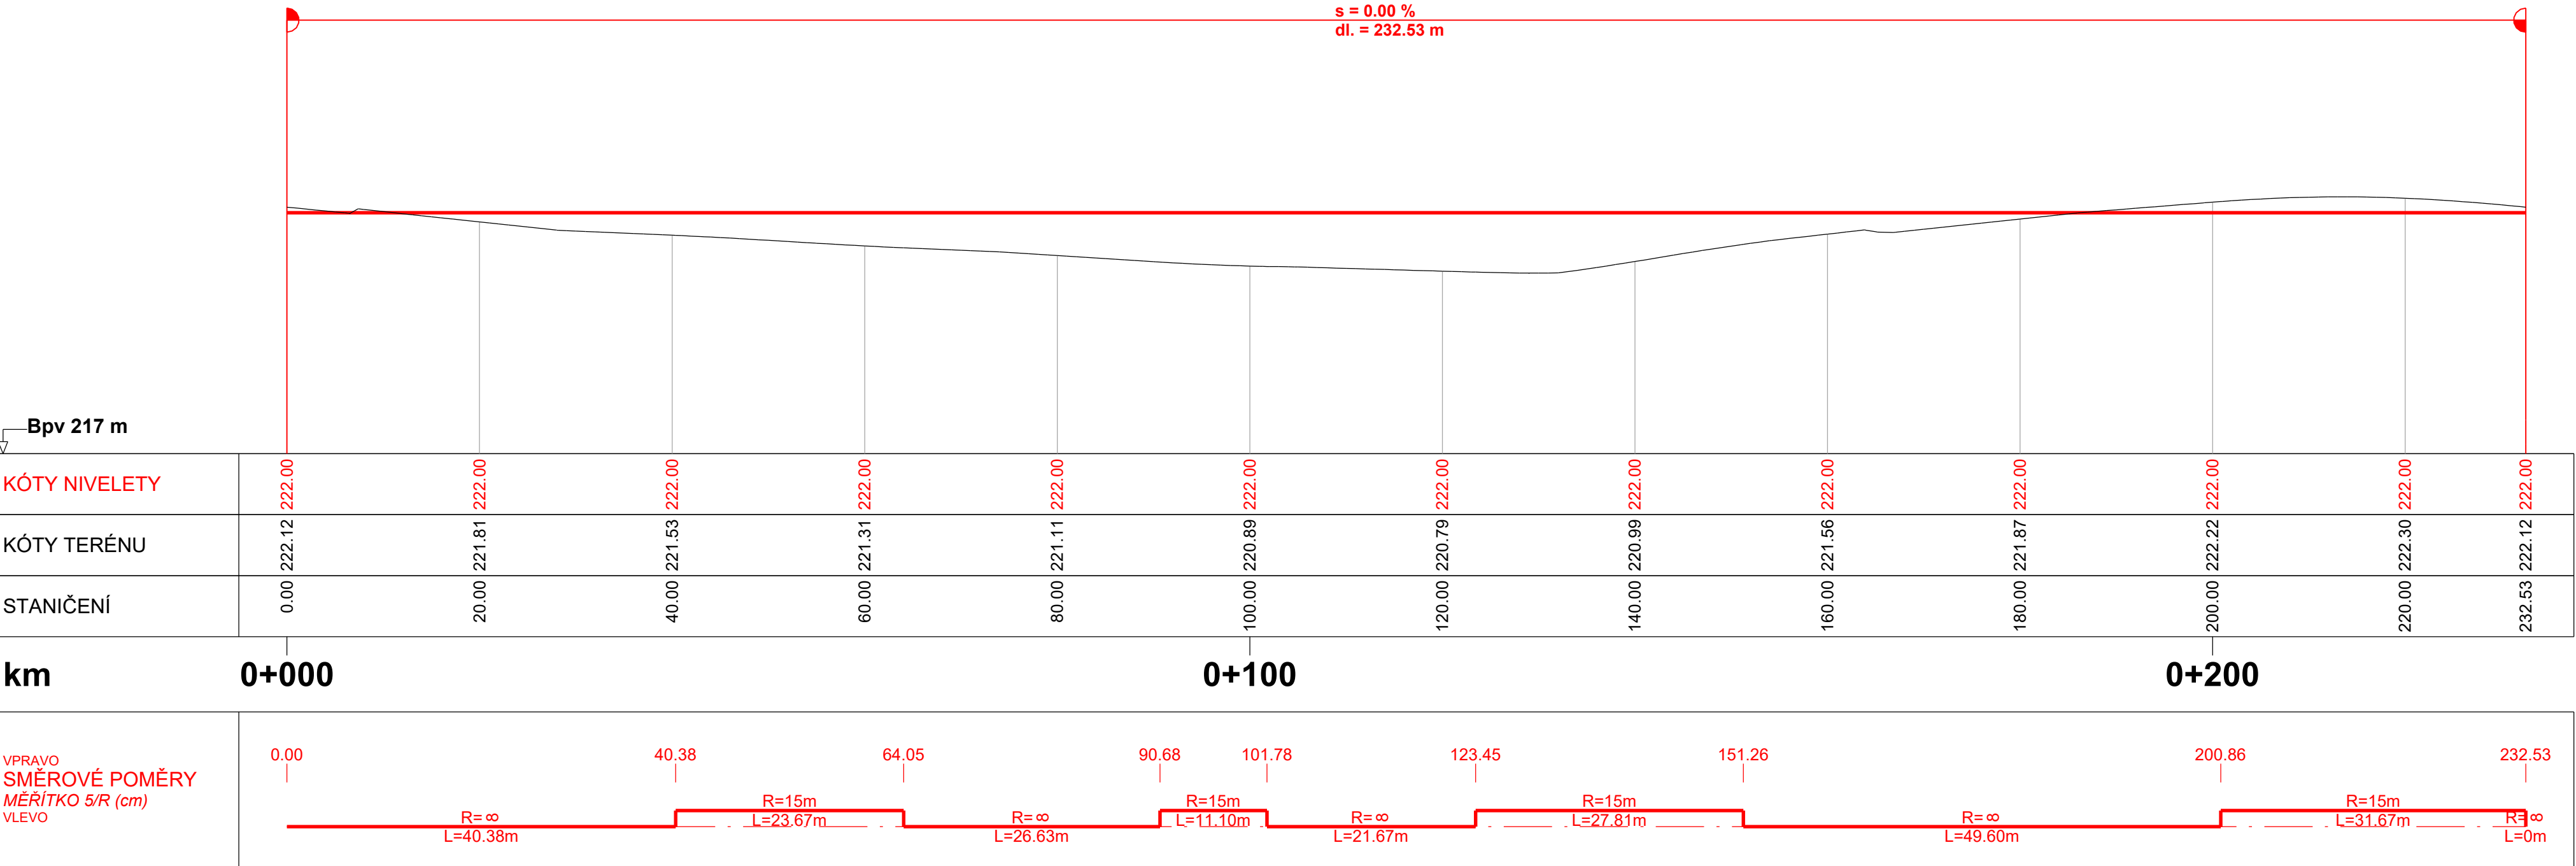

Souřadnicový systém: S-JTSK
/ýškový systém: Bpv

SO 360.10 DUN a retenční nádrže na I/16

Čerčanská 2023/12, Krč, 140 00 Praha 4

/aňurova 505/17
460 07 Liberec 3

3