


PODÉLNÝ ŘEZ RETENČNÍ NÁDRŽÍ M 1:100

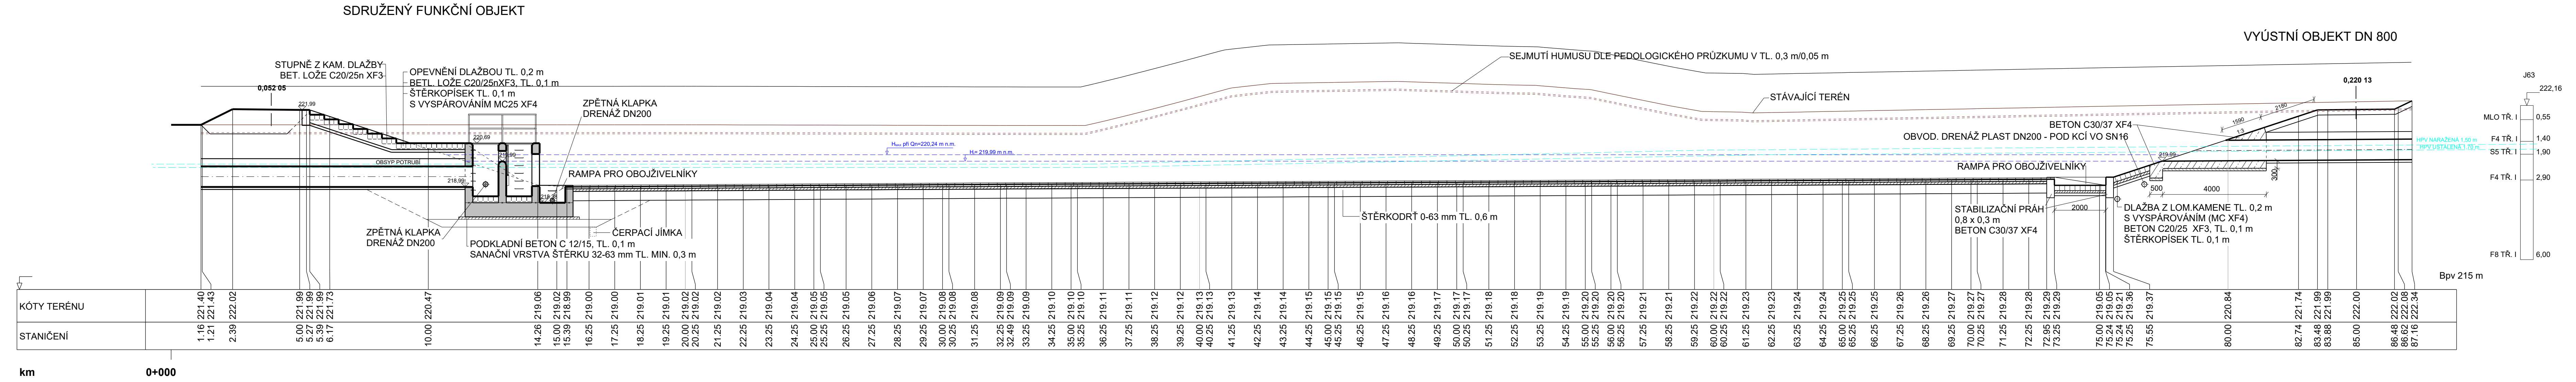

Souřadnicový systém: S-JTSK
Výškový systém: Bpv

360.10 DUN a retenční nádrže na I/16

Objednatel:



**ŘEDITELSTVÍ
SILNIC
A DÁLNIC**

Ředitelství silnic a dálnic s. p.
Čerčanská 2023/12, Krč, 140 00 Praha 4

Zhotovitel:	Valbek, spol. s r.o. Vaňurova 505/17 460 07 Liberec 3
	

	Vypracoval	ING. V. JURÁNEK		Zak. číslo	21-L113-001	
	Zodp. projektant	ING. J. VANCL		Datum	02/2025	
	Tech. kontrola	ING. D. LANDA		Stupeň	PDPS	
	Akce	I/16 MLADÁ BOLESLAV - MARTINOVICE			Počet formátů	6 x A4
	Zhotovitel: Valbek, spol. s r.o. Vafurkova 505/II 460 07 Liberec 3	Přiloha	PODELNÝ ŘEZ RETENČNÍ NÁDRŽÍ			Měřitko
Č. přílohy						Paré
4.1						