


PŘÍČNÝ ŘEZ RETENČNÍ NÁDRŽÍ  
M 1:100

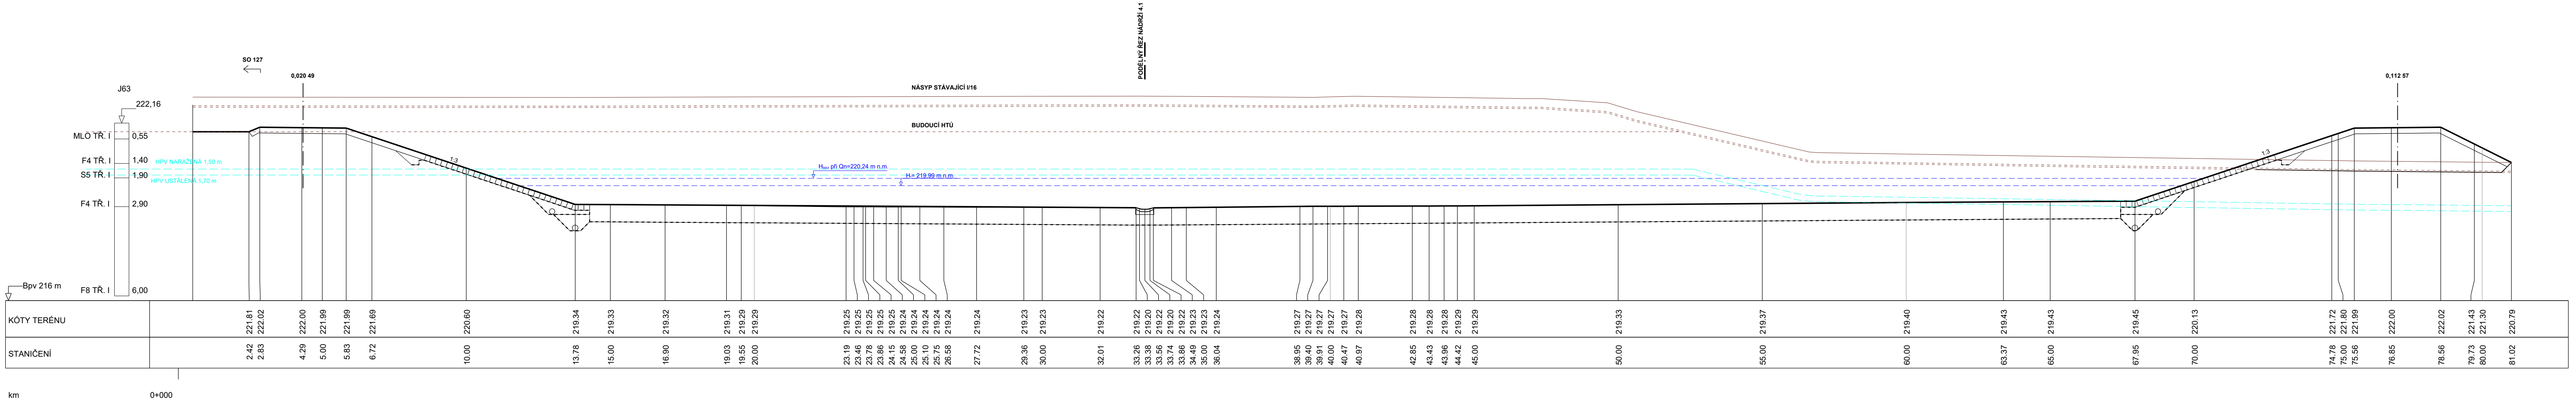

Souřadnicový systém: S-JTSK  
Výškový systém: Bpv

360.10 DUN a retenční nádrže na I/16

Objednatel:



**ŘEDITELSTVÍ  
SILNIC  
A DÁLNIC**

**Ředitelství silnic a dálnic s. p.**  
Čerčanská 2023/12, Krč, 140 00 Praha 4

Zhotovitel:



**Valbek, spol. s r.o.**  
Vaňurova 505/17  
460 07 Liberec 3

|                                                                                      |                                               |                            |                                                                                       |               |             |
|--------------------------------------------------------------------------------------|-----------------------------------------------|----------------------------|---------------------------------------------------------------------------------------|---------------|-------------|
|  | Vypracoval                                    | ING. V. JURÁNEK            |    | Zak. číslo    | 21-LI13-001 |
|                                                                                      | Zodp. projektant                              | ING. J. VANCL              |   | Datum         | 02/2025     |
|                                                                                      | Tech. kontrola                                | ING. D. LANDA              |  | Stupeň        | PDPS        |
|                                                                                      | Akce<br><br>I/16 MLADÁ BOLESLAV - MARTINOVICE |                            |                                                                                       | Počet formátů | 6xA4        |
| Měřítko                                                                              |                                               |                            |                                                                                       | 1:100         |             |
| Č. přílohy                                                                           |                                               |                            |                                                                                       | Paré          |             |
| Zhotovitel:<br>Valbek, spol. s r.o.<br>Vaňurova 505/17<br>460 07 Liberec 3           | Příloha                                       | PŘÍČNÝ ŘEZ RETENČNÍ NÁDRŽÍ |                                                                                       |               | 4.2         |
|                                                                                      |                                               |                            |                                                                                       |               |             |