
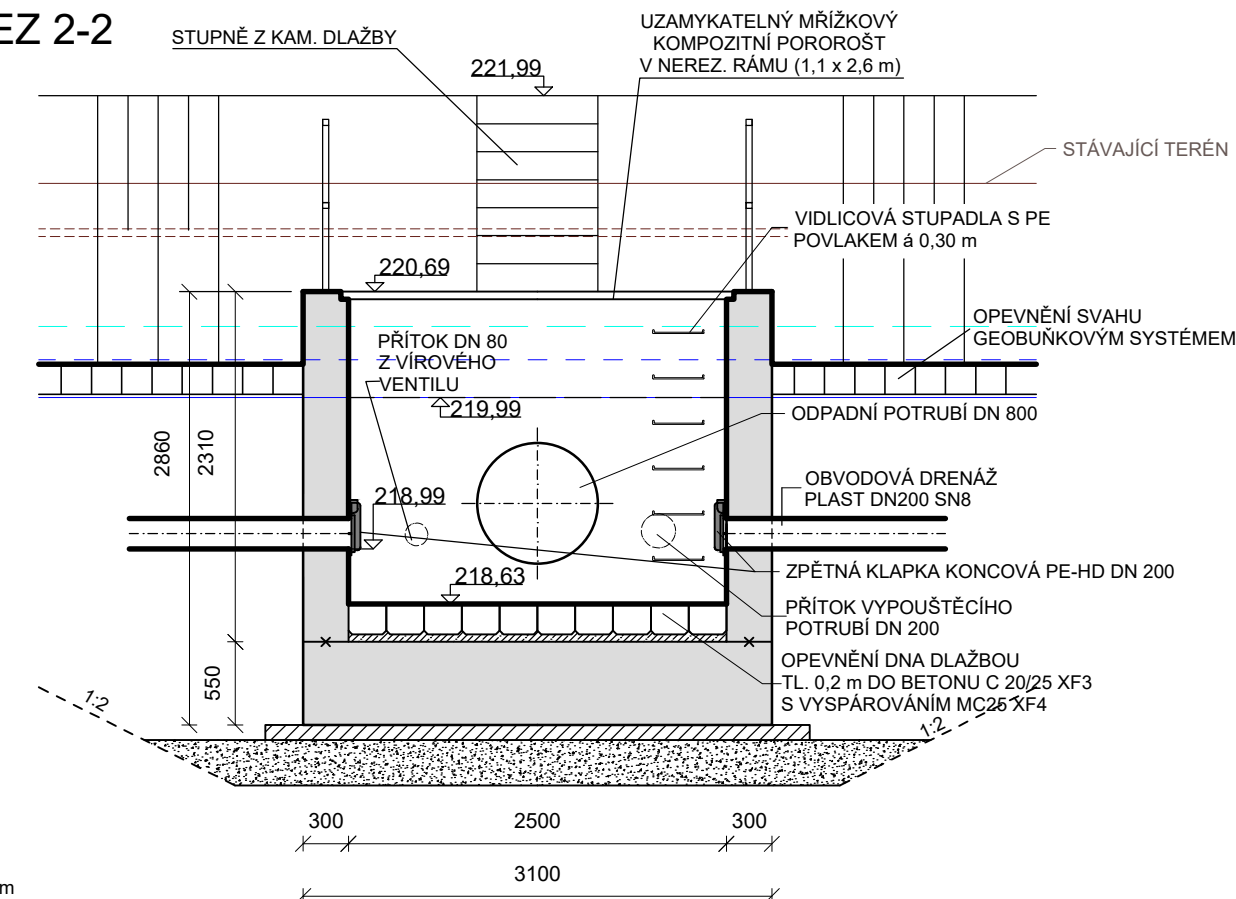


SO 360.10 - SFO
M 1:50

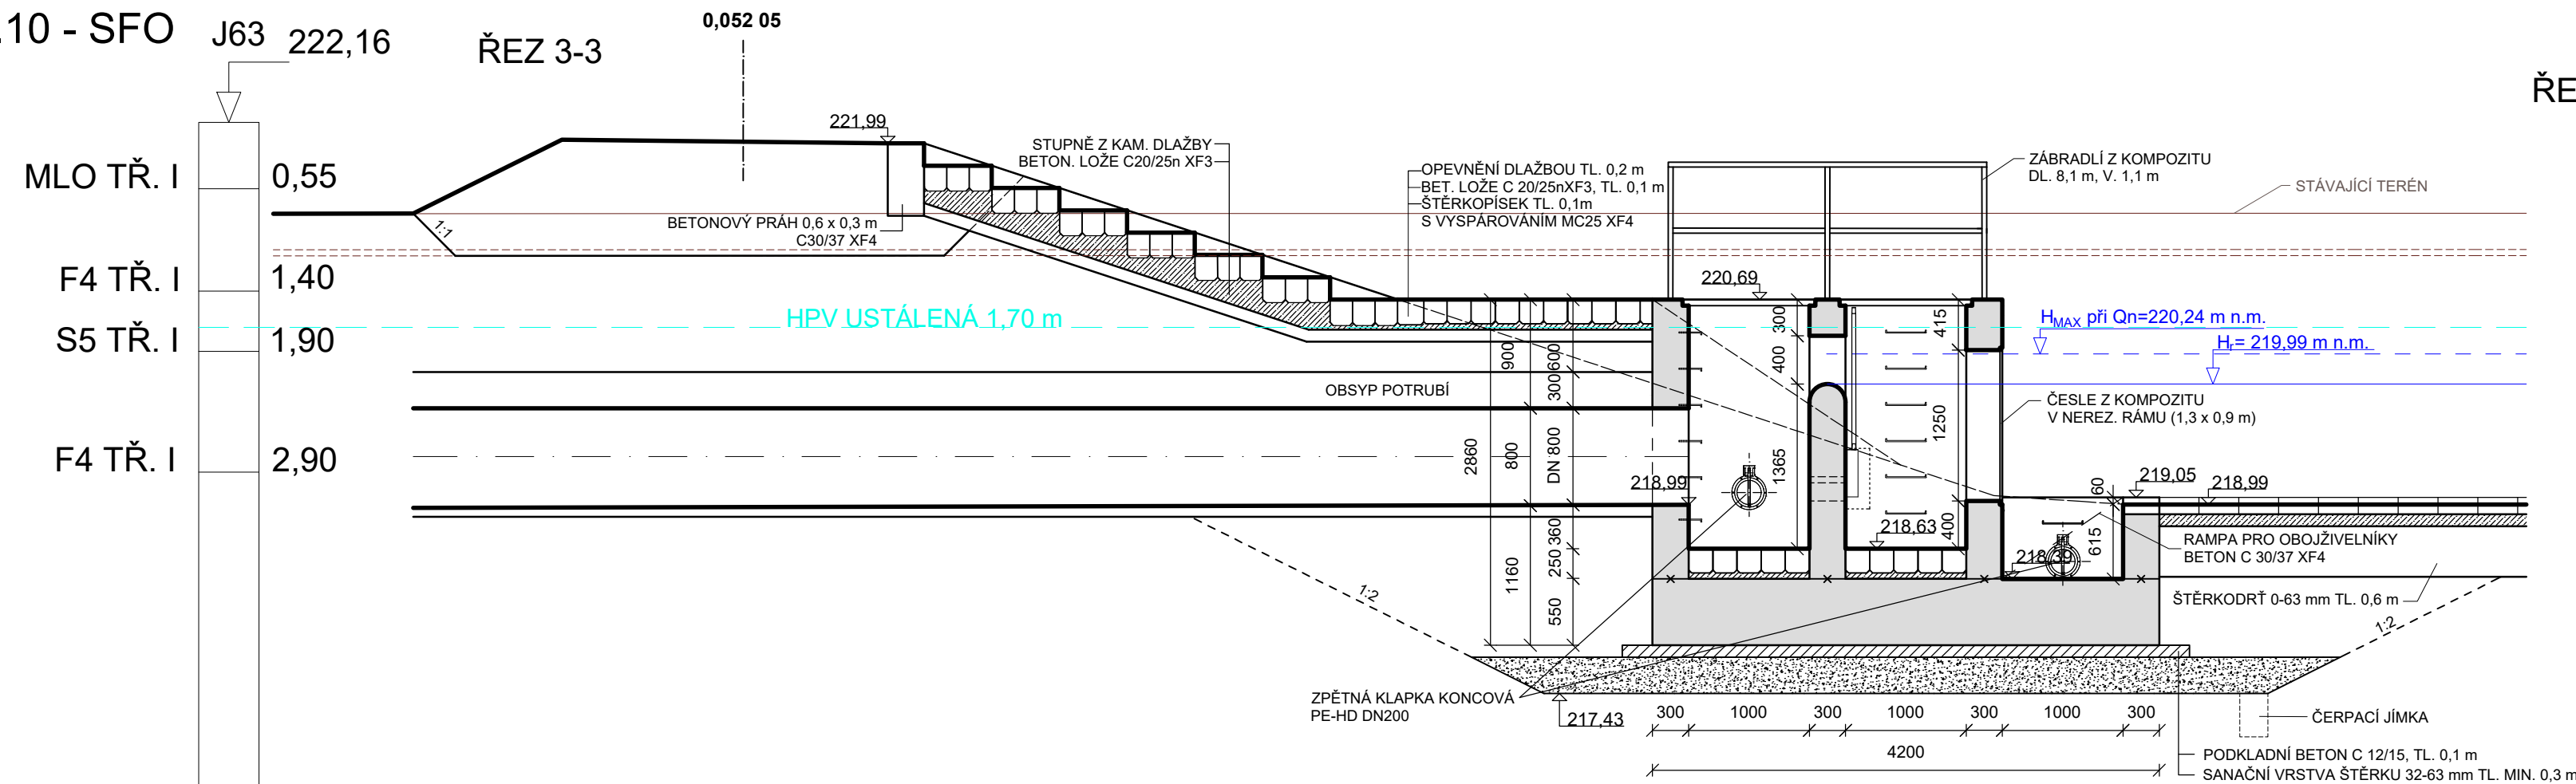

POZNÁMKA:

POŽADAVKY NA POHLEDOVÝ BETON KONSTRUKCE SFO Z HLEDISKA SMĚSI KAMENIVA, HUTNOSTI POVRCHU, BARVY, ODSTŮNÍ, STEJNORODOSTI A ZPŮSOBU BEDNĚNÍ DLE TKP 18
HRANY ŽB KONSTRUKCE BUDOU ZKOSENY 30/30 mm
PROSTUPY VE STĚNÁCH A PRACOVNÍ SPÁRY BUDOU TĚSNĚNY TĚSNÍCÍ PÁSKOU
PRACOVNÍ A DILATAČNÍ SPÁRY V POHLEDOVÉM BETONU ZKOSENY DLE TKP 18
OPEVNĚNÍ PŘÍSTUPU K SFO BUDE PROVEDENO DLAŽBOU
Z LOMOVÉHO KAMENE TL. 0,2 m DO BETONU C 20/25n(XF3, S VYSYPÁROVÁNÍM MC (XF4)
(DLAŽBA Z KAMENE viz ČSN EN 13383-1 KÁMEN PRO VODNÍ STAVBY)

Souřadnicový systém: S-JTSK

Výškový systém: Bpv

SO 360.10

DUN a retenční nádrže na I/16

Objednatel:

ŘEDITELSTVÍ SILNIC A DÁLNIC

Ředitelství silnic a dálnic s. p.

Čerčanská 2023/12, Krč, 140 00 Praha 4



Valbek, spol. s r.o.

Vaňurova 505/17

460 07 Liberec 3



Zhotovitel:
Valbek, spol. s r.o.
Vaňurova 505/17
460 07 Liberec 3

	Příloha
--	----------------

SDRUŽENÝ FUNKČNÍ OBJEKT

číslo	21-LI13-001
-------	-------------

Expiry Date	21/12/2025
Expiry Date	02/2025

číslo	02/2023
datum	2023

Open	PDPs
100	100

čet formátů	4 x A4
-------------	--------

řítka	1 : 50
-------	--------

přílohy	Paré
---------	------

© 2006 The Authors

5

•

© 2006 The Authors
