


PODÉLNÝ ŘEZ RETENČNÍ NÁDRŽÍ

M 1:100

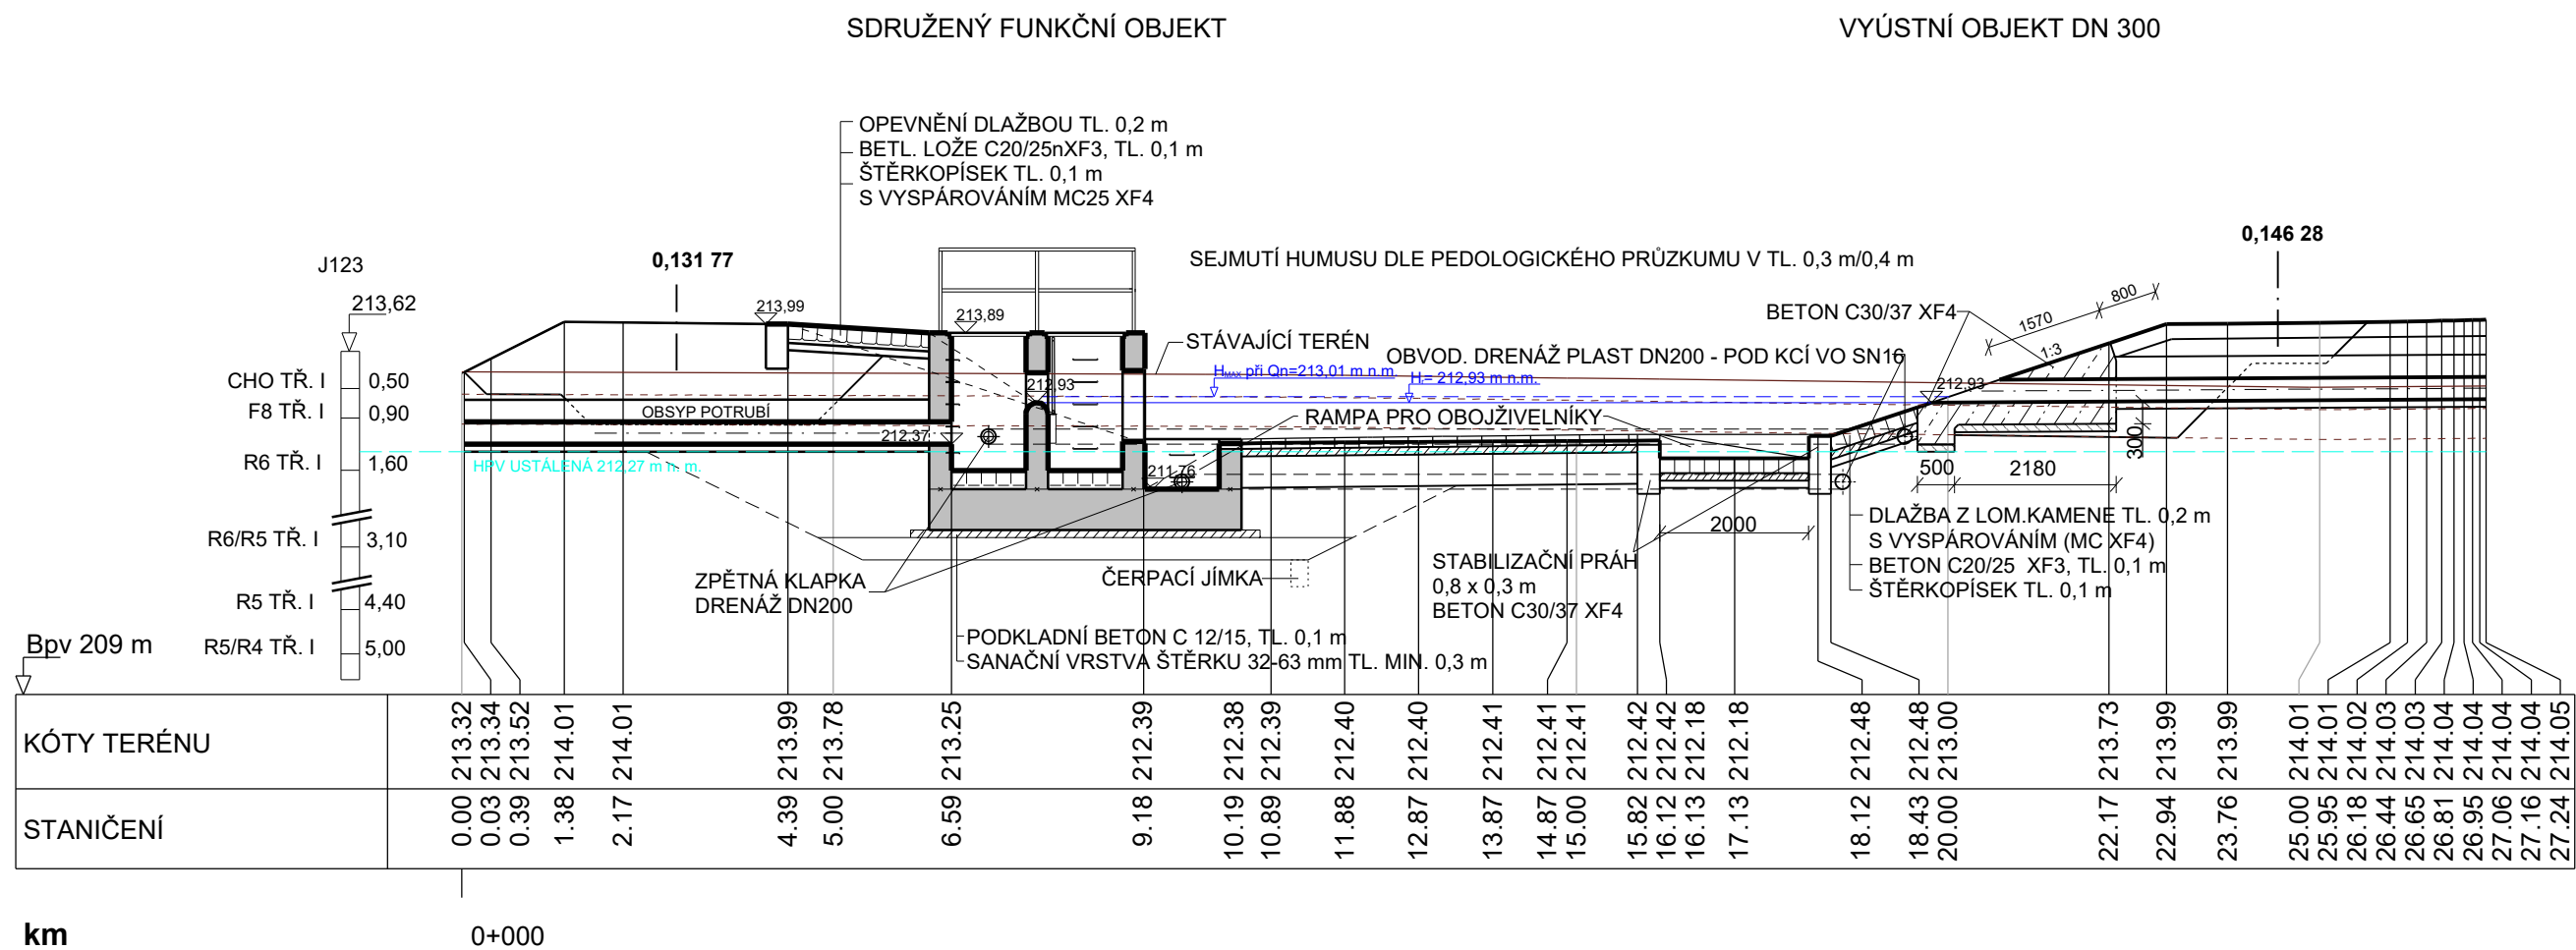

Souřadnicový systém: S-JTSK
Výškový systém: Bpv

SO 360.4 DUN a retenční nádrže na I/16

Objednatel:

ŘEDITELSTVÍ SILNIC A DÁLNIC

Ředitelství silnic a dálnic s. p.

Čerčanská 2023/12, Krč, 140 00 Praha 4

Zhotovitel:**Valbek, spol. s r.o.**

Vaňurova 505/17
460 07 Liberec 3

	Vypracoval	ING. V. JURÁNEK	<i>Juránek</i>	Zak. číslo	21-LI13-001
	Zodp. projektant	ING. J. VANCL	<i>Vancl</i>	Datum	02/2025
	Tech. kontrola	ING. D. LANDA	<i>Landa</i>	Stupeň	PDPS
	Akce			Počet formátů	4 x A4
I/16 MLADÁ BOLESLAV - MARTINOVICE				Měřítko	1:100
				Č. přílohy	Paré
Zhotovitel: Valbek, spol. s r.o. Vaňurova 505/17 460 07 Liberec 3	Příloha PODÉLNÝ ŘEZ RETENČNÍ NÁDRŽÍ			4.1	