



SO 360.4 - SFO
M 1:50

ŘEZ 3-3


0,131 77

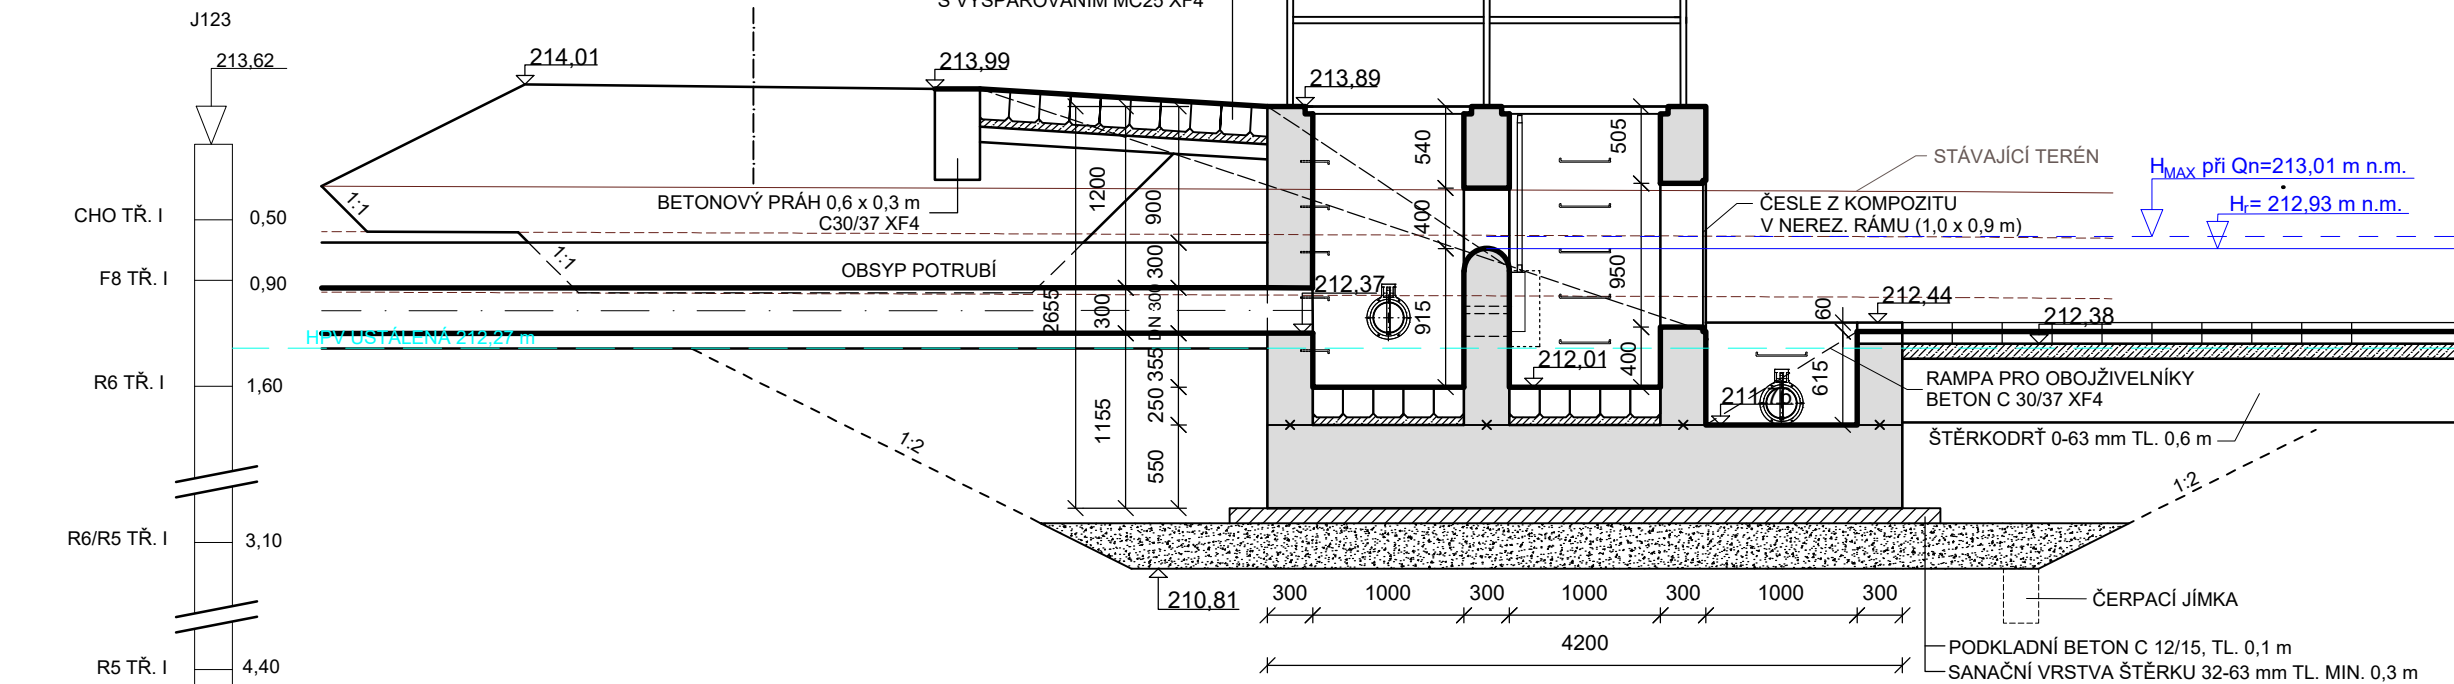


PŮDORYS

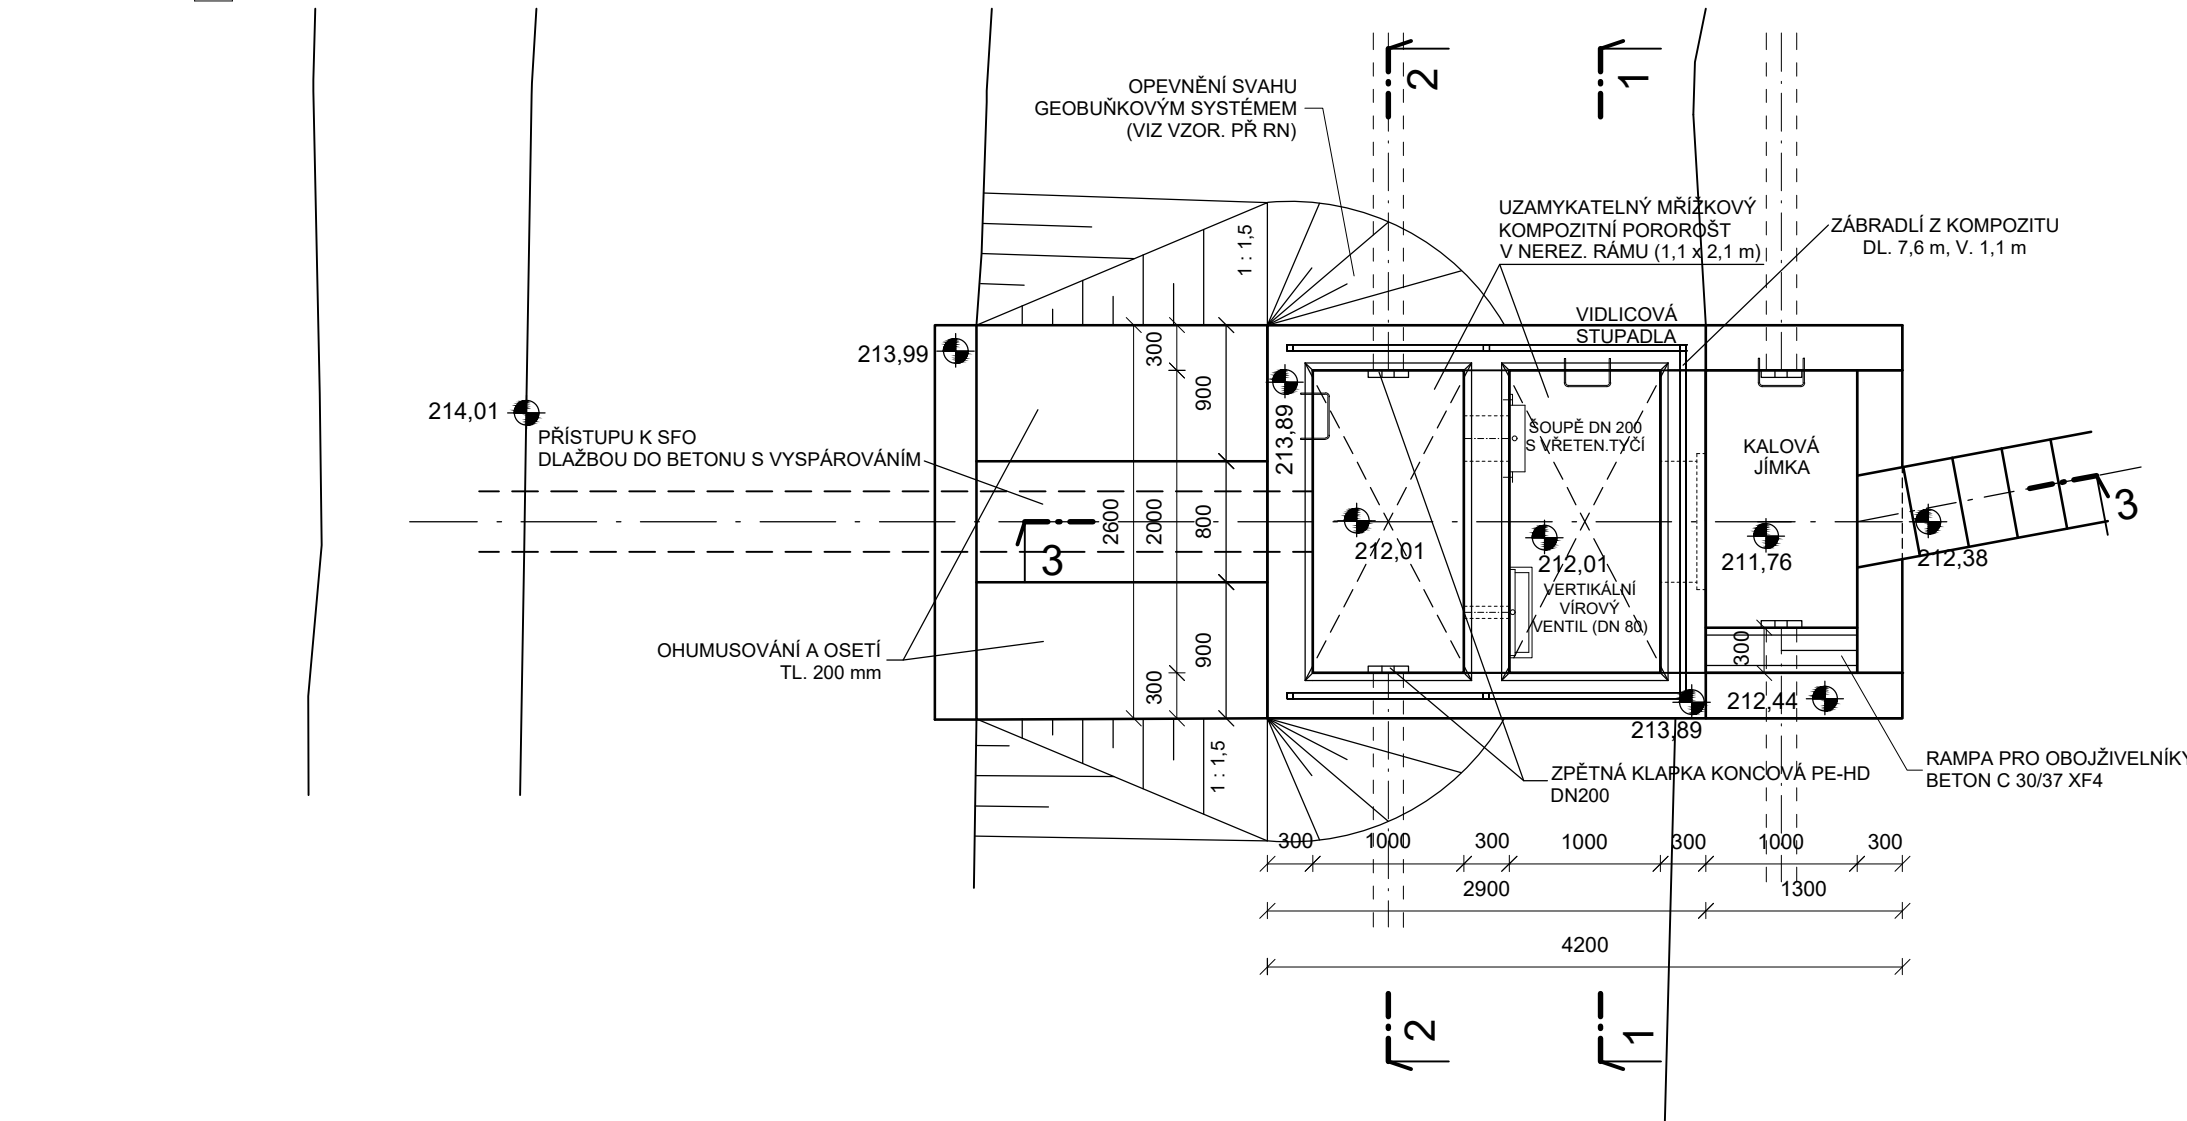

ŘEZ 2-2

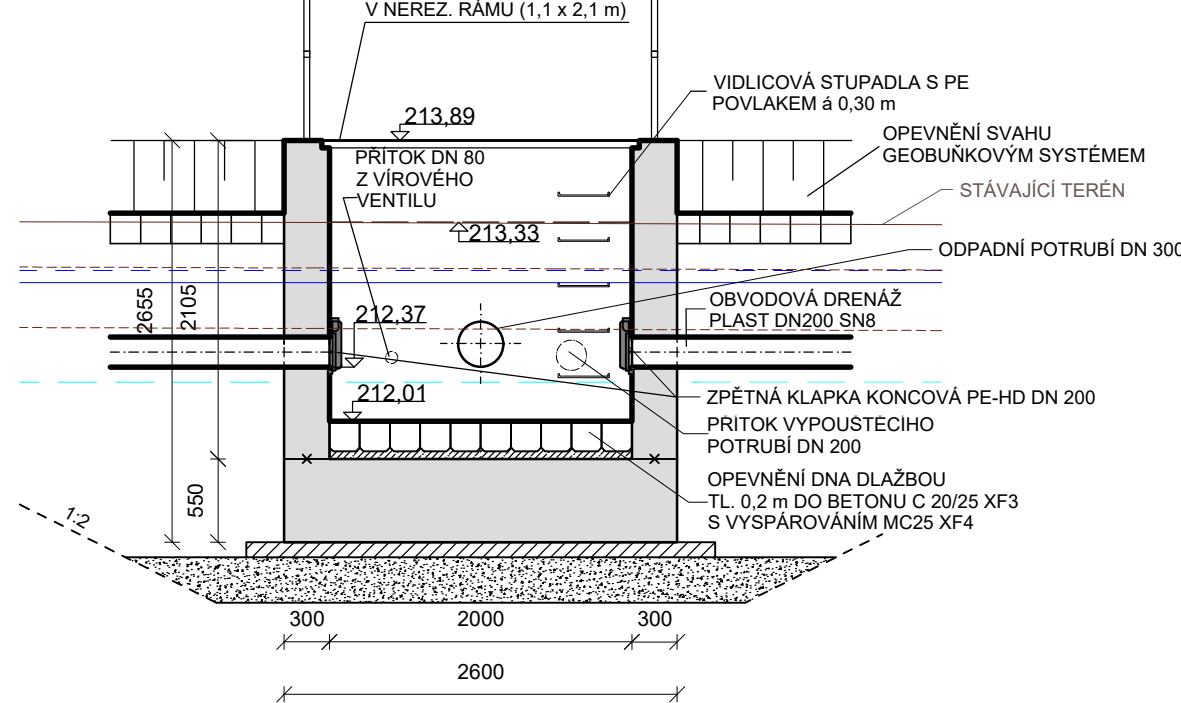

ŘEZ 1-1

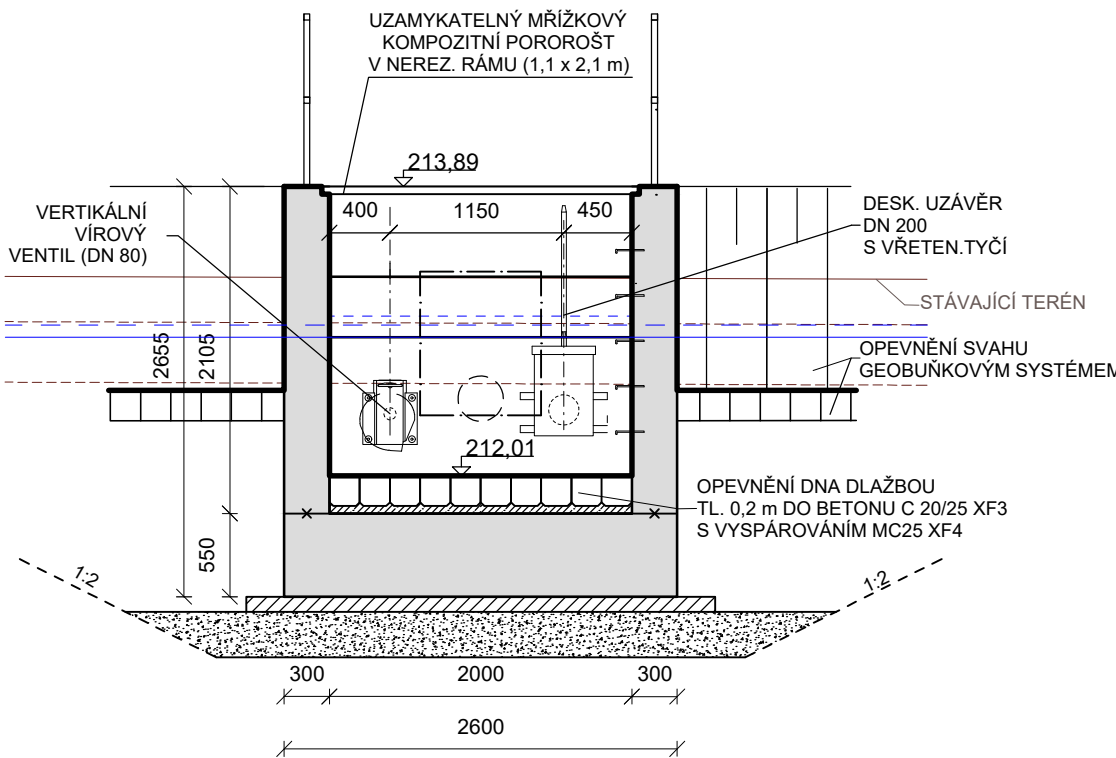

POZNÁMKA:

POŽADAVKY NA POHLEDOVÝ BETON KONSTRUKCE SFO Z HLEDISKA SMĚSI KAMENIVA, HUTNOSTI POVRCHU, BARVY, ODSŤÍNU, STEJNORODOSTI A ZPŮSOBU BEDNĚNÍ DLE TKP 18 HRANY ŽB KONSTRUKCE BUDOU ZKOŠENY 30/30 mm PROSTUPY VE STĚNÁCH A PRACOVNÍ SPÁRY BUDOU TĚSNĚNY TĚSNÍCÍ PÁSKOU PRACOVNÍ A DILATAČNÍ SPÁRY V POHLEDOVÉM BETONU ZKOŠENY DLE TKP 18 OPEVNĚNÍ PŘÍSTUPU K SFO BUDE PROVEDENO DLAŽBOU Z LOMOVÉHO KAMENE TL. 0,2 m DO BETONU C 20/25nXF3, S VYSPÁROVÁNÍM MC (XF4) (DLAŽBA Z KAMENE viz ČSN EN 13383-1 KÁMEN PRO VODNÍ STAVBY)

Souřadnicový systém: S-JTSK
Výškový systém: BpV

SO 360.4

DUN a retenční nádrže na I/16

Objednatel:



ŘEDITELSTVÍ
SILNIC
A DÁLNIC

Ředitelství silnic a dálnic s. p.
Čerčanská 2023/12, Krč, 140 00 Praha 4



Valbek, spol. s r.o.
Vaňurova 505/17
460 07 Liberec 3



Zhotovitel:
Valbek, spol. s r.o.
Vaňurova 505/17
460 07 Liberec 3

Příloha

SDRUŽENÝ FUNKČNÍ OBJEKT

5