


PODÉLNÝ ŘEZ RETENČNÍ NÁDRŽÍ

M 1:100

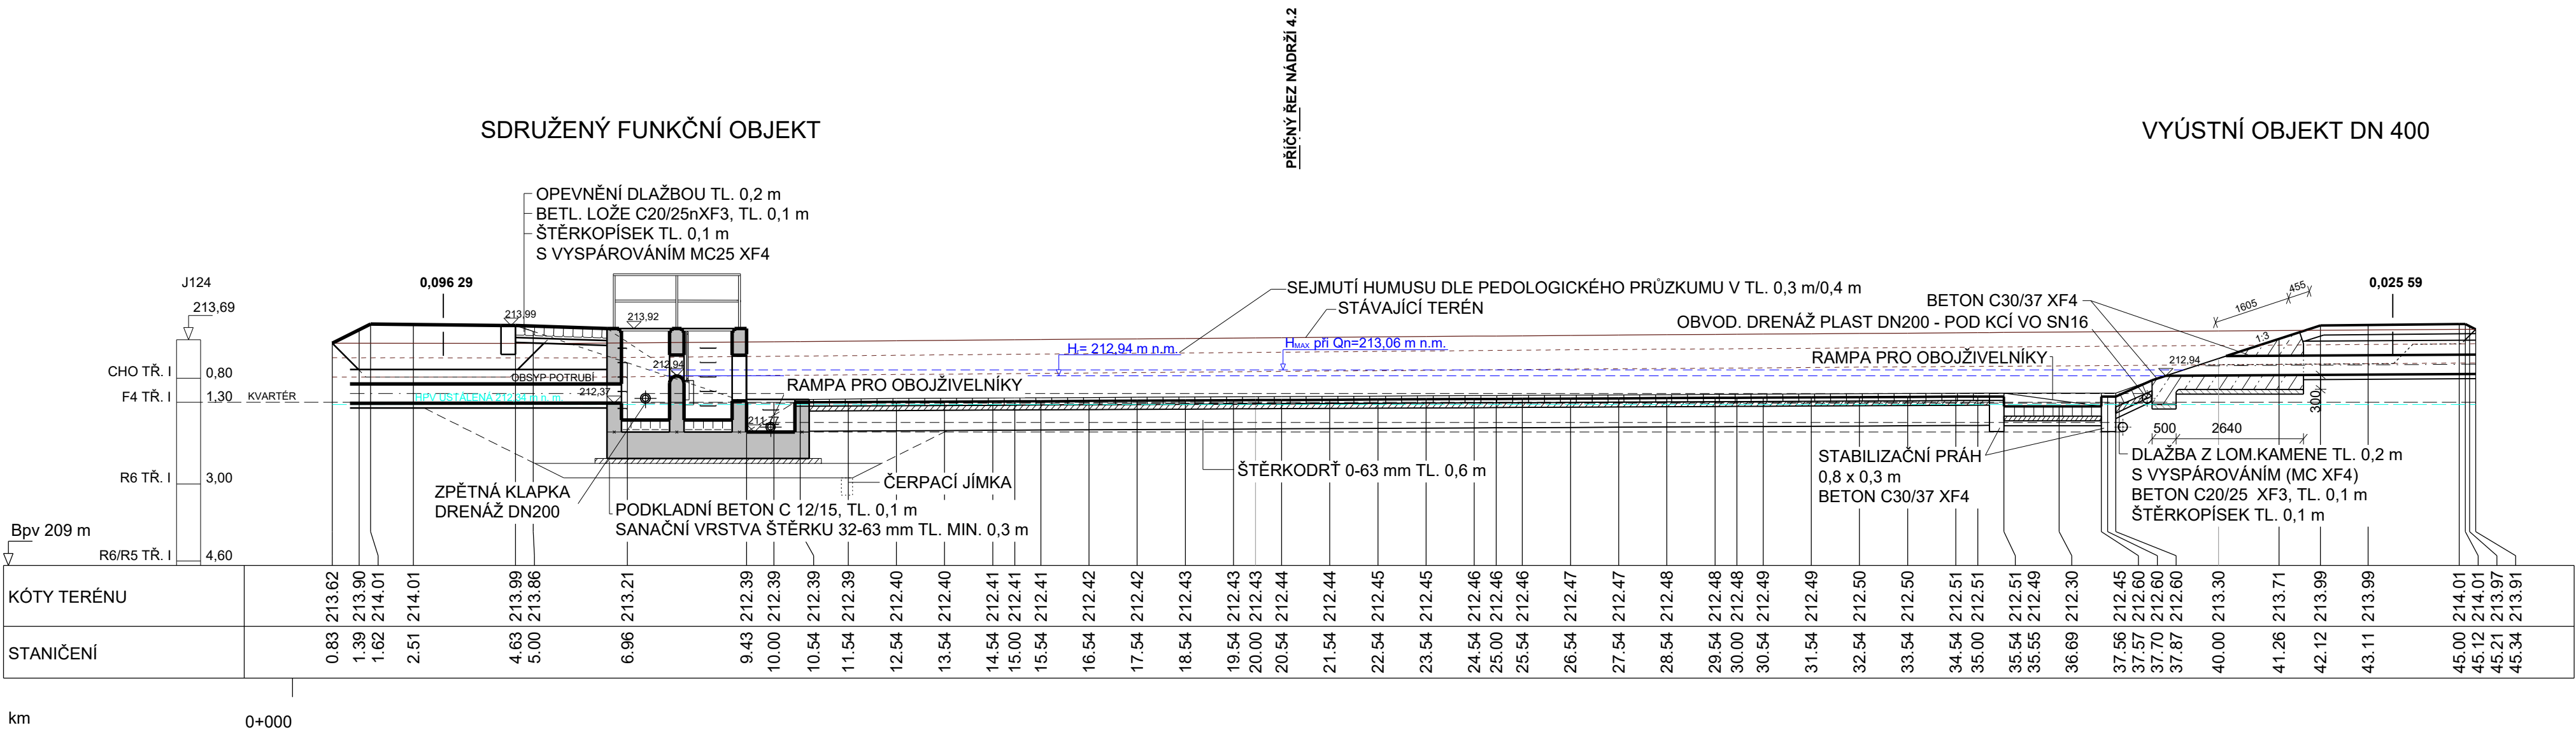

Souřadnicový systém: S-JTSK
Výškový systém: Bpv

360.5 DUN a retenční nádrže na I/16

Objednatel:

ŘEDITELSTVÍ SILNIC A DÁLNIC

Ředitelství silnic a dálnic s. p.

Čerčanská 2023/12, Krč, 140 00 Praha 4

Zhotovitel:

**Valbek, spol. s r.o.**

Vaňurova 505/17
460 07 Liberec 3

	Vypracoval	ING. V. JURÁNEK		Zak. číslo	21-LI13-001	
	Zodp. projektant	ING. J. VANCL		Datum	02/2025	
	Tech. kontrola	ING. D. LANDA		Stupeň	PDPS	
	Akce	I/16 MLADÁ BOLESLAV - MARTINOVICE			Počet formátů	4 x A4
					Měřítka	1:100
				Č. přílohy	Paré	
Zhotovitel: Valbek, spol. s r.o. Vaňurova 505/17 460 07 Liberec 3	Příloha	PODÉLNÝ ŘEZ RETENČNÍ NÁDRŽÍ			4.1	