



SO 360.5 - SFO
M 1:50


ŘEZ 3-3

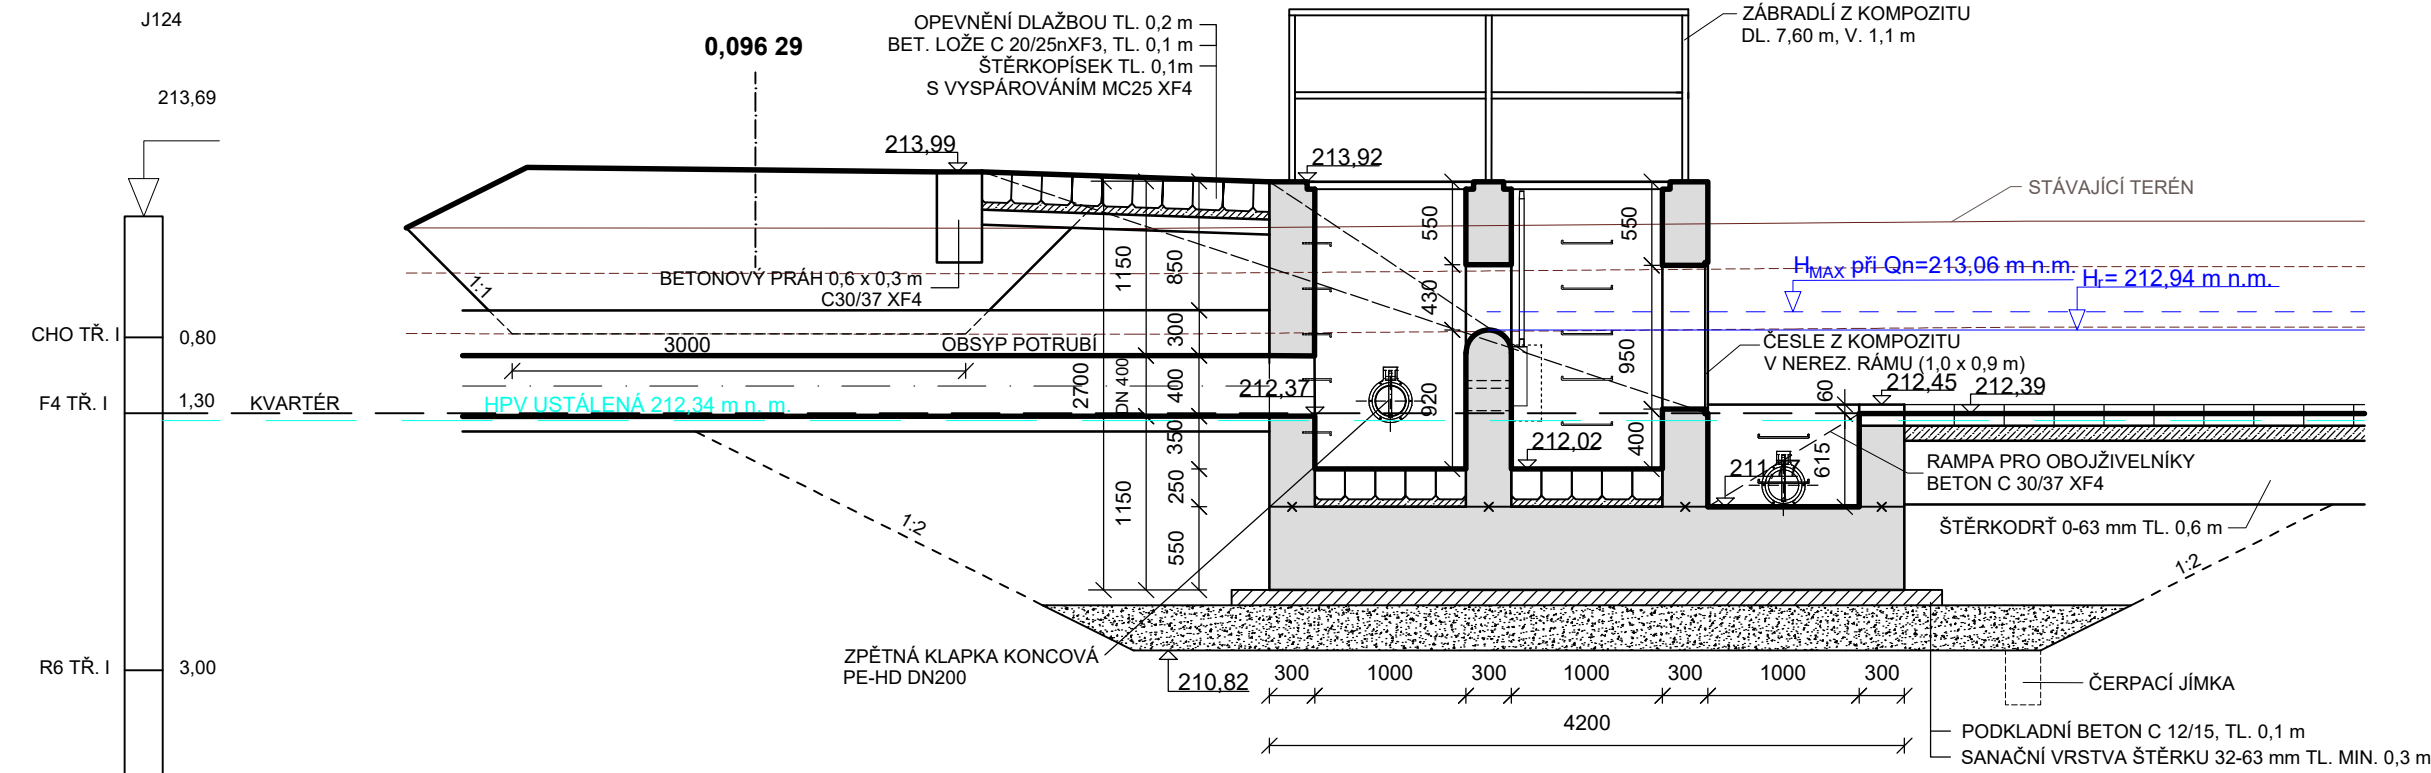


PŮDORYS

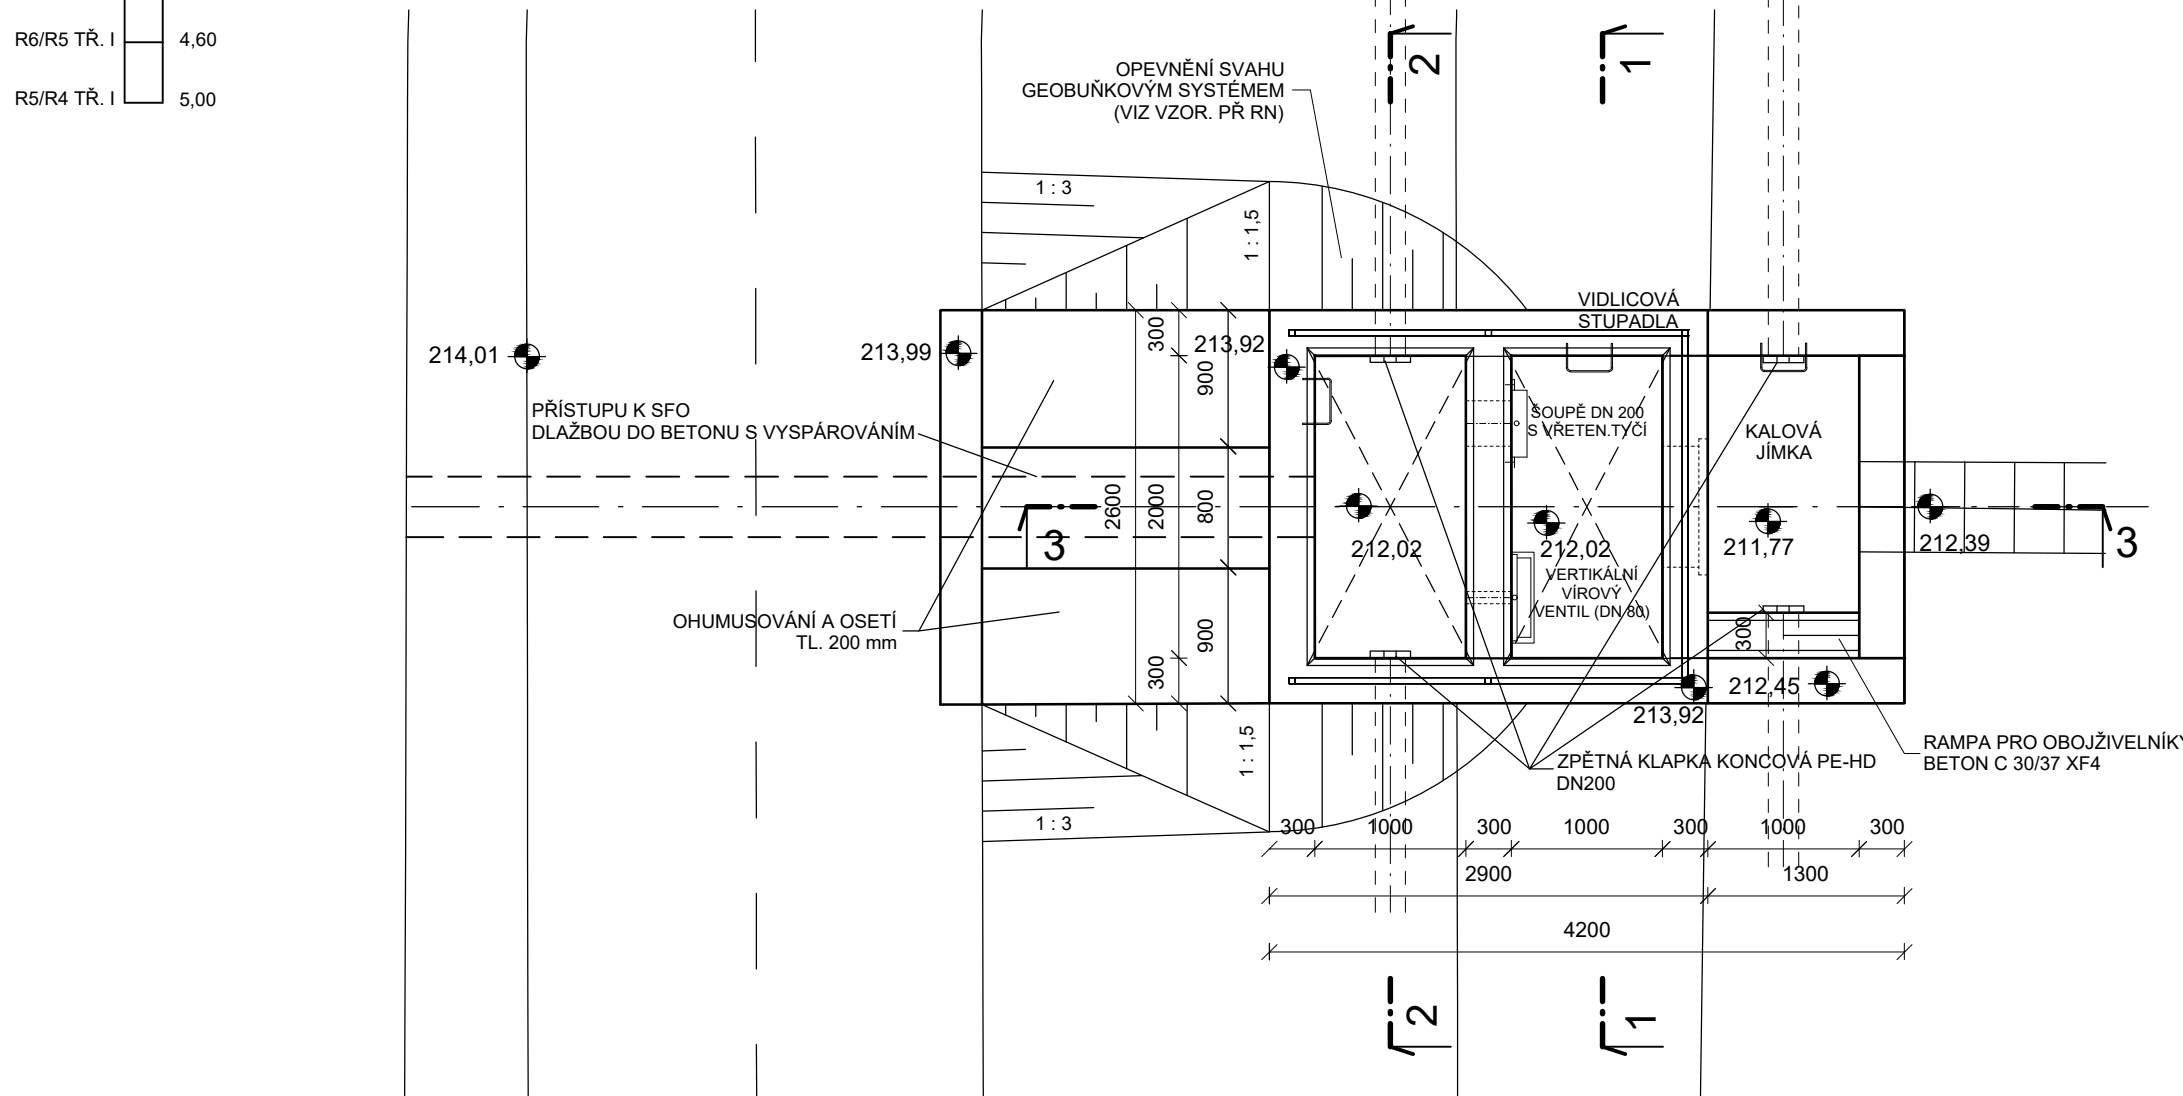

ŘEZ 2-2

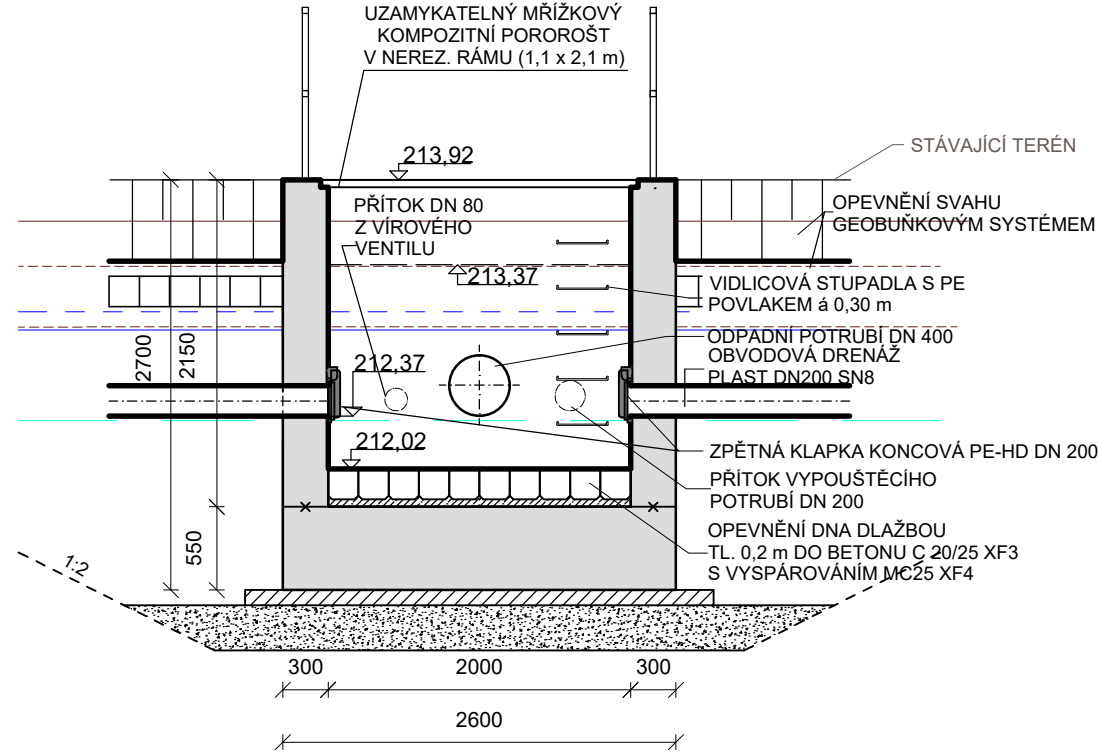

ŘEZ 1-1

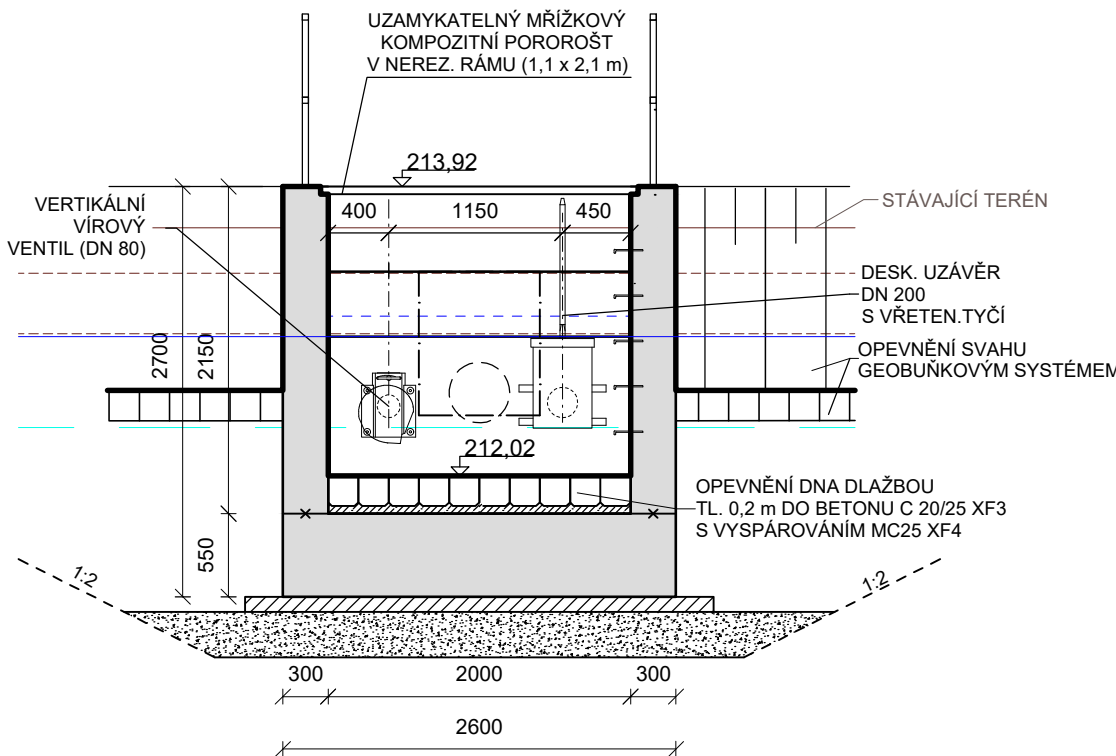

POZNÁMKA:

POŽADAVKY NA POHLEDOVÝ BETON KONSTRUKCE SFO Z HLEDISKA SMĚSI KAMENIVA, HUTNOSTI POVRCHU, BARVY, ODSTÍNU, STEJNORODOSTI A ZPŮSOBU BEDNĚNÍ DLE TKP 18
HRANY Žb KONSTRUKCE BUDOU ZKOŠENY 30/30 mm
PROSTUPY VE STĚNÁCH A PRACOVNÍ SPÁRY BUDOU TĚSNĚNY TĚSNÍCÍ PÁSKOU
PRACOVNÍ A DILATAČNÍ SPÁRY V POHLEDOVÉM BETONU ZKOŠENY DLE TKP 18
OPEVNĚNÍ PŘÍSTUPU K SFO BUDE PROVEDENO DLAŽBOU
Z LOMOVÉHO KAMENE TL. 0,2 m DO BETONU C 20/25XF3, S VYSPÁROVÁNÍM MC (XF4)
(DLAŽBA Z KAMENE viz ČSN EN 13383-1 KÁMEN PRO VODNÍ STAVBY)

Souřadnicový systém: S-JTSK

Výškový systém: Bpv

SO 360.5

DUN a retenční nádrže na I/16



ŘEDITELSTVÍ
SILNIC
A DÁLNIC

Ředitelství silnic a dálnic s. p.

Čerčanská 2023/12, Krč, 140 00 Praha 4



Valbek, spol. s r.o.

Vaňurova 505/17

460 07 Liberec 3



Zhotovitel:
Valbek, spol. s r.o.
Vaňurova 505/17
460 07 Liberec 3

Příloha
SDRUŽENÝ FUNKČNÍ OBJEKT

Vypracoval	ING. V. JURÁNEK		Zak. číslo	21-L113-001
Zodp. projektant	ING. J. VANCL		Datum	02/2025
Tech. kontrola	ING. D. LANDA		Stupeň	PDPS
Akce I/16 MLADÁ BOLESLAV - MARTINOVICE			Počet formátů	4 x A4
			Měřítko	1 : 50
			Č. přílohy	Paré
			5	
Příloha SDRUŽENÝ FUNKČNÍ OBJEKT				