


SITUACE
M 1 : 500

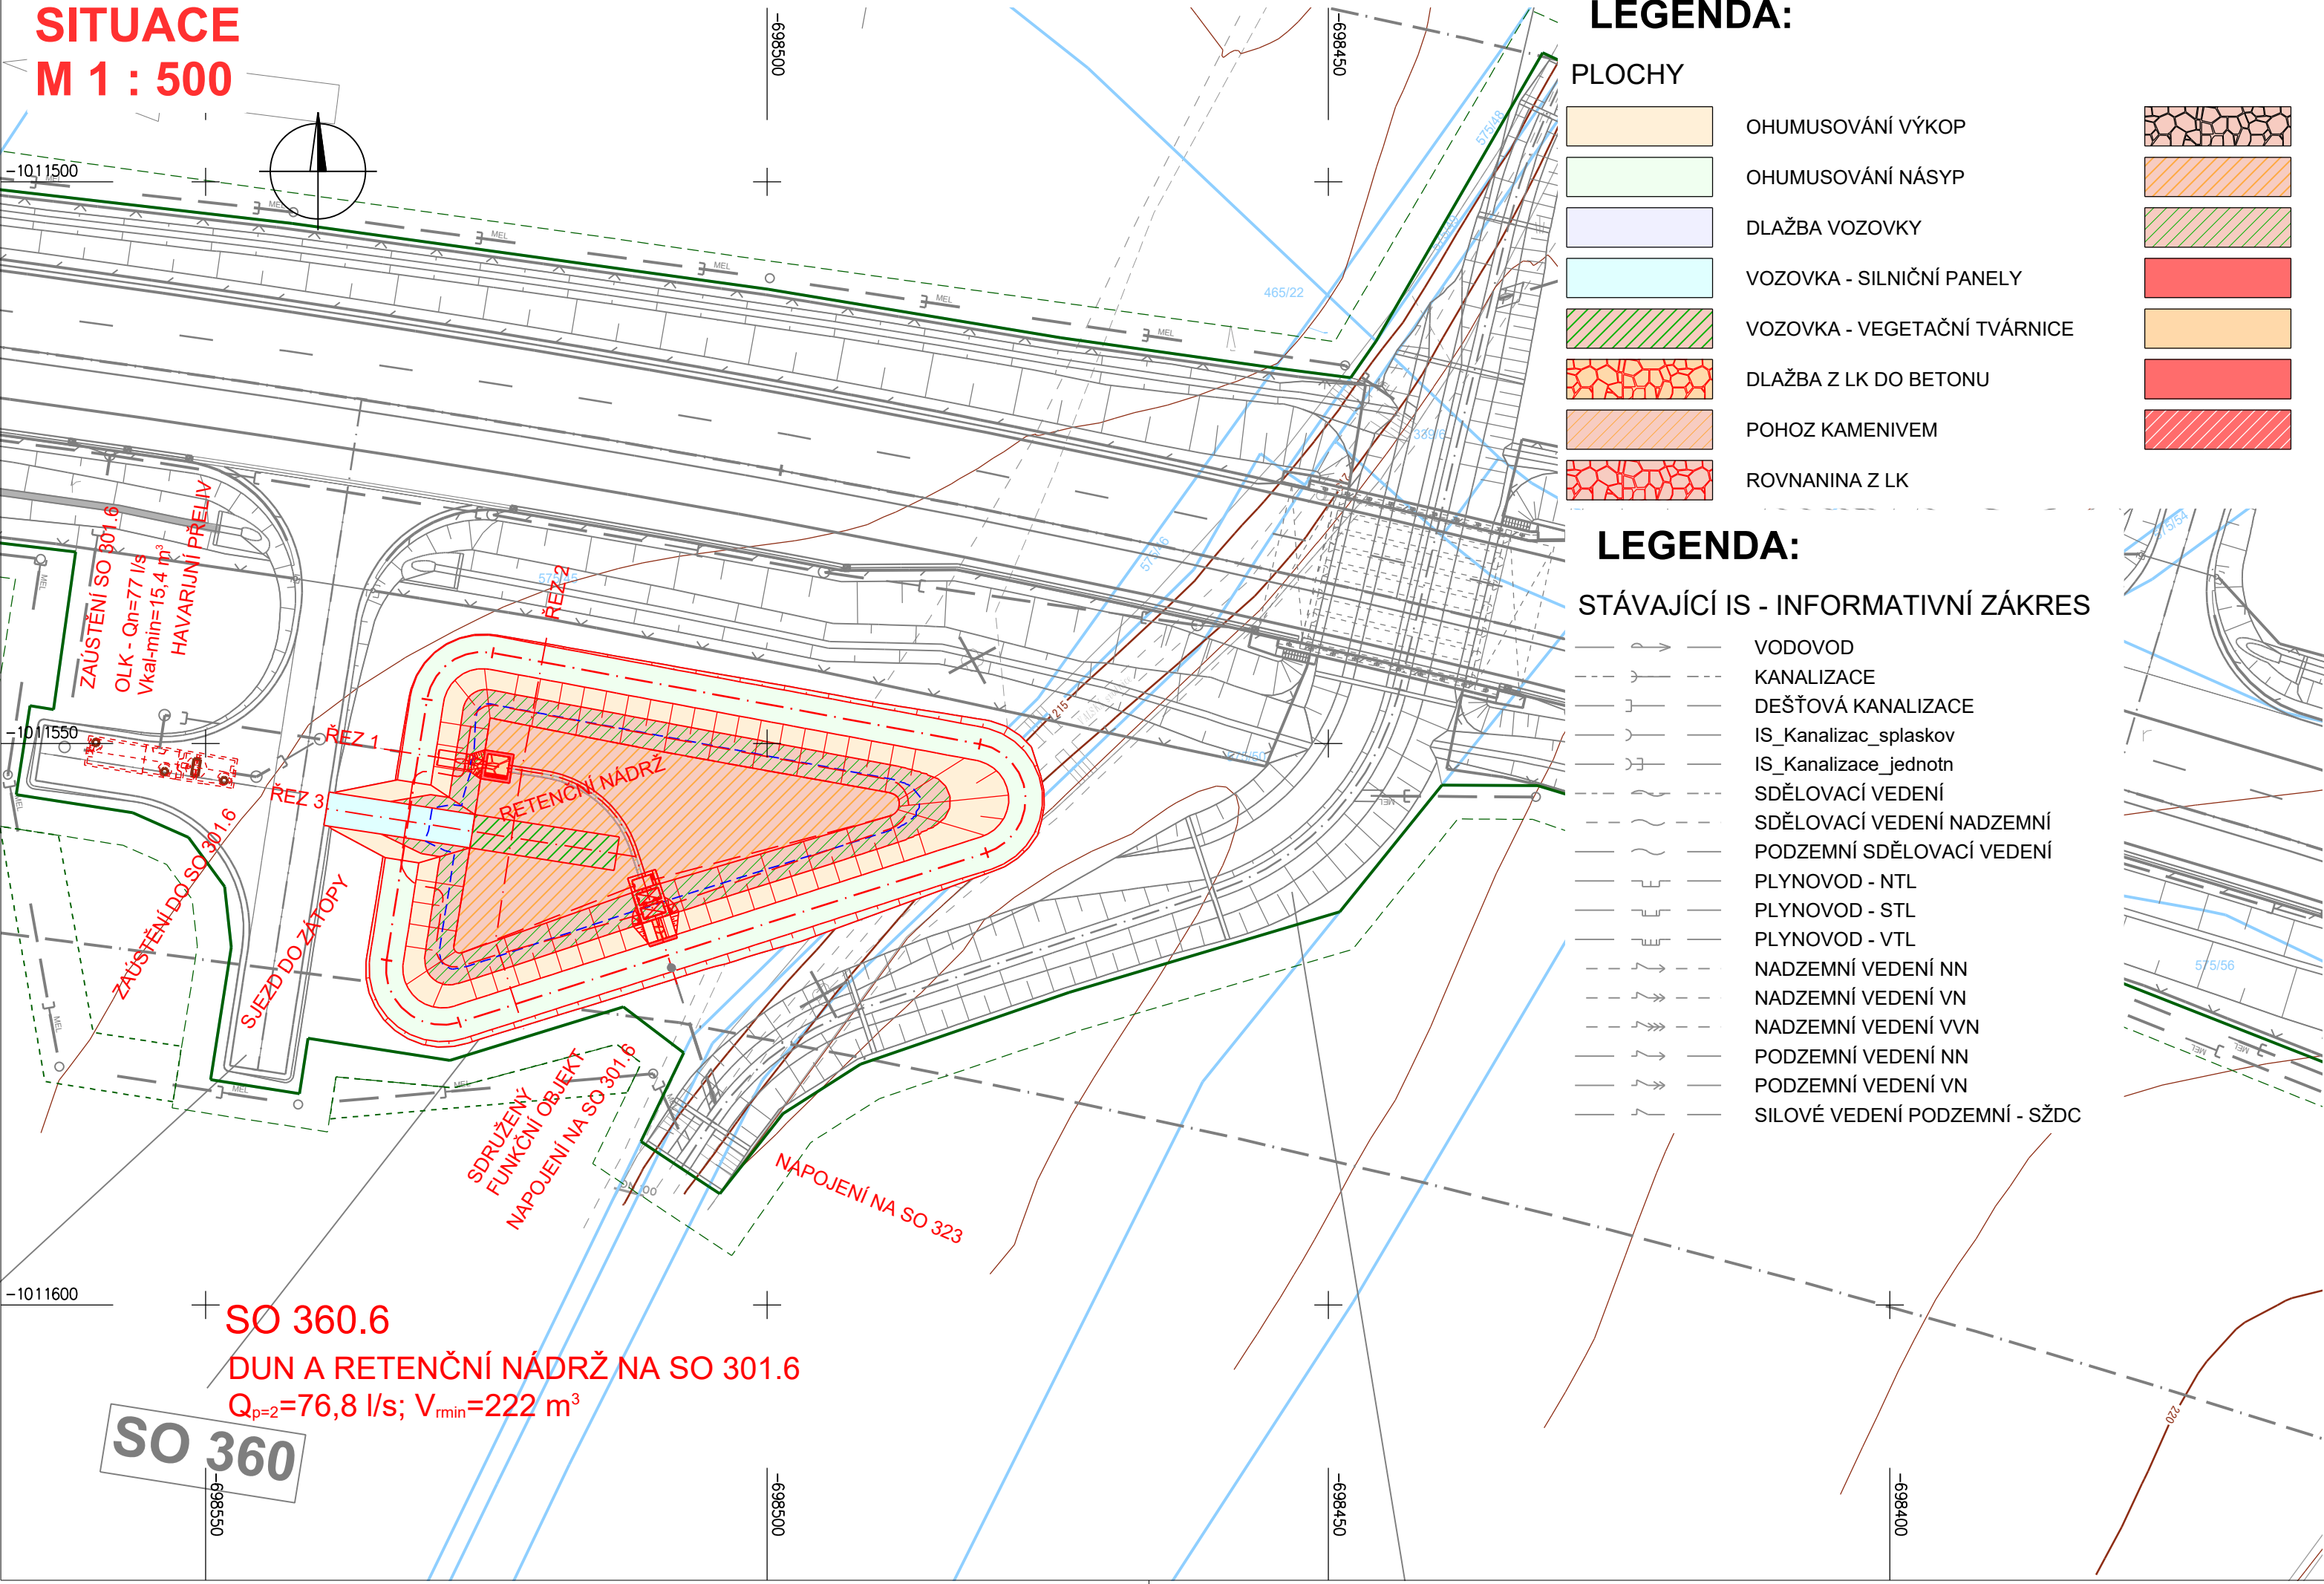

LEGENDA:

PLOCHY

- OHUMUSOVÁNÍ VÝKOP
- OHUMUSOVÁNÍ NÁSYP
- DLAŽBA VOZOVKY
- VOZOVKA - SILNIČNÍ PANELE
- VOZOVKA - VEGETAČNÍ TVÁRNICE
- DLAŽBA Z LK DO BETONU
- POHOZ KAMENIVEM
- ROVNaNINA Z LK

- ROVNaNINA Z LK S OHUMUSOVÁNÍM
- PLOCHY ZE ŠD
- GEOBUŇKOVÝ SYSTÉM
- PRÁH BETONOVÝ
- PRÁH Z LK NA CM
- BETONOVÉ KONSTRUKCE
- ŽB KONSTRUKCE


KATASTR NEMOVITOSTÍ

- HRANICE K.Ú.
- HRANICE PARCEL
- TRVALÝ ZÁBOR
- HRANICE DOČASNÉHO ZÁBORU NAD 1 ROK
- DOČASNÝ ZÁBOR DO 1 ROKU

LEGENDA:

STÁVAJÍCÍ IS - INFORMATIVNÍ ZÁKRES

- VODOVOD
- KANALIZACE
- DEŠŤOVÁ KANALIZACE
- IS_Kanalizac_splaskov
- IS_Kanalizace_jednotn
- SDĚLOVACÍ VEDENÍ
- SDĚLOVACÍ VEDENÍ NADZEMNÍ
- PODZEMNÍ SDĚLOVACÍ VEDENÍ
- PLYNOVOD - NTL
- PLYNOVOD - STL
- PLYNOVOD - VTL
- NADZEMNÍ VEDENÍ NN
- NADZEMNÍ VEDENÍ VN
- NADZEMNÍ VEDENÍ VVN
- PODZEMNÍ VEDENÍ NN
- PODZEMNÍ VEDENÍ VN
- SILOVÉ VEDENÍ PODZEMNÍ - SŽDC

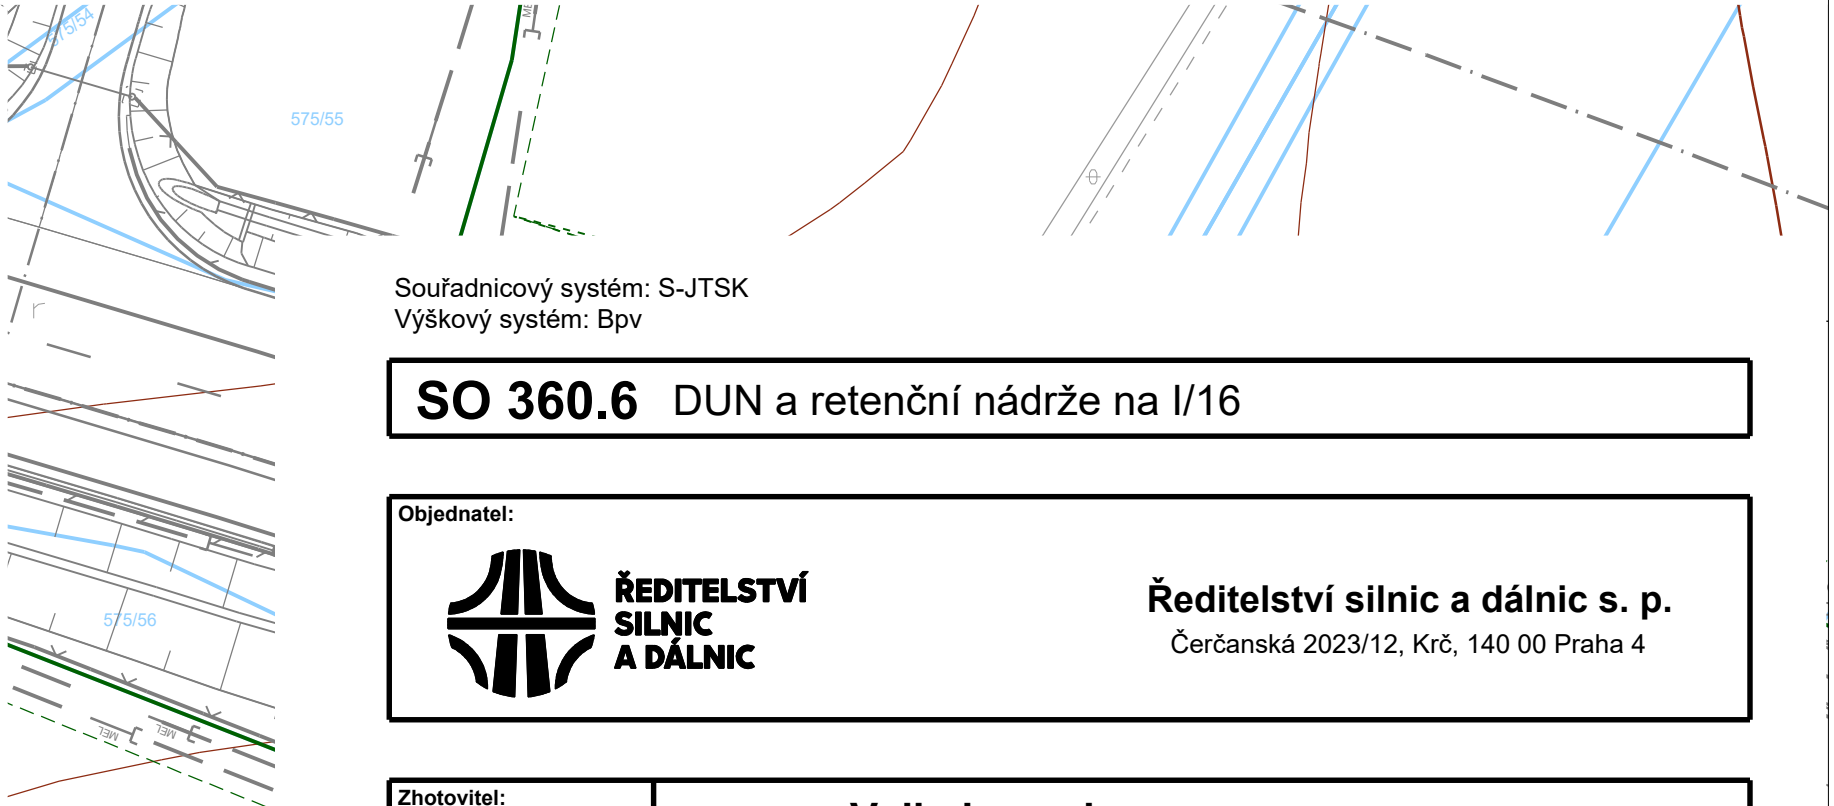

SO 360.6 DUN a retenční nádrže na I/16

Objednatel:



Ředitelství silnic a dálnic s. p.
Čerčanská 2023/12, Krč, 140 00 Praha 4

Zhotovitel:



Valbek, spol. s r.o.
Vaňurova 505/17
460 07 Liberec 3



Vypracoval	ING. J. VANCL		Zak. číslo	21-LI13-001
Zodp. projektant	ING. J. VANCL		Datum	02/2025
Tech. kontrola	ING. D. LANDA		Stupeň	PDPS
Akce			Počet formátů	3 x A4
I/16 MLADÁ BOLESLAV - MARTINOVICE			Měřítko	1 : 500
			Č. přílohy	Paré
Příloha			1	

Zhotovitel:
Valbek, spol. s r.o.
Vaňurova 505/17
460 07 Liberec 3

SITUACE