


PODÉLNÝ PROFIL HRÁZÍ RETENČNÍ NÁDRŽE


M 1 : 500

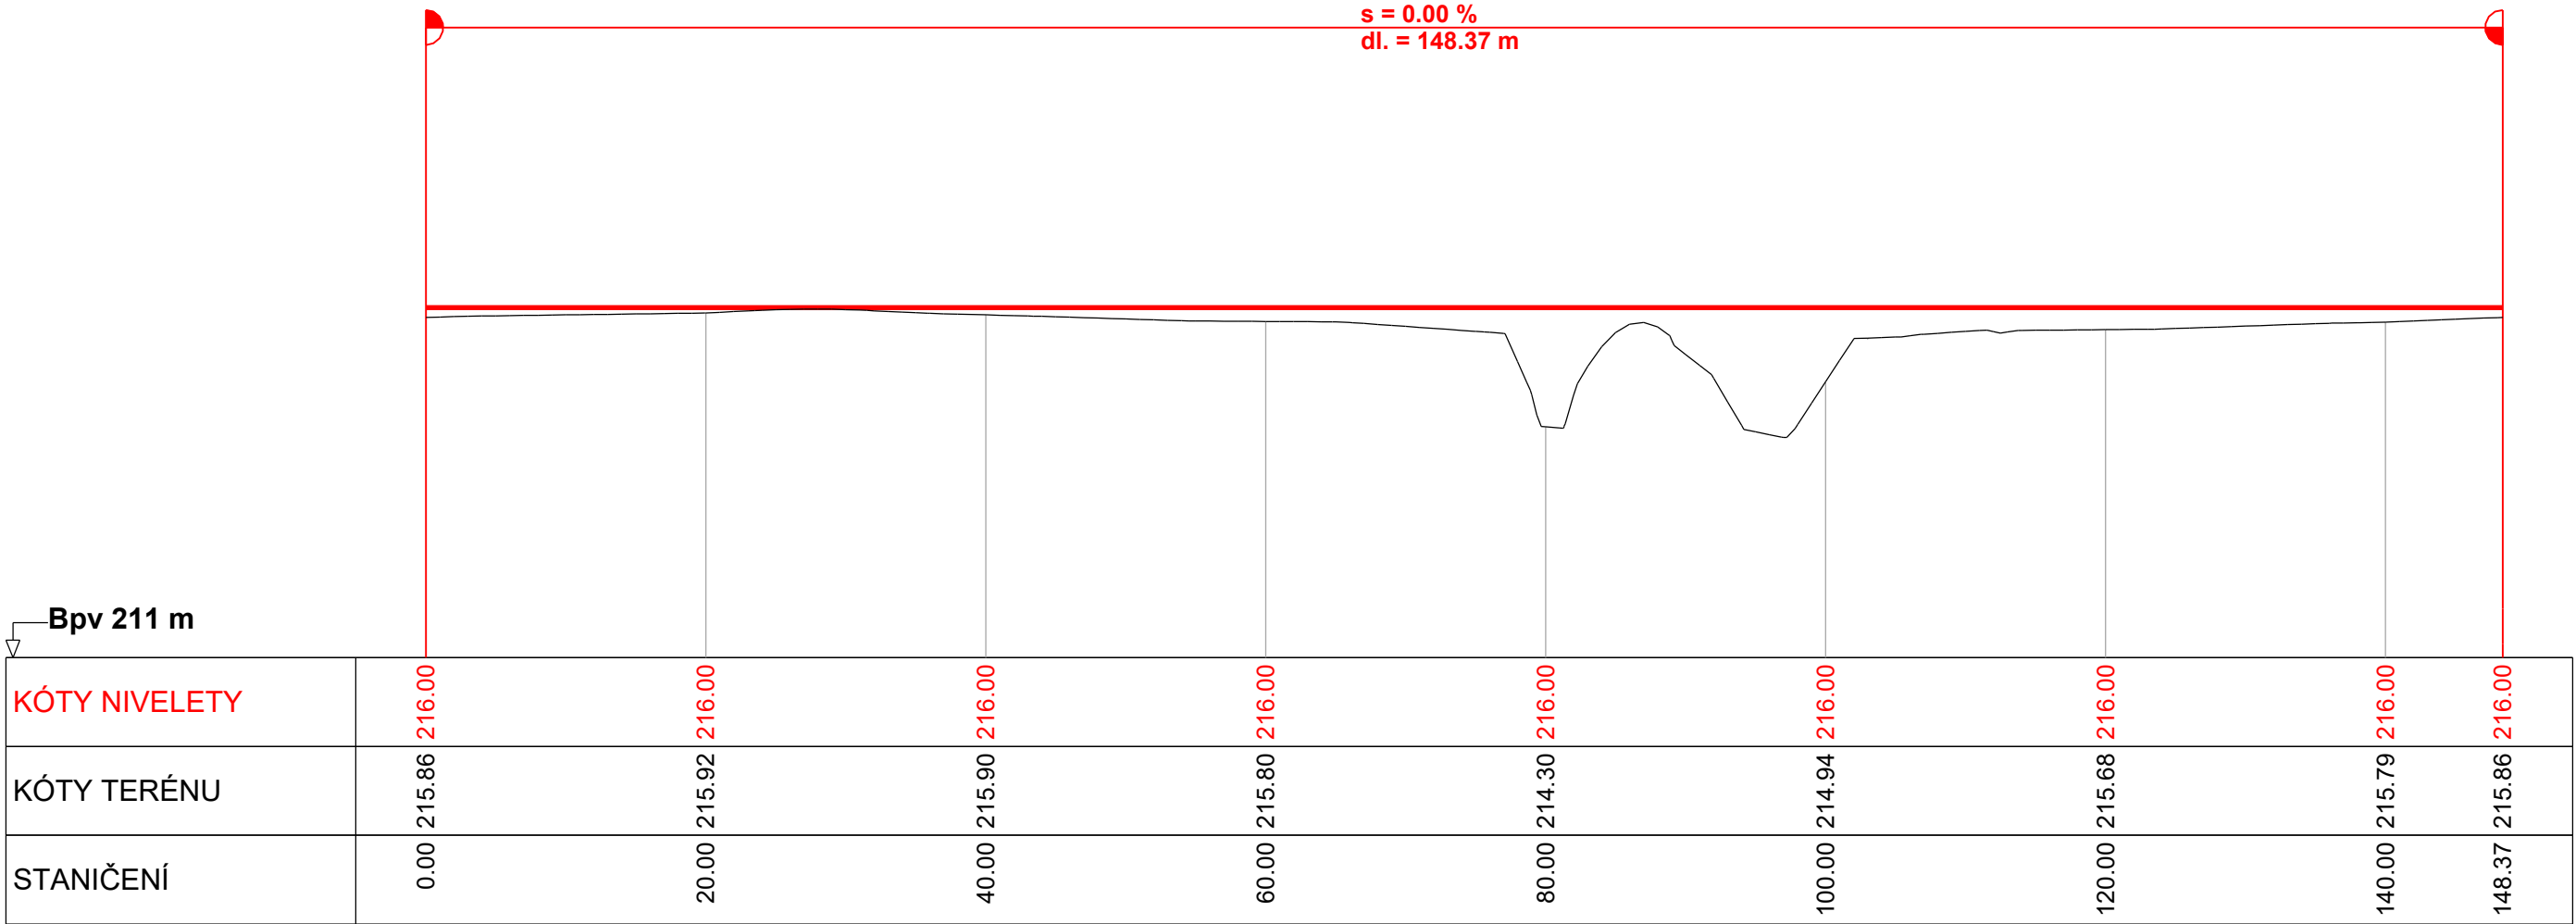

Bpv 211 m

km 0+000 0+100

VPRAVO
SMĚROVÉ POMĚRY
MĚŘÍTKO 5/R (cm)
VLEVO

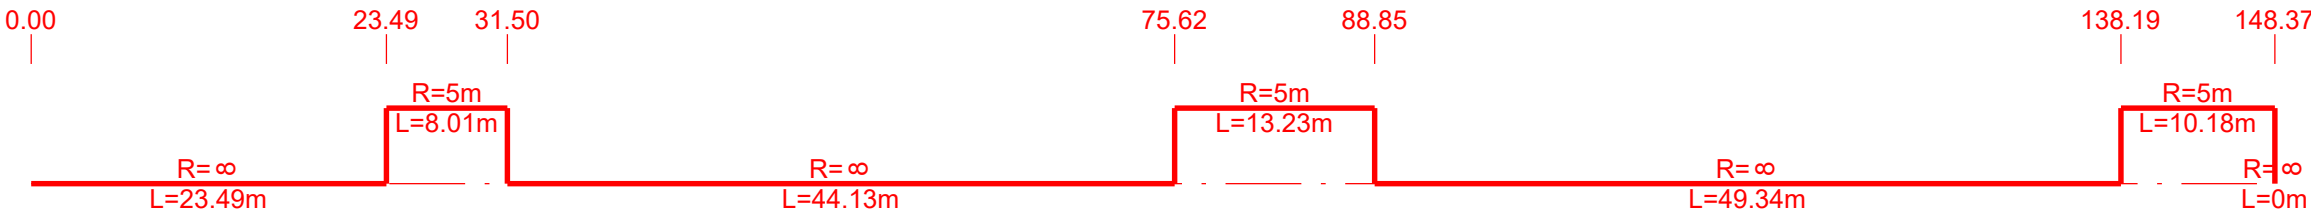

Souřadnicový systém: S-JTSK
Výškový systém: Bpv

SO 360.6 DUN a retenční nádrže na I/16

Objednatel:



ŘEDITELSTVÍ
SILNIC
A DÁLNIC

Ředitelství silnic a dálnic s. p.
Čerčanská 2023/12, Krč, 140 00 Praha 4

Zhotovitel:



Valbek, spol. s r.o.
Vaňurova 505/17
460 07 Liberec 3



Vypracoval	ING. J. VANCL	
Zodp. projektant	ING. J. VANCL	
Tech. kontrola	ING. D. LANDA	

Akce
I/16 MLADÁ BOLESLAV - MARTINOVICE

Zhotovitel:
Valbek, spol. s r.o.
Vaňurova 505/17
460 07 Liberec 3

Příloha
PODÉLNÝ PROFIL HRÁZÍ RETENČNÍ NÁDRŽE

Zak. číslo	21-LI13-001
Datum	02/2025
Stupeň	PDPS
Počet formátů	3 x A4
Měřítko	1 : 500/100
Č. přílohy	Paré
3	