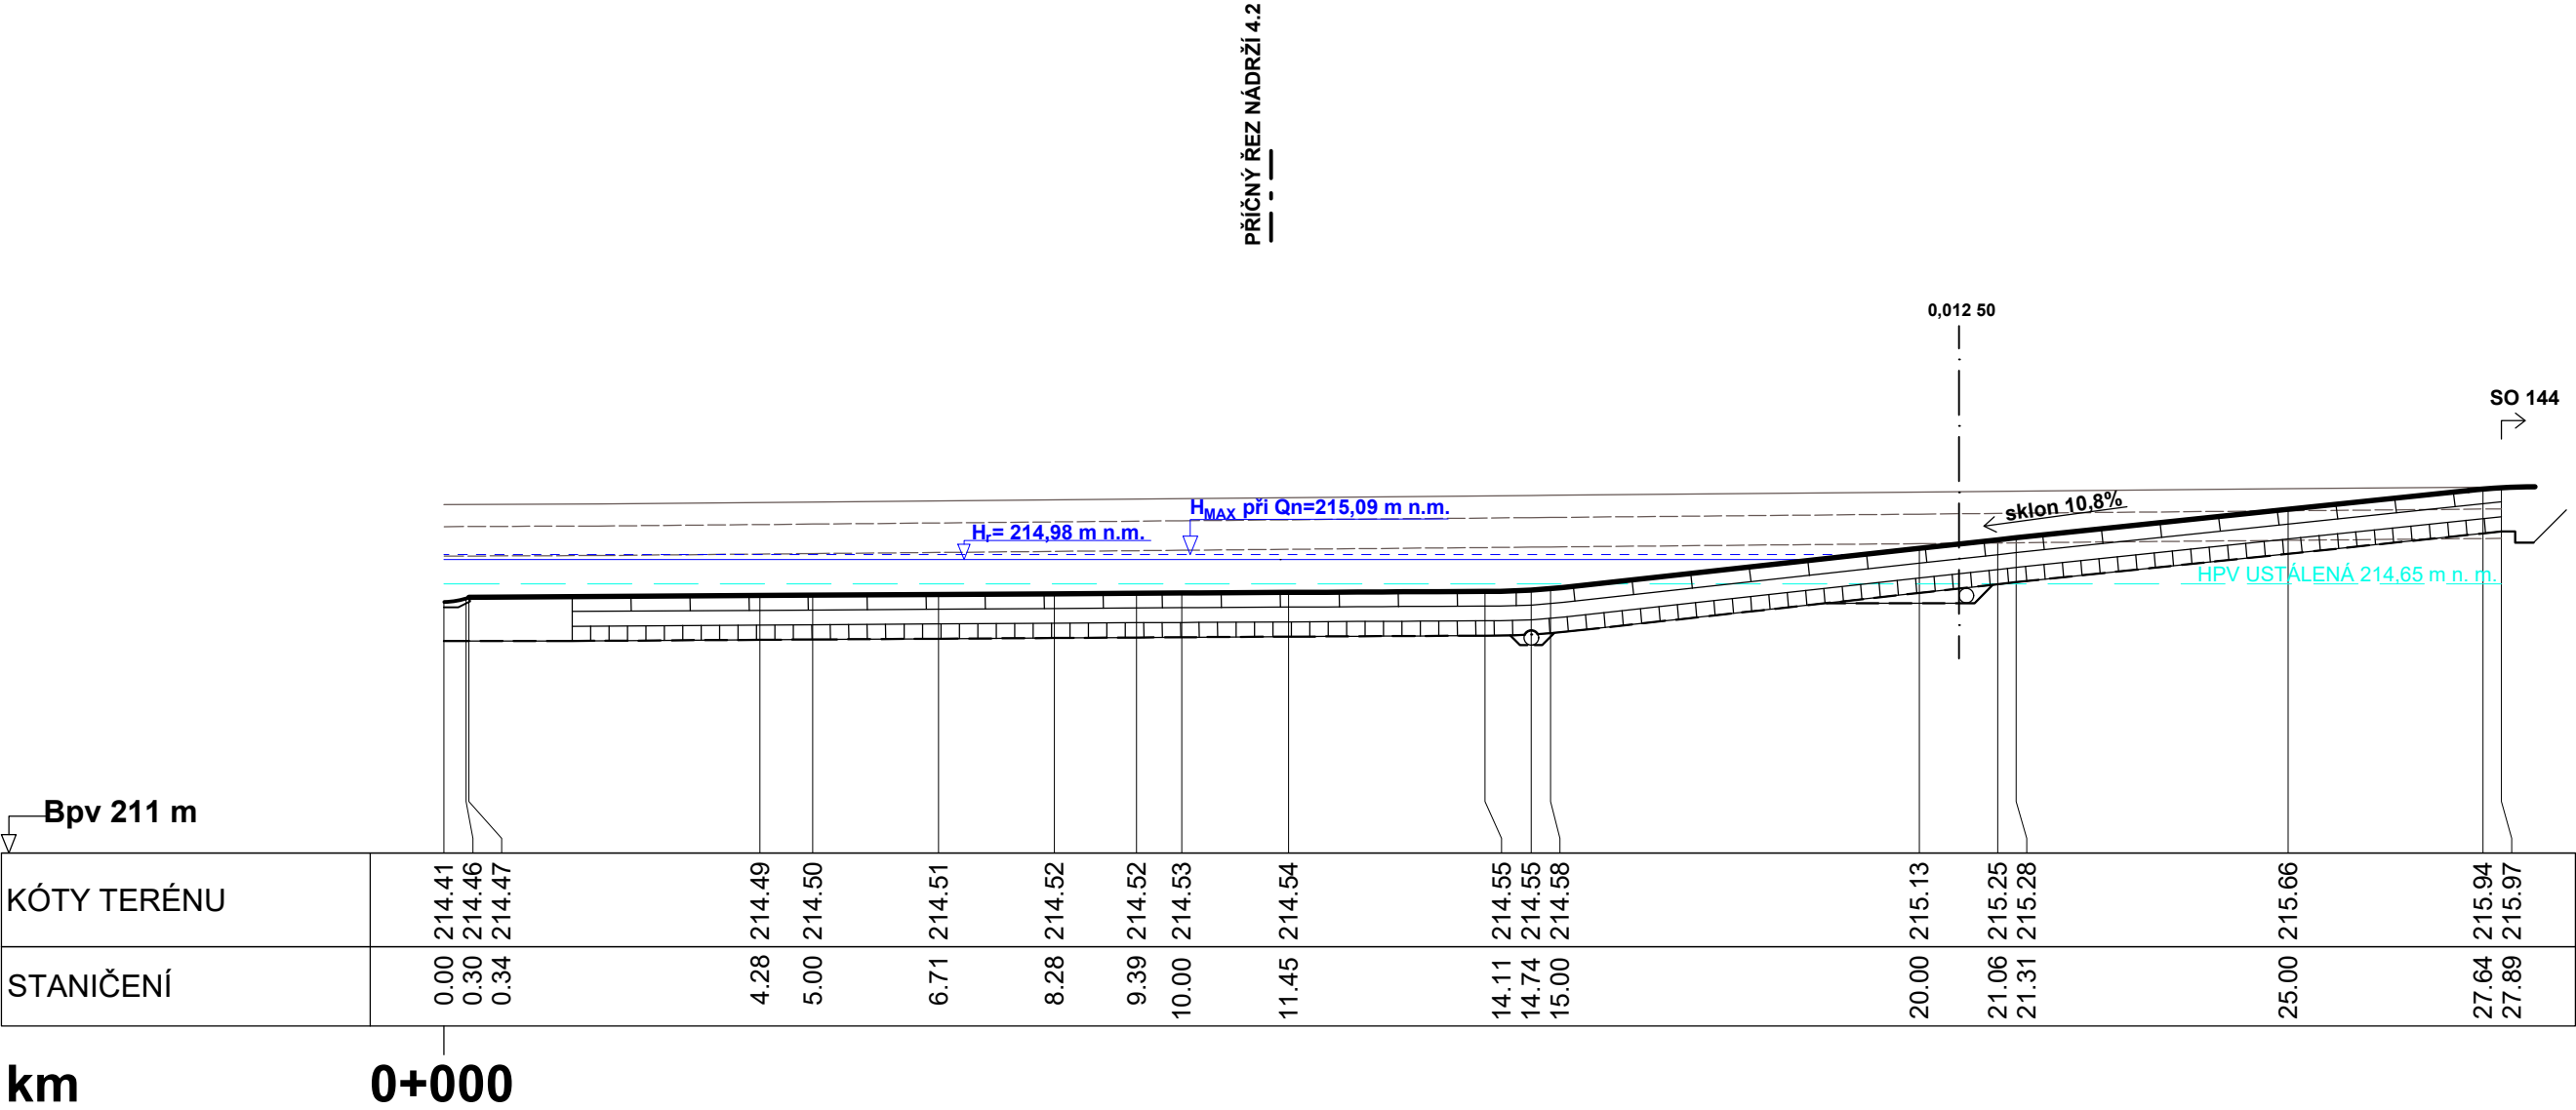


PODÉLNÝ ŘEZ SJEZDEM DO NÁDRŽE
M 1:100



Souřadnicový systém: S-JTSK
Výškový systém: Bpv

SO 360.6 DUN a retenční nádrže na I/16

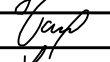
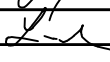
Objednatel:



Ředitelství silnic a dálnic s. p.
Čerčanská 2023/12, Krč, 140 00 Praha 4



Valbek, spol. s r.o.
Vaňurova 505/17
460 07 Liberec 3

	Vypracoval	ING. V. JURÁNEK		Zak. číslo	21-LI13-001
	Zodp. projektant	ING. J. VANCL		Datum	02/2025
	Tech. kontrola	ING. D. LANDA		Stupeň	PDPS
	Akce I/16 MLADÁ BOLESLAV - MARTINOVICE			Počet formátů	3 x A4
				Měřítko	1 : 100
Č. přílohy				Paré	
Zhotovitel: Valbek, spol. s r.o. Vaňurova 505/17 460 07 Liberec 3				4.3	
Příloha PODÉLNÝ ŘEZ SJEZDEM DO NÁDRŽE					