

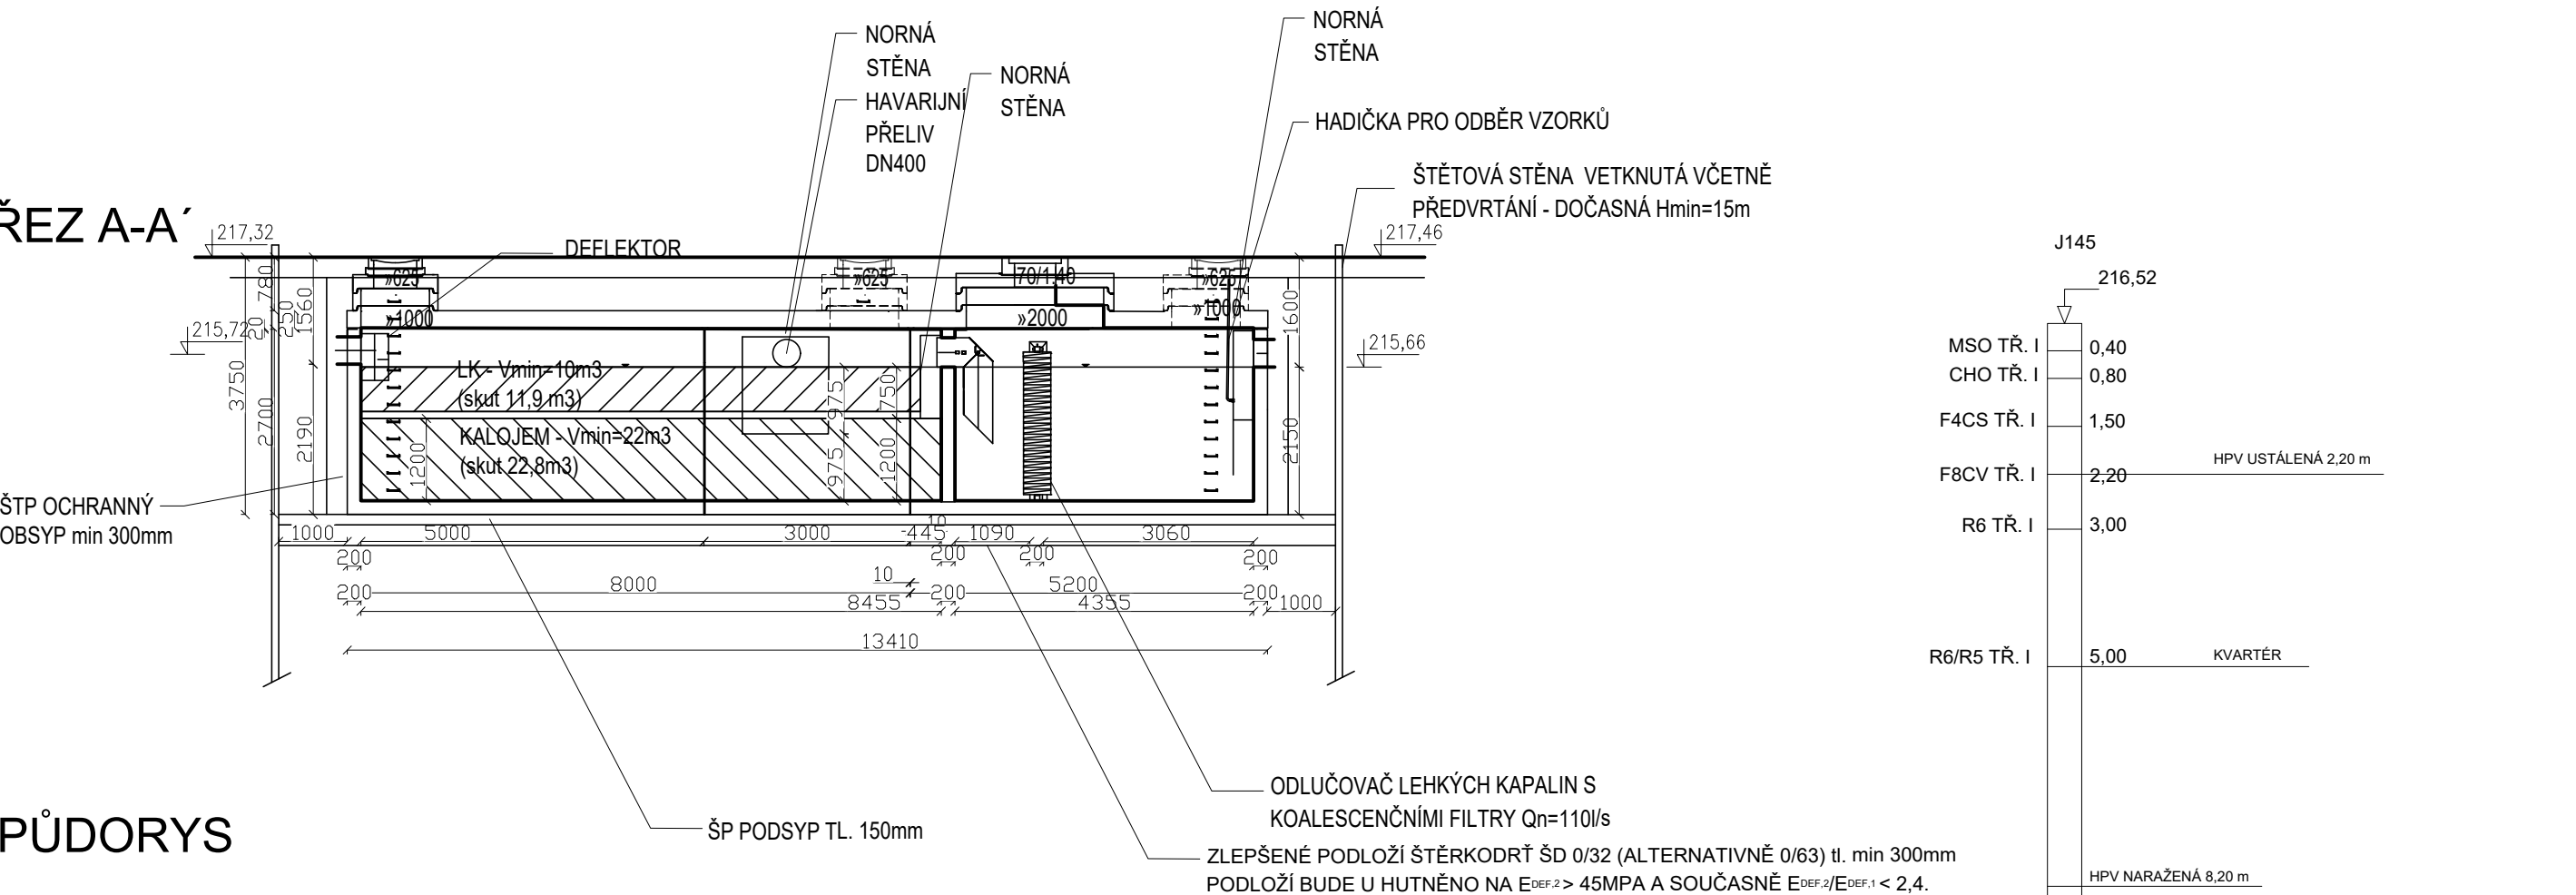


SO 360.7 DISPOZIČNÍ VÝKRES OLK  
M 1:100

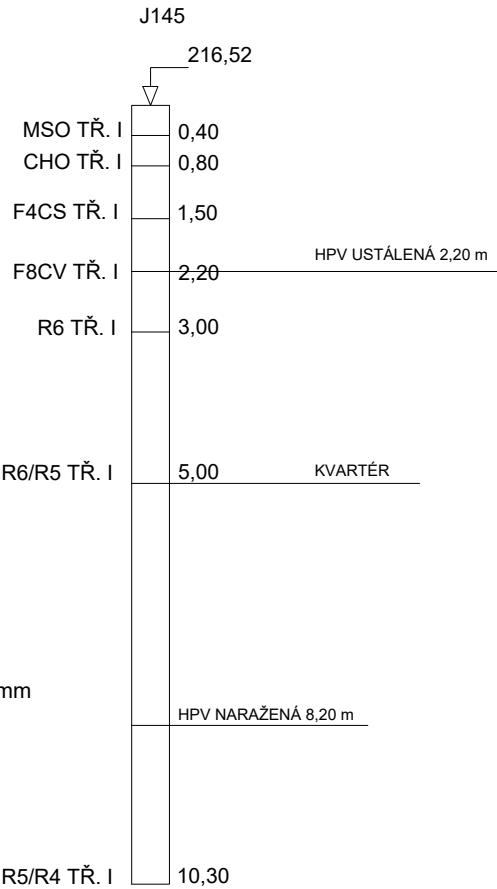

PŮDORYS

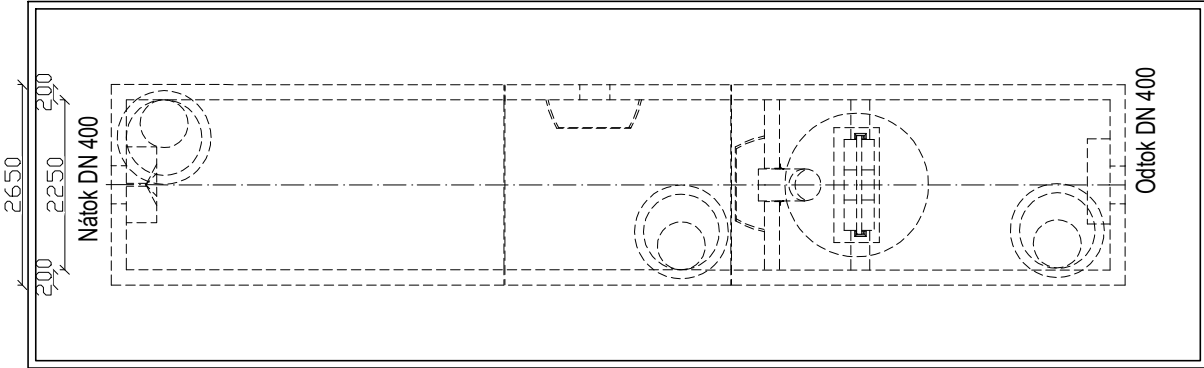

POZN.

- TVAR NÁDRŽE BUDE UPŘESNĚN V DALŠÍM STUPNI PD DLE KONKRÉTNÍHO DODAVATELE NA ZÁKLADĚ VTD BUDE UPŘESNĚN ZPŮSOB ZALOŽENÍ POMOCÍ ŠTĚTOVNIC
- NÁDRŽE BUDOU VYBAVENY VÝSTUPY PRO OBOJŽIVELNÍKY
- DUN JE NAVRŽENA S VODOTĚSNÝMI SYSTÉMEM SEŠROUBOVÁNÍM PŘES TĚSNĚNÍ, ŠACHTOVÉ NÁSTAVBY POUŽÍVAJÍ STANDARDNÍ JAZÝČKOVÉ TĚSNĚNÍ. NA STROPNÍ DESCE NÁDRŽE BUDOU ZABETONOVÁNY PROFILY SPOJE PRO TOTO TĚSNĚNÍ.
- DO KAŽDÉ ČÁSTI DUN MUSÍ BÝT UMOŽNĚN VSTUP PŘES VSTUPNÍ KOMÍN (STUPADLA / ŽEBŘÍK)
- VE DNĚ BUDE ZŘÍZENÁ ČERPAČÍ JÍMKA PRO ČERPÁNÍ PŘÍPADNÉ PRŮSAKOVÉ VODY
- VNĚJŠÍ POVRCH STROPU OPATŘEN PENETRAČNÍM ASFALTOVÝM NÁTĚREM, SPOJE STROPNÍCH DÍLŮ NÁSLEDNĚ PŘEKRYT NATAVITELNÝMI ASFALTOVÝMI PÁSY

Souřadnicový systém: S-JTSK  
Výškový systém: Bpv

SO 360.7 DUN a retenční nádrže na I/16

Objednatel:



**ŘEDITELSTVÍ  
SILNIC  
A DÁLNIC**

**Ředitelství silnic a dálnic s. p.**

Čerčanská 2023/12, Krč, 140 00 Praha 4

Zhotovitel:



**Valbek, spol. s r.o.**

Vaňurova 505/17  
460 07 Liberec 3

|                                                                                       |                                      |               |                                                                                       |               |             |
|---------------------------------------------------------------------------------------|--------------------------------------|---------------|---------------------------------------------------------------------------------------|---------------|-------------|
|  | Vypracoval                           | ING. J. VANCL |  | Zak. číslo    | 21-LI13-001 |
|                                                                                       | Zodp. projektant                     | ING. J. VANCL |                                                                                       | Datum         | 02/2025     |
|                                                                                       | Tech. kontrola                       | ING. D. LANDA |                                                                                       | Stupeň        | PDPS        |
|                                                                                       | Akce                                 |               |                                                                                       | Počet formátů | 3 x A4      |
|                                                                                       | I/16 MLADÁ BOLESLAV - MARTINOVICE    |               |                                                                                       | Měřítko       | 1 : 100     |
| Zhotovitel:<br>Valbek, spol. s r.o.<br>Vaňurova 505/17<br>460 07 Liberec 3            | Příloha<br><br>DISPOZIČNÍ VÝKRES OLK |               |                                                                                       | Č. přílohy    | Paré        |
|                                                                                       |                                      |               |                                                                                       | 2             |             |