

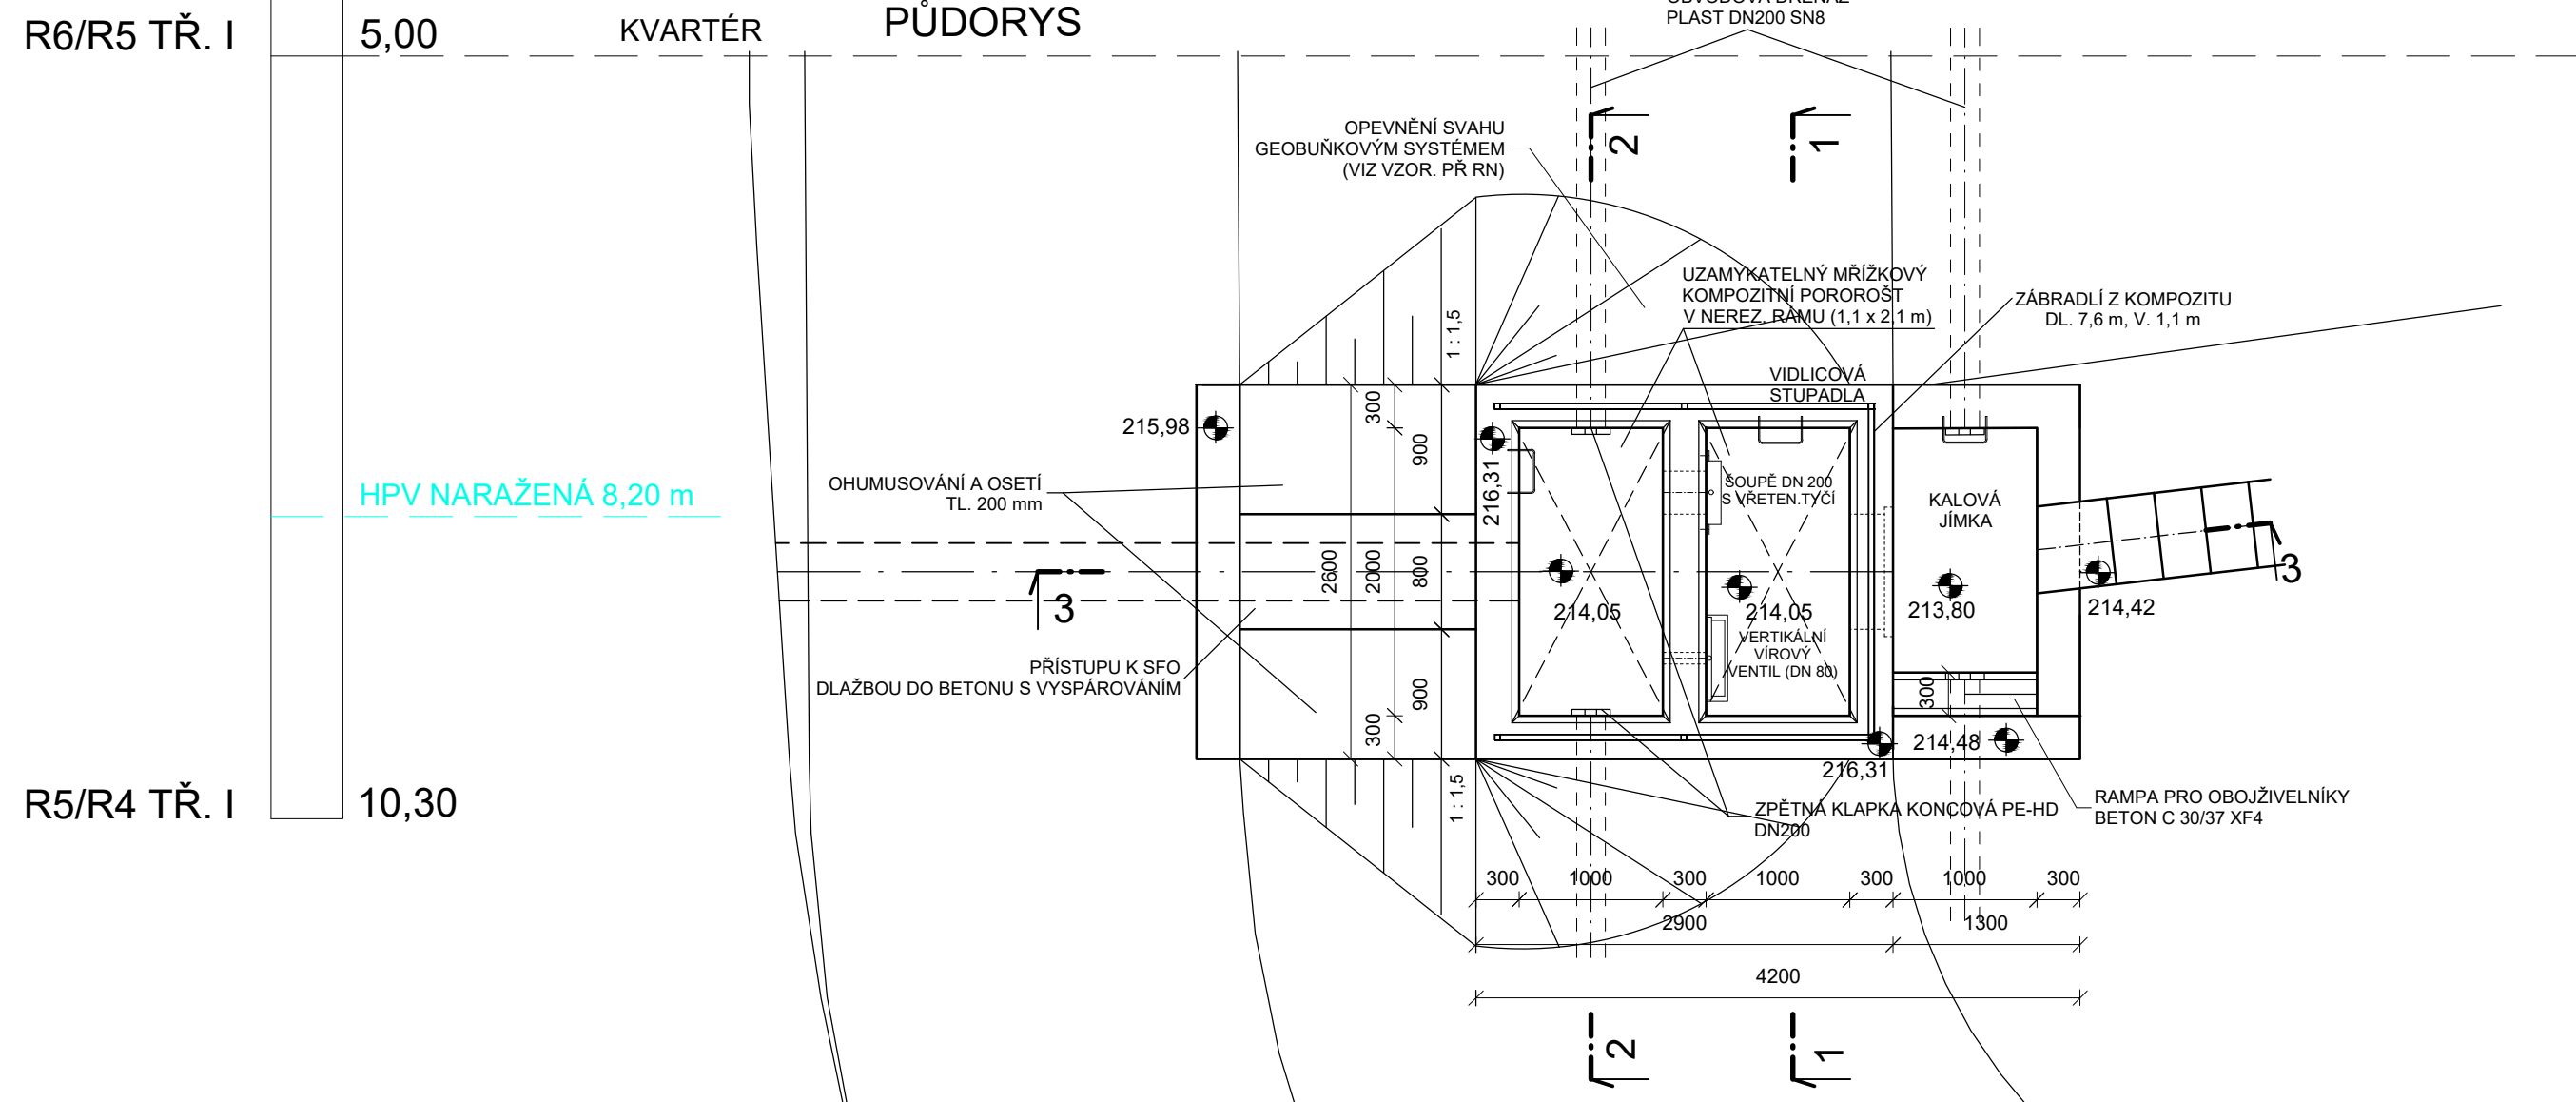


J145 ŘEZ 3-3

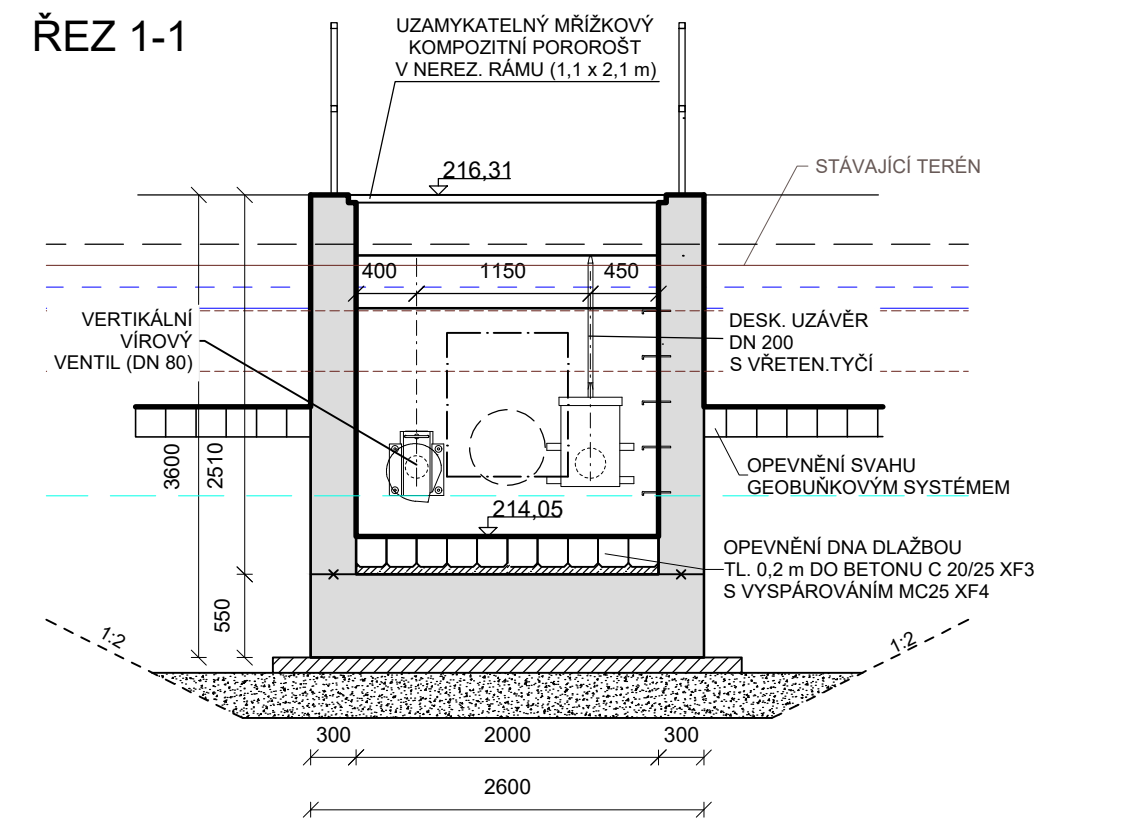

ŘEZ 1-1

 

	Vypracoval	ING. V. JURÁNEK		Zak. číslo	21-L113-001	
	Zodp. projektant	ING. J. VANCL			Datum	02/2025
	Tech. kontrola	ING. D. LANDA				Stupeň
	Akce I/16 MLADÁ BOLESLAV - MARTINOVICE			Počet formátů		4 x A4
Zhotovitel: Valbek, spol. s r.o. Vaňurova 505/17 460 07 Liberec 3	Příloha SDRUŽENÝ FUNKČNÍ OBJEKT			Měřítko	1 : 50	
				Č. přílohy	Paré	
				5		