


PODÉLNÝ ŘEZ SJEZDEM DO NÁDRŽE
M 1:100

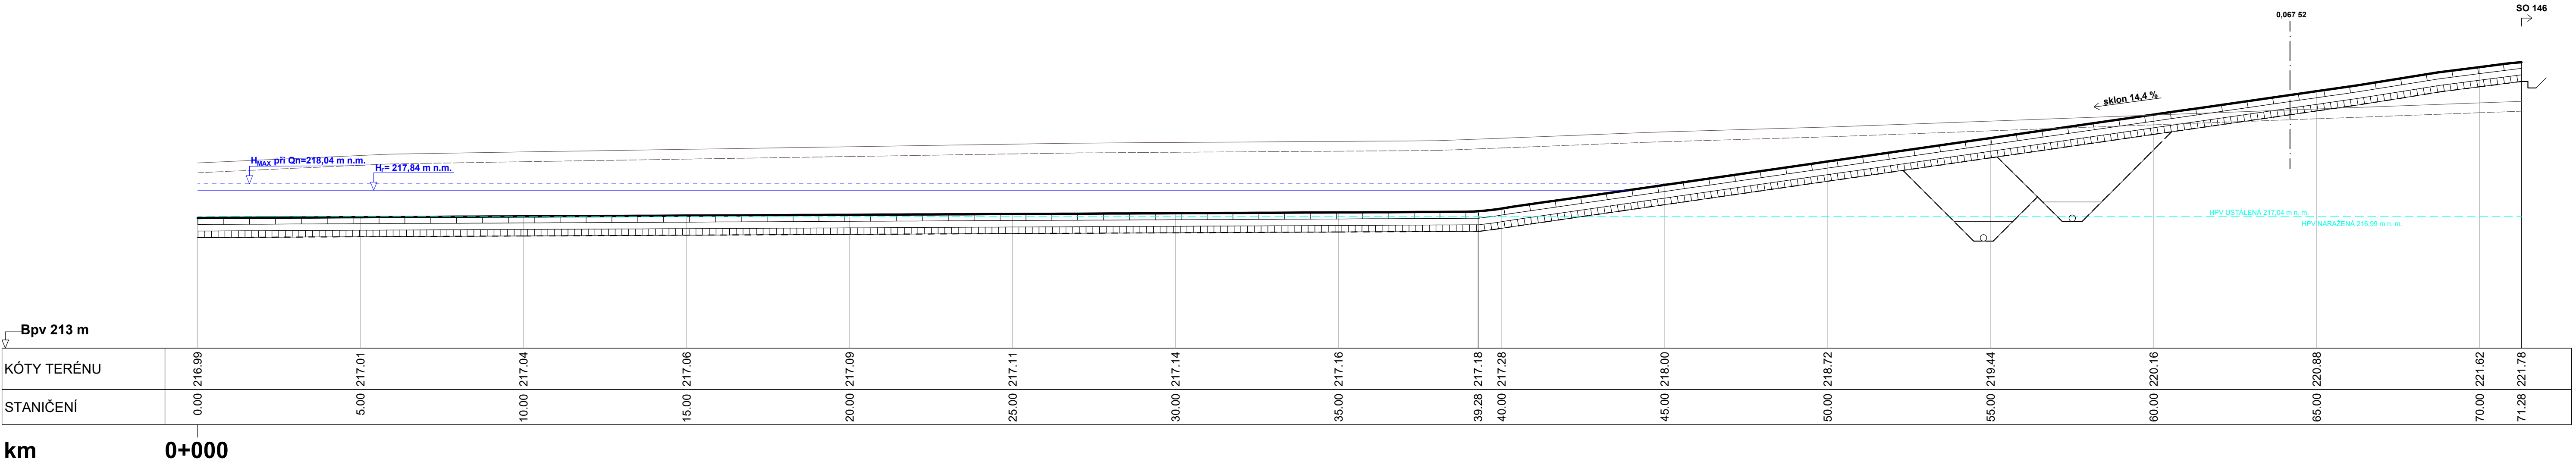

Souřadnicový systém: S-JTSK
Výškový systém: Bpv

SO 360.8 DUN a retenční nádrže na I/16

Objednatel:



**ŘEDITELSTVÍ
SILNIC
A DÁLNIC**

Ředitelství silnic a dálnic s. p.
Čerčanská 2023/12, Krč, 140 00 Praha 4



Valbek, spol. s r.o.
Vaňurova 505/17
460 07 Liberec 3

	Vypracoval	ING. V. JURÁNEK		Zak. číslo	21-L113-001
	Zodp. projektant	ING. J. VANCL		Datum	02/2025
	Tech. kontrola	ING. D. LANDA		Stupeň	PDPS
	Akce I/16 MLADÁ BOLESLAV - MARTINOVICE			Počet formátů	4 x A4
				Měřítko	1 : 100
Zhotovitel: Valbek, spol. s r.o. Vaňurova 505/17 460 07 Liberec 3	Příloha PODÉLNÝ ŘEZ SJEZDEM DO NÁDRŽE			Č. přílohy	Paré
				4.3	