


PODÉLNÝ ŘEZ SJEZDEM DO NÁDRŽE
M 1:100

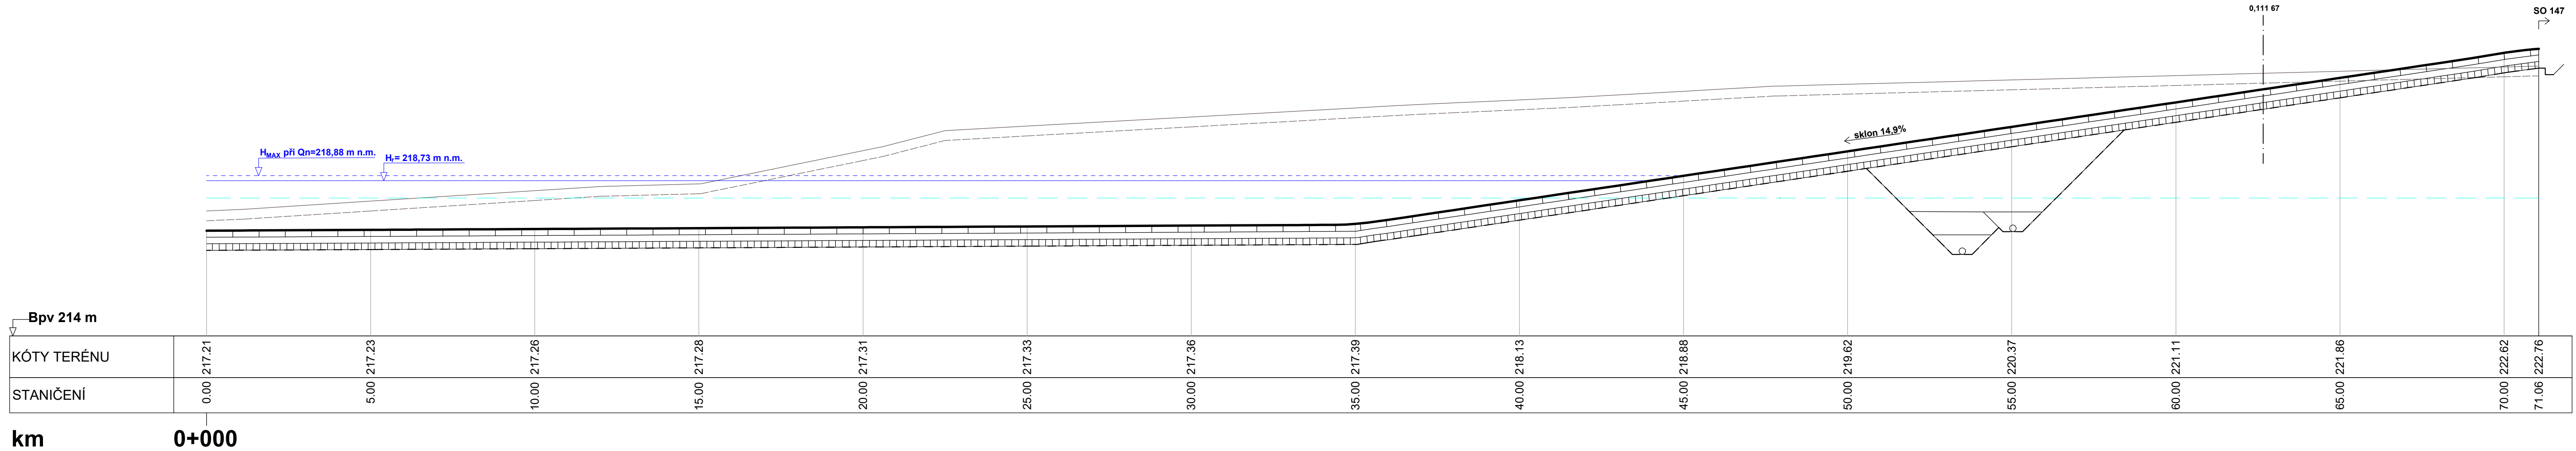


Souřadnicový systém: S-JTSK
Výškový systém: Bpv

SO 360.9

DUN a retenční nádrže na I/16

Objednatel:

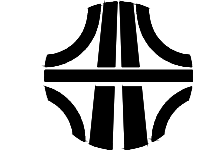

ŘEDITELSTV
SILNIC
A DÁLNIC

Ředitelství silnic a dálnic s. p.
Čerčanská 2023/12, Krč, 140 00 Praha 4



Valbek, spol. s r.o.
Vaňurova 505/17
460 07 Liberec 3



Zhotovitel:
Valbek, spol. s r.o.
Vaňurova 505/17
460 07 Liberec 3


Příloha

PODÉLNÝ ŘEZ SJEZDEM DO NÁDRŽE

Vypracoval
ING. V. JURÁNEK

Zodp. projektant
ING. J. VANCL

Tech. kontrola
ING. D. LANDA

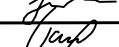



Zak. číslo

21-L113-001

Datum

02/2025

Stupeň

PDPS

Počet formátů

4 x A4

Měřítko

1 : 100

Č. přílohy

Paré

4.3