
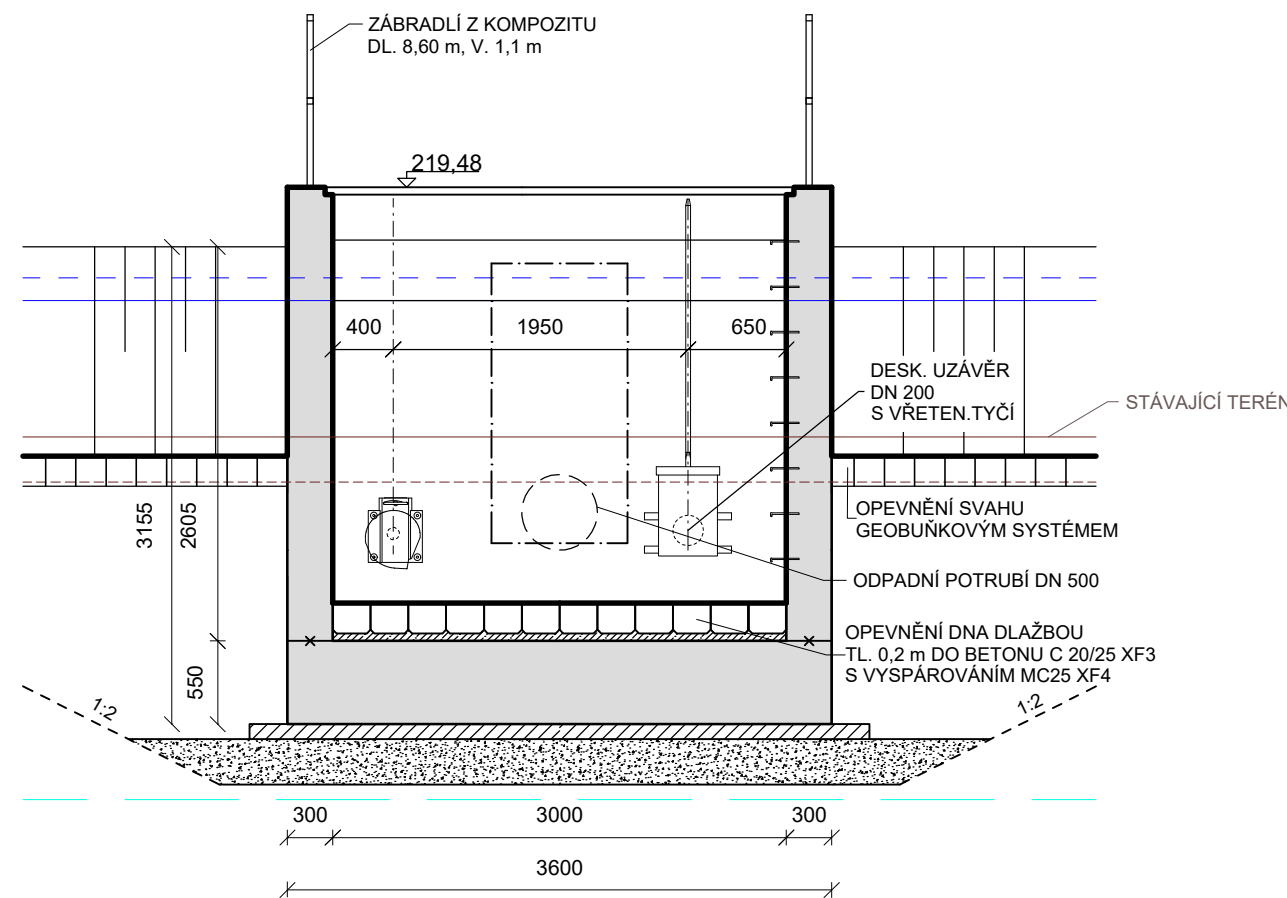
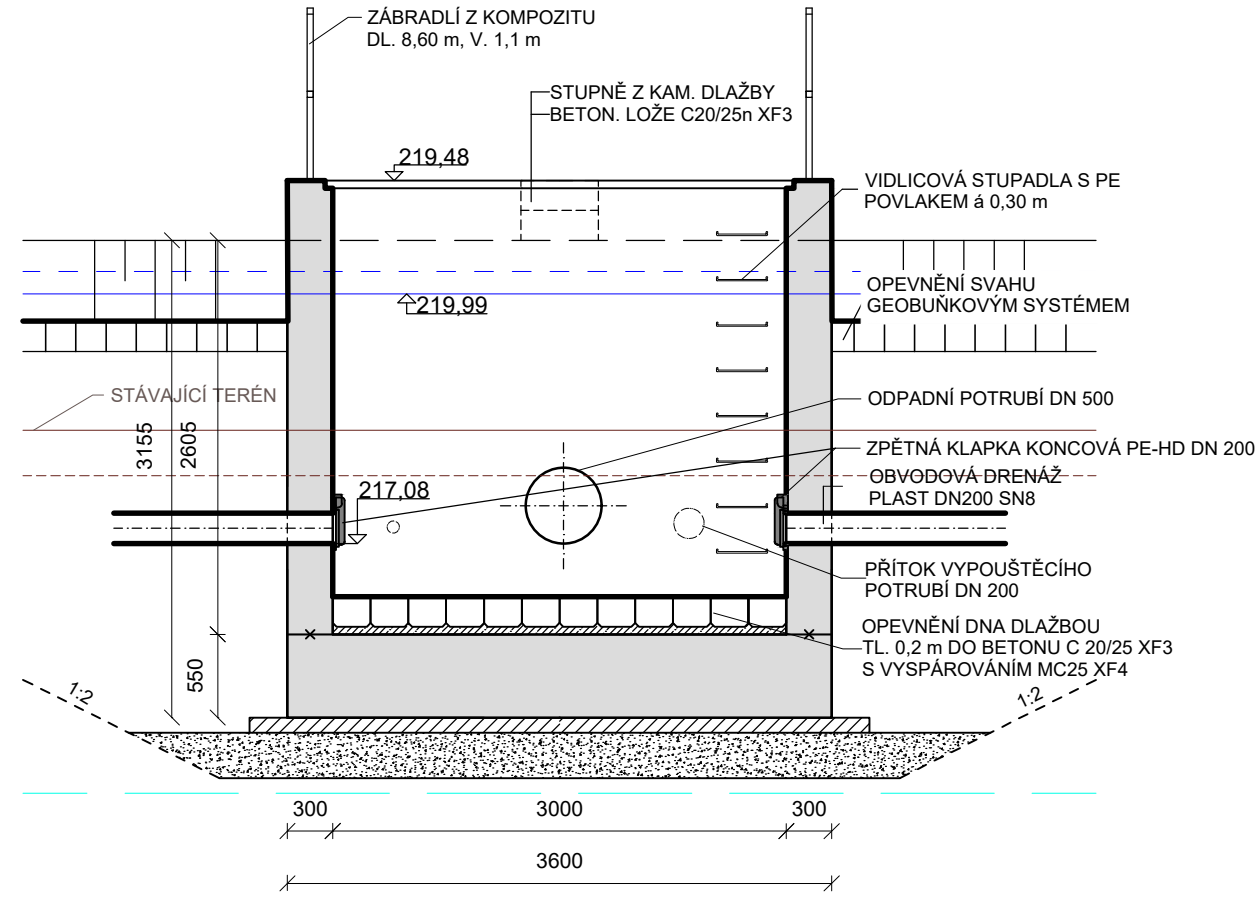
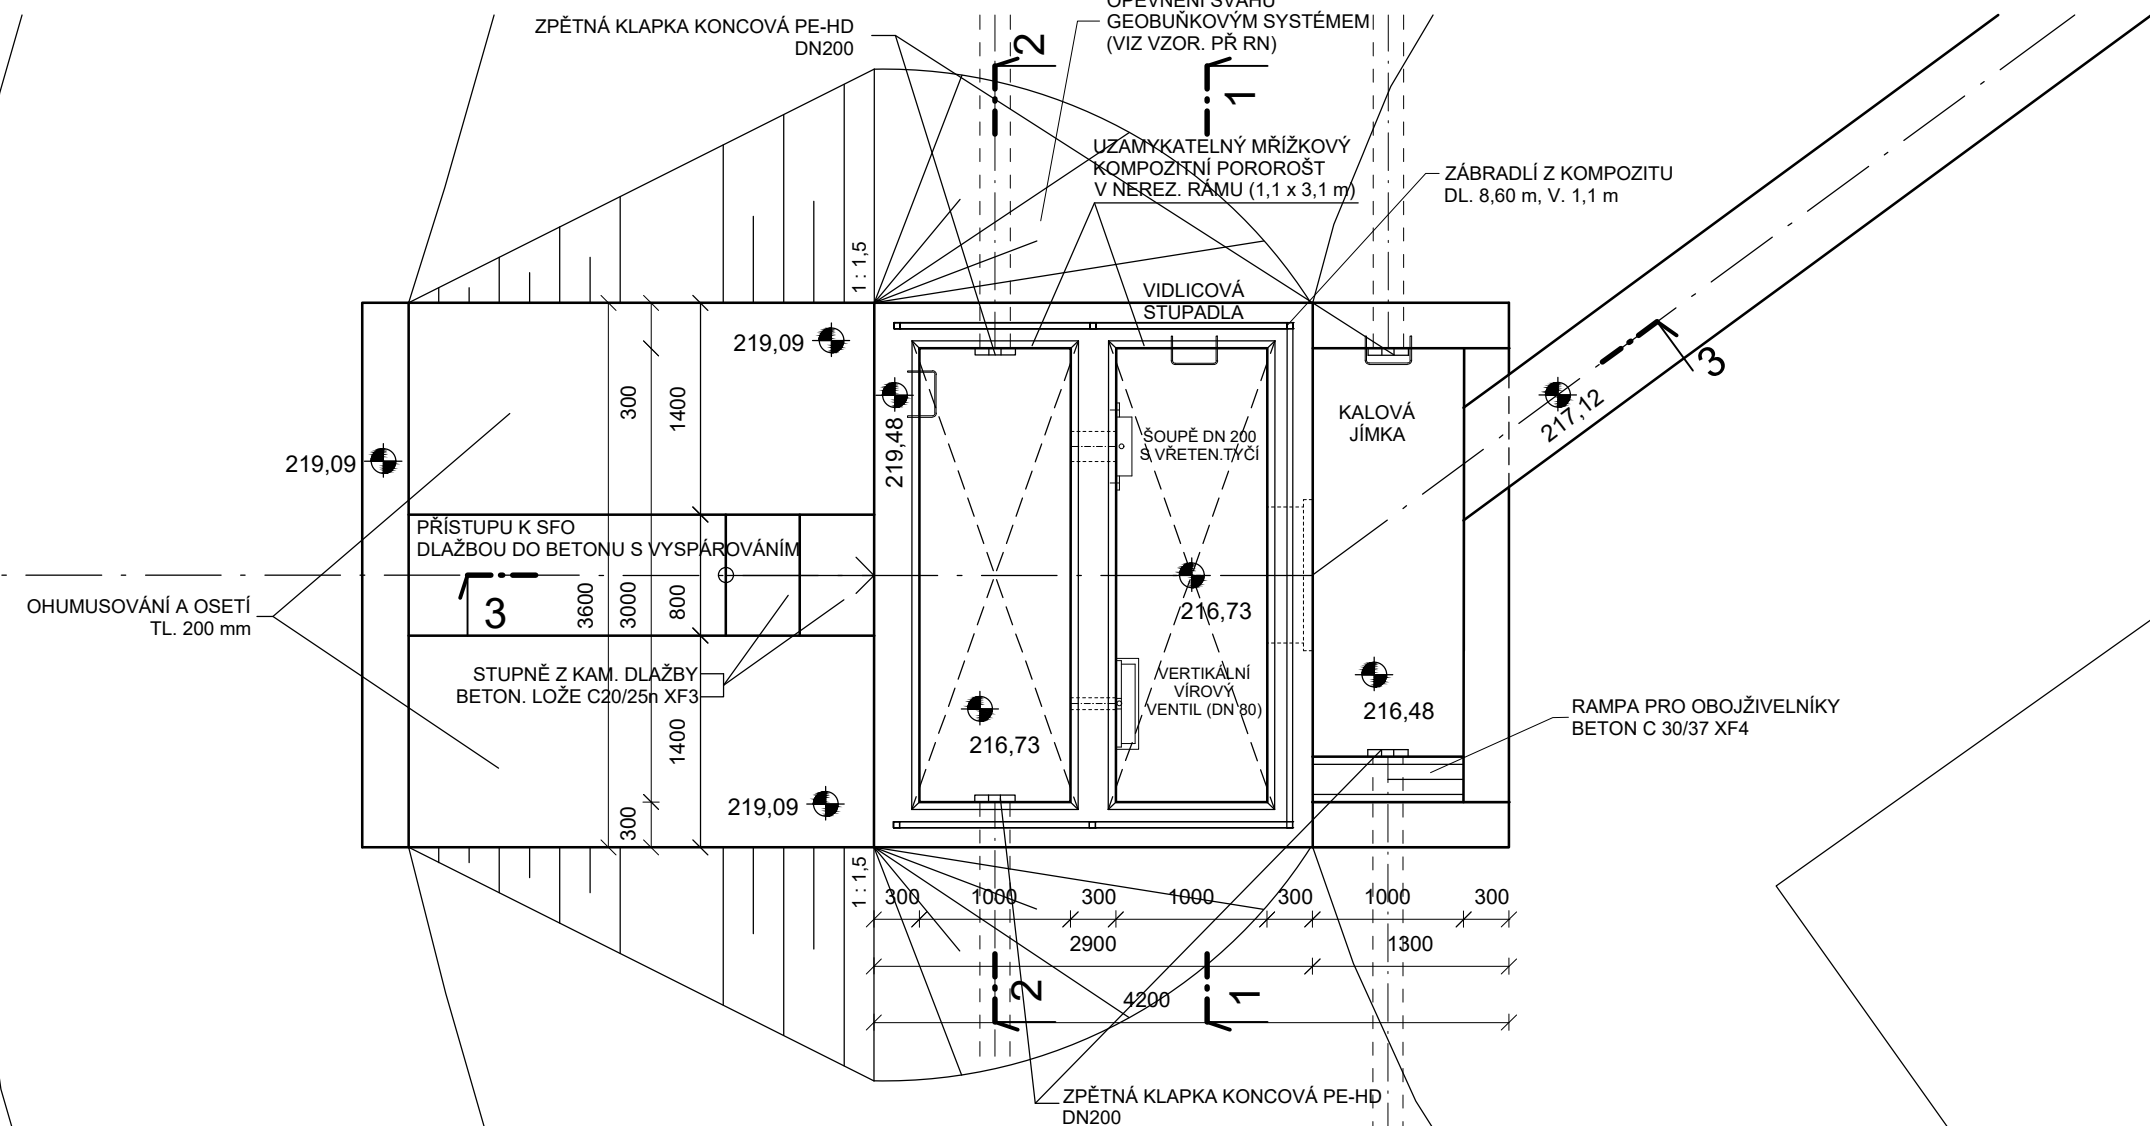


SO 360.9 - SFO  
M 1:50

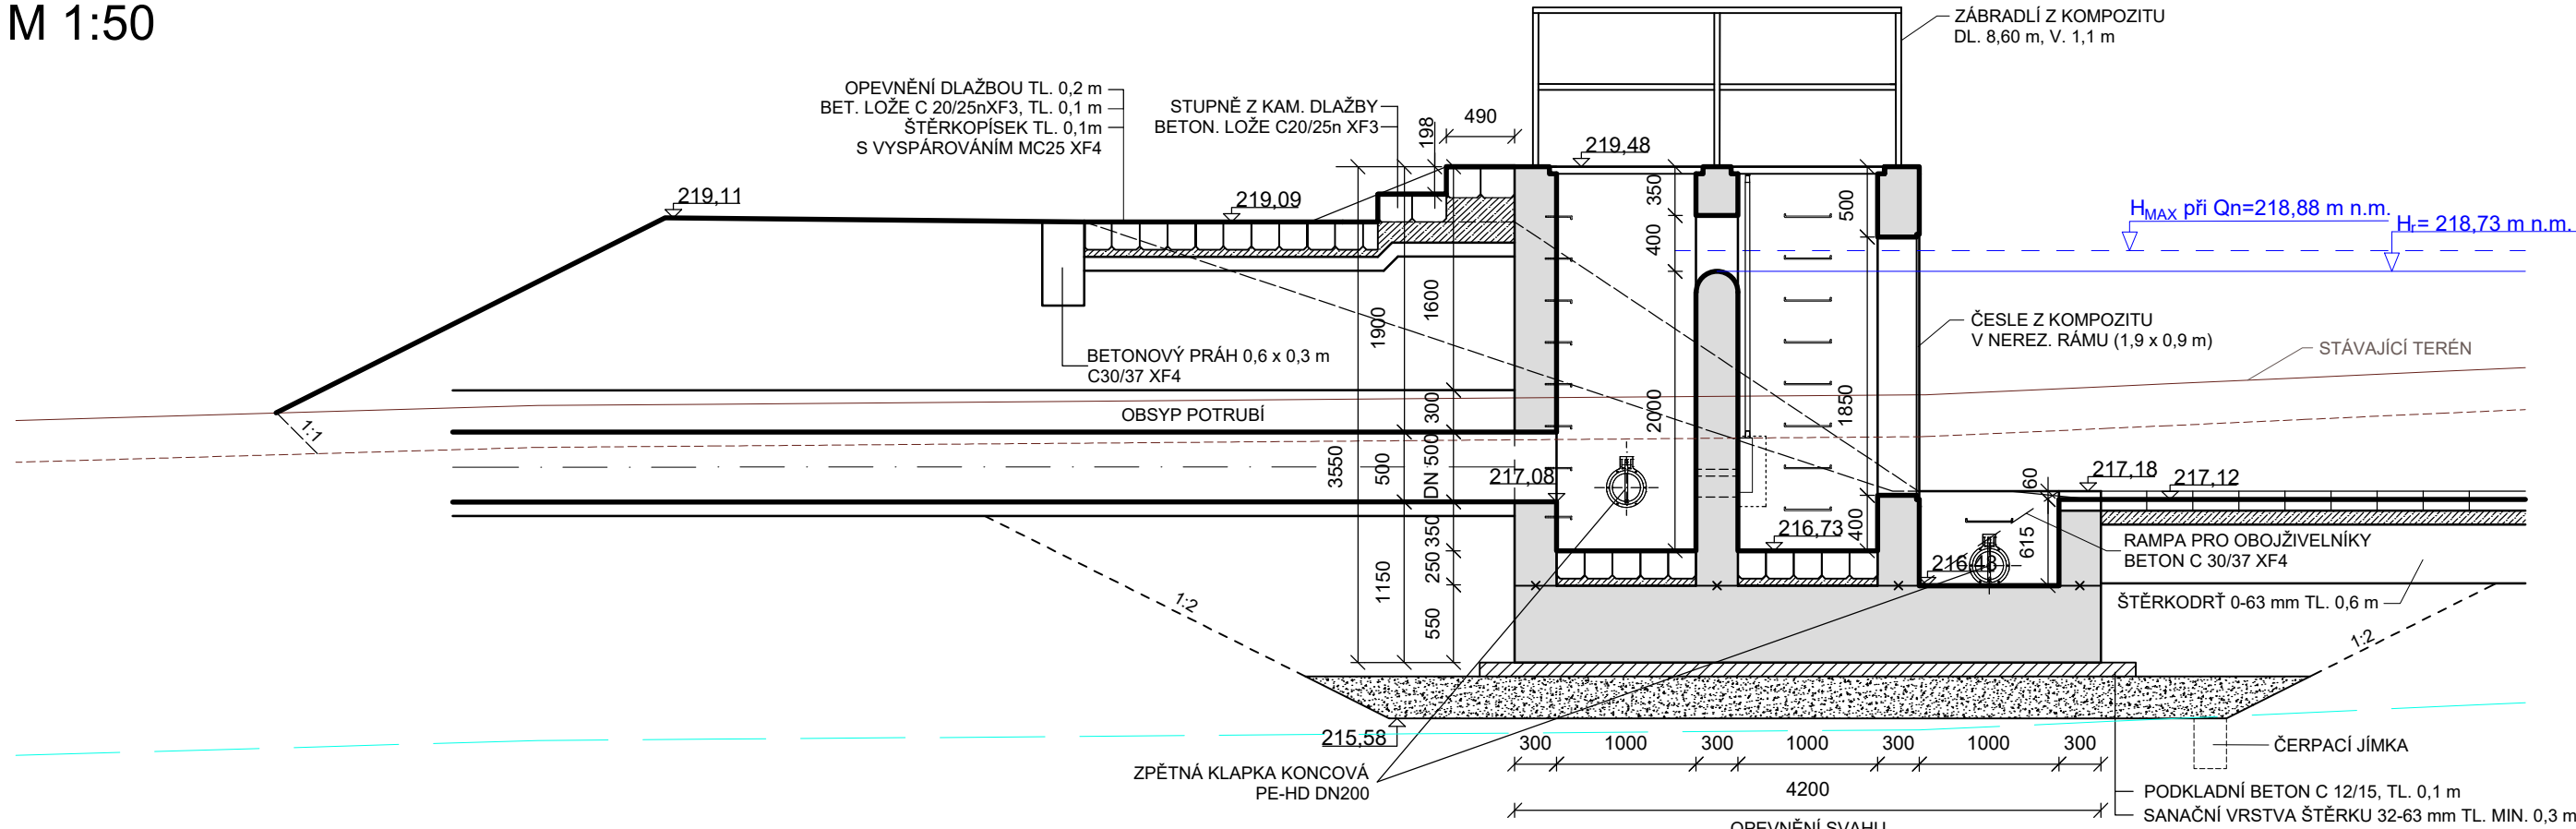

POZNÁMKA:

POŽADAVKY NA POHLEDOVÝ BETON KONSTRUKCE SFO Z HLEDISKA SMĚSI KAMENIVA, HUTNOSTI POVRCHU, BARVY, ODSTÍNU, STEJNORODOSTI A ZPŮSOBU BEDNĚNÍ DLE TKP 18 HRANY ŽB KONSTRUKCE BUDOU ZKOSENY 30/30 mm PRŮSTUPY VE STĚNÁCH A PRACOVNÍ SPÁRY BUDOU TĚSNĚNY TĚSNÍCÍ PÁSKOU PRACOVNÍ A DILATAČNÍ SPÁRY V POHLEDOVÉM BETONU ZKOSENY DLE TKP 18 OPEVNĚNÍ PŘÍSTUPU K SFO BUDE PROVEDENO DLAŽBOU Z LOMOVÉHO KAMENE TL. 0,2 m DO BETONU C 20/25nXF3, S VYSPÁROVÁNÍM MC (XF4) (DLAŽBA Z KAMENE viz ČSN EN 13383-1 KÁMEN PRO VODNÍ STAVBY)

Souřadnicový systém: S-JTSK  
Výškový systém: Bpv

SO 360.9

DUN a retenční nádrže na I/16

Objednatel:



ŘEDITELSTVÍ  
SILNIC  
A DÁLNIC

Ředitelství silnic a dálnic s. p.  
Čerčanská 2023/12, Krč, 140 00 Praha 4



Valbek, spol. s r.o.  
Vaňurova 505/17  
460 07 Liberec 3



Zhotovitel:

Valbek, spol. s r.o.  
Vaňurova 505/17  
460 07 Liberec 3

Příloha

SDRUŽENÝ FUNKČNÍ OBJEKT

Valbek, spol. s r.o.  
Vaňurova 505/17  
460 07 Liberec 3

|   |                 |                                                                                       |               |             |
|---|-----------------|---------------------------------------------------------------------------------------|---------------|-------------|
| Vypracoval   | ING. V. JURÁNEK |  | Zak. číslo    | 21-L113-001 |
| Zodp. projektant   | ING. J. VANCL   |  | Datum         | 02/2025     |
| Tech. kontrola   | ING. D. LANDA   |  | Stupeň        | PDPS        |
| Akce<br><br>I/16 MLADÁ BOLESLAV - MARTINOVICE<br><br><br><br><br><br><br><br><br><br>Příloha<br><br>SDRUŽENÝ FUNKČNÍ OBJEKT |                 |                                                                                       | Počet formátů | 4 x A4      |
|   |                 |                                                                                       | Měřítko       | 1 : 50      |
|   |                 |                                                                                       | Č. přílohy    | Paré        |
|   |                 |                                                                                       | 5             |             |
|   |                 |                                                                                       |               |             |