


SITUACE  
M 1 : 1 000



## LEGENDA:

### STÁVAJÍCÍ IS - INFORMATIVNÍ ZÁKRES

- VODOVOD
- KANALIZACE
- DEŠŤOVÁ KANALIZACE
- IS\_Kanalizac\_splaskov
- IS\_Kanalizac\_jednotn
- SDĚLOVACÍ VEDENÍ
- SDĚLOVACÍ VEDENÍ NADZEMNÍ
- PODZEMNÍ SDĚLOVACÍ VEDENÍ
- PLYNOVOD - NTL
- PLYNOVOD - STL
- PLYNOVOD - VTL
- NADZEMNÍ VEDENÍ NN
- NADZEMNÍ VEDENÍ VVN
- PODZEMNÍ VEDENÍ NN
- PODZEMNÍ VEDENÍ VVN
- SILOVÉ VEDENÍ PODZEMNÍ - SŽDC

Souřadnicový systém: S-JTSK  
Výškový systém: Bpiv

### SO 380 Úpravy meliorací

Objednatel:

**ŘEDITELSTVÍ  
SILNIC  
A DÁLNIC**

Ředitelství silnic a dálnic s. p.  
Čerčanská 2023/12, Krč, 140 00 Praha 4

Zhotovitel:

**Valbek**

**Valbek, spol. s r.o.**  
Vaňurova 505/17  
460 07 Liberec 3

|                                                             |                            |               |             |
|-------------------------------------------------------------|----------------------------|---------------|-------------|
| Vypracoval                                                  | ING. J. VANCL              | Zak. číslo    | 21-L113-001 |
| Zodp. projektant                                            | ING. J. VANCL              | Datum         | 02/2025     |
| Tech. kontrola                                              | ING. D. LANDA              | Stupeň        | PDPS        |
| Akce                                                        |                            | Počet formátů | 8 x A4      |
|                                                             |                            | Měřítko       | 1 : 1 000   |
|                                                             |                            | Č. přílohy    | Paré        |
| Zhotovitel:                                                 | Příloha                    |               |             |
| Valbek, spol. s r.o.<br>Vaňurova 505/17<br>460 07 Liberec 3 | SITUACE č. 11 - VĚTEV Q, R |               |             |
|                                                             |                            |               | 2.11        |