


SITUACE
M 1 : 1 000

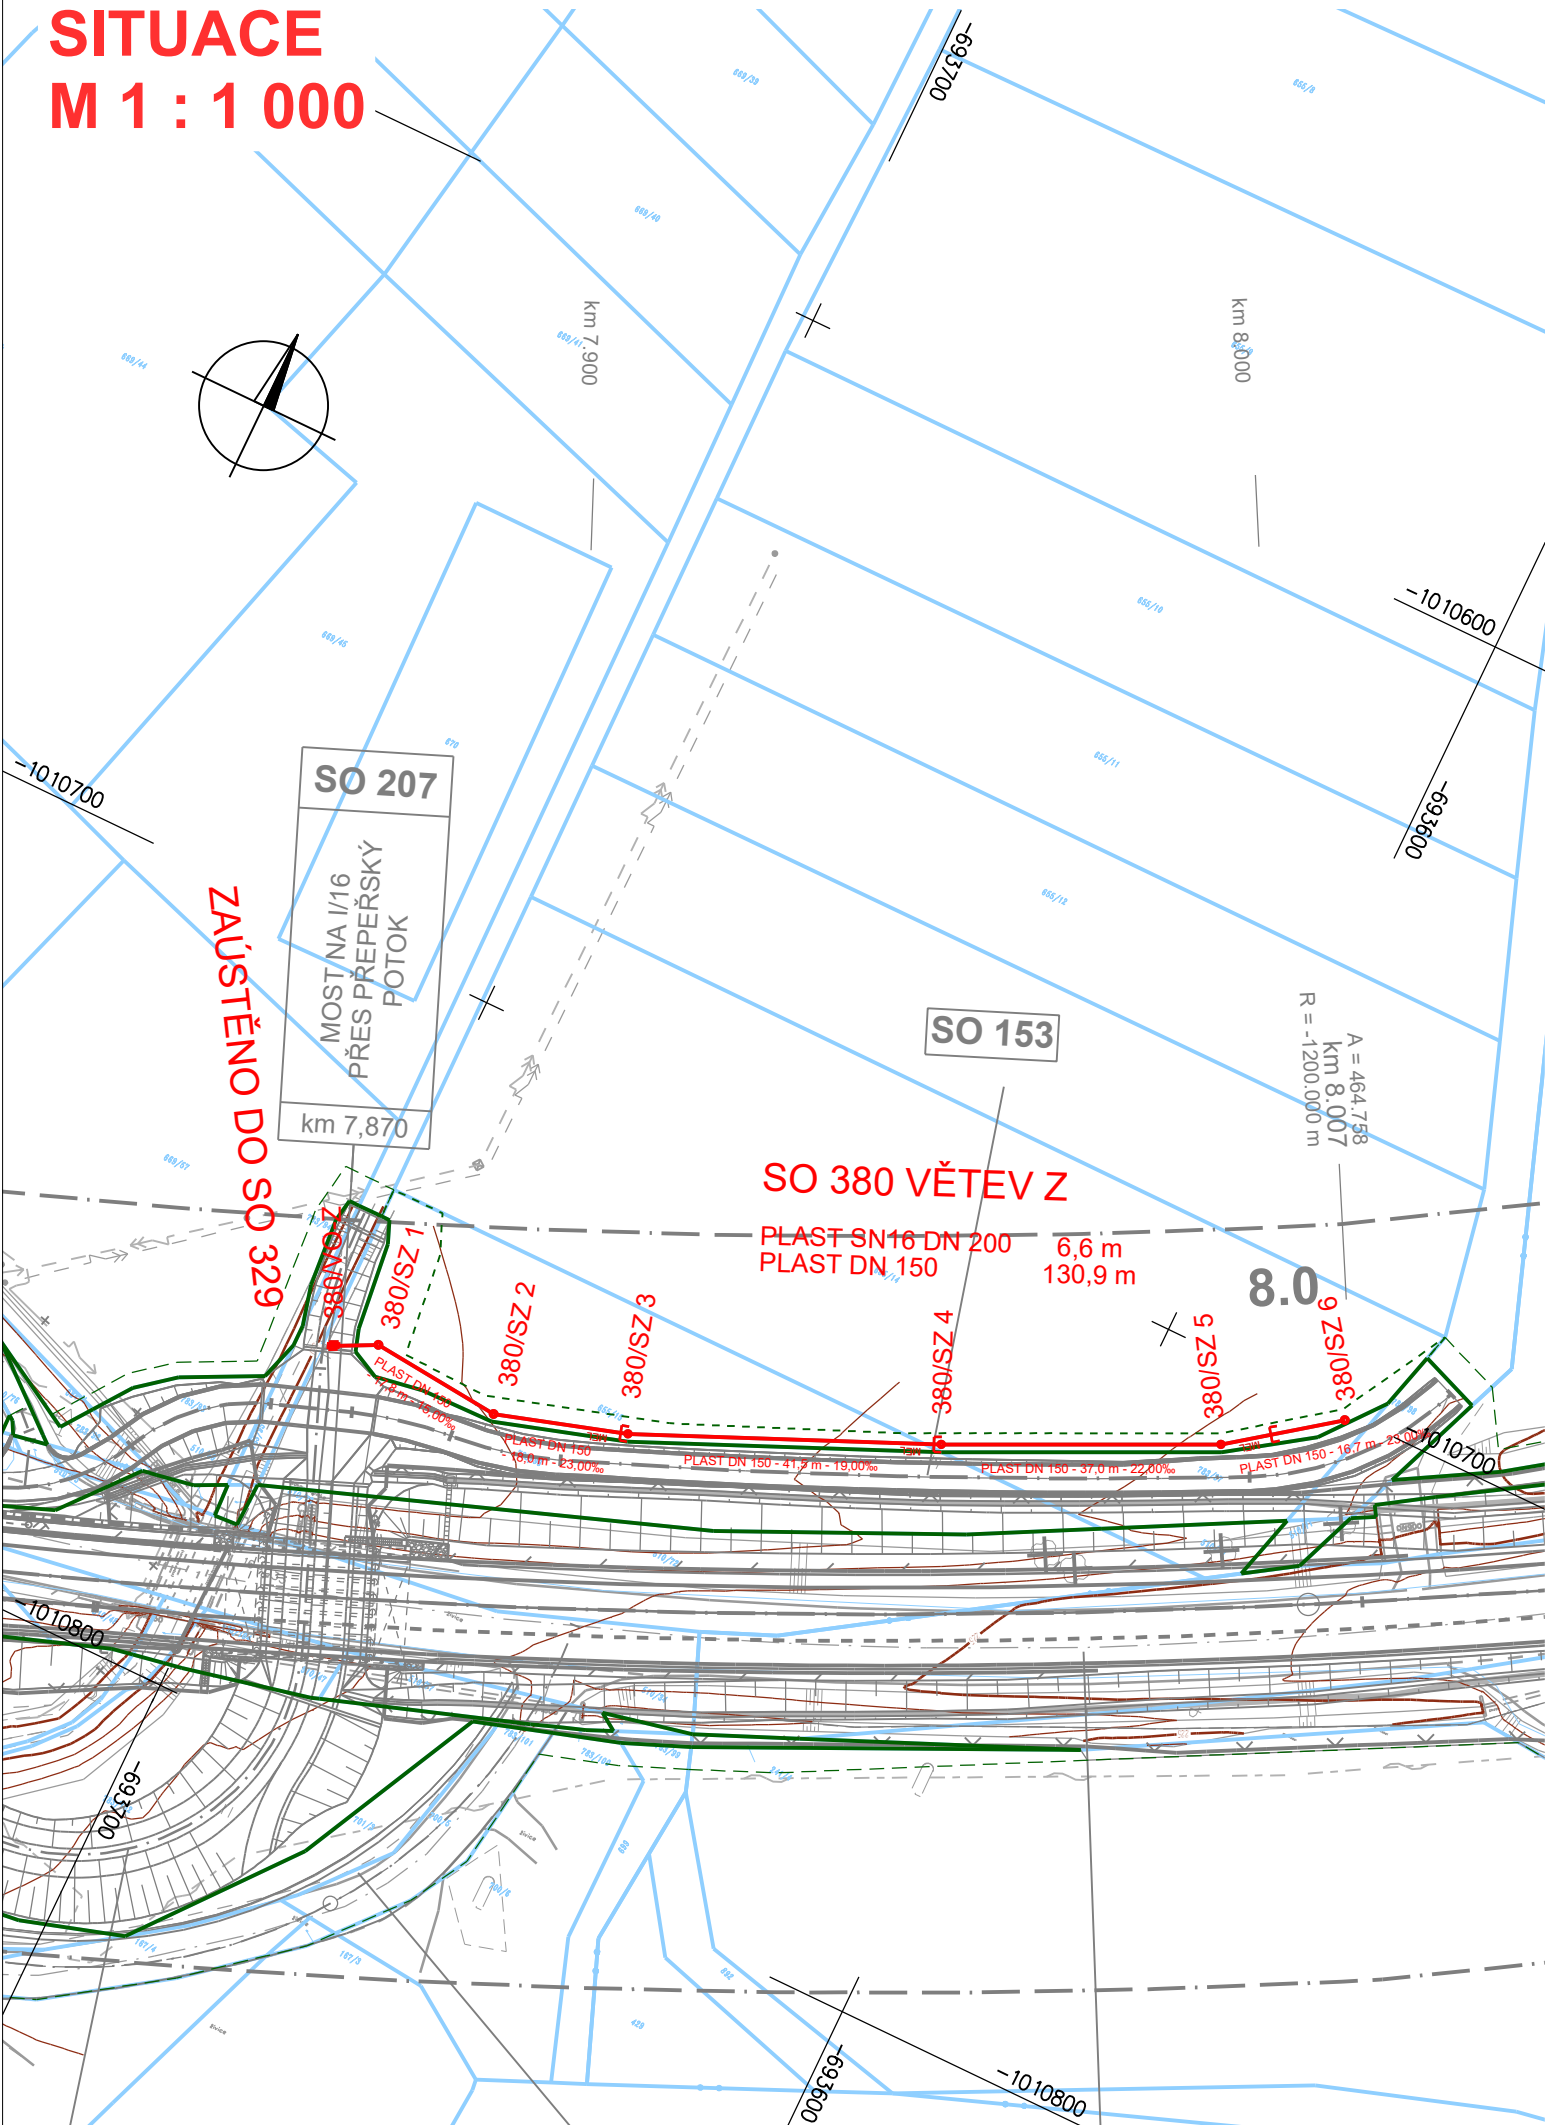

LEGENDA:

STÁVAJÍCÍ IS - INFORMATIVNÍ ZÁKRES

	VODOVOD
	KANALIZACE
	DEŠŤOVÁ KANALIZACE
	IS_Kanalizac_splaskov
	IS_Kanalizace_jednotn
	SDĚLOVACÍ VEDENÍ
	SDĚLOVACÍ VEDENÍ NADZEMNÍ
	PODZEMNÍ SDĚLOVACÍ VEDENÍ
	PLYNOVOD - NTL
	PLYNOVOD - STL
	PLYNOVOD - VTL
	NADZEMNÍ VEDENÍ NN
	NADZEMNÍ VEDENÍ VN
	NADZEMNÍ VEDENÍ VVN
	PODZEMNÍ VEDENÍ NN
	PODZEMNÍ VEDENÍ VN
	SILOVÉ VEDENÍ PODZEMNÍ - SŽDC

Souřadnicový systém: S-JTSK
Výškový systém: Bpv

SO 380 Úpravy meliorací

Objednatel:



ŘEDITELSTVÍ
SILNIC
A DÁLNIC

Ředitelství silnic a dálnic s. p.
Čerčanská 2023/12, Krč, 140 00 Praha 4

Zhotovitel:



Valbek, spol. s r.o.
Vaňurova 505/17
460 07 Liberec 3

	Vypracoval	ING. J. VANCL		Zak. číslo	21-LI13-001
	Zodp. projektant	ING. J. VANCL		Datum	02/2025
	Tech. kontrola	ING. D. LANDA		Stupeň	PDPS
	Akce I/16 MLADÁ BOLESLAV - MARTINOVICE			Počet formátů	2 x A4
				Měřítko	1 : 1 000
Zhotovitel: Valbek, spol. s r.o. Vaňurova 505/17 460 07 Liberec 3	Příloha SITUACE č. 15 - VĚTEV Z			2.15	Paré