
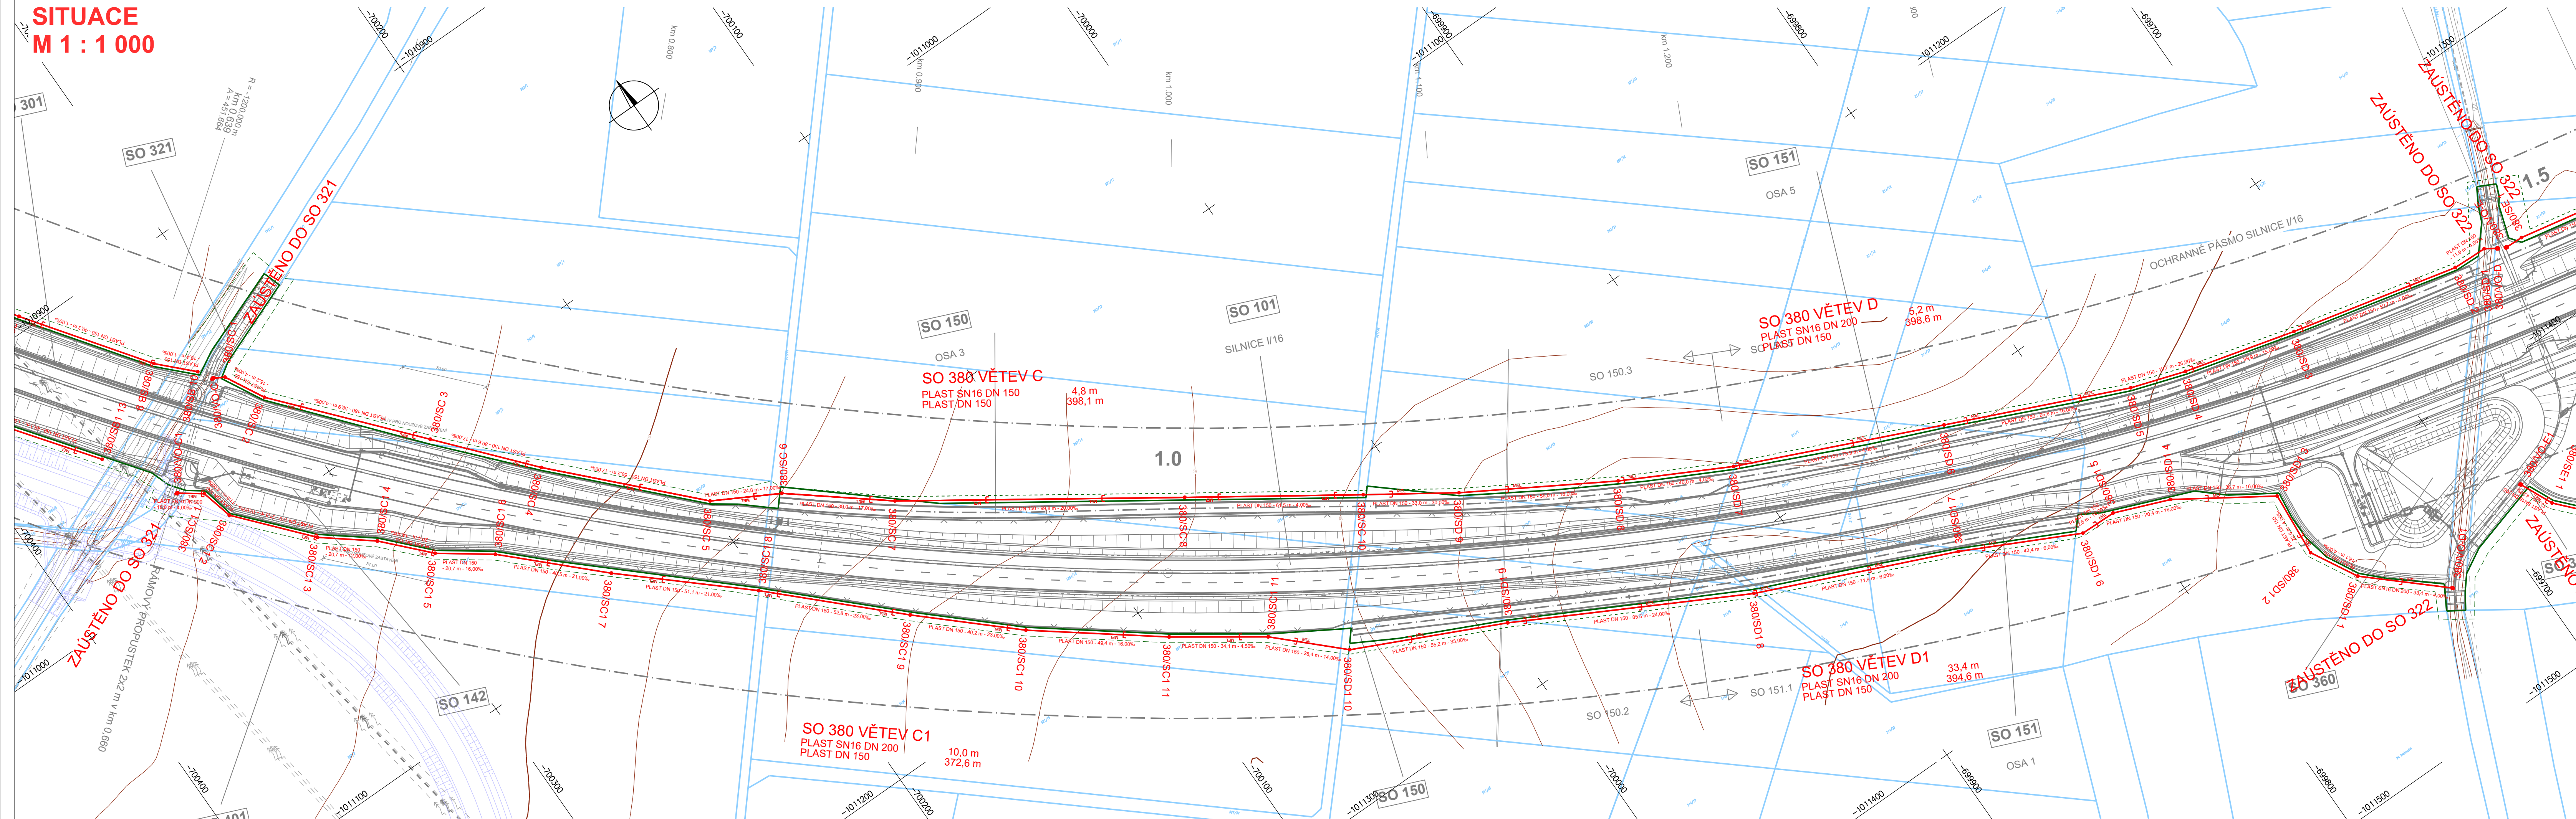


SITUACE
M 1 : 1 000

 

LEGENDA:

STÁVAJÍCÍ IS - INFORMATIVNÍ ZÁKRES

- | | |
|---|-------------------------------|
|  | VODOVOD |
|  | KANALIZACE |
|  | DEŠŤOVÁ KANALIZACE |
|  | IS_Kanalizac_splaskov |
|  | IS_Kanalizace_jednotn |
|  | SDĚLOVACÍ VEDEŇÍ |
|  | SDĚLOVACÍ VEDEŇÍ NADZEMNÍ |
|  | PODZEMNÍ SDĚLOVACÍ VEDEŇÍ |
|  | PLYNOVOD - NTL |
|  | PLYNOVOD - STL |
|  | PLYNOVOD - VTL |
|  | NADZEMNÍ VEDEŇÍ NN |
|  | NADZEMNÍ VEDEŇÍ VN |
|  | NADZEMNÍ VEDEŇÍ VVN |
|  | PODZEMNÍ VEDEŇÍ NN |
|  | PODZEMNÍ VEDEŇÍ VN |
|  | SILOVÉ VEDEŇÍ PODZEMNÍ - SŽDC |

Souřadnicový systém: S-JTSK
Výškový systém: Bpv

SO 380	Úpravy meliorací
---------------	------------------

Objednatel:




**ŘEDITELSTVÍ
SILNIC
A DÁLNIC**

Ředitelství silnic a dálnic s. p.
Čerčanská 2023/12, Krč, 140 00 Praha 4

Zhotovitel:



Valbek, spol. s r.o.
Vaňurova 505/17
460 07 Liberec 3

 	Vypracoval ING. J. VANCL		Zak. číslo 21-L113-001
	Zodp. projektant ING. J. VANCL		Datum 02/2025
	Tech. kontrola ING. D. LANDA		Stupeň PDPS
	Akce I/16 MLADÁ BOLESLAV - MARTINOVICE		Počet formátů 5 x A4
Zhotovitel: Valbek, spol. s r.o. Vaňurova 505/17 460 07 Liberec 3	Příloha SITUACE č. 2 - VĚTEV C, C1, D a D1	Měřítko 1 : 1 000	Č. přílohy Paré
			2.2