


SITUACE
M 1 : 1 000

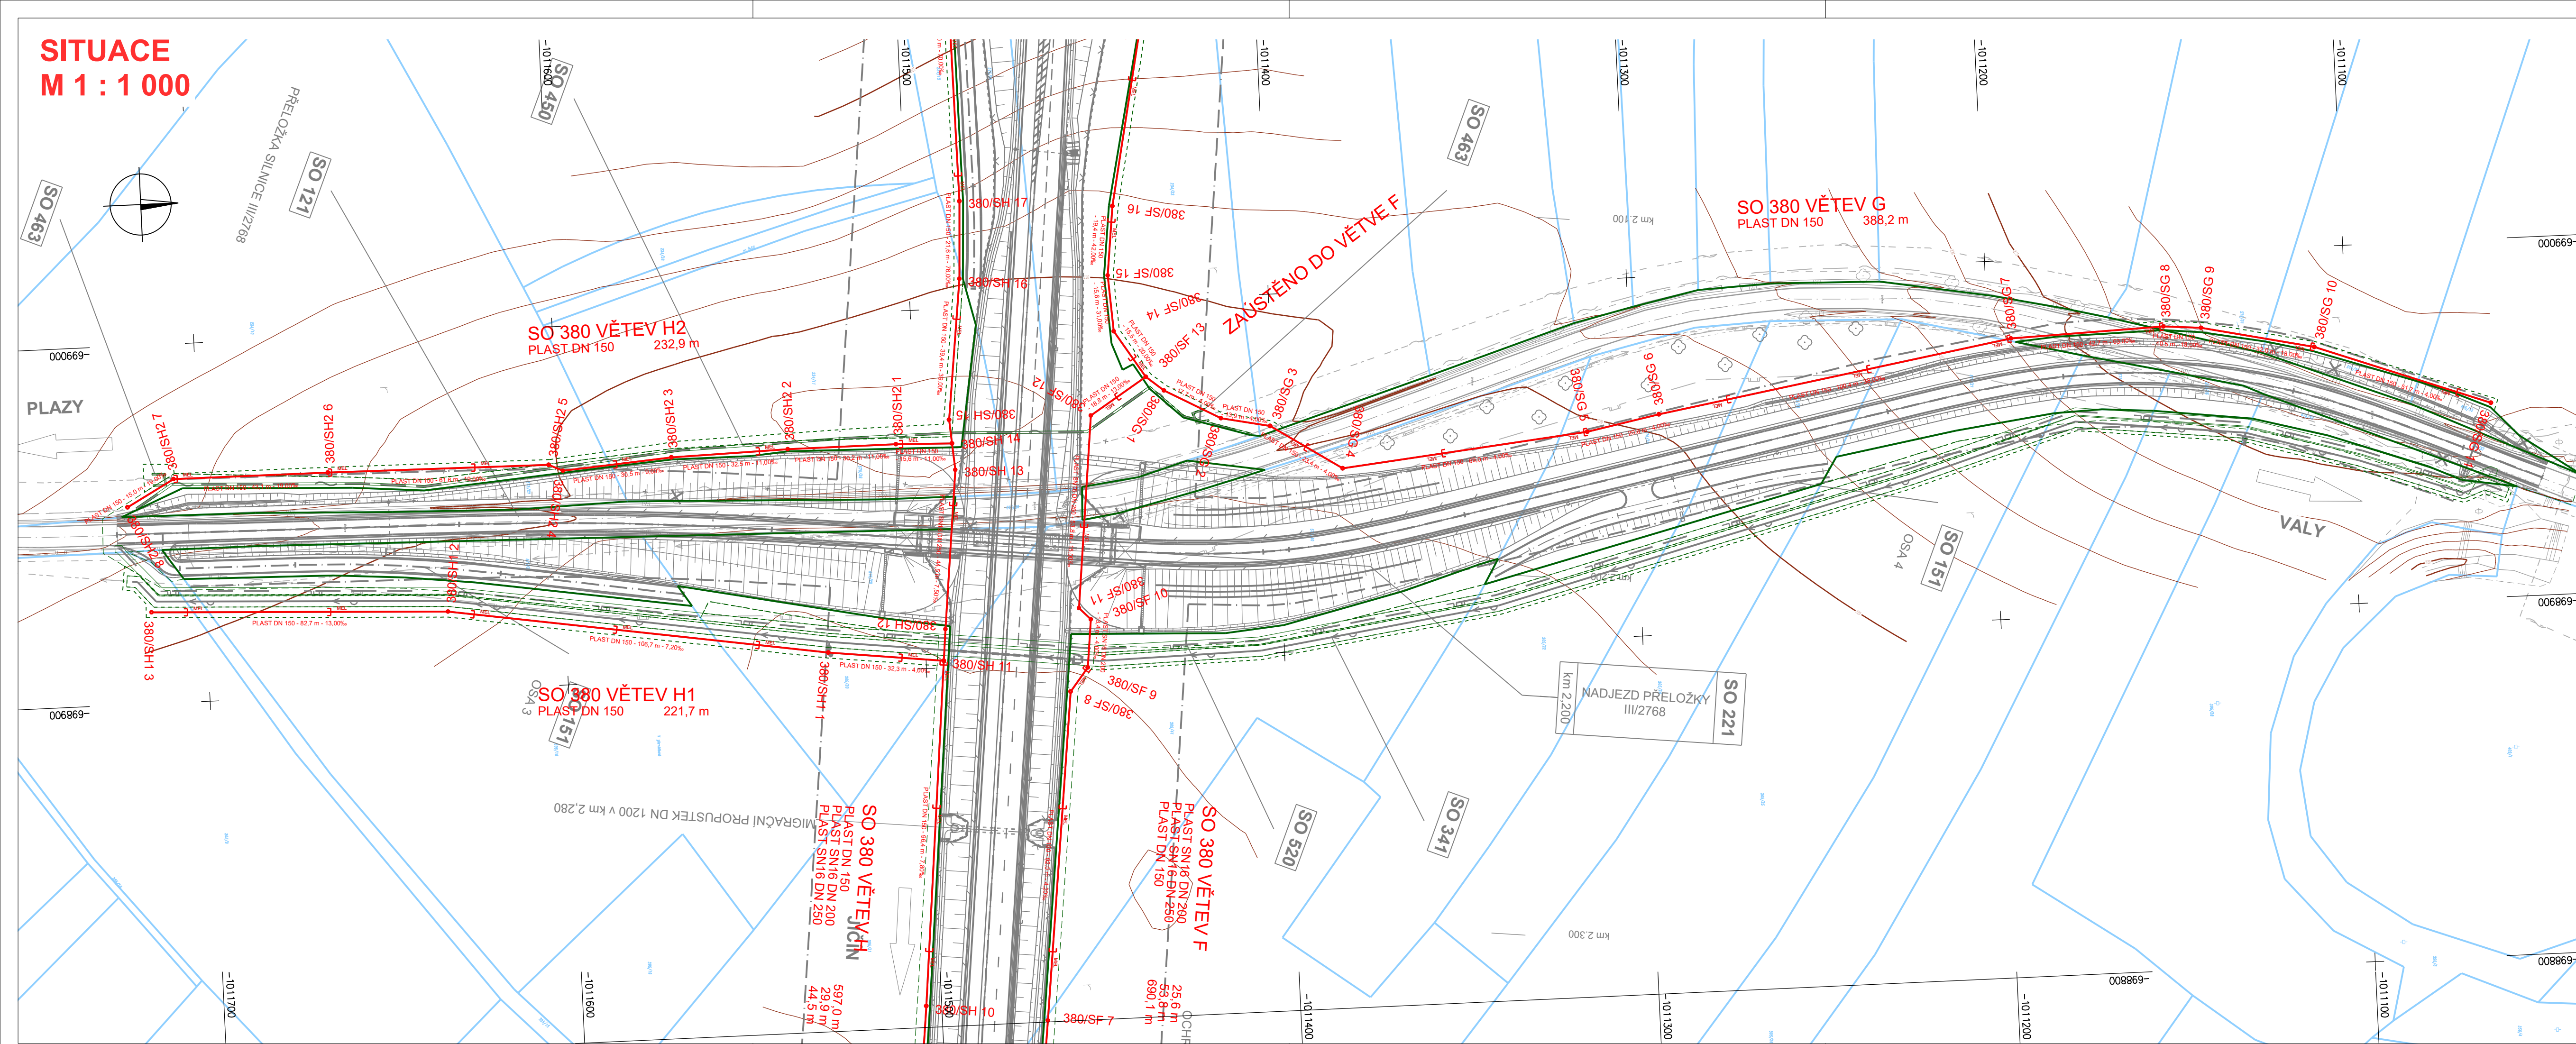

LEGENDA:

STÁVAJÍCÍ IS - INFORMATIVNÍ ZÁKRES

- VODOVOD
- KANALIZACE
- DEŠŤOVÁ KANALIZACE
- IS_Kanalizac_splaskov
- IS_Kanalizace_jednotn
- SDĚLOVACÍ VEDENÍ
- SDĚLOVACÍ VEDENÍ NADZEMNÍ
- PODZEMNÍ SDĚLOVACÍ VEDENÍ
- PLYNOVOD - NTL
- PLYNOVOD - STL
- PLYNOVOD - VTL
- NADZEMNÍ VEDENÍ NN
- NADZEMNÍ VEDENÍ VN
- NADZEMNÍ VEDENÍ VVN
- PODZEMNÍ VEDENÍ NN
- PODZEMNÍ VEDENÍ VN
- SILOVÉ VEDENÍ PODZEMNÍ - SŽDC

Souřadnicový systém: S-JTSK
Výškový systém: Bpv

SO 380 Úpravy meliorací

Objednatel:



**ŘEDITELSTVÍ
SILNIC
A DÁLNIC**

Ředitelství silnic a dálnic s. p.
Čerčanská 2023/12, Krč, 140 00 Praha 4

Zhotovitel:



Valbek

Valbek, spol. s r.o.
Vaňurova 505/17
460 07 Liberec 3

	Vypracoval	ING. J. VANCL		Zak. číslo	21-L113-001	
	Zodp. projektant	ING. J. VANCL		Datum	02/2025	
	Tech. kontrola	ING. D. LANDA		Stupeň	PDPS	
	Akce	I/16 MLADÁ BOLESLAV - MARTINOVICE			Počet formátů	5 x A4
					Měřítko	1 : 1 000
Zhotovitel: Valbek, spol. s r.o. Vaňurova 505/17 07 Liberec 3	Příloha	SITUACE č. 5 - VĚTEV G, H1 a H2			2.5 Č. přílohy Paré	