


SITUACE
M 1 : 1 000

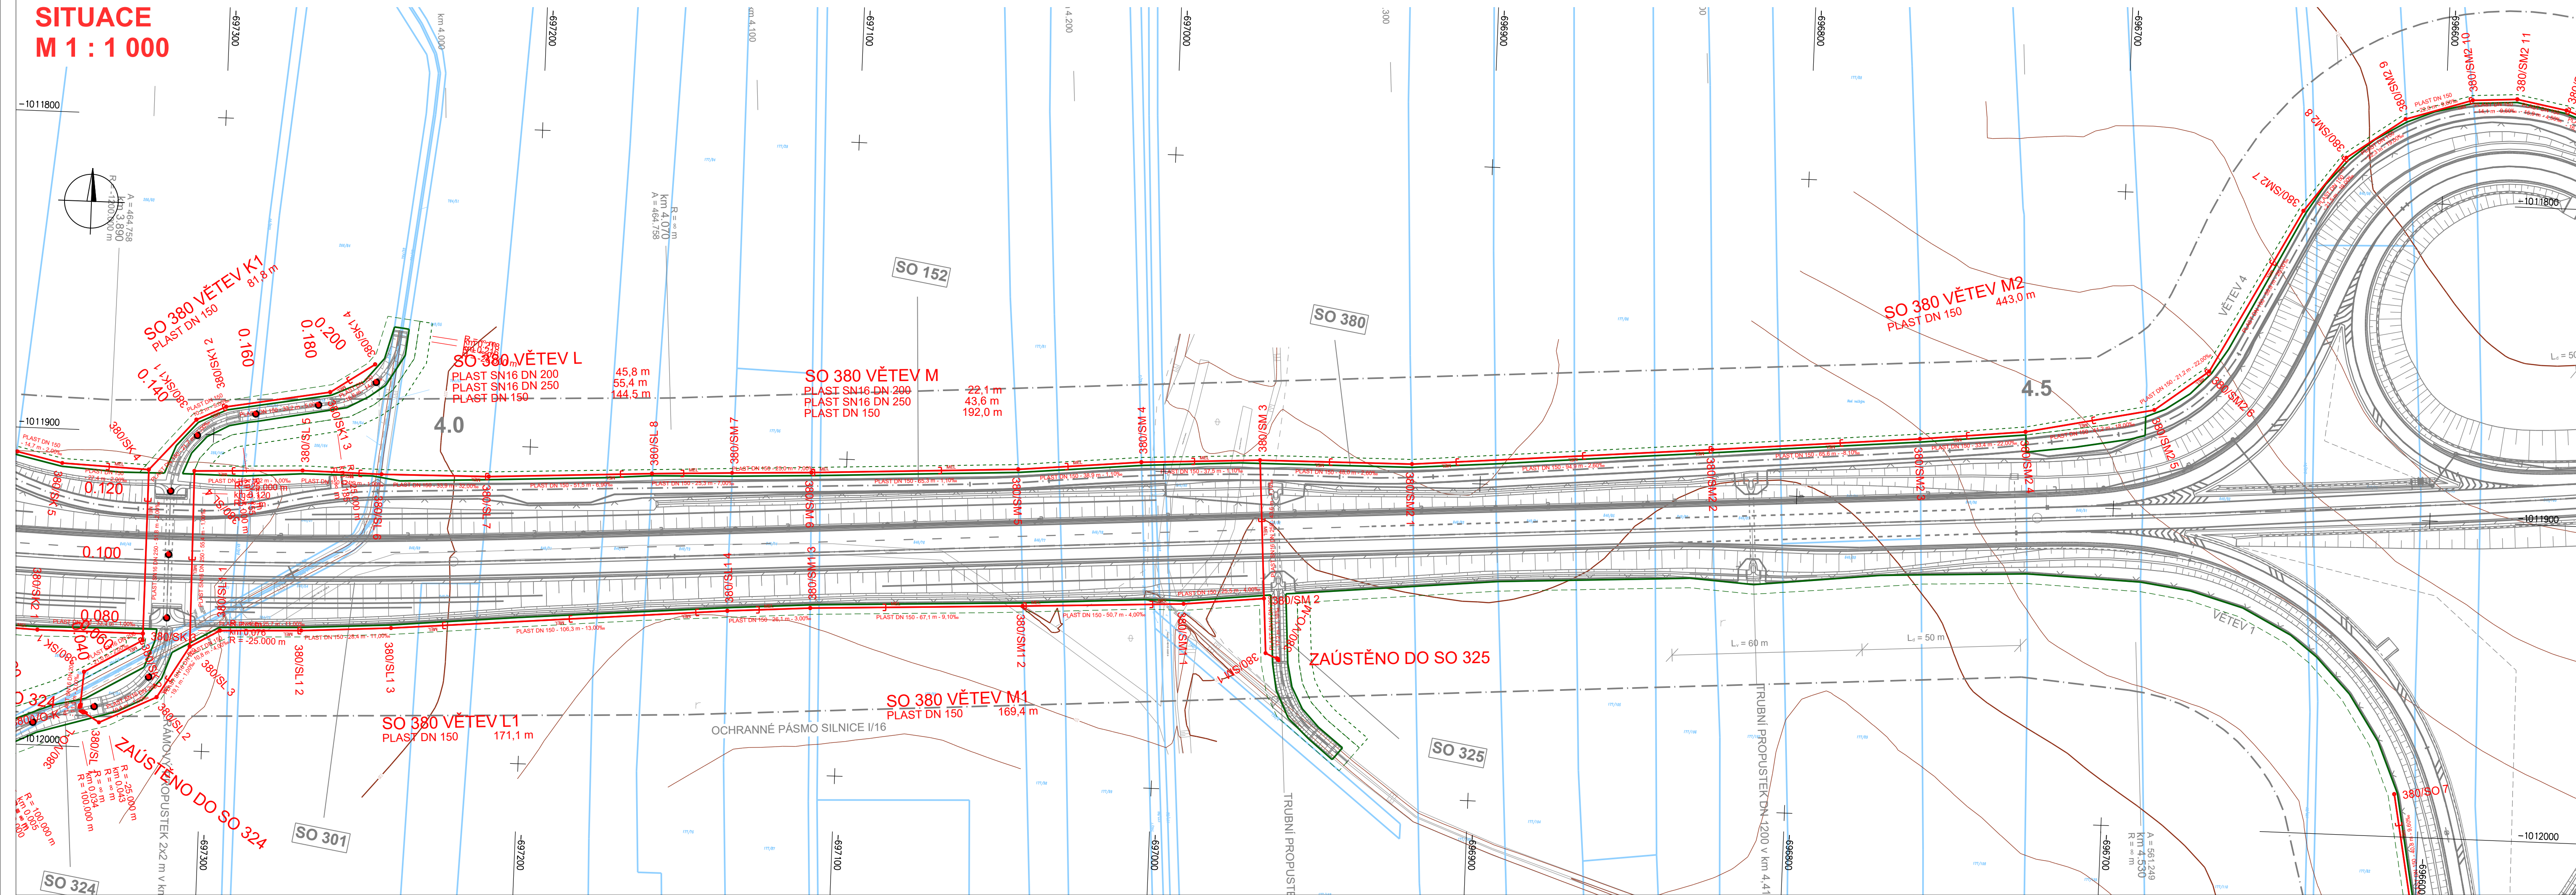

LEGENDA:

STÁVAJÍCÍ IS - INFORMATIVNÍ ZÁKRES

- | | |
|---|-------------------------------|
|  | VODOVOD |
|  | KANALIZACE |
|  | DEŠŤOVÁ KANALIZACE |
|  | IS_Kanalizac_splaskov |
|  | IS_Kanalizace_jednotn |
|  | SDĚLOVACÍ VEDENÍ |
|  | SDĚLOVACÍ VEDENÍ NADZEMNÍ |
|  | PODZEMNÍ SDĚLOVACÍ VEDENÍ |
|  | PLYNOVOD - NTL |
|  | PLYNOVOD - STL |
|  | PLYNOVOD - VTL |
|  | NADZEMNÍ VEDENÍ NN |
|  | NADZEMNÍ VEDENÍ VN |
|  | NADZEMNÍ VEDENÍ VVN |
|  | PODZEMNÍ VEDENÍ NN |
|  | PODZEMNÍ VEDENÍ VN |
|  | SILOVÉ VEDENÍ PODZEMNÍ - SŽDC |

Souřadnicový systém: S-JTSK
Výškový systém: Bpv

SO 380 Úpravy meliorací

Objednatel:



ŘEDITELSTVÍ SILNIC A DÁLNIC

Ředitelství silnic a dálnic s. p.
Čerčanská 2023/12, Krč, 140 00 Praha 4

Zhotovitel:



Valbek, spol. s r.o.
Vaňurova 505/17
460 07 Liberec 3



Zhotovitel:
Valbek, spol. s r.
Vaňurova 505/17
460 07 Liberec 3

Vypracoval	ING. J. VANCL		Zak. číslo	21-LI13-001
Zodp. projektant	ING. J. VANCL		Datum	02/2025
Tech. kontrola	ING. D. LANDA		Stupeň	PDPS
Akce			Počet formátů	5 x A4
I/16 MLADÁ BOLESLAV - MARTINOVICE			Měřítko	1 : 1 000
			Č. přílohy	Paré
Příloha			2.8	
SITUACE č. 8 - VĚTEV L, L1, M, M1 a M2				