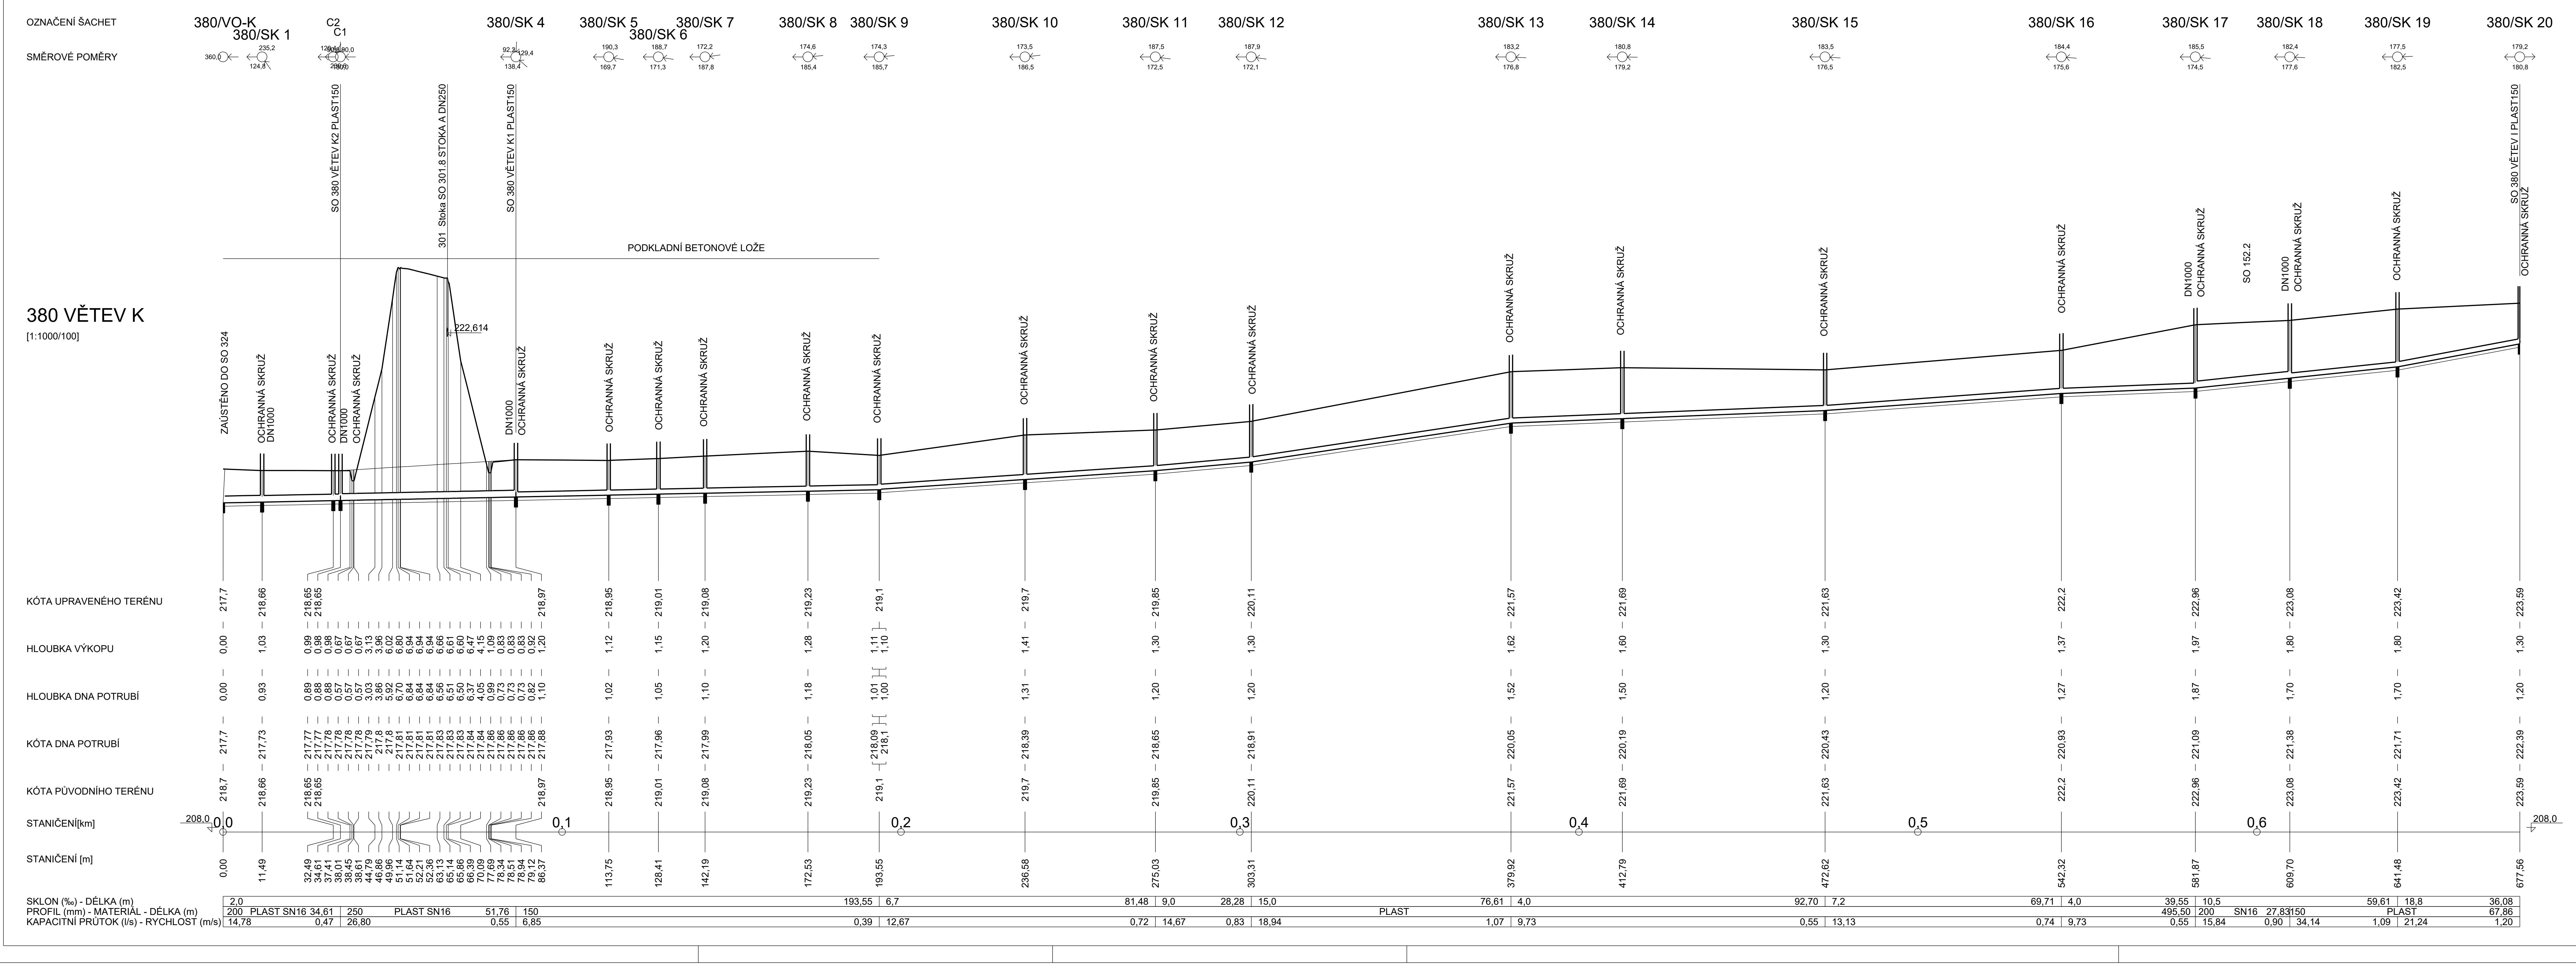
OZNAČENÍ ŠACHET
SMĚROVÉ POMĚRY
380/VO-K
380/SK 1
C2
C1
380/SK 4
380/SK 5
380/SK 6
380/SK 7
380/SK 8
380/SK 9
380/SK 10
380/SK 11
380/SK 12
380/SK 13
380/SK 14
380/SK 15
380/SK 16
380/SK 17
380/SK 18
380/SK 19
380/SK 20
SO 380 VĚTEV K2 PLAST150
301 Stoka SO 301.8 STOKA A DN250
SO 380 VĚTEV K1 PLAST150
SO 380 VĚTEV I PLAST150
PODKLADNÍ BETONOVÉ LOŽE
380 VĚTEV K
[1:1000/100]
ZAÚSTĚNO DO SO 324
OCHRANNÁ SKRUŽ
DN1000
SO 152.2
222,614
KÓTA UPRAVENÉHO TERÉNU
HLOUBKA VÝKOPU
HLOUBKA DNA POTRUBÍ
KÓTA DNA POTRUBÍ
KÓTA PŮVODNÍHO TERÉNU
STANIČENÍ[km]
STANIČENÍ [m]
SKLON (‰) - DÉLKA (m)
PROFIL (mm) - MATERIÁL - DÉLKA (m)
KAPACITNÍ PRŮTOK (l/s) - RYCHLOST (m/s)

OZNAČENÍ ŠACHET	
C1	380/SK 3
C2	380/SK 2

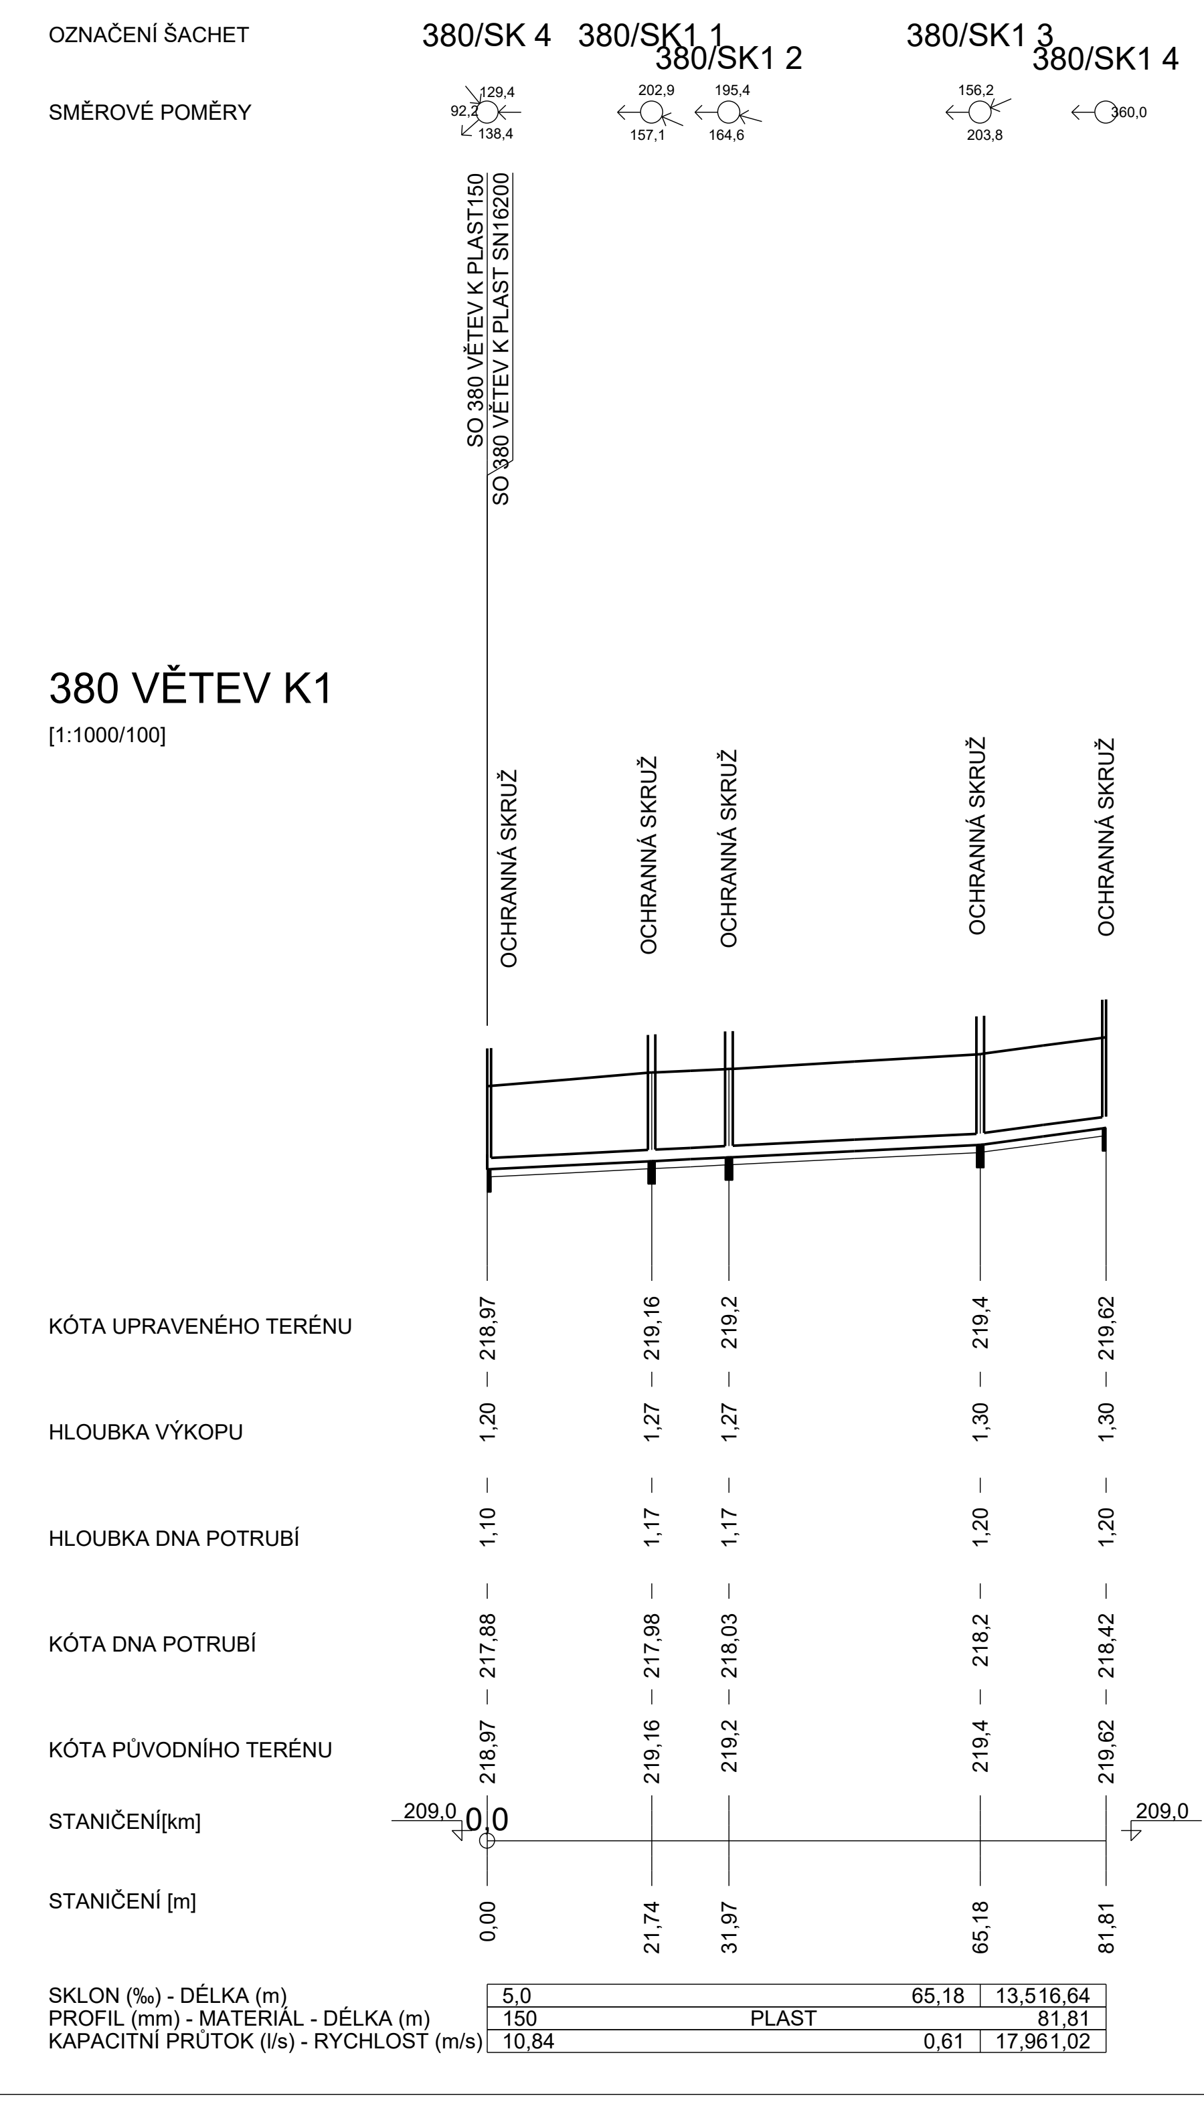
OZNAČENÍ ŠACHET
SMĚROVÉ POMĚRY
380/SK 4
380/SK1 1
380/SK1 2
380/SK1 3
380/SK1 4
SO 380 VĚTEV K PLAST150
SO 380 VĚTEV K PLAST SN16200
380 VĚTEV K1
[1:1000/100]
OCHRANNÁ SKRUŽ
KÓTA UPRAVENÉHO TERÉNU
HLOUBKA VÝKOPU
HLOUBKA DNA POTRUBÍ
KÓTA DNA POTRUBÍ
KÓTA PŮVODNÍHO TERÉNU
STANIČENÍ[km]
STANIČENÍ [m]
SKLON (‰) - DÉLKA (m)
PROFIL (mm) - MATERIÁL - DÉLKA (m)
KAPACITNÍ PRŮTOK (l/s) - RYCHLOST (m/s)

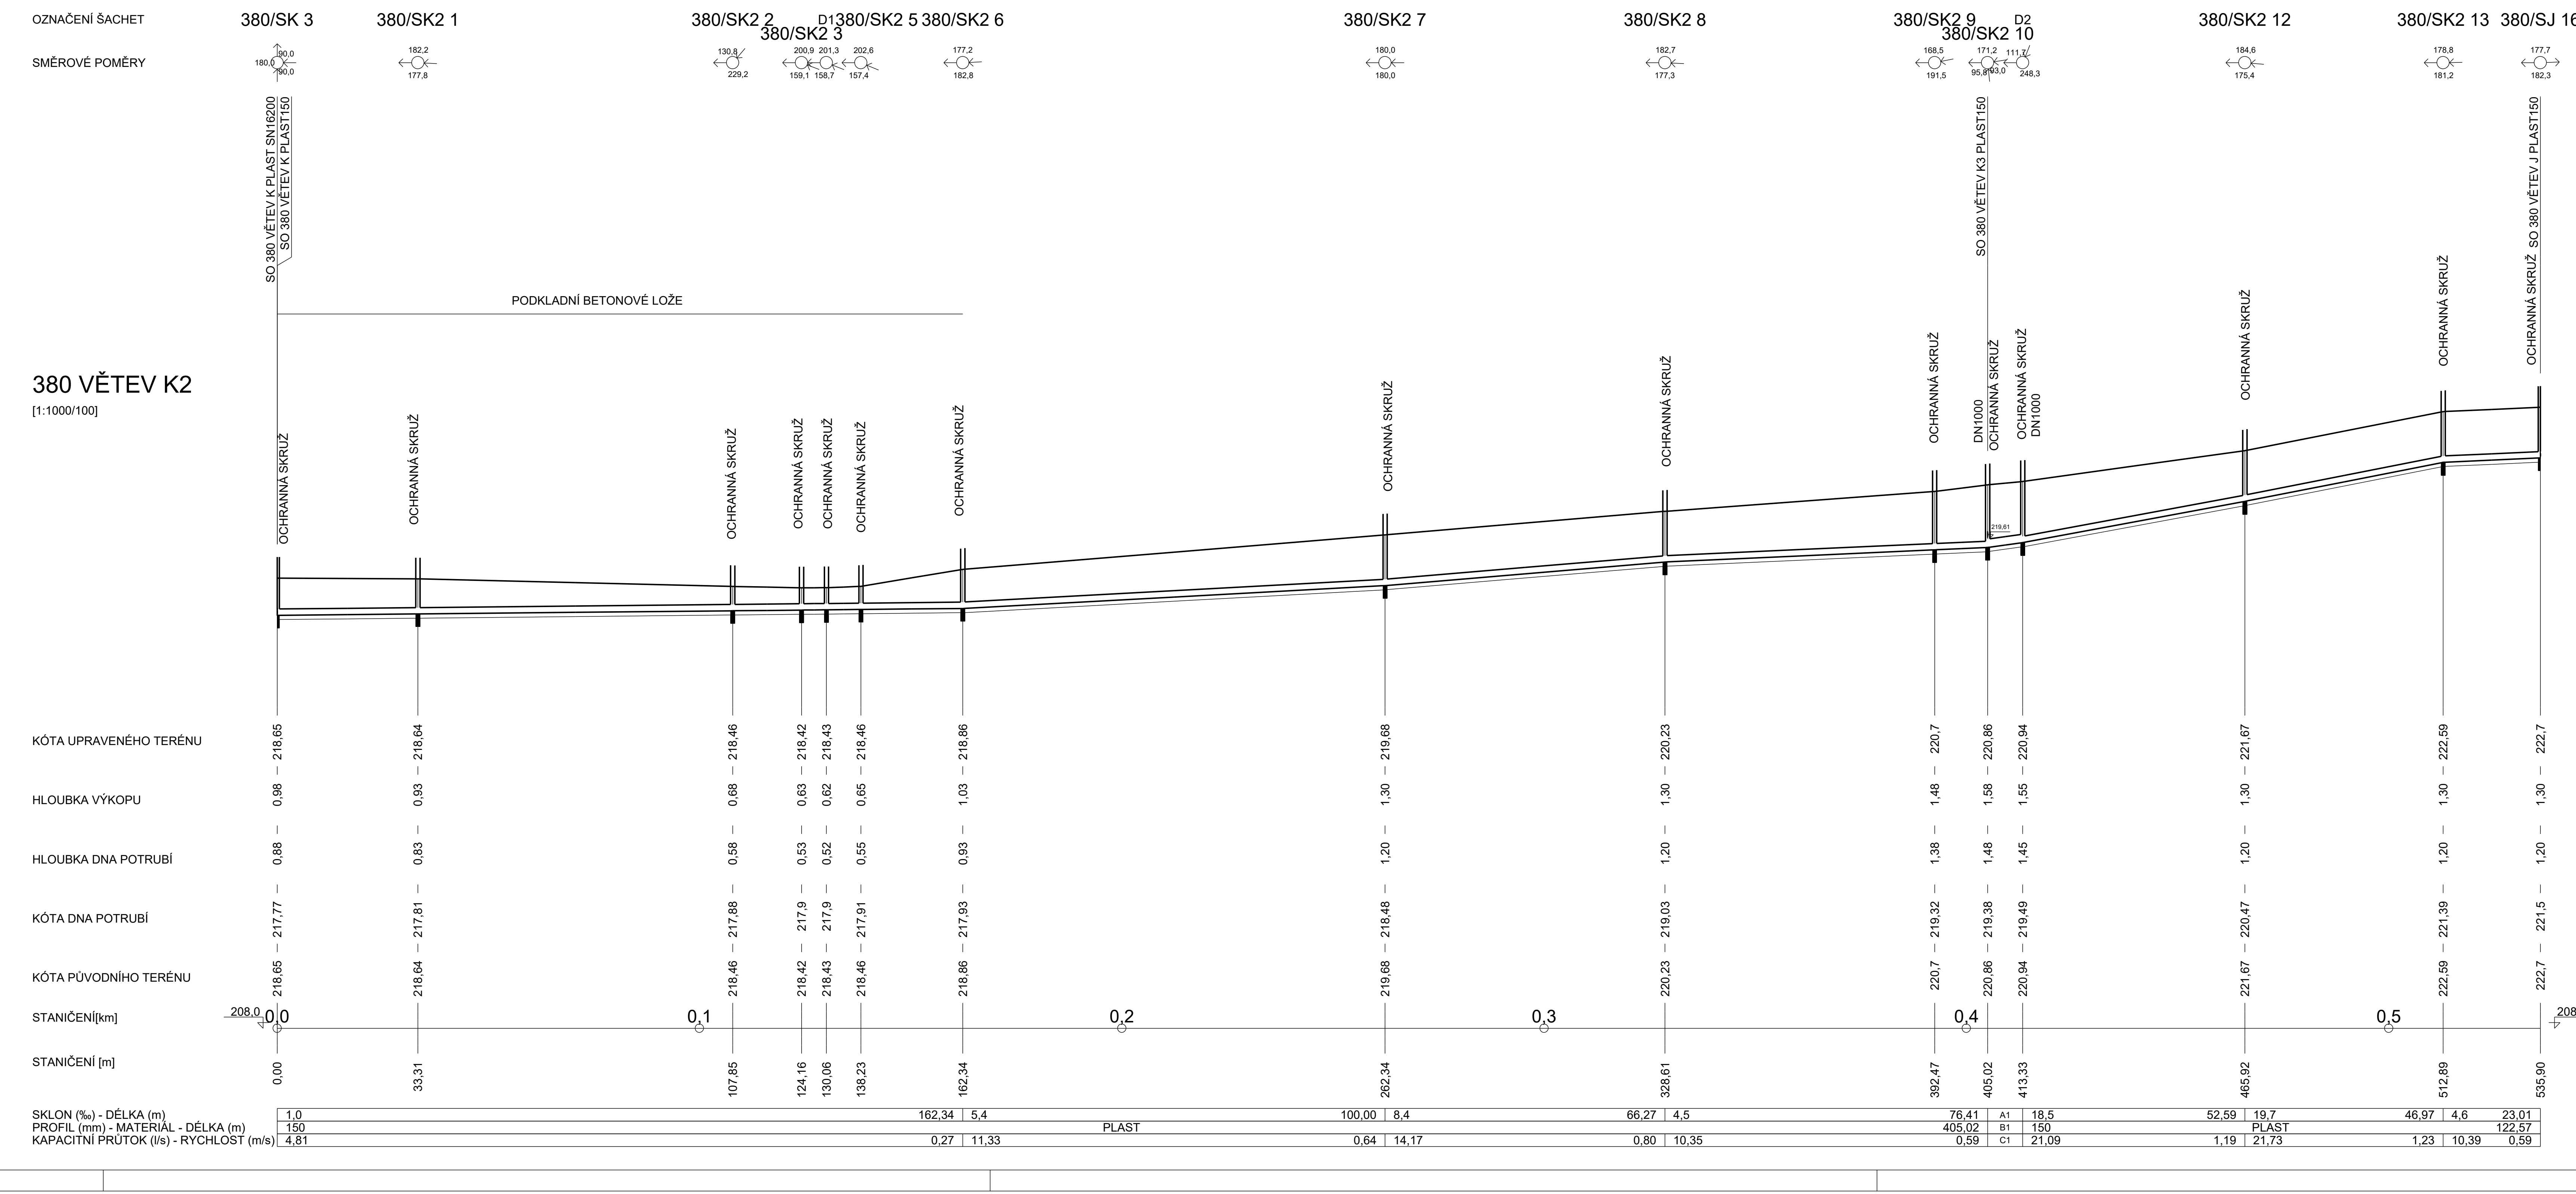
OZNAČENÍ ŠACHET
SMĚROVÉ POMĚRY
380/SK 3
380/SK2 1
380/SK2 2
D1
380/SK2 3
380/SK2 5
380/SK2 6
380/SK2 7
380/SK2 8
380/SK2 9
D2
380/SK2 10
380/SK2 12
380/SK2 13
380/SJ 16
SO 380 VĚTEV K PLAST SN16200
SO 380 VĚTEV K PLAST150
SO 380 VĚTEV K3 PLAST150
SO 380 VĚTEV J PLAST150
PODKLADNÍ BETONOVÉ LOŽE
380 VĚTEV K2
[1:1000/100]
OCHRANNÁ SKRUŽ
DN1000
KÓTA UPRAVENÉHO TERÉNU
HLOUBKA VÝKOPU
HLOUBKA DNA POTRUBÍ
KÓTA DNA POTRUBÍ
KÓTA PŮVODNÍHO TERÉNU
STANIČENÍ[km]
STANIČENÍ [m]
SKLON (‰) - DÉLKA (m)
PROFIL (mm) - MATERIÁL - DÉLKA (m)
KAPACITNÍ PRŮTOK (l/s) - RYCHLOST (m/s)

SKLON (‰) - DÉLKA (m)	
A1	13,9, 8,31
PROFIL (mm) - MATERIÁL - DÉLKA (m)	
B1	200, PLAST SN16, 8,31
KAPACITNÍ PRŮTOK (l/s) - RYCHLOST (m/s)	
C1	39,32, 1,25
OZNAČENÍ ŠACHET	
D1	380/SK2 4
D2	380/SK2 11

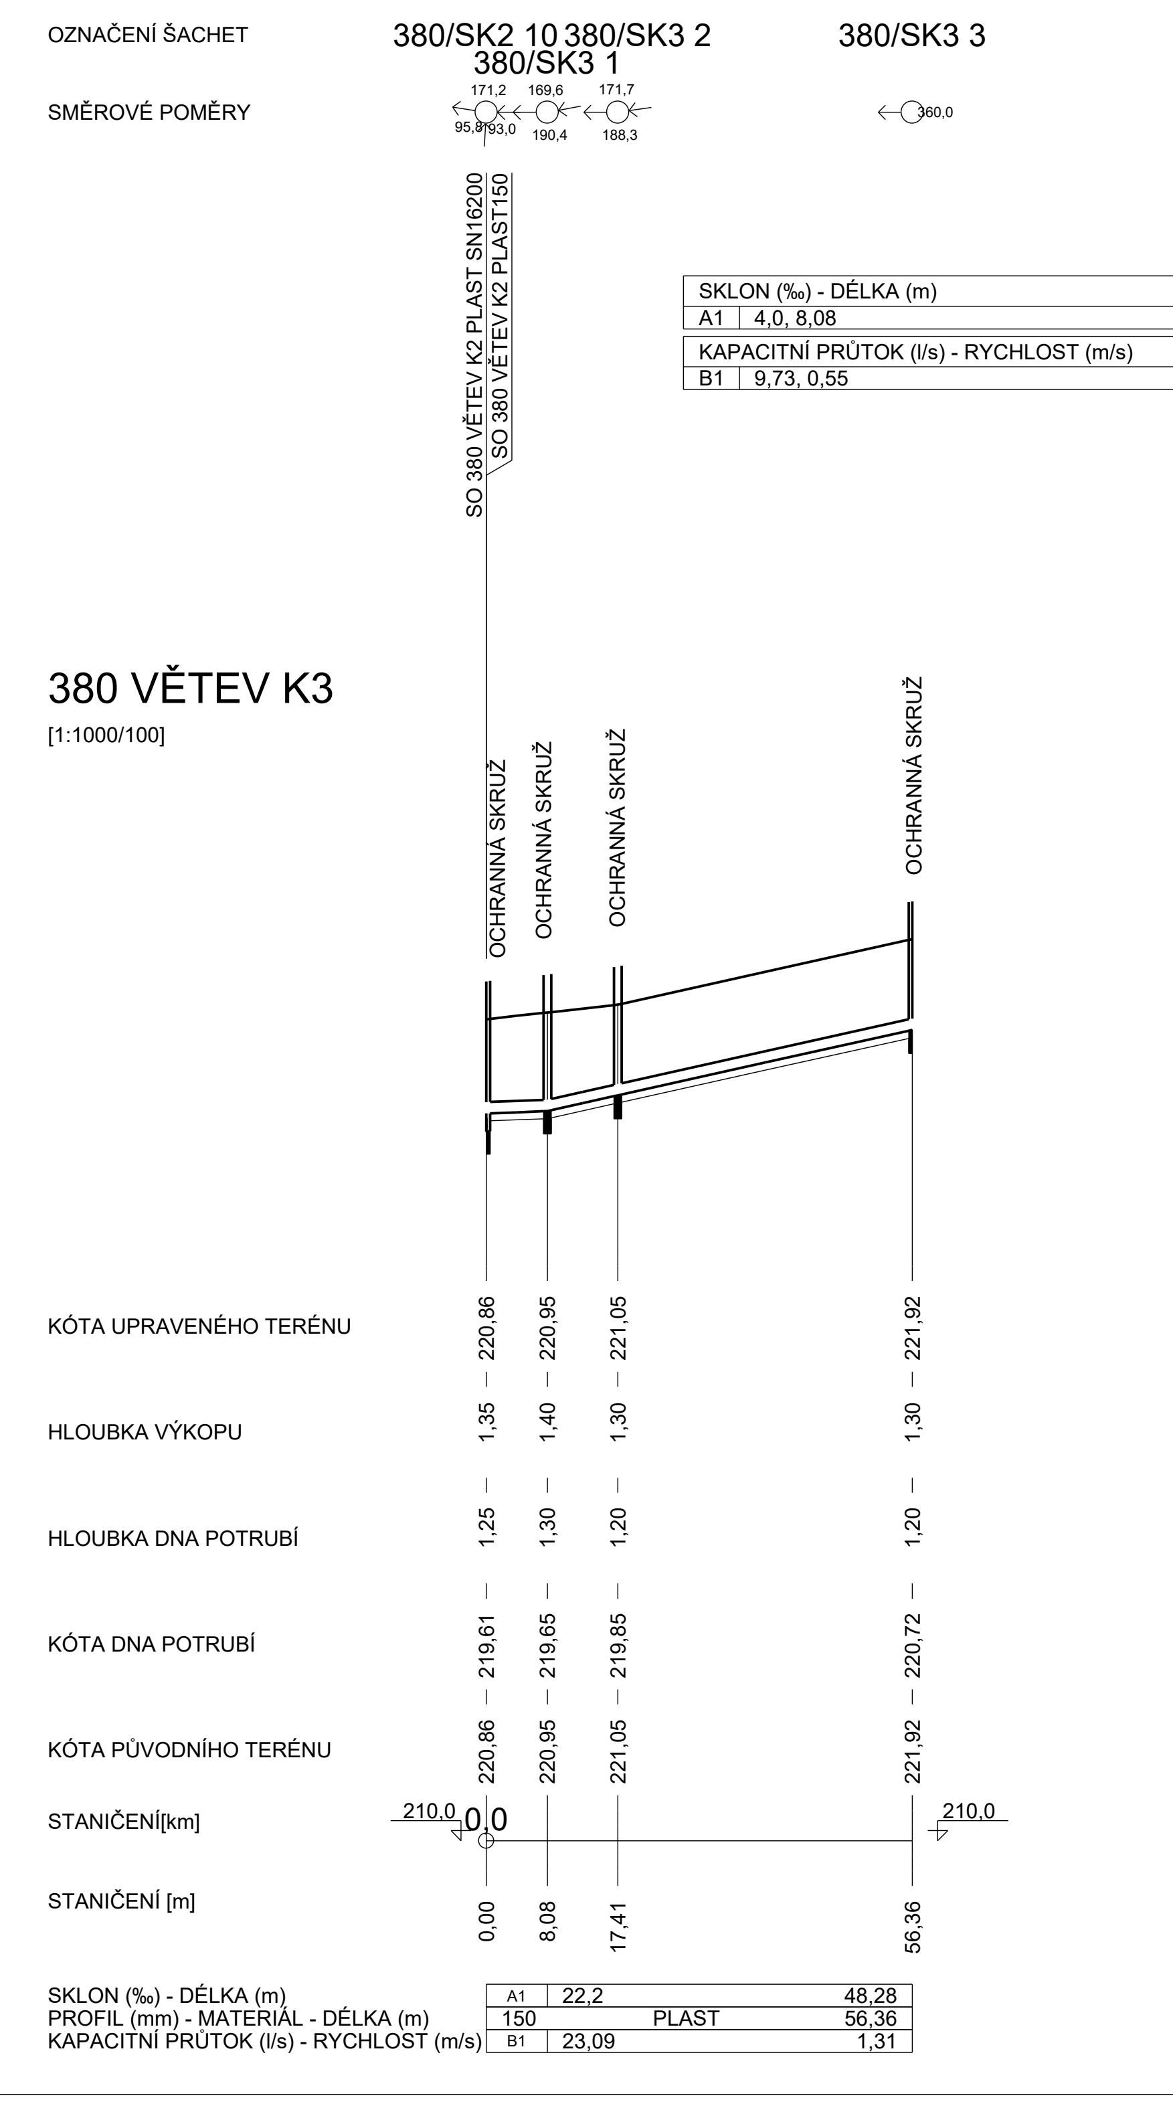
OZNAČENÍ ŠACHET
SMĚROVÉ POMĚRY
380/SK2 10
380/SK3 1
380/SK3 2
380/SK3 3
SO 380 VĚTEV K2 PLAST SN16200
SO 380 VĚTEV K2 PLAST150
380 VĚTEV K3
[1:1000/100]
OCHRANNÁ SKRUŽ
KÓTA UPRAVENÉHO TERÉNU
HLOUBKA VÝKOPU
HLOUBKA DNA POTRUBÍ
KÓTA DNA POTRUBÍ
KÓTA PŮVODNÍHO TERÉNU
STANIČENÍ[km]
STANIČENÍ [m]
SKLON (‰) - DÉLKA (m)
PROFIL (mm) - MATERIÁL - DÉLKA (m)
KAPACITNÍ PRŮTOK (l/s) - RYCHLOST (m/s)

SKLON (‰) - DÉLKA (m)	
A1	4,0, 8,08
KAPACITNÍ PRŮTOK (l/s) - RYCHLOST (m/s)	
B1	9,73, 0,55

Souřadnicový systém: S-JTSK
Výškový systém: Bpv

SO 380 Úpravy meliorací

Objednatel:

Ředitelství silnic a dálnic s. p.
Čerčanská 2023/12, Krč, 140 00 Praha 4

Zhotovitel:

Valbek, spol. s r.o.
Vaňurova 505/17
460 07 Liberec 3

Vypracoval	ING. J. VANCL		Zak. číslo	21-LI13-001
Zodp. projektant	ING. J. VANCL		Datum	02/2025
Tech. kontrola	ING. D. LANDA		Stupeň	PDPS
Akce			Počet formátů	11 x A4
			Měřítko	1 : 1000/100
			Č. přílohy	Paré

Akce
I/16 MLADÁ BOLESLAV - MARTINOVICE

Zhotovitel:
Valbek, spol. s r.o.
Vaňurova 505/17
460 07 Liberec 3

Příloha
PODÉLNÝ PROFIL Č. 11 - VĚTEV K, K1, K2, K3

3.11