PROFIL (mm) - MATERIÁL - DÉLKA (m)	
A1	200, PLAST SN16, 6,85

KAPACITNÍ PRŮTOK (l/s) - RYCHLOST (m/s)	
B1	10,39, 0,33

OZNAČENÍ ŠACHET	
C1	380/SL 1

OZNAČENÍ ŠACHET

SMĚROVÉ POMĚRY

380 VĚTEV L

[1:1000/100]

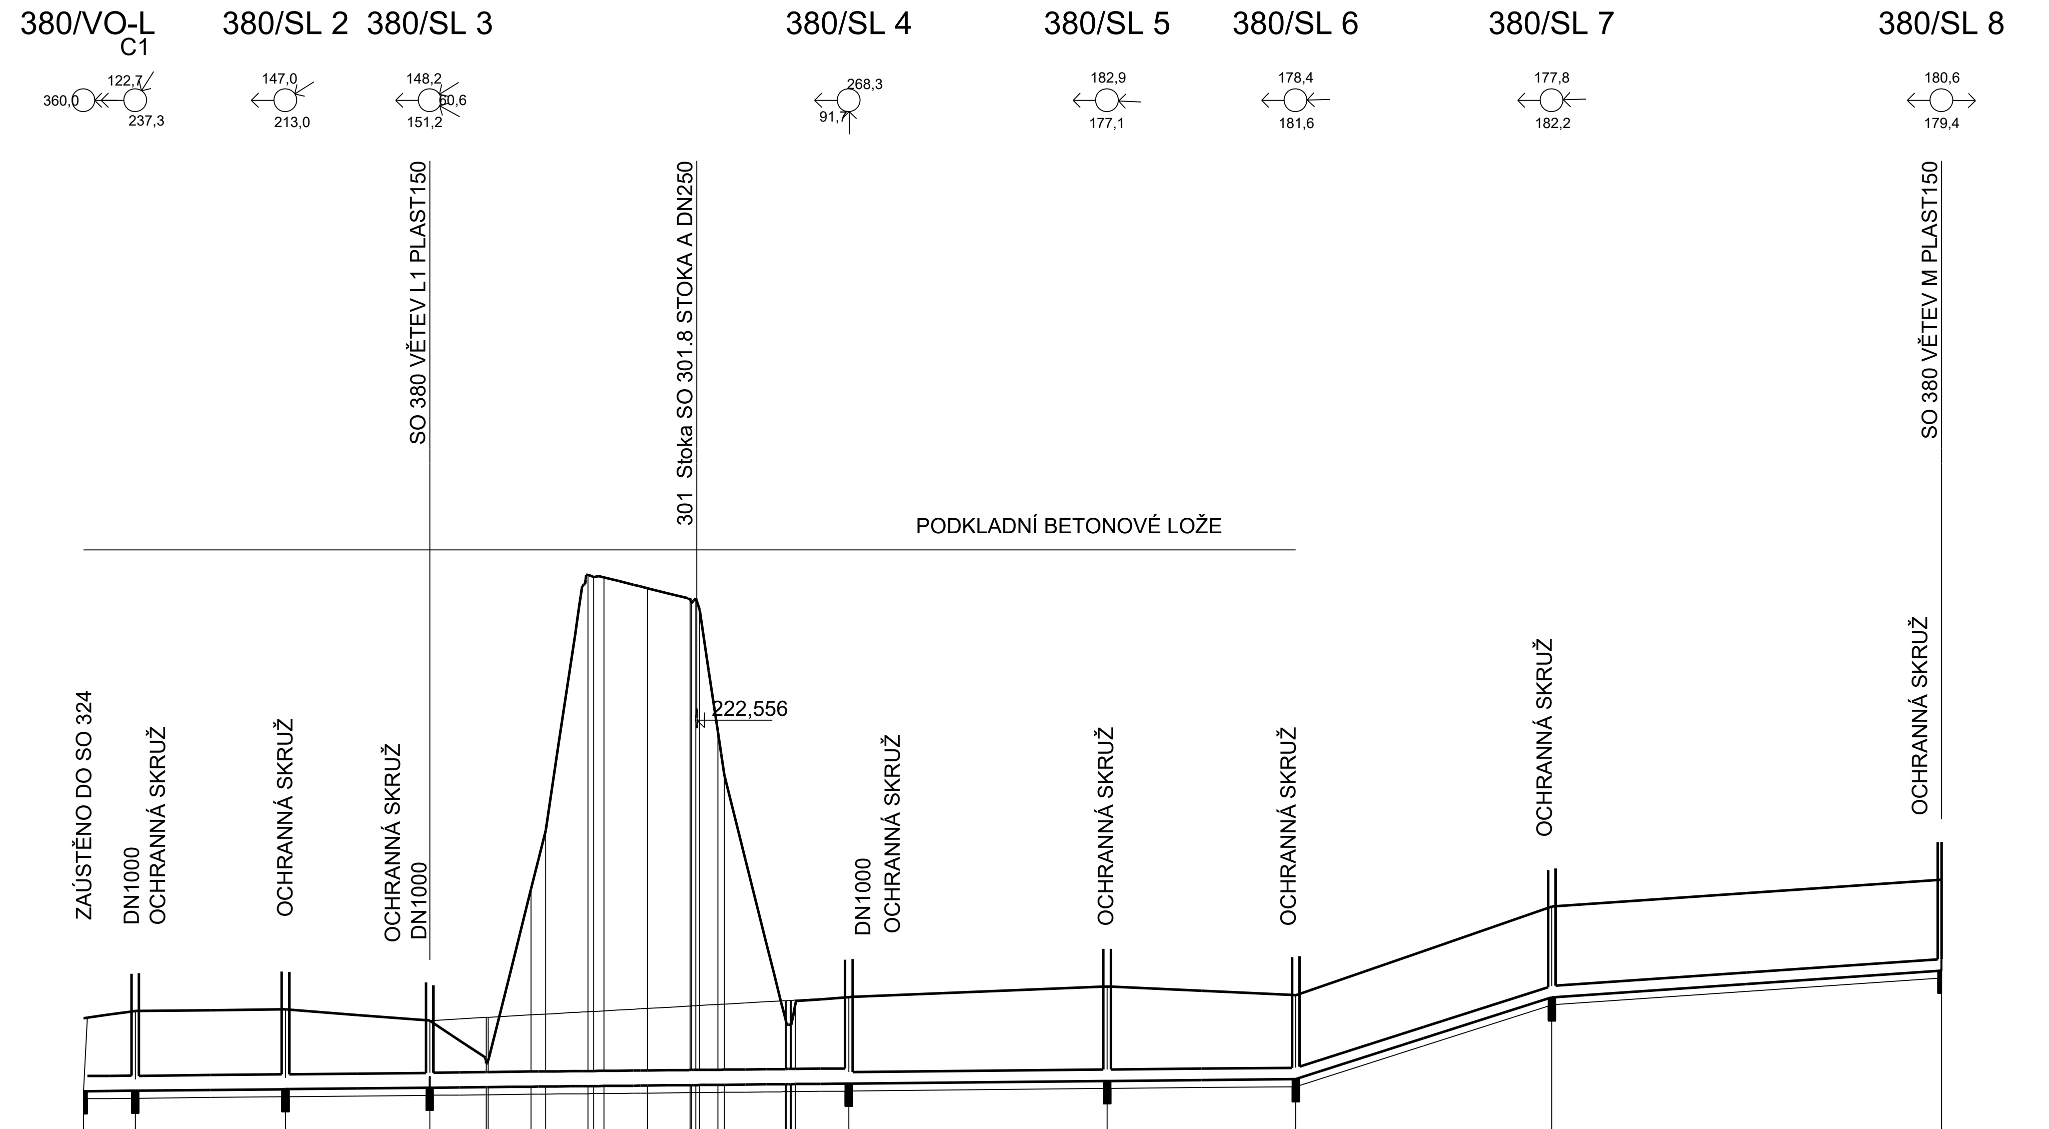
380/VO-L
C1
360,0
122,7
237,3
380/SL 2
147,0
213,0
380/SL 3
148,2
60,6
151,2
380/SL 4
268,3
91,7
380/SL 5
182,9
177,1
380/SL 6
178,4
181,6
380/SL 7
177,8
182,2
380/SL 8
180,6
179,4
SO 380 VĚTEV L1 PLAST150
301 Stoka SO 301.8 STOKA A DN250
SO 380 VĚTEV M PLAST150
PODKLADNÍ BETONOVÉ LOŽE
222,556
ZAÚSTĚNO DO SO 324
DN1000
OCHRANNÁ SKRUŽ
OCHRANNÁ SKRUŽ
OCHRANNÁ SKRUŽ
DN1000
DN1000
OCHRANNÁ SKRUŽ
OCHRANNÁ SKRUŽ
OCHRANNÁ SKRUŽ
OCHRANNÁ SKRUŽ
OCHRANNÁ SKRUŽ

KÓTA UPRAVENÉHO TERÉNU	217,75	218,81	218,83	218,68																				218,99	219,13	219,02	220,19	220,55
HLOUBKA VÝKOPU	0,00	1,15	1,15	0,99	0,41	0,45	2,72	3,48	6,86	6,86	6,83	6,68	6,53	6,53	6,43	6,38	4,77	4,19	0,96	0,89	0,89	0,89	1,16	1,24	1,35	1,21	1,30	1,30
HLOUBKA DNA POTRUBÍ	0,00	1,05	1,05	0,89	0,31	0,35	2,62	3,38	6,76	6,76	6,73	6,58	6,43	6,43	6,33	6,28	4,67	4,09	0,86	0,79	0,79	0,79	1,06	1,14	1,25	1,11	1,20	1,20
KÓTA DNA POTRUBÍ	217,75	217,76	217,78	217,8	217,8	217,8	217,81	217,81	217,82	217,82	217,82	217,82	217,83	217,83	217,83	217,83	217,83	217,83	217,84	217,84	217,84	217,84	217,84	217,85	217,89	217,91	218,99	219,35
KÓTA PŮVODNÍHO TERÉNU	218,72	218,81	218,83	218,68																				218,99	219,13	219,02	220,19	220,55
STANIČENÍ [m]	0,00	6,85	26,71	45,80	53,28	53,53	59,20	61,13	66,74	67,46	68,83	74,59	80,23	80,37	80,98	81,48	83,90	84,76	92,82	93,01	93,46	93,61	94,15	101,21	135,39	160,32	194,19	245,71

STANIČENÍ[km] 208,0 0,0 0,1 0,2 208,0

SKLON (‰) - DÉLKA (m)	1,0		160,32	31,9 33,86	6,9 51,52
PROFIL (mm) - MATERIÁL - DÉLKA (m)	200 PLAST SN16 45,80	250 PLAST SN16 55,41	150	PLAST	144,50
KAPACITNÍ PRŮTOK (l/s) - RYCHLOST (m/s)	10,39 0,33	18,86 0,38	4,81 0,27	27,69 1,57	12,81 0,72

SKLON (‰) - DÉLKA (m)	
A1	4,0, 10,77

KAPACITNÍ PRŮTOK (l/s) - RYCHLOST (m/s)	
B1	9,73, 0,55

OZNAČENÍ ŠACHET

SMĚROVÉ POMĚRY

380 VĚTEV L1

[1:1000/100]

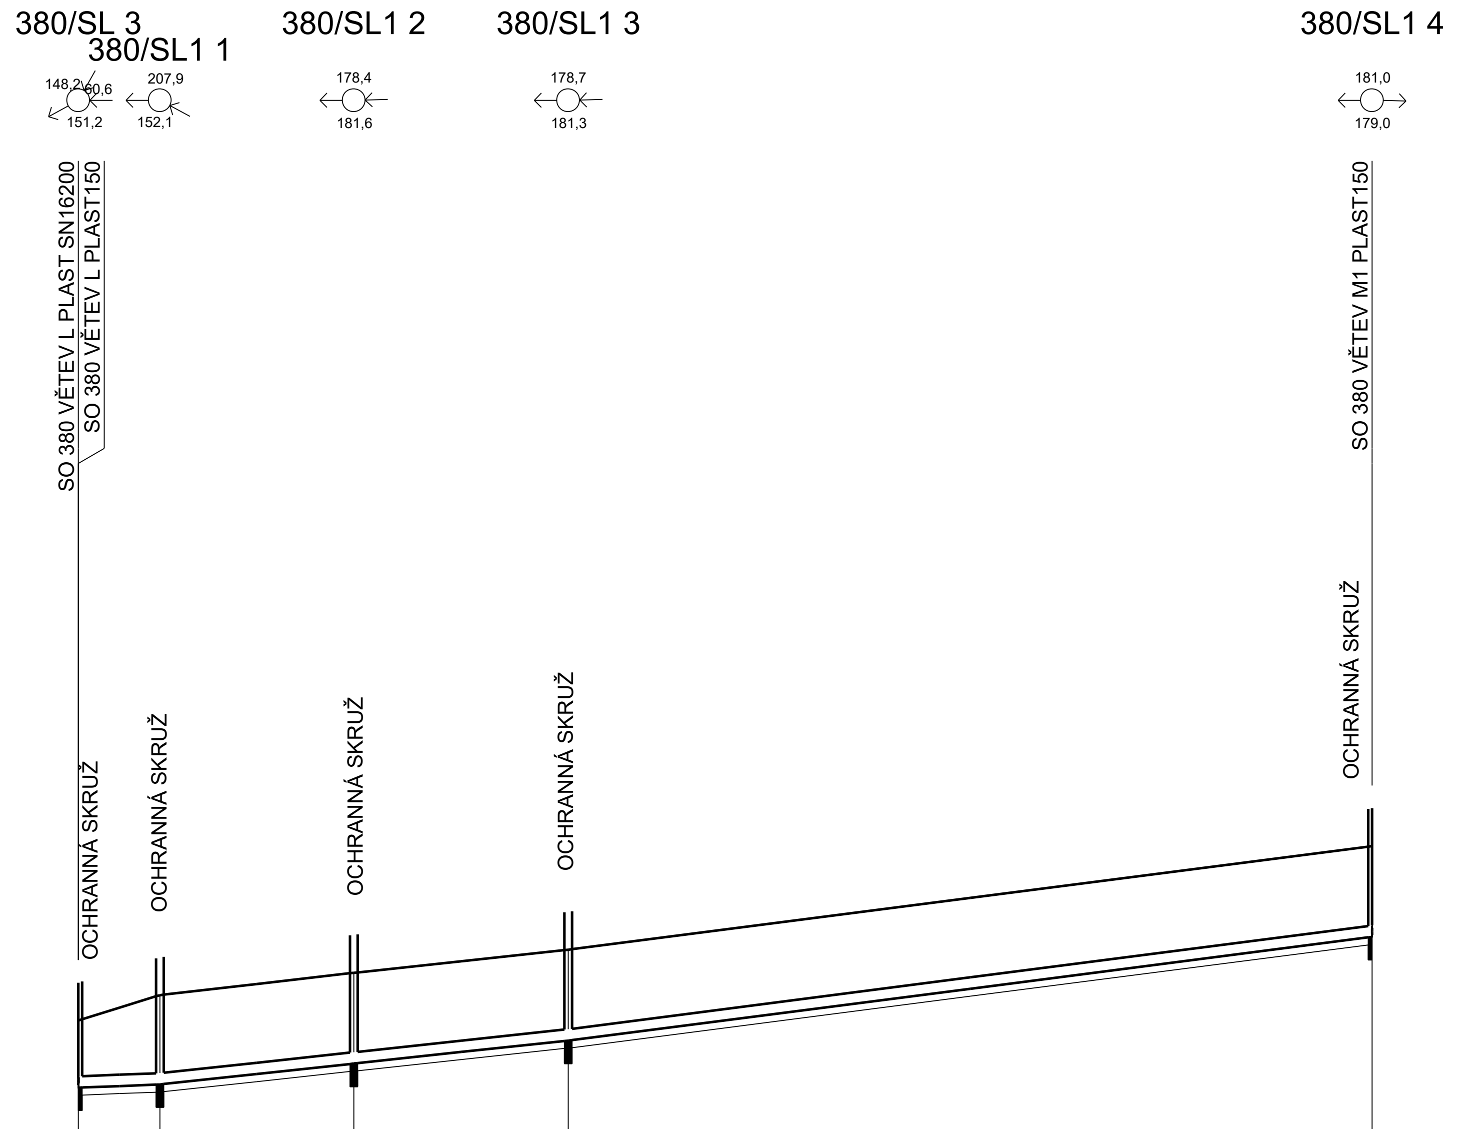
380/SL 3
380/SL1 1
148,2
60,6
151,2
207,9
152,1
380/SL1 2
178,4
181,6
380/SL1 3
178,7
181,3
380/SL1 4
181,0
179,0
SO 380 VĚTEV L PLAST SN16200
SO 380 VĚTEV L PLAST150
SO 380 VĚTEV M1 PLAST150
OCHRANNÁ SKRUŽ
OCHRANNÁ SKRUŽ
OCHRANNÁ SKRUŽ
OCHRANNÁ SKRUŽ
OCHRANNÁ SKRUŽ

KÓTA UPRAVENÉHO TERÉNU	218,68	219,02	219,32	219,62	220,99
HLOUBKA VÝKOPU	0,99	1,28	1,30	1,30	1,30
HLOUBKA DNA POTRUBÍ	0,89	1,18	1,20	1,20	1,20
KÓTA DNA POTRUBÍ	217,8	217,84	218,12	218,42	219,79
KÓTA PŮVODNÍHO TERÉNU	218,68	219,02	219,32	219,62	220,99
STANIČENÍ [m]	0,00	10,77	36,43	64,80	171,12

STANIČENÍ[km] 208,0 0,0 0,1 208,0

SKLON (‰) - DÉLKA (m)	A1	10,8 25,65	10,7 28,37	12,9 106,32
PROFIL (mm) - MATERIÁL - DÉLKA (m)	150		PLAST	171,12
KAPACITNÍ PRŮTOK (l/s) - RYCHLOST (m/s)	B1	16,05 0,91	16,01 0,91	17,56 0,99

Souřadnicový systém: S-JTSK
Výškový systém: Bpv

SO 380 Úpravy meliorací

Objednatel:

Ředitelství silnic a dálnic s. p.
Čerčanská 2023/12, Krč, 140 00 Praha 4

Zhotovitel:

Valbek, spol. s r.o.
Vaňurova 505/17
460 07 Liberec 3

Vypracoval	ING. J. VANCL		**Zak. číslo**	**21-LI13-001**
Zodp. projektant	ING. J. VANCL		**Datum**	**02/2025**
Tech. kontrola	ING. D. LANDA		**Stupeň**	**PDPS**
Akce	**I/16 MLADÁ BOLESLAV - MARTINOVICE**		**Počet formátů**	**5 x A4**
			Měřítko	**1 : 1000/100**
			Č. přílohy	**Paré**
Příloha	PODÉLNÝ PROFIL Č. 12 - VĚTEV L, L1		**3.12**	

Zhotovitel:
Valbek, spol. s r.o.
Vaňurova 505/17
460 07 Liberec 3