
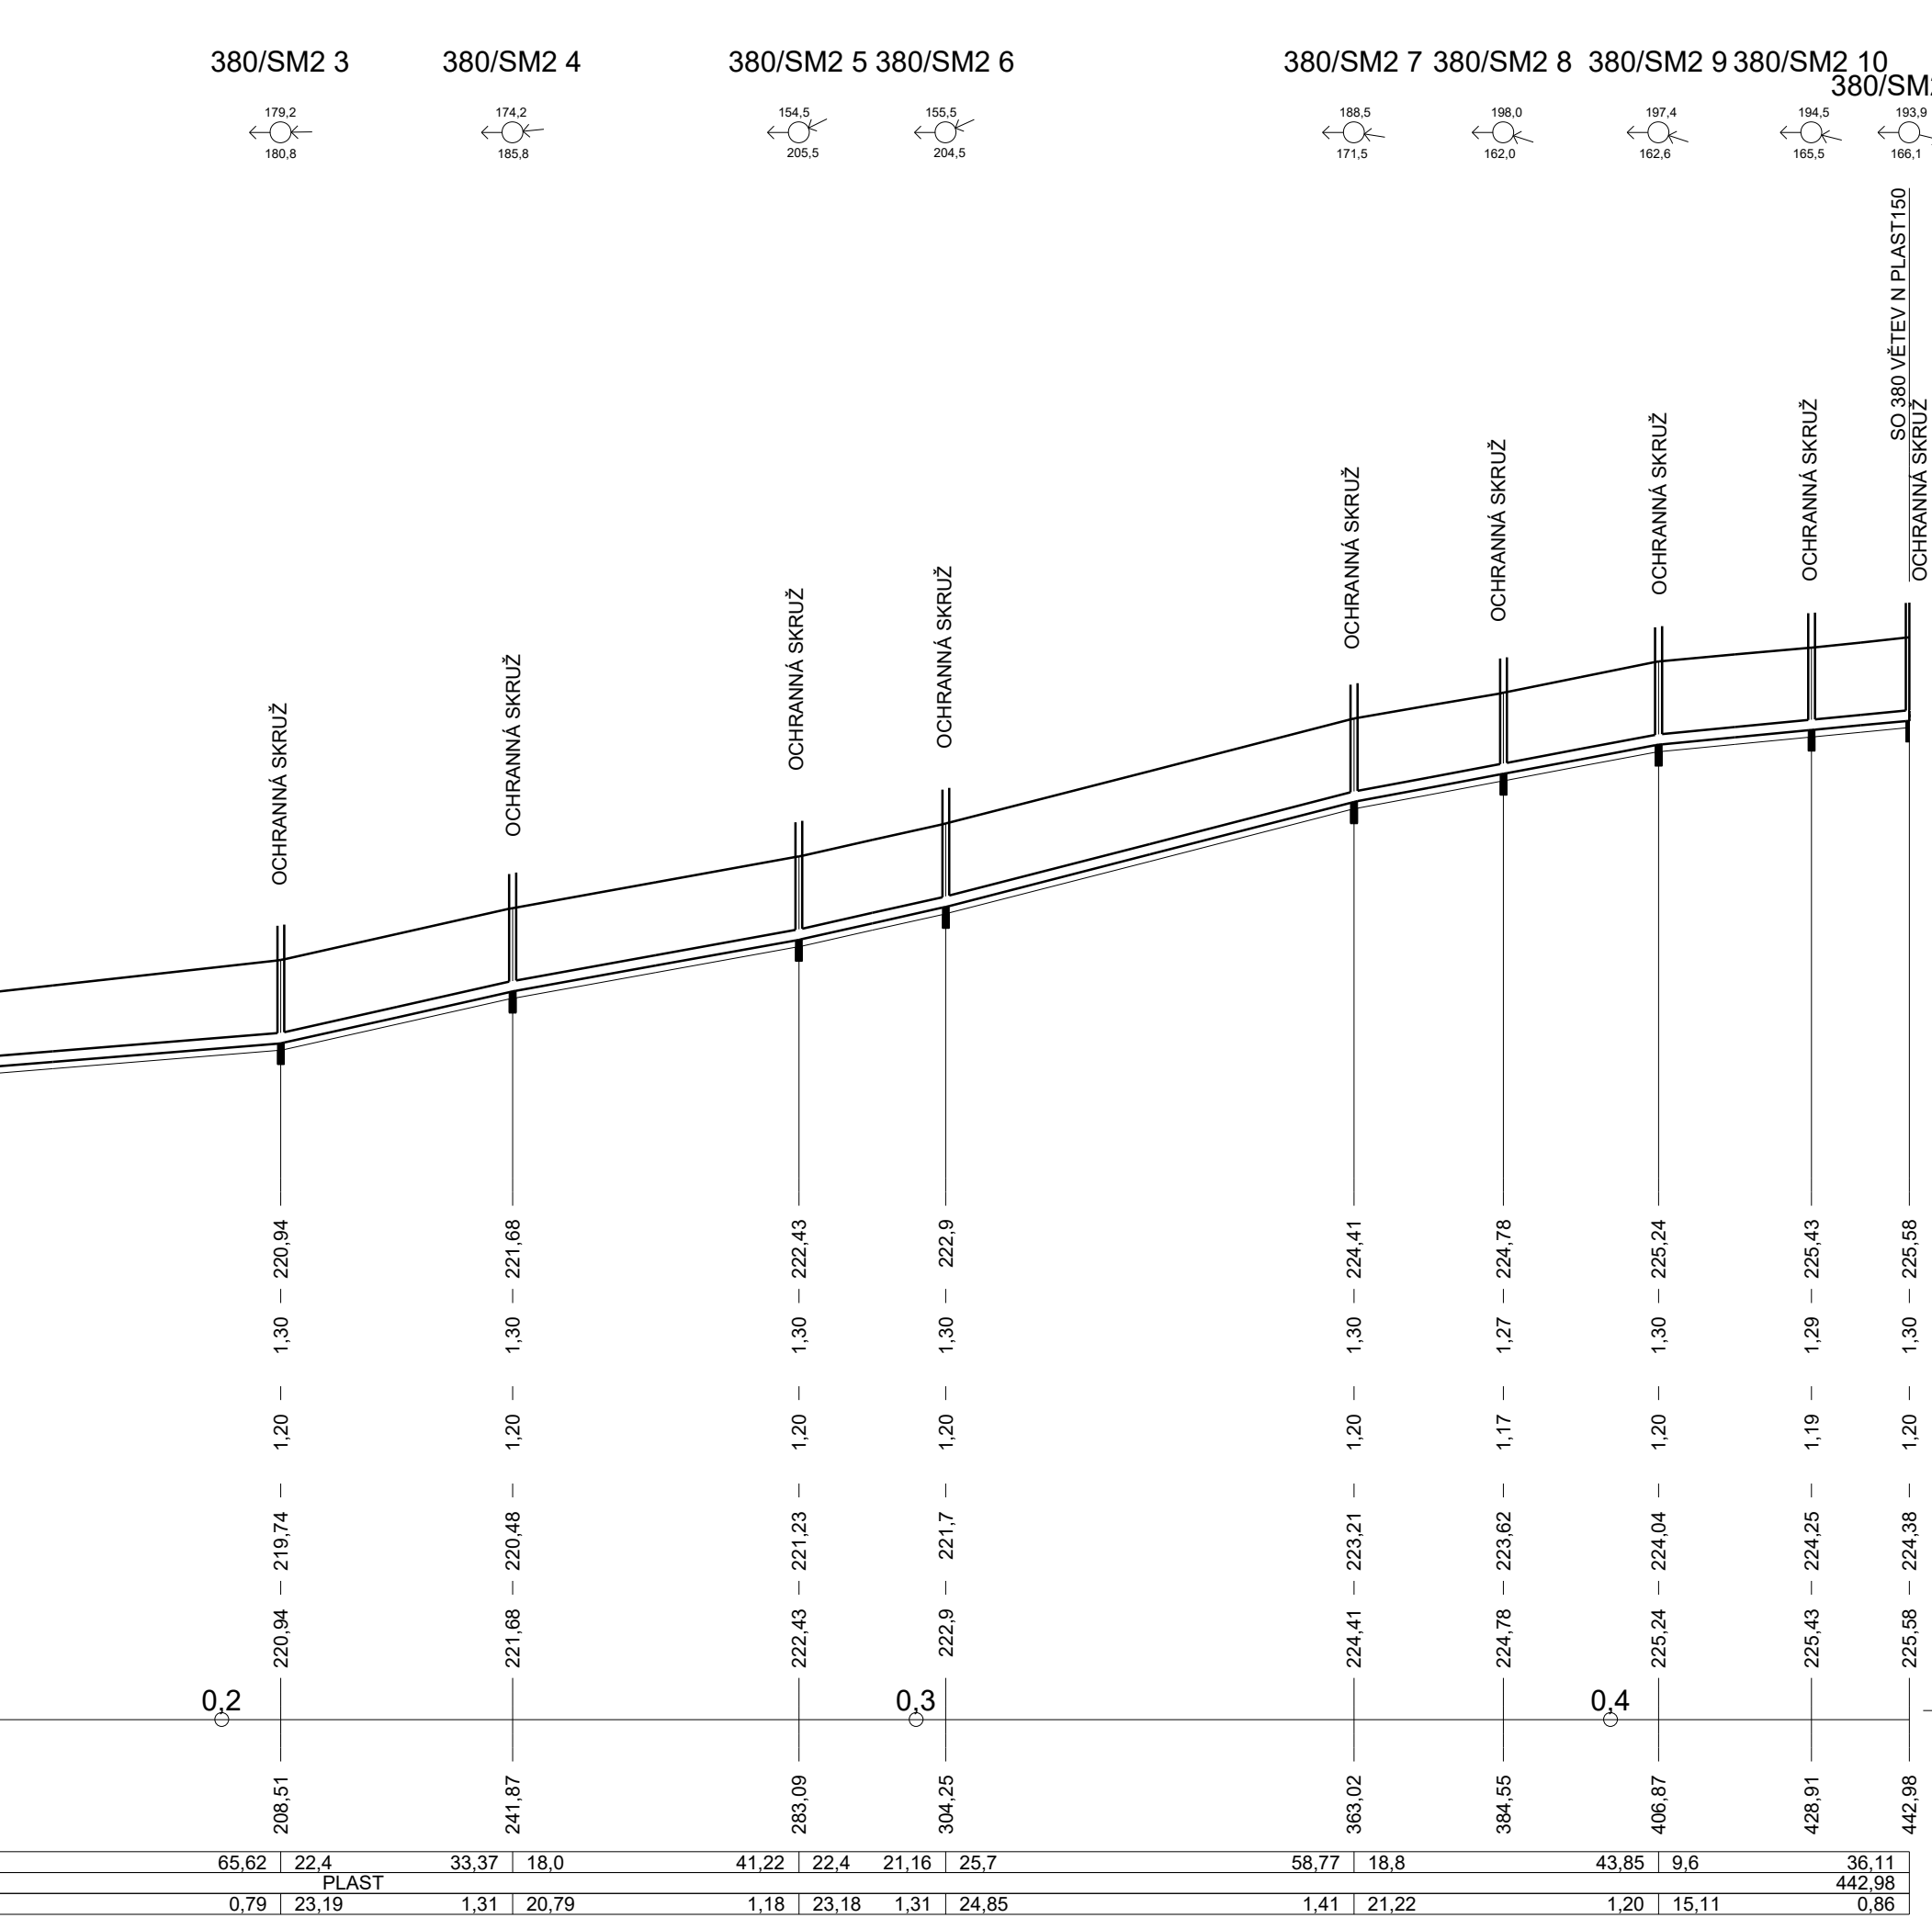
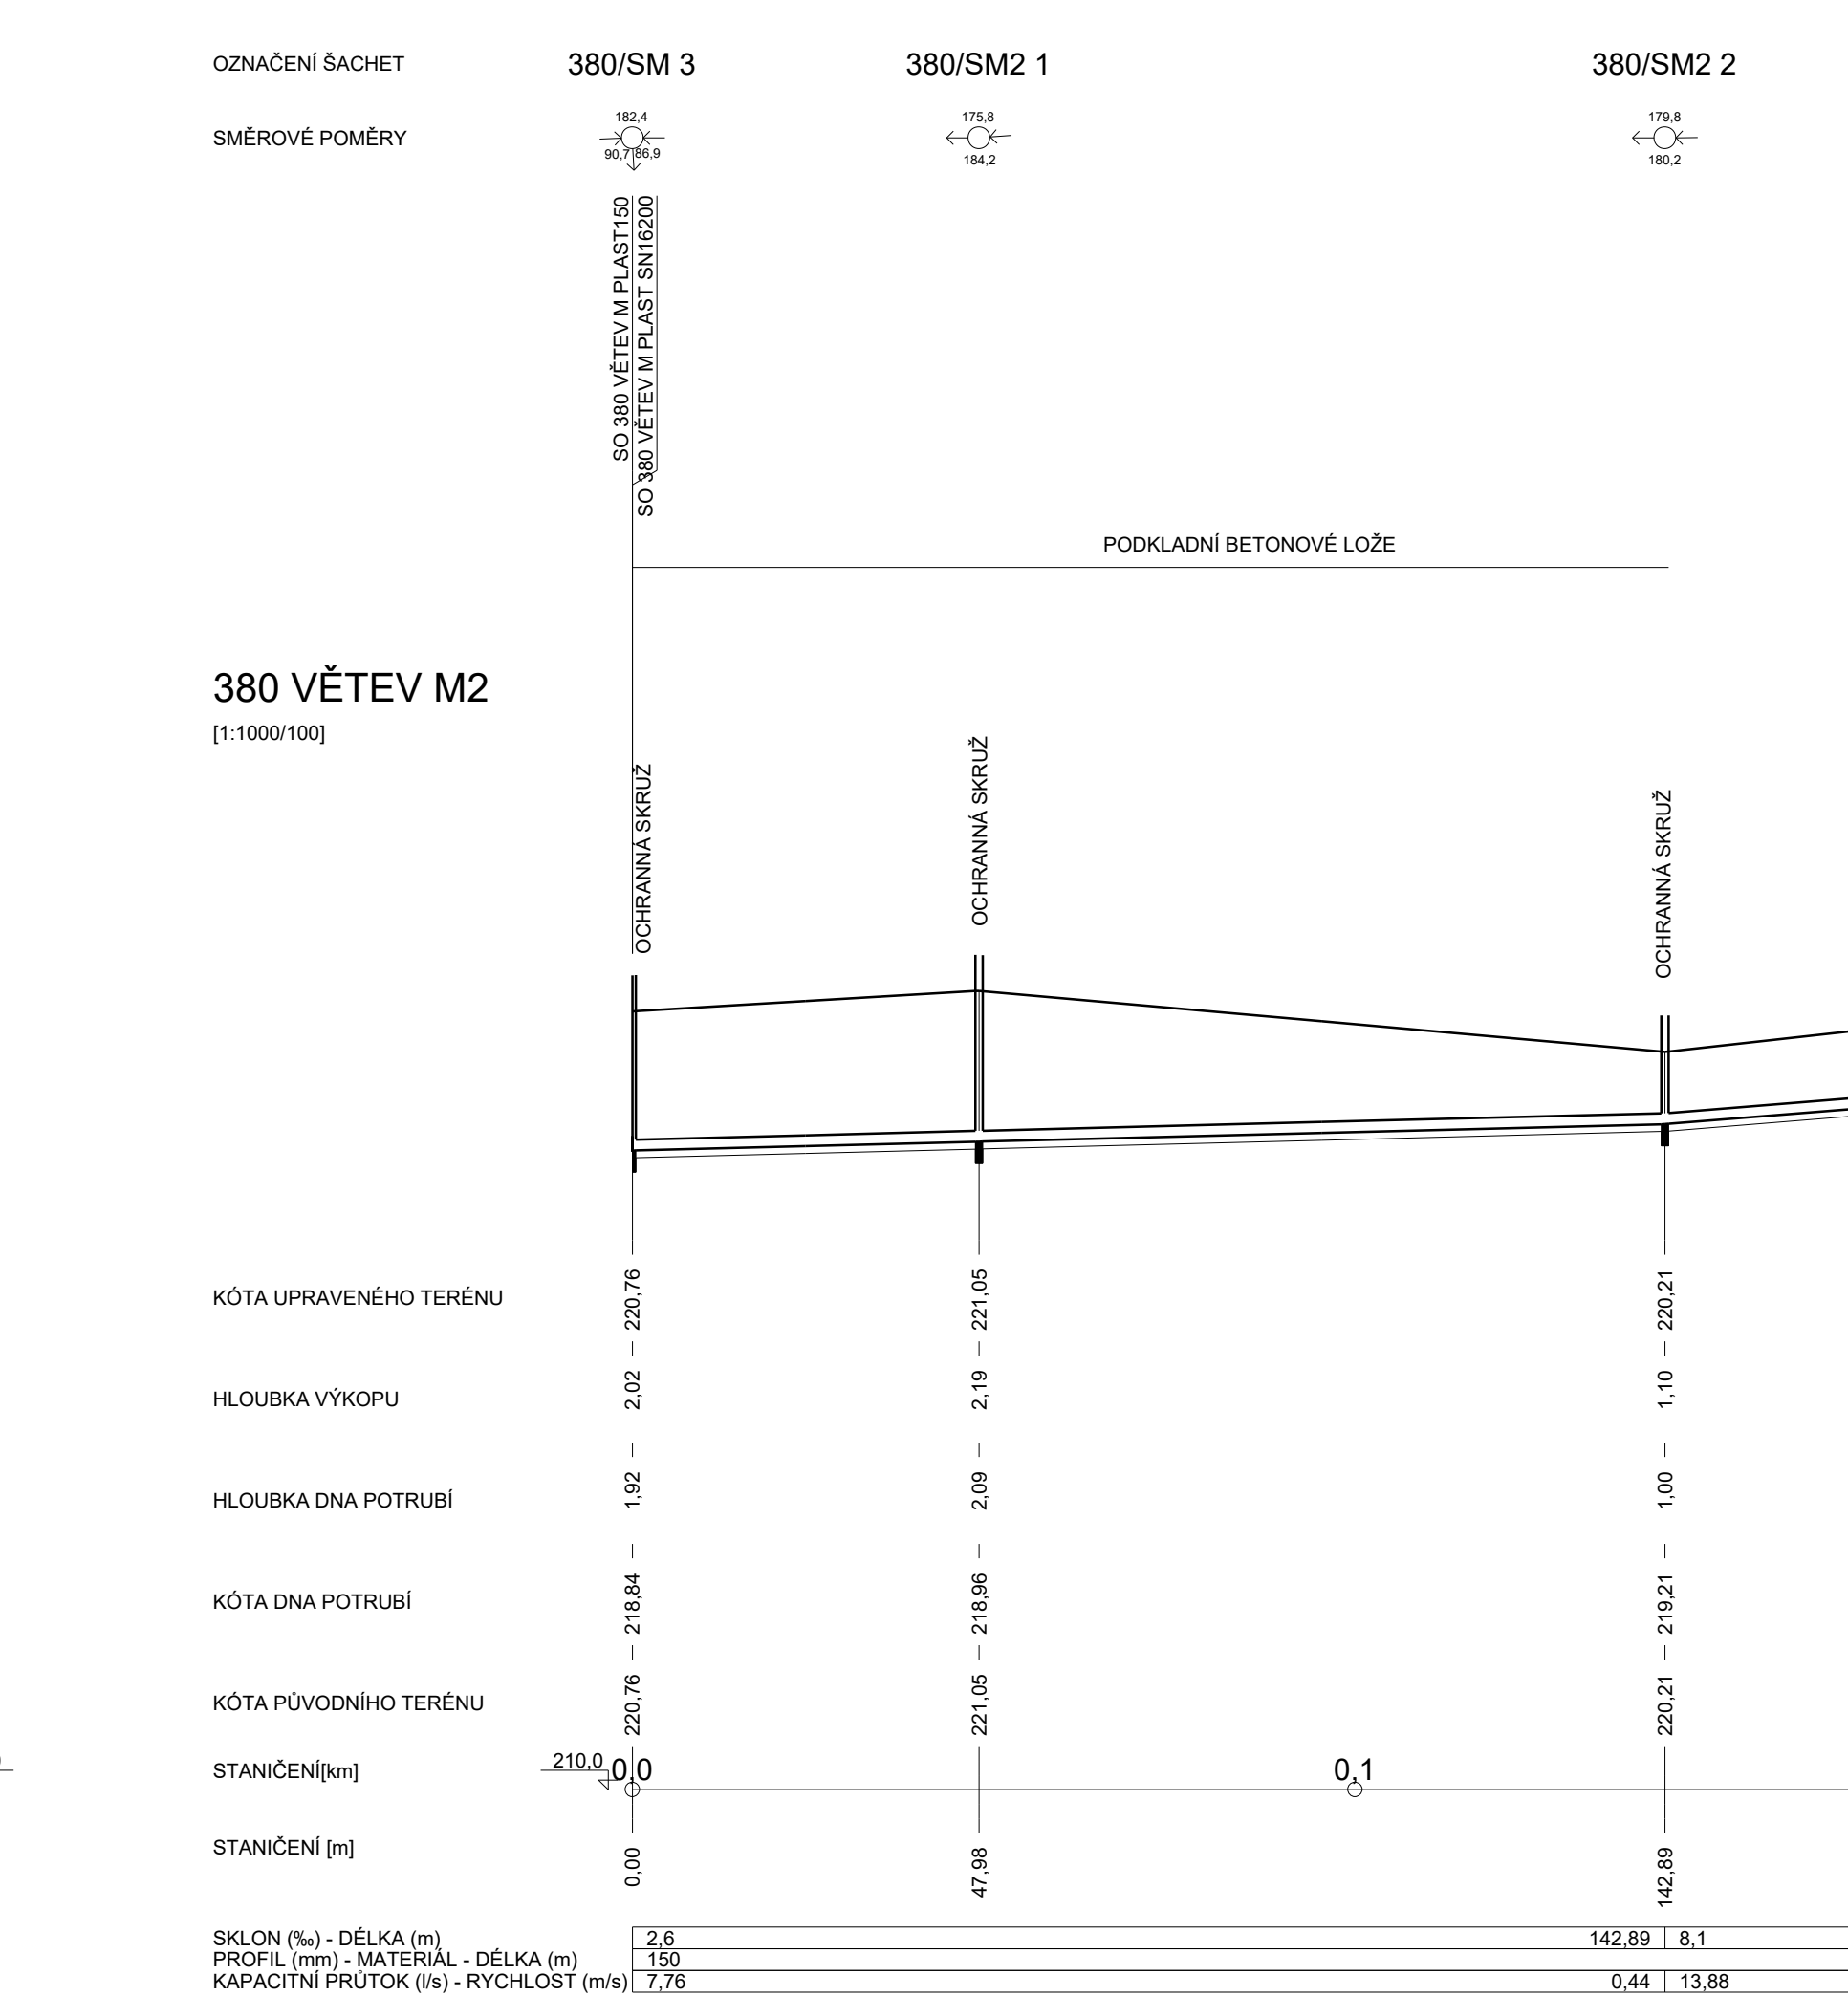
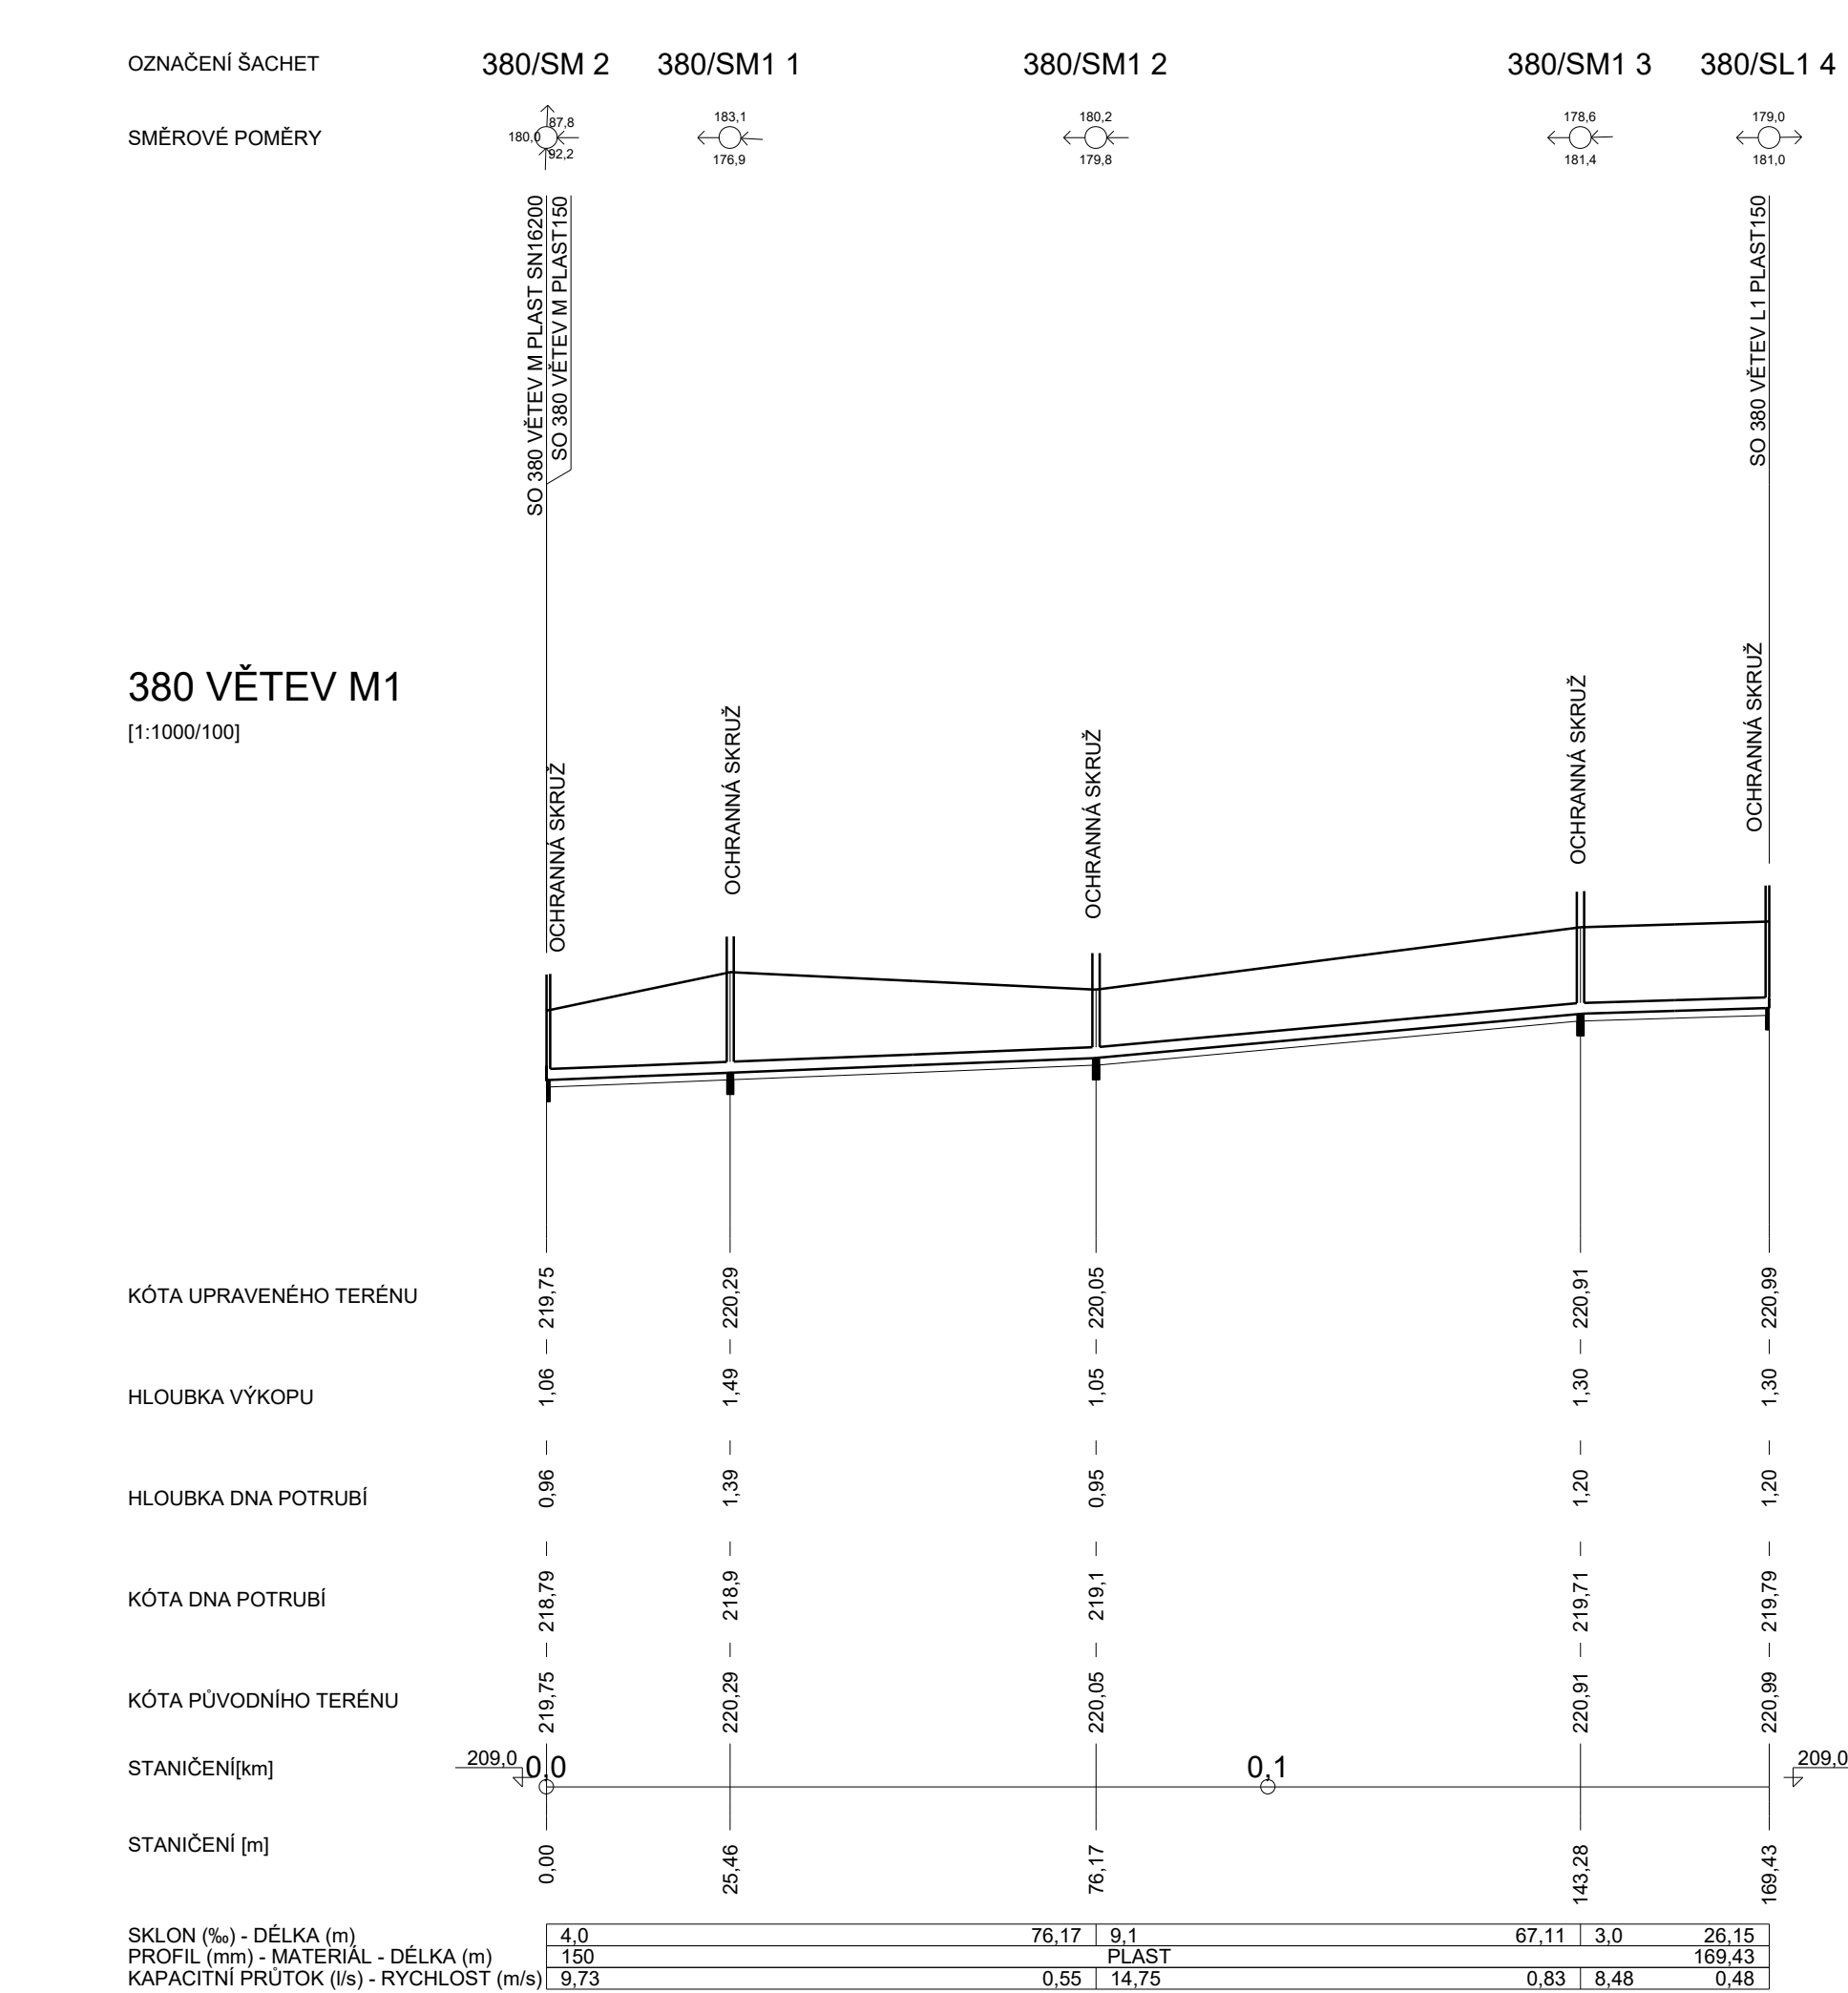


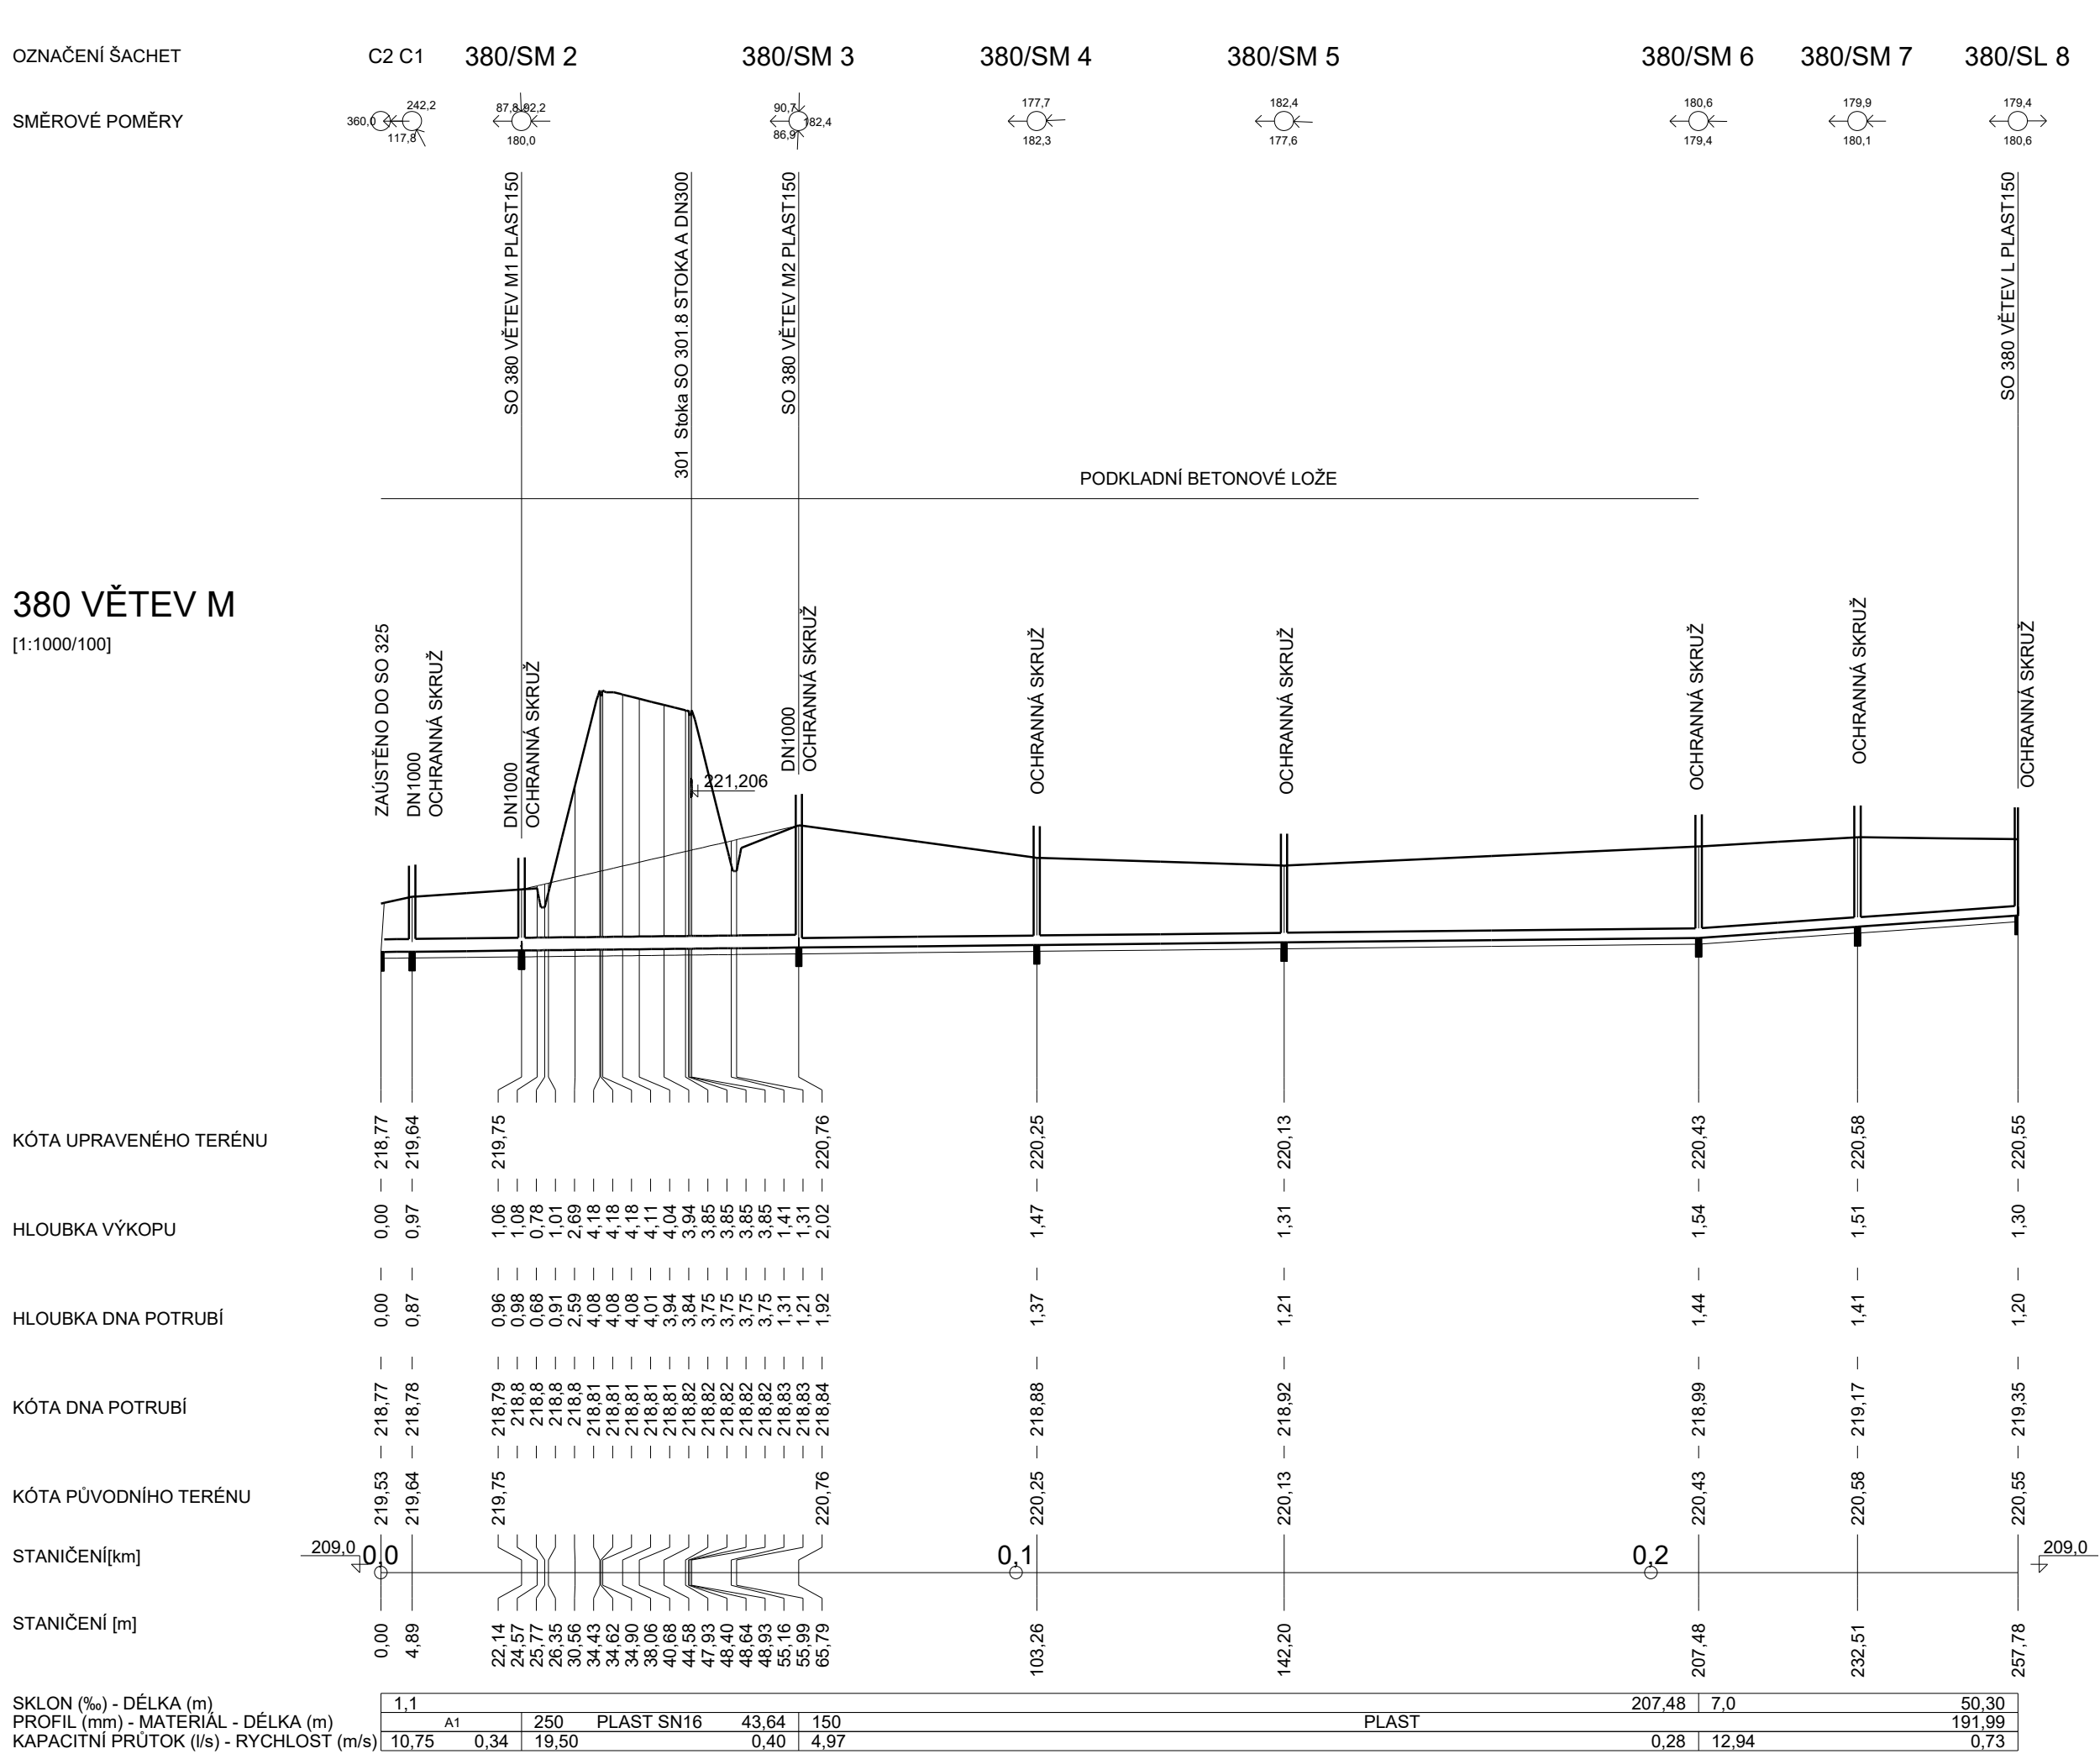

Souřadnicový systém: S-JTSK. Výškový systém: Bpv. SO 380 Úpravy meliorací. Ředitelství silnic a dálnic s. p. Čerčanská 2023/12, Krč, 140 00 Praha 4. Zhotovitel: Valbek, spol. s r.o. Vaňurova 505/17, 460 07 Liberec 3. Valbek. I/16 MLADÁ BOLESLAV - MARTINOVICE. Podélný profil č. 13 - Větev M, M1, M2. Zak. číslo: 21-L113-001. Datum: 02/2025. Stupeň: PDPS. Počet formátů: 8 x A4. Měřítko: 1 : 1000/100. Č. přílohy: Paré. 3.13.