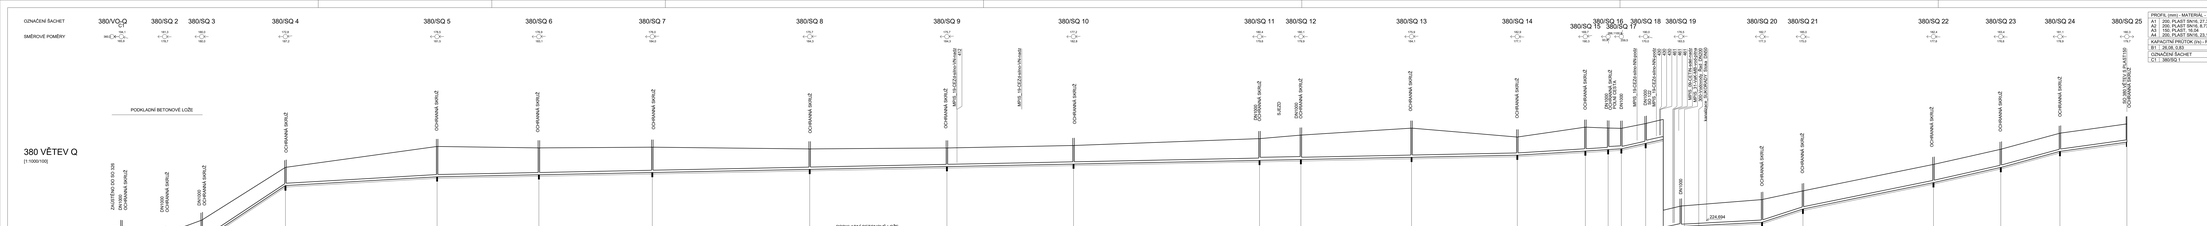
OZNAČENÍ ŠACHET
SMĚROVÉ POMĚRY
380/VO-Q
380/SQ 2
380/SQ 3
380/SQ 4
380/SQ 5
380/SQ 6
380/SQ 7
380/SQ 8
380/SQ 9
380/SQ 10
380/SQ 11
380/SQ 12
380/SQ 13
380/SQ 14
380/SQ 15
380/SQ 16
380/SQ 17
380/SQ 18
380/SQ 19
380/SQ 20
380/SQ 21
380/SQ 22
380/SQ 23
380/SQ 24
380/SQ 25
PODKLADNÍ BETONOVÉ LOŽE
380 VĚTEV Q
[1:1000/100]
KOTA UPRAVENÉHO TERÉNU
HLOUBKA VÝKOPU
HLOUBKA DNA POTRUBÍ
KÓTA DNA POTRUBÍ
KÓTA PŮVODNÍHO TERÉNU
STANIČENÍ[km]
STANIČENÍ[m]
SKLON (%) - DÉLKA (m)
PROFIL (mm) - MATERIÁL - DÉLKA (m)
KAPACITNÍ PRŮTOK (l/s) - RYCHLOST (m/s)
PLAST
PROFIL (mm) - MATERIÁL - DÉLKA (m)
A1 - 250, PLAST, BN/8, 6,73
A2 - 250, PLAST, BN/8, 6,73
A3 - 160, PLAST, 16,04
A4 - 250, PLAST, BN/8, 23,17
KAPACITNÍ PRŮTOK (l/s) - RYCHLOST (m/s)
B1 - 26,08; 0,93
OZNAČENÍ ŠACHET
C1 - 380/SQ.1
Souřadnicový systém: S-JTSK
Výškový systém: Bpv
SO 380 Úpravy meliorací
Objednatel:
ŘEDITELSTVÍ SILNIC A DÁLNIC
Ředitelství silnic a dálnic s. p.
Čerťanská 2023/12, Kvč, 140 00 Praha 4
Zhotovitel:
Valbek, spol. s r.o.
Vařurova 505/17
460 07 Liberec 3
Vypracoval: ING. J. VANCL
Zodp. projektant: ING. J. VANCL
Tech. kontrola: ING. D. LANDA
Akce
I/16 MLADÁ BOLESLAV - MARTINOVICE
Zhotovitel:
Valbek, spol. s r.o.
Vařurova 505/17
460 07 Liberec 3
Příloha
PODÉLNÝ PROFIL Č. 17 - VĚTEV Q
Zak. číslo: 31-U13-001
Datum: 02/2015
Stupeň: PDPS
Počet formátů: 5 x A4
Měřítko: 1 : 1000/100
Č. přílohy: 3.17
Paré: