

OZNAČENÍ ŠACHET

SMĚROVÉ POMĚRY

380/VO-A

380/SA 1

380/SA 2


380/SA 3

380/SA 4

380/SA 5

380/SA 6

380/SA 7

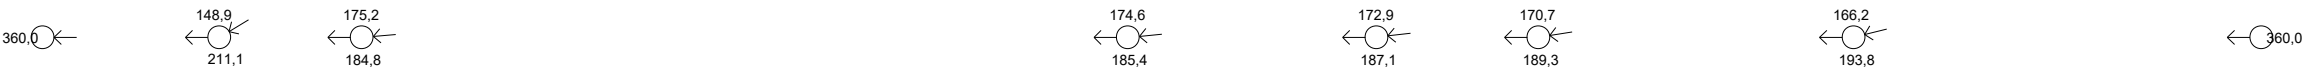

MPIS_31-Vak-MB-kan-jednot
PREKLADA SE
vytlak HORNÍ STAKORY Rad DN160
300-Vodovody Rad DN160
MPIS_19-CEZd-silno-VN-nařz

SO 123

DN1000
OCHRANNÁ SKRUŽ

OCHRANNÁ SKRUŽ

OCHRANNÁ SKRUŽ

OCHRANNÁ SKRUŽ

OCHRANNÁ SKRUŽ

OCHRANNÁ SKRUŽ

OCHRANNÁ SKRUŽ

380 VĚTEV A

[1:1000/100]

ZAÚSTĚNO DO SO 320

PODKLADNÍ BETONOVÉ LOŽE

211,046

211,228

KÓTA UPRAVENÉHO TERÉNU

HLOUBKA VÝKOPU

HLOUBKA DNA POTRUBÍ

KÓTA DNA POTRUBÍ

KÓTA PŮVODNÍHO TERÉNU

STANIČENÍ[km]

STANIČENÍ [m]

SKLON (‰) - DÉLKA (m)
PROFIL (mm) - MATERIÁL - DÉLKA (m)
KAPACITNÍ PRŮTOK (l/s) - RYCHLOST (m/s)

0,3			293,43
A1	150		270,07
5,61	0,18	2,59	0,15
PLAST			

PROFIL (mm) - MATERIÁL - DÉLKA (m)
A1 200, PLAST SN16, 23,36

Souřadnicový systém: S-JTSK
Výškový systém: BpV

SO 380 Úpravy meliorací

Objednatel:



ŘEDITELSTVÍ
SILNIC
A DÁLNIC

Ředitelství silnic a dálnic s. p.
Čerčanská 2023/12, Krč, 140 00 Praha 4

Zhotovitel:



Valbek, spol. s r.o.
Vaňurova 505/17
460 07 Liberec 3



Vypracoval
Zodp. projektant
Tech. kontrola

ING. J. VANCL
ING. J. VANCL
ING. D. LANDA

Zak. číslo
Datum
Stupeň

21-LI13-001
02/2025
PDPS

Akce
I/16 MLADÁ BOLESLAV - MARTINOVICE

Počet formátů
Měřítko
Č. přílohy

3 x A4
1 : 1000/100
Paré

Zhotovitel:
Valbek, spol. s r.o.
Vaňurova 505/17
460 07 Liberec 3

Příloha
PODÉLNÝ PROFIL Č. 1 - VĚTEV A

3.1