



OZNAČENÍ ŠACHET

SMĚROVÉ POMĚRY


380/VO-X
380/SX 1

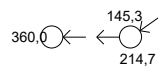

380/SX 2 3
380/SX 3

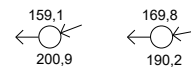

380/SX 4 380/SX 6
3 380/SX 5

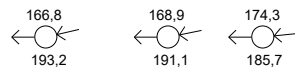


380/SX 7




380/SX 8



8 380/SX 10
380/SX 9 3

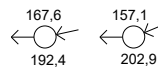

380/SX 10
SX 9 380/SX 11

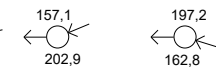


380/SW 3



SKLON (‰) - DĚLKA (m)	
A1	4,0, 10,42
PROFIL (mm) - MATERIÁL - DĚLKA (m)	
B1	200, PLAST SN16, 10,42
KAPACITNÍ PRŮTOK (l/s) - RYCHLOST (m/s)	
C1	20,99, 0,67

380 VĚTEV X

[1:1000/100]

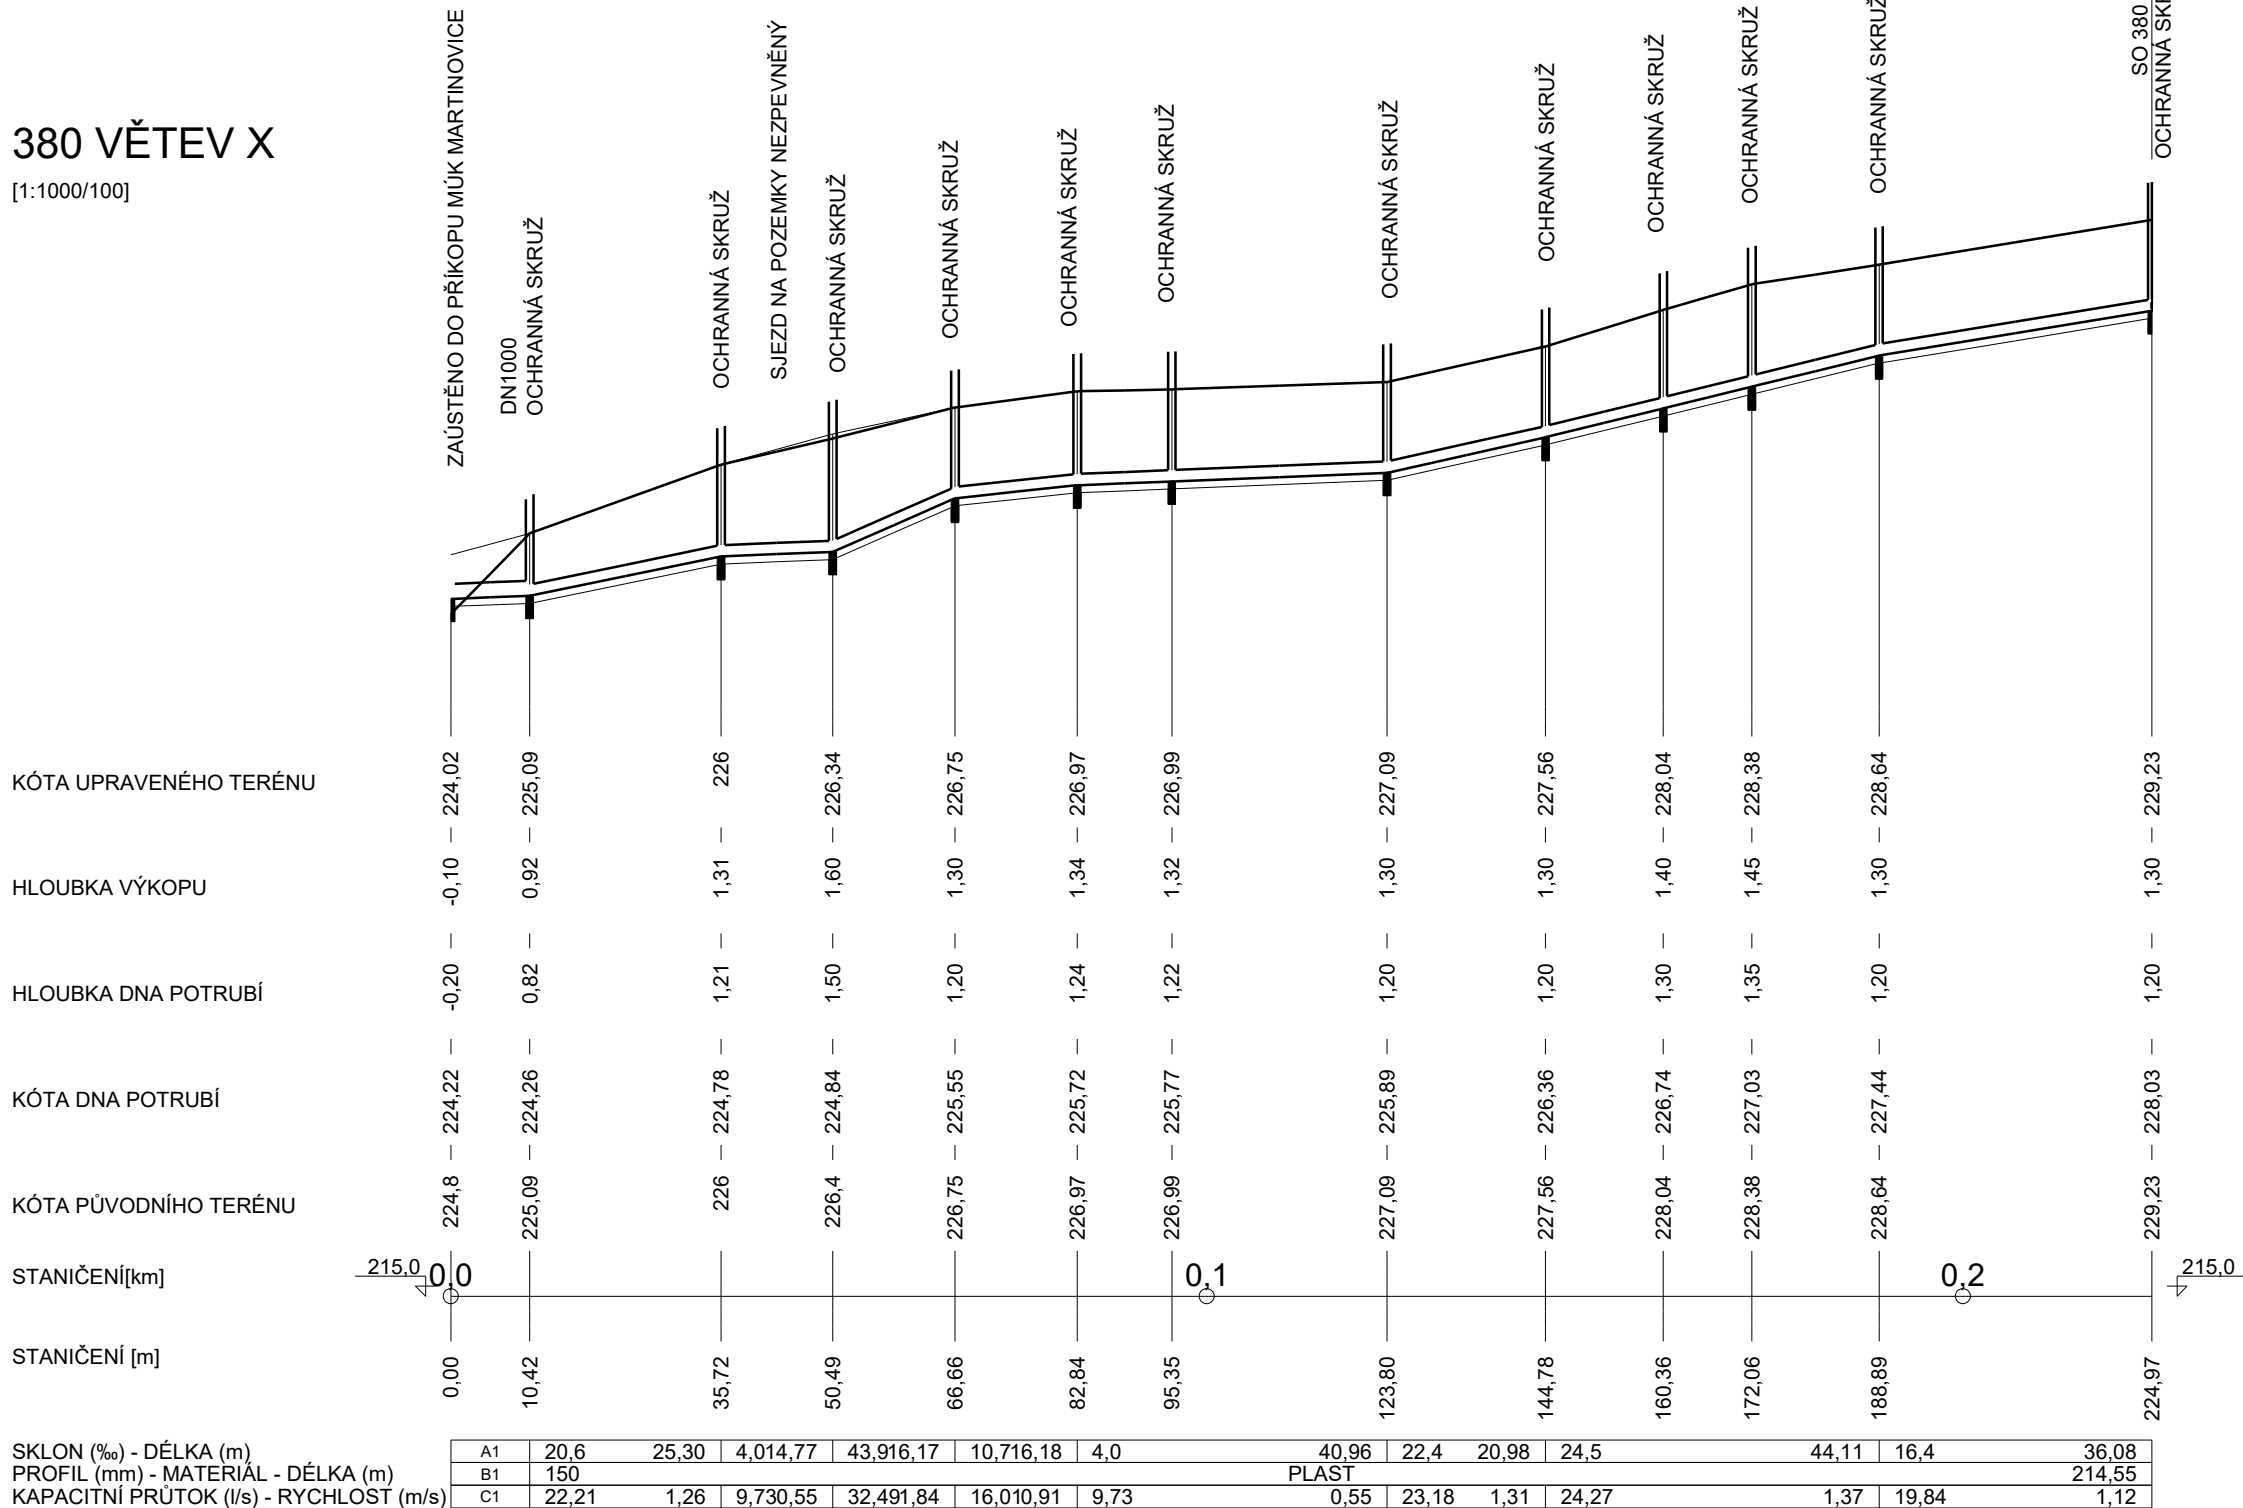

Souřadnicový systém: S-JTSK

Výškový systém: Bpv

SO 380 Úpravy meliorací

Objednatel:

ŘEDITELSTVÍ SILNIC A DÁLNIC

Ředitelství silnic a dálnic s. p.

Čerčanská 2023/12, Krč, 140 00 Praha 4

Zhotovitel:

**Valbek, spol. s r.o.**

Vaňurova 505/17
460 07 Liberec 3



Vypracoval	ING. J. VANCL		Zak. číslo	21-LI13-001
Zodp. projektant	ING. J. VANCL		Datum	02/2025
Tech. kontrola	ING. D. LANDA		Stupeň	PDPS
AKCE I/16 MLADÁ BOLESLAV - MARTINOVICE			Počet formátů	3 x A4
			Měřítko	1 : 1000/100
			Č. přílohy	Paré
Příloha PODÉLNÝ PROFIL Č. 24 - VĚTEV X			3.24	