

OZNAČENÍ ŠACHET


SMĚROVÉ POMĚRY

380/VOZ

380/SZ 2 380/SZ 3

380/SZ 4

380/SZ 5 380/SZ 6

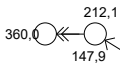

SKLON (‰) - DÉLKA (m)	
A1	29,1, 6,61
PROFIL (mm) - MATERIÁL - DÉLKA (m)	
B1	200, PLAST SN16, 6,61
KAPACITNÍ PRŮTOK (l/s) - RYCHLOST (m/s)	
C1	56,96, 1,81
OZNAČENÍ ŠACHET	
D1	380/SZ 1

380 VĚTEV Z

[1:1000/100]

KÓTA UPRAVENÉHO TERÉNU

HLOUBKA VÝKOPU

HLOUBKA DNA POTRUBÍ


KÓTA DNA POTRUBÍ

KÓTA PŮVODNÍHO TERÉNU

STANIČENÍ[km]

STANIČENÍ [m]

SKLON (‰) - DÉLKA (m)	A1	14,7	17,75	22,9	17,98	19,4	41,46	22,2	37,00	23,2	16,70
PROFIL (mm) - MATERIÁL - DÉLKA (m)	B1	150					PLAST				130,88
KAPACITNÍ PRŮTOK (l/s) - RYCHLOST (m/s)	C1	18,77	1,06	23,47	1,33	21,57	1,22	23,07	1,31	23,62	1,34

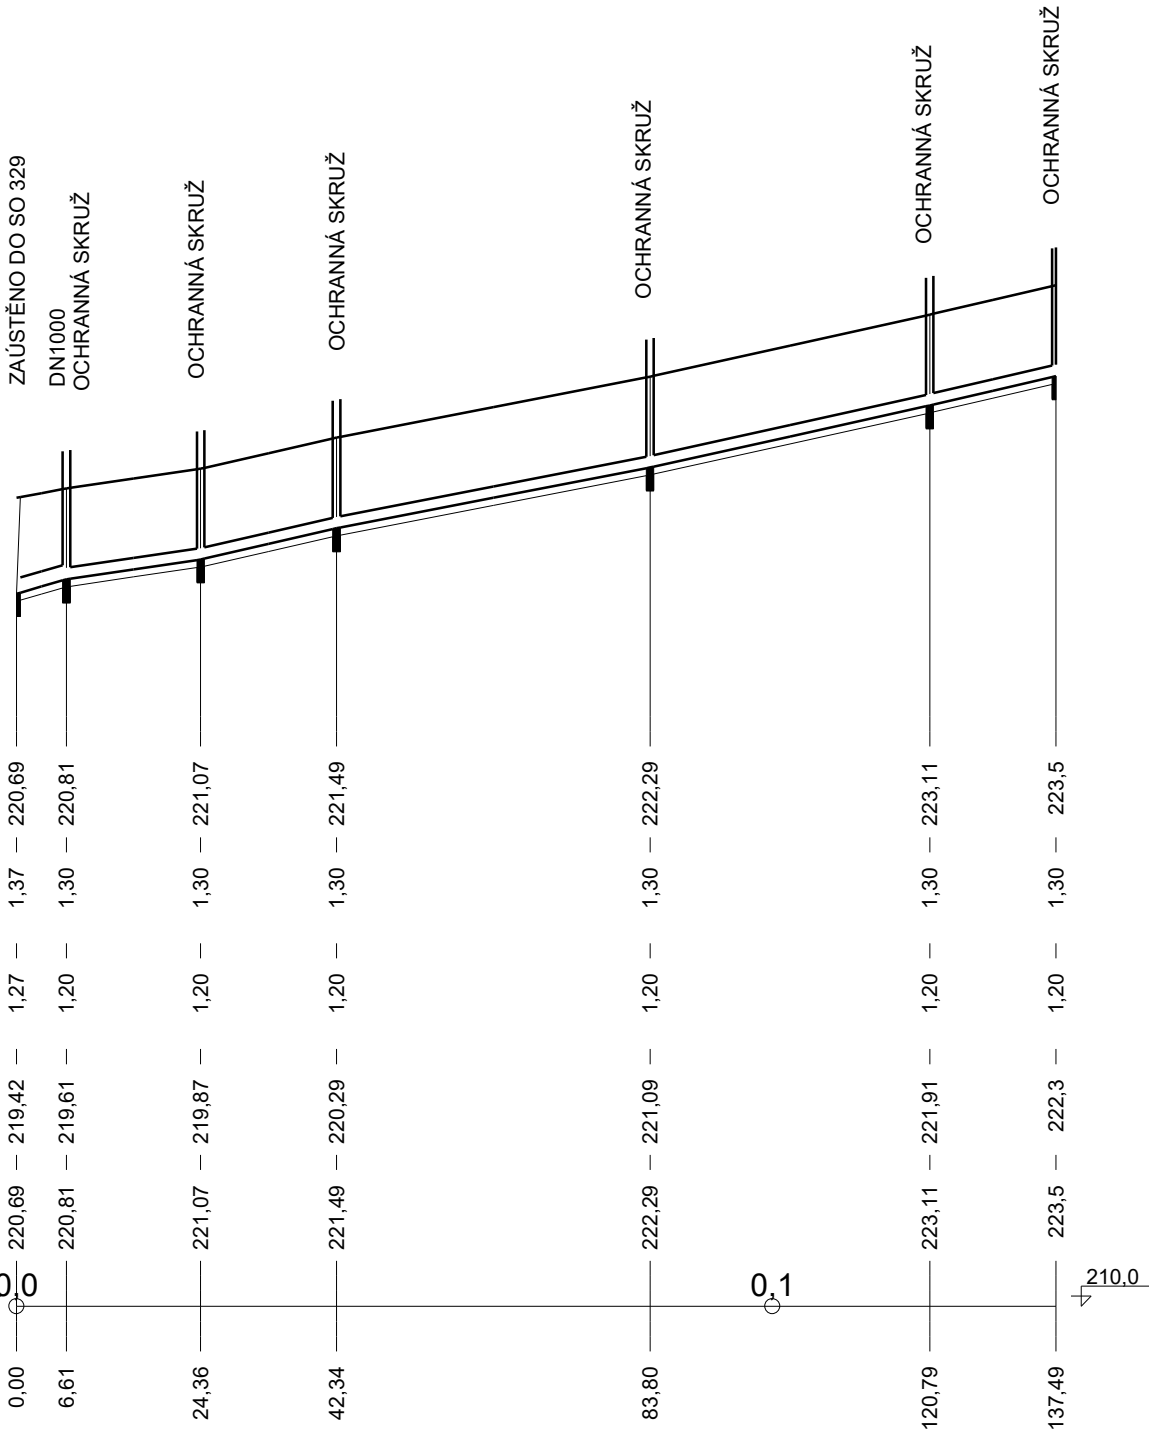

Souřadnicový systém: S-JTSK

Výškový systém: Bpv

SO 380 Úpravy meliorací

Objednatel:



ŘEDITELSTVÍ
SILNIC
A DÁLNIC

Ředitelství silnic a dálnic s. p.

Čerčanská 2023/12, Krč, 140 00 Praha 4

Zhotovitel:



Valbek, spol. s r.o.

Vaňurova 505/17

460 07 Liberec 3



Vypracoval
Zodp. projektant
Tech. kontrola

ING. J. VANCL

ING. J. VANCL

ING. D. LANDA

Akce
I/16 MLADÁ BOLESLAV - MARTINOVICE

Zak. číslo

21-LI13-001

Datum

02/2025

Stupeň

PDPS

Počet formátů

3 x A4

Měřítko

1 : 1000/100

Č. přílohy

Paré

Zhotovitel:

Valbek, spol. s r.o.

Vaňurova 505/17

460 07 Liberec 3

Příloha

PODÉLNÝ PROFIL Č. 26 - VĚTEV Z

3.26