
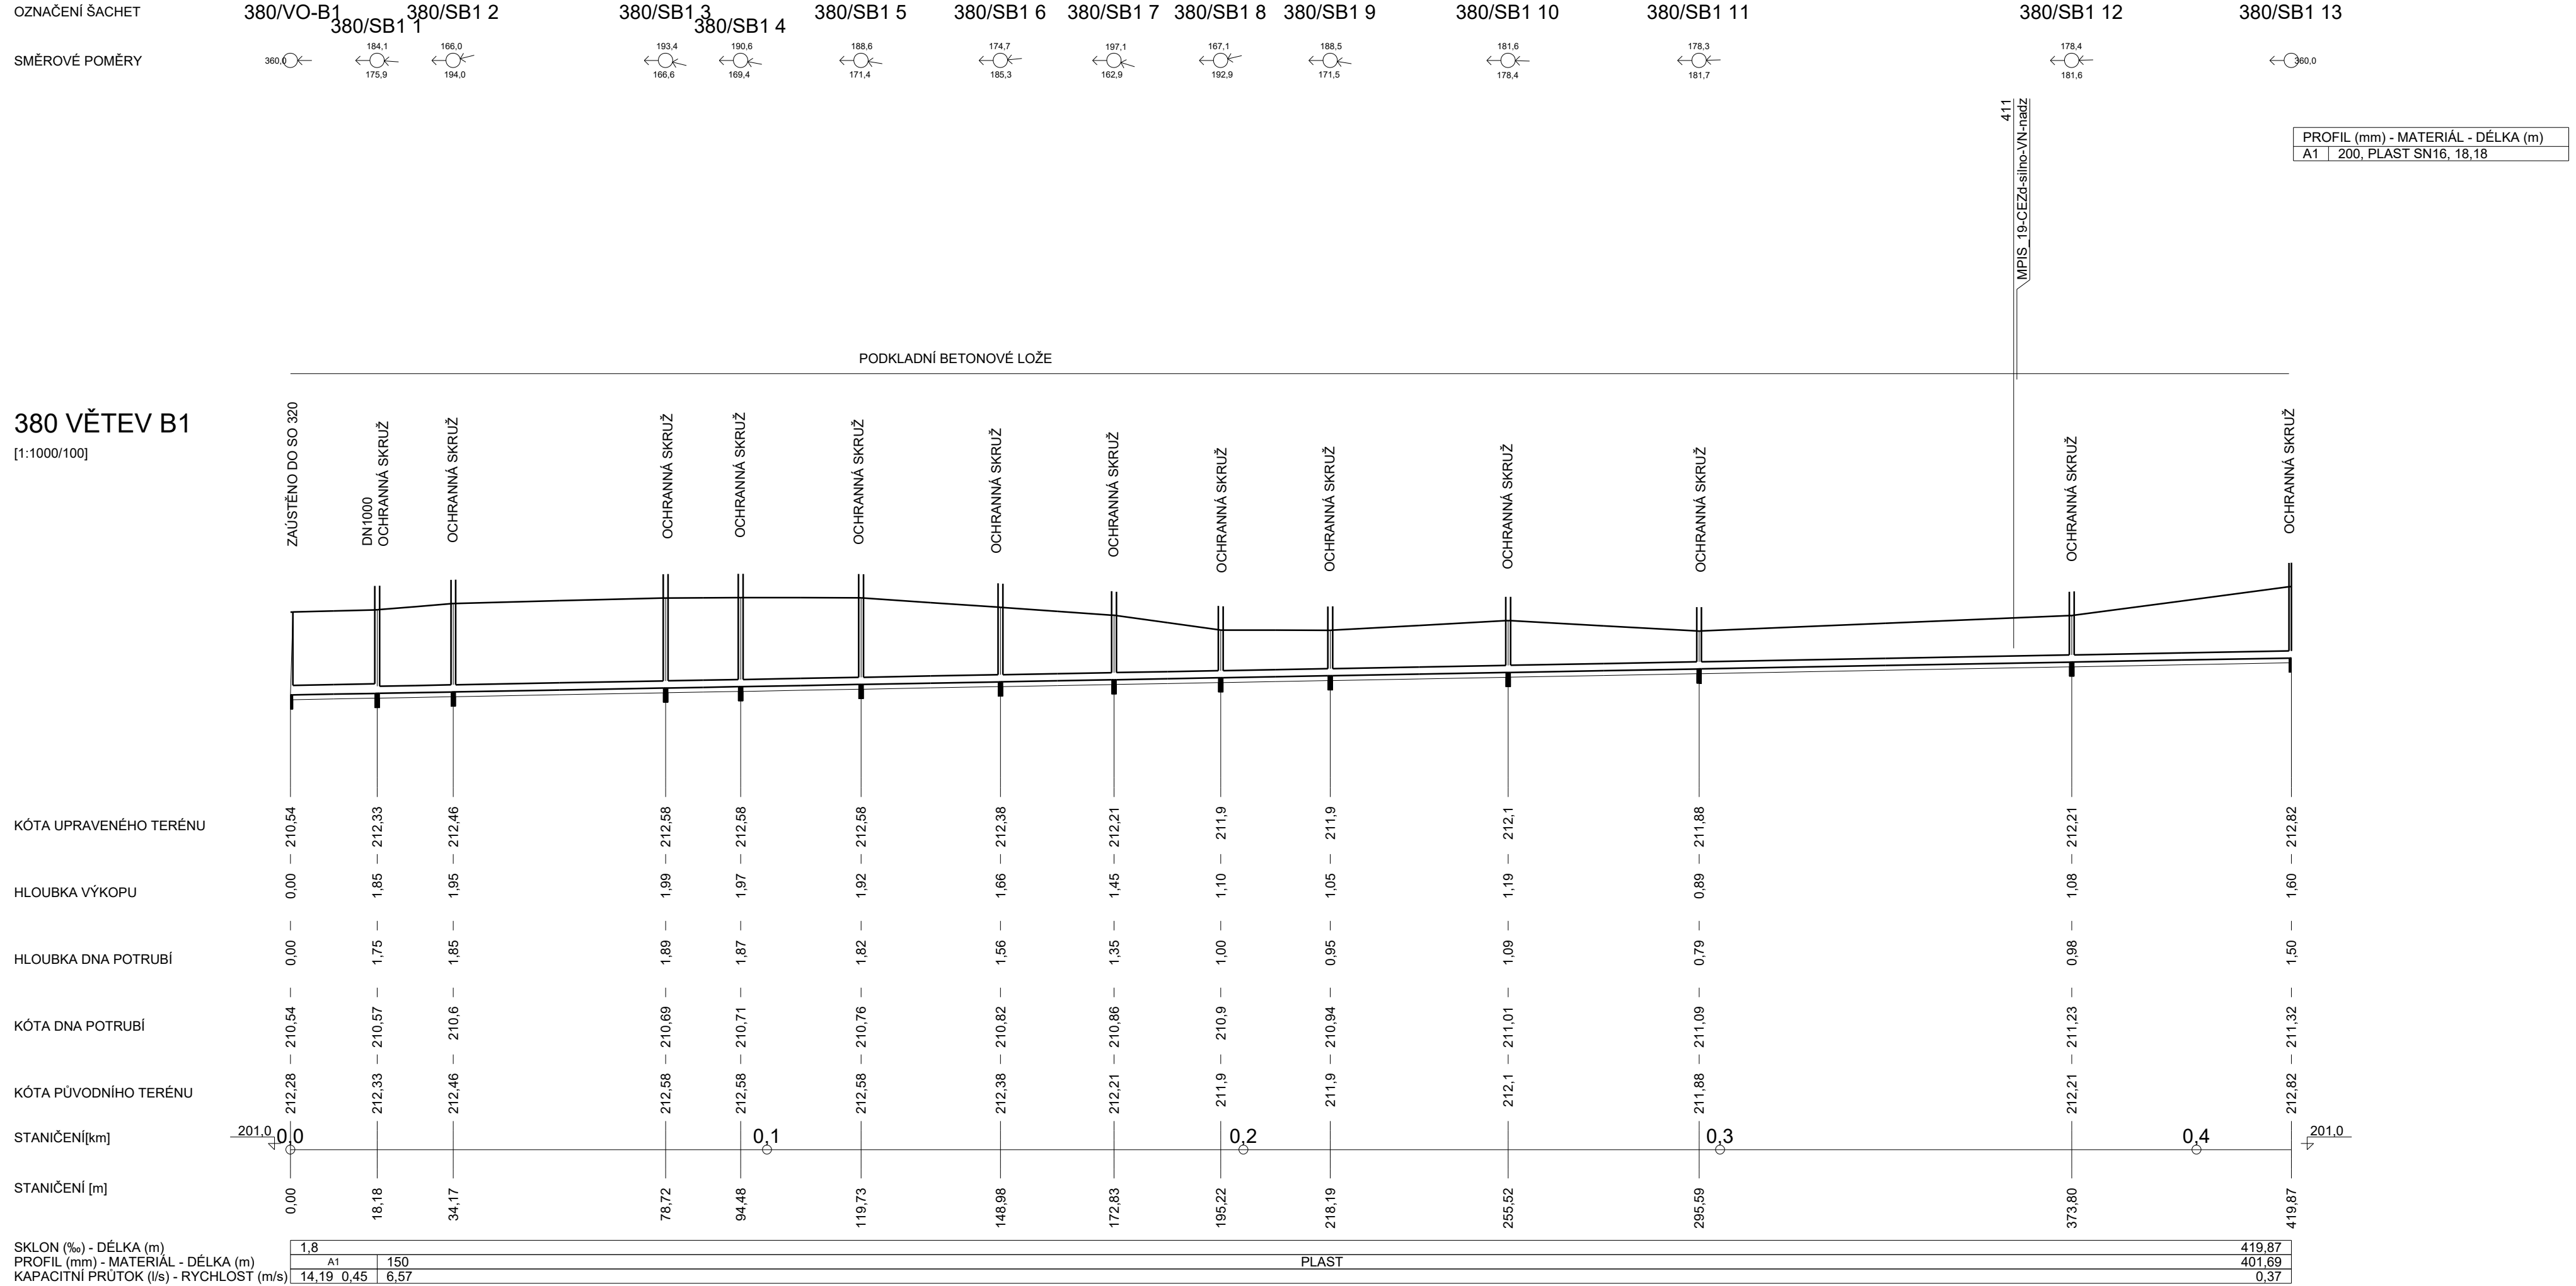


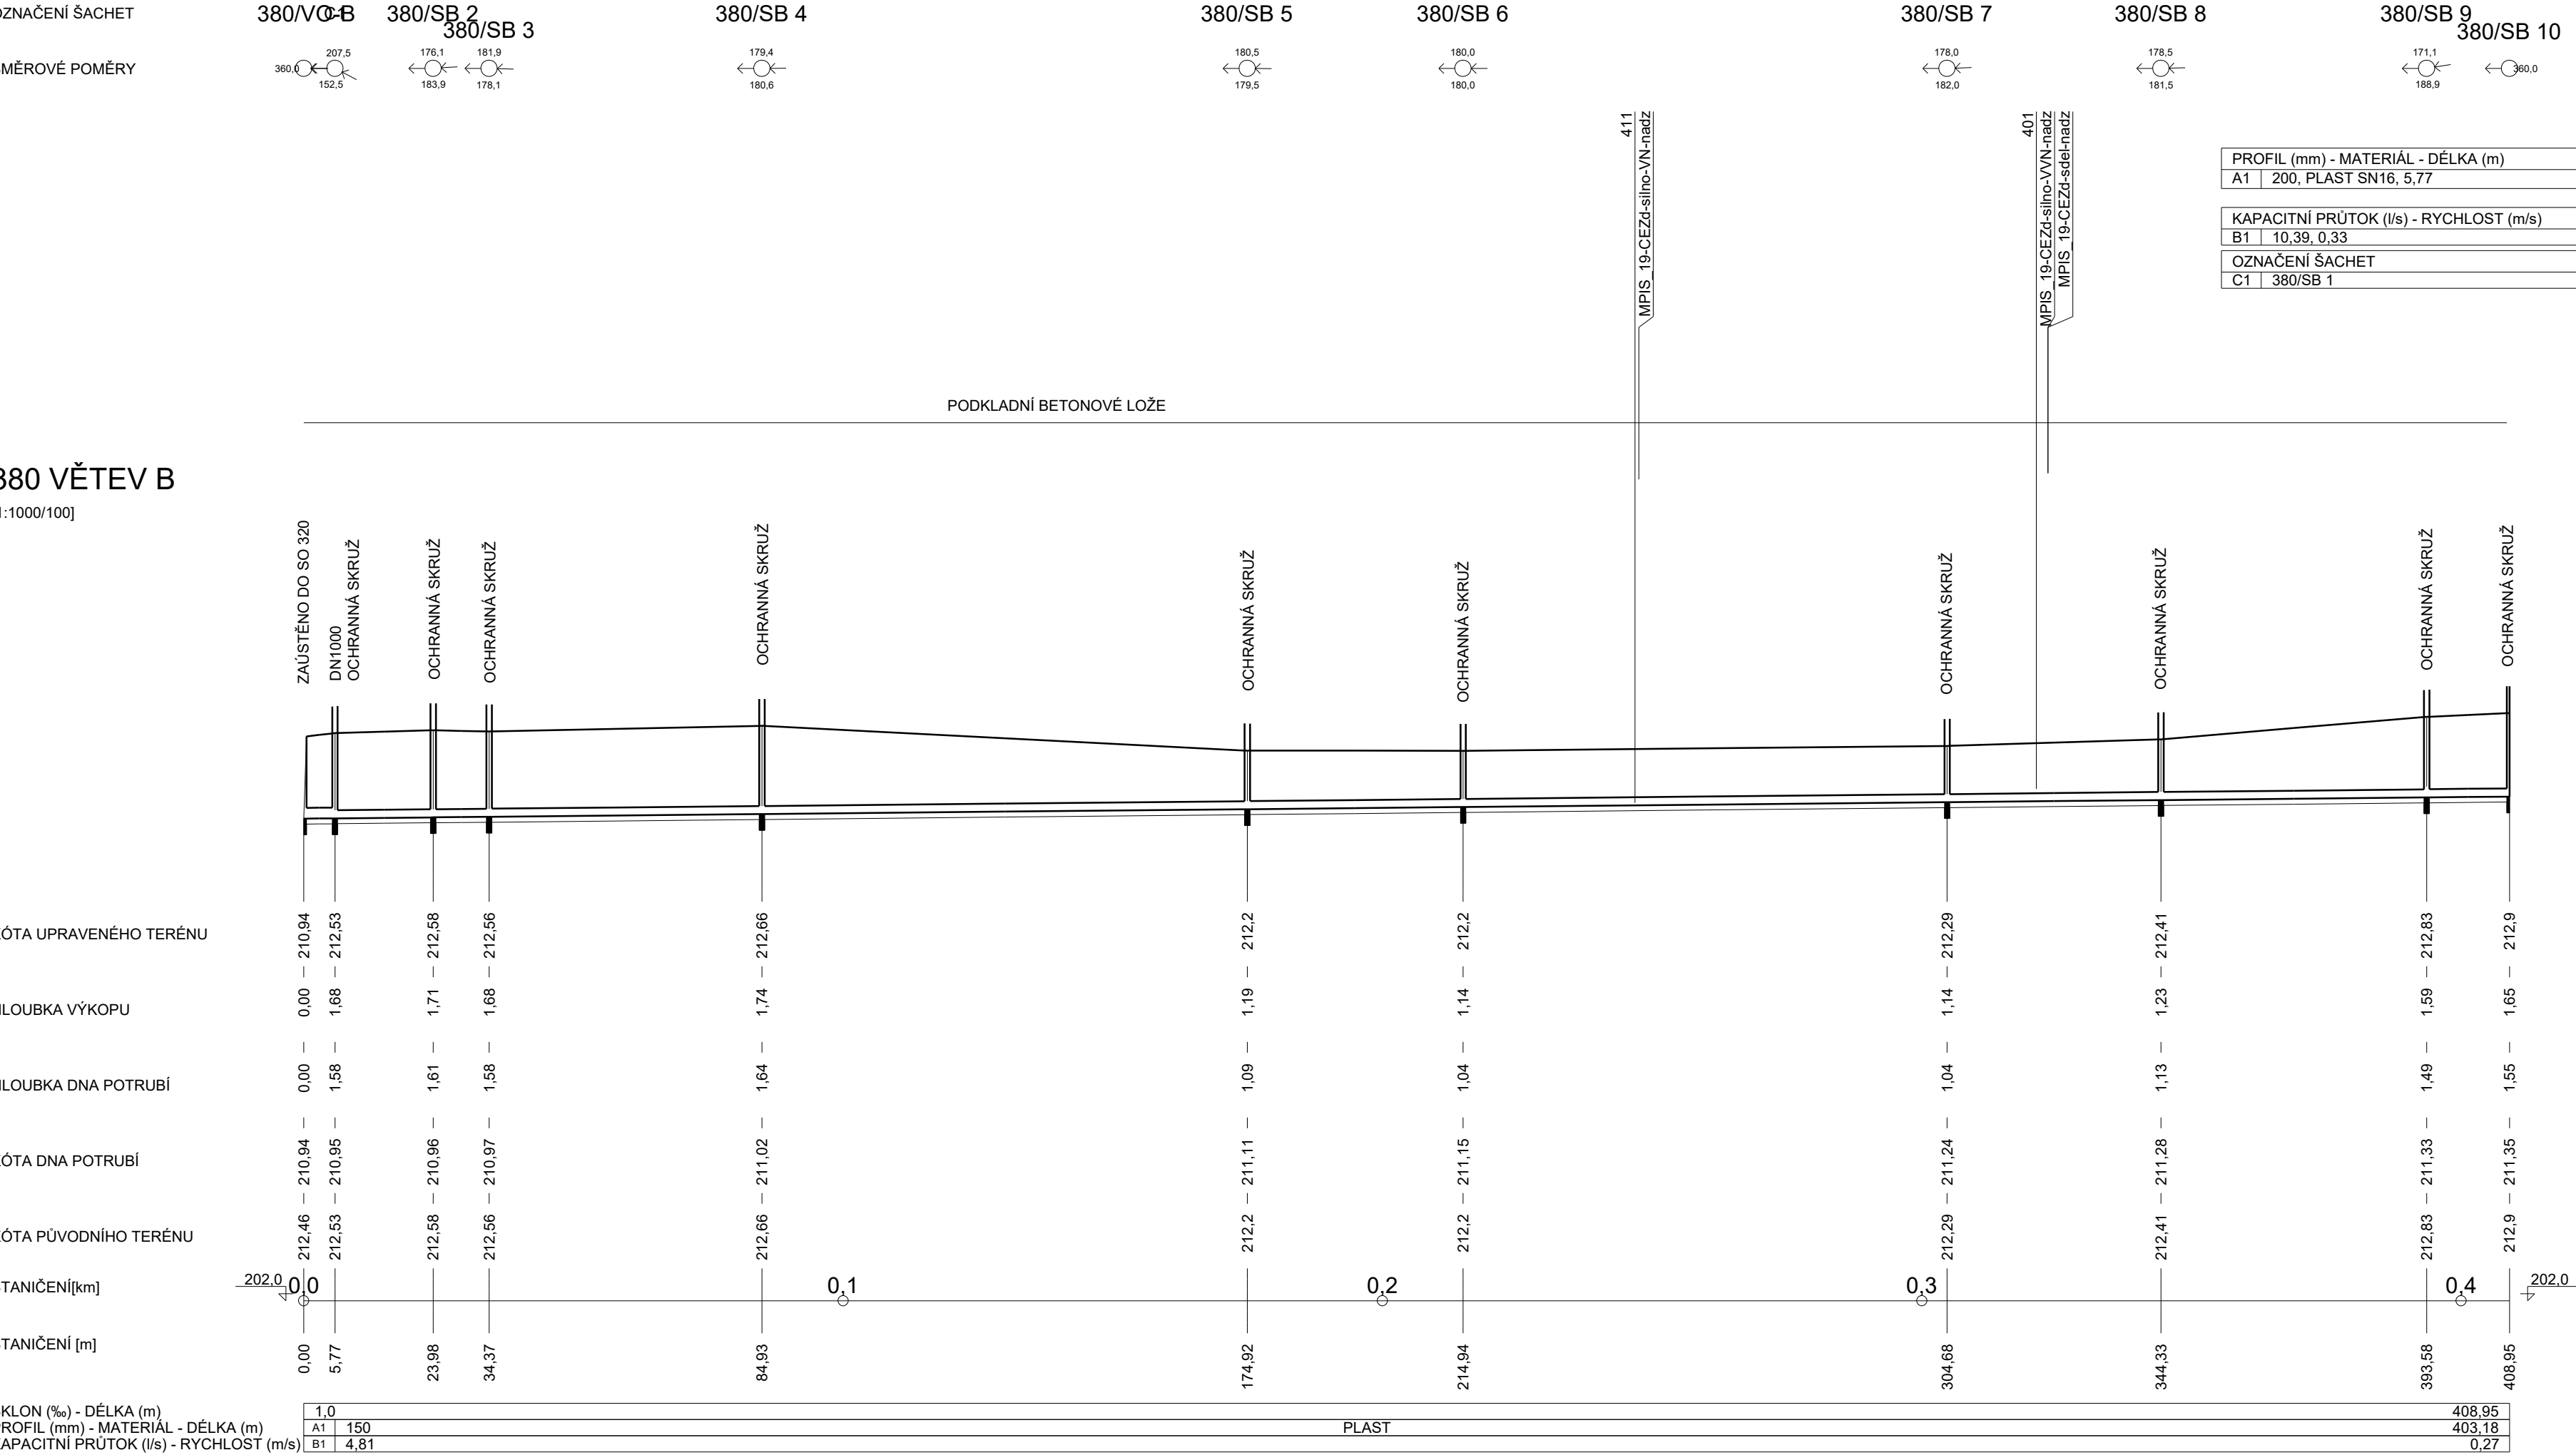

Souřadnicový systém: S-JTSK
Výškový systém: Bpv

SO 380 Úpravy meliorací

Objednatel:

**ŘEDITELSTVÍ SILNIC A DÁLNIC**



Ředitelství silnic a dálnic s. p.
Čerčanská 2023/12, Krč, 140 00 Praha 4

Zhotovitel:

**Valbek**

Valbek, spol. s r.o.
Vaňurova 505/17
460 07 Liberec 3

**Valbek**

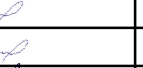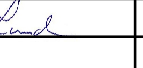Vypracoval	ING. J. VANCL		Zak. číslo	21-L113-001
Zodp. projektant	ING. J. VANCL		Datum	02/2025
Tech. kontrola	ING. D. LANDA		Stupeň	PDPS
Akce	I/16 MLADÁ BOLESLAV - MARTINOVICE		Počet formátů	7 x A4
Zhotovitel:	Valbek, spol. s r.o. Vaňurova 505/17 460 07 Liberec 3		Měřítko	1 : 1000/100
Příloha	PODÉLNÝ PROFIL Č. 2 - VĚTEV B, B1		Č. přílohy	Paré

3.2