
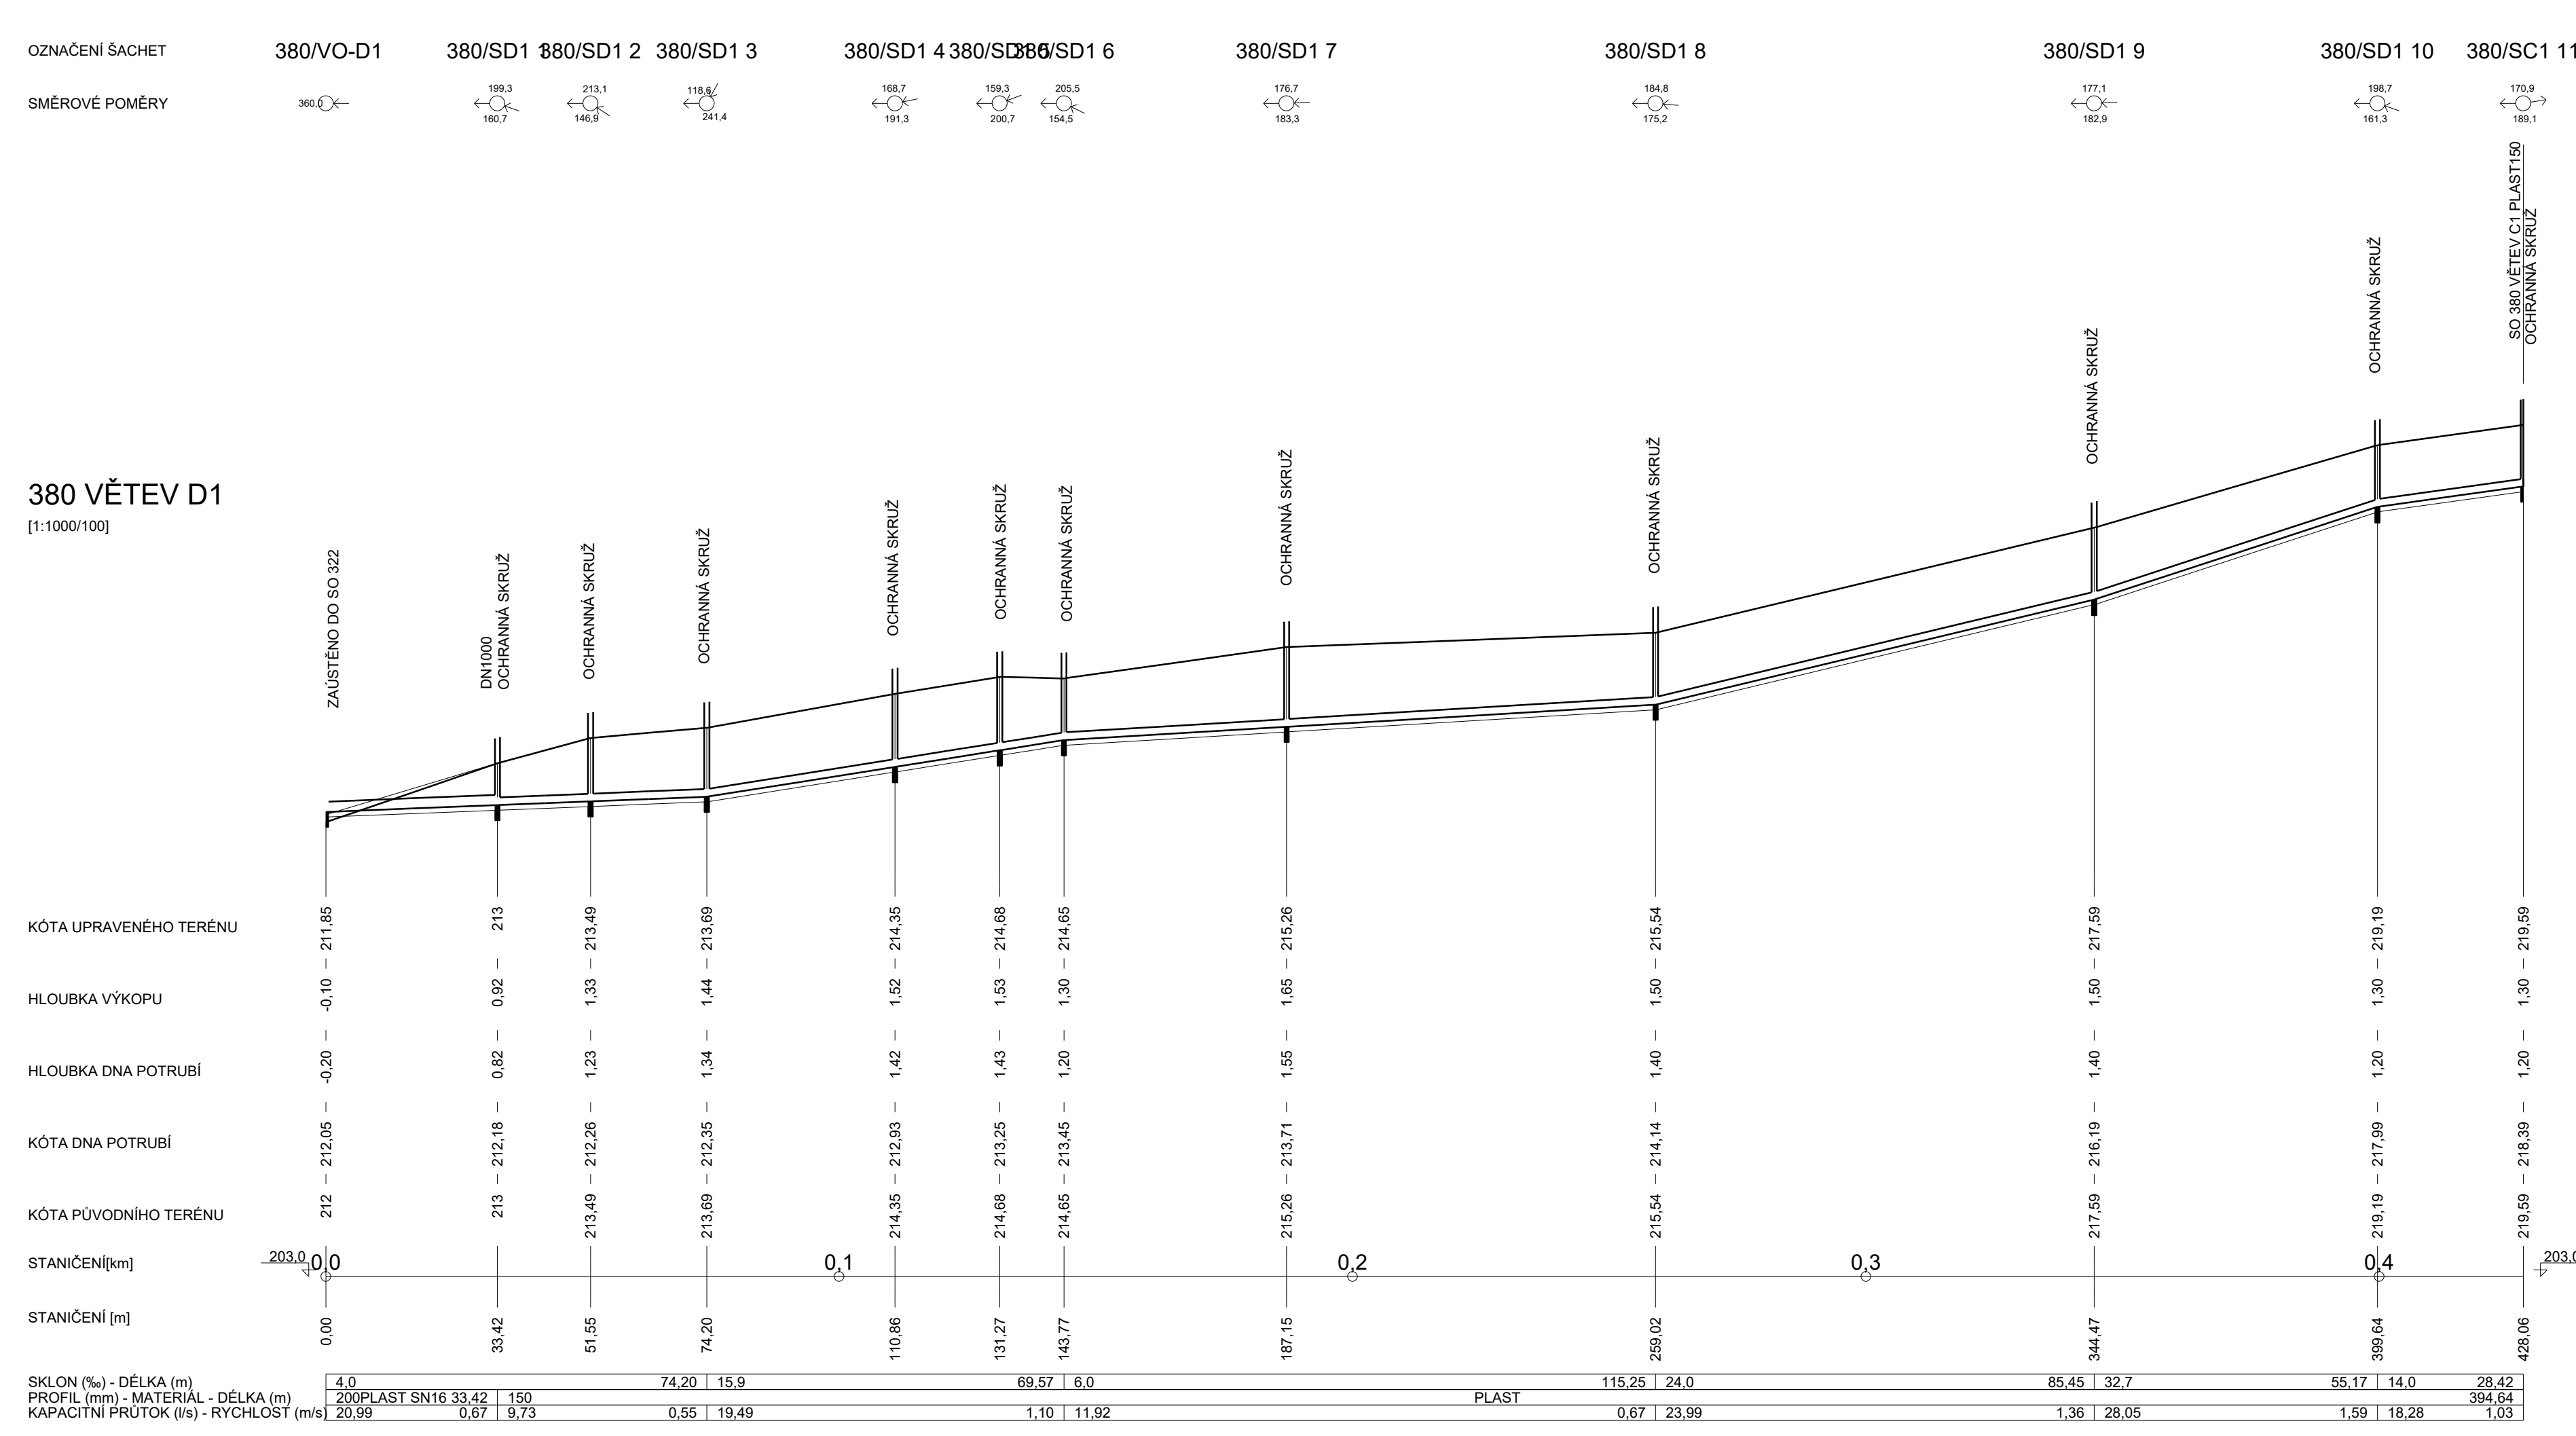


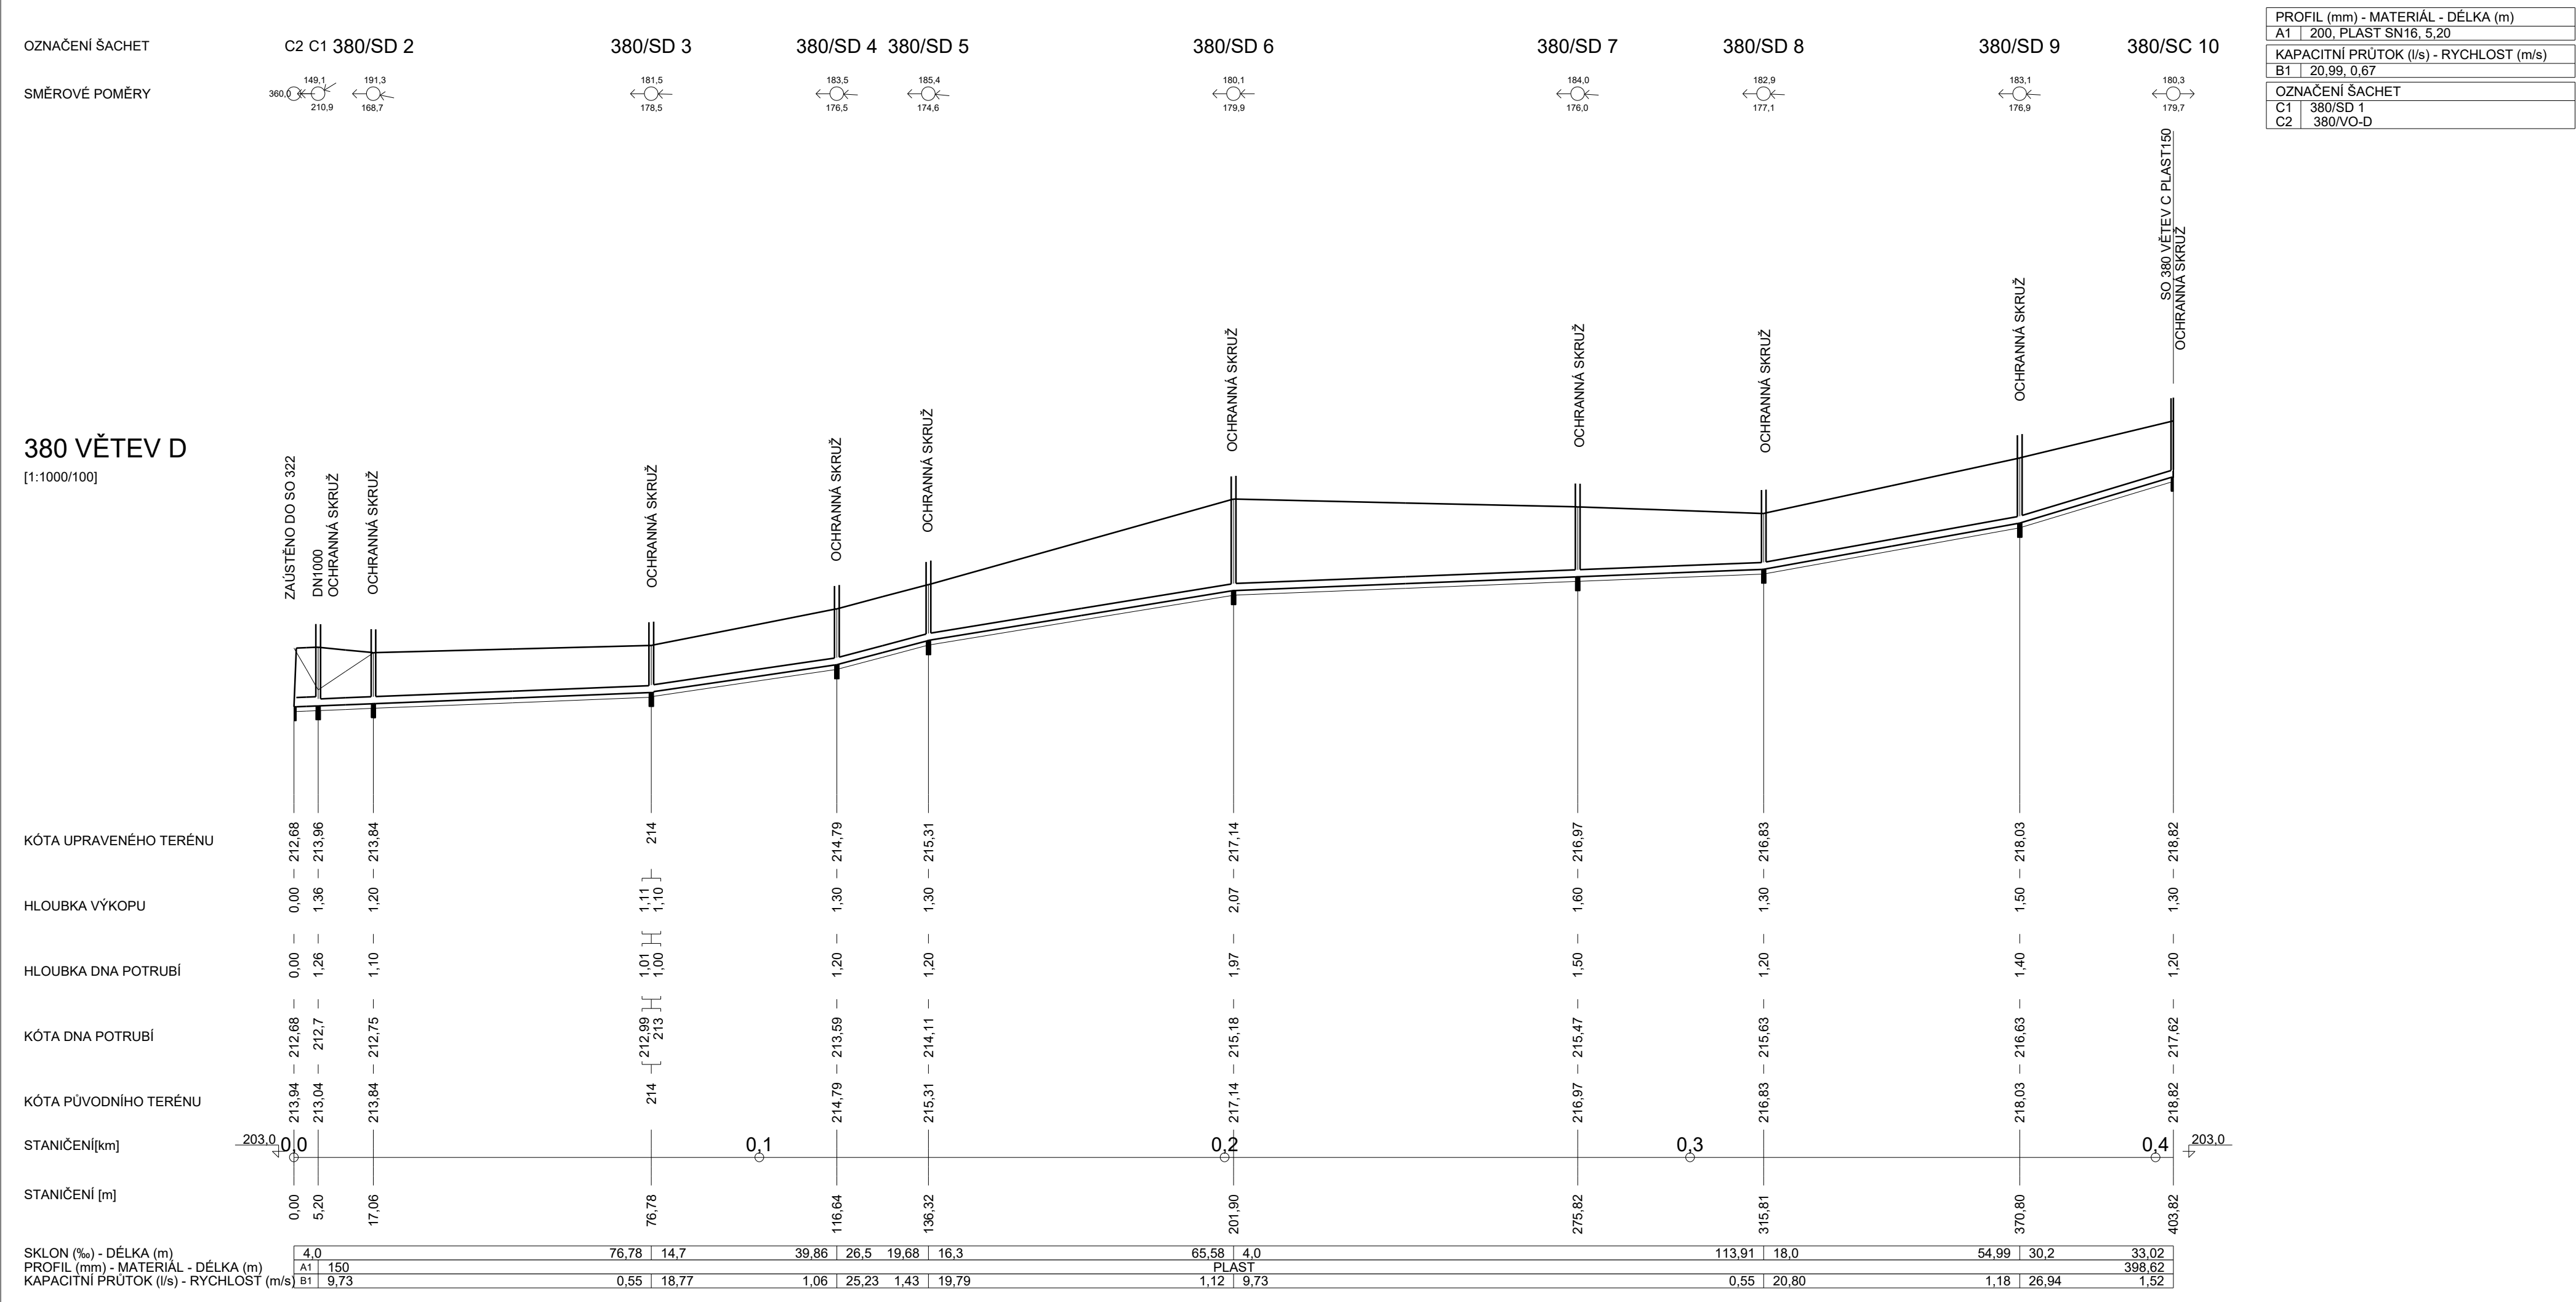

Souřadnicový systém: S-JTSK
Výškový systém: Bpv

SO 380

Úpravy meliorací

Objednatel:



ŘEDITELSTVÍ
SILNIC
A DÁLNIC

Ředitelství silnic a dálnic s. p.
Čerčanská 2023/12, Krč, 140 00 Praha 4



Zhotovitel:



Valbek

Valbek, spol. s r.o.

Vaňurova 505/17
460 07 Liberec 3

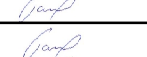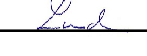 Zhotovitel: Valbek, spol. s r.o. Vaňurova 505/17 460 07 Liberec 3	Vypracoval		ING. J. VANCL		Zak. číslo	21-L113-001
	Zodp. projektant		ING. J. VANCL		Datum	02/2025
	Tech. kontrola		ING. D. LANDA		Stupeň	PDPS
	Akce I/16 MLADÁ BOLESLAV - MARTINOVICE		Počet formátů 7 x A4		Měřítko	1 : 1000/100
					Č. přílohy	Paré
Příloha		PODÉLNÝ PROFIL Č. 4 - VĚTEV D, D1		3.4		