
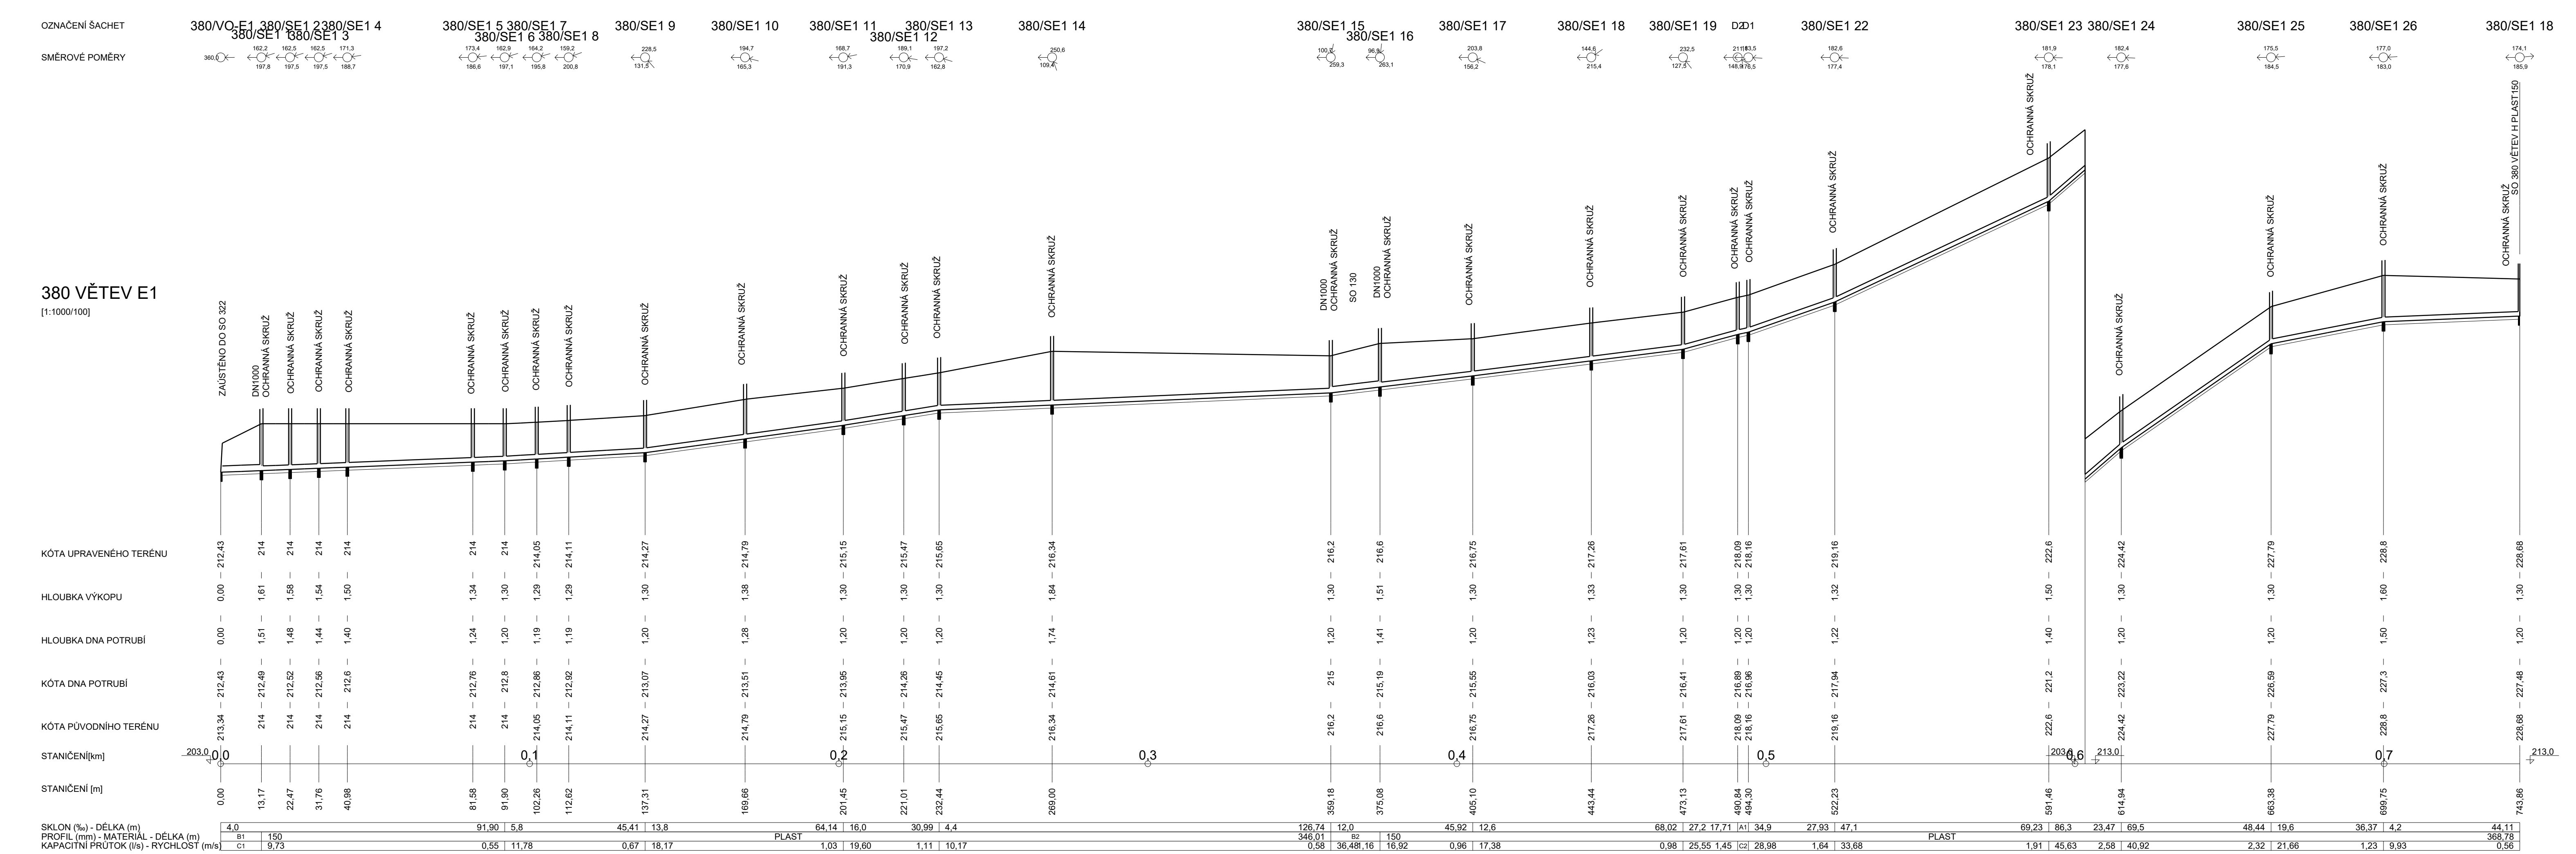


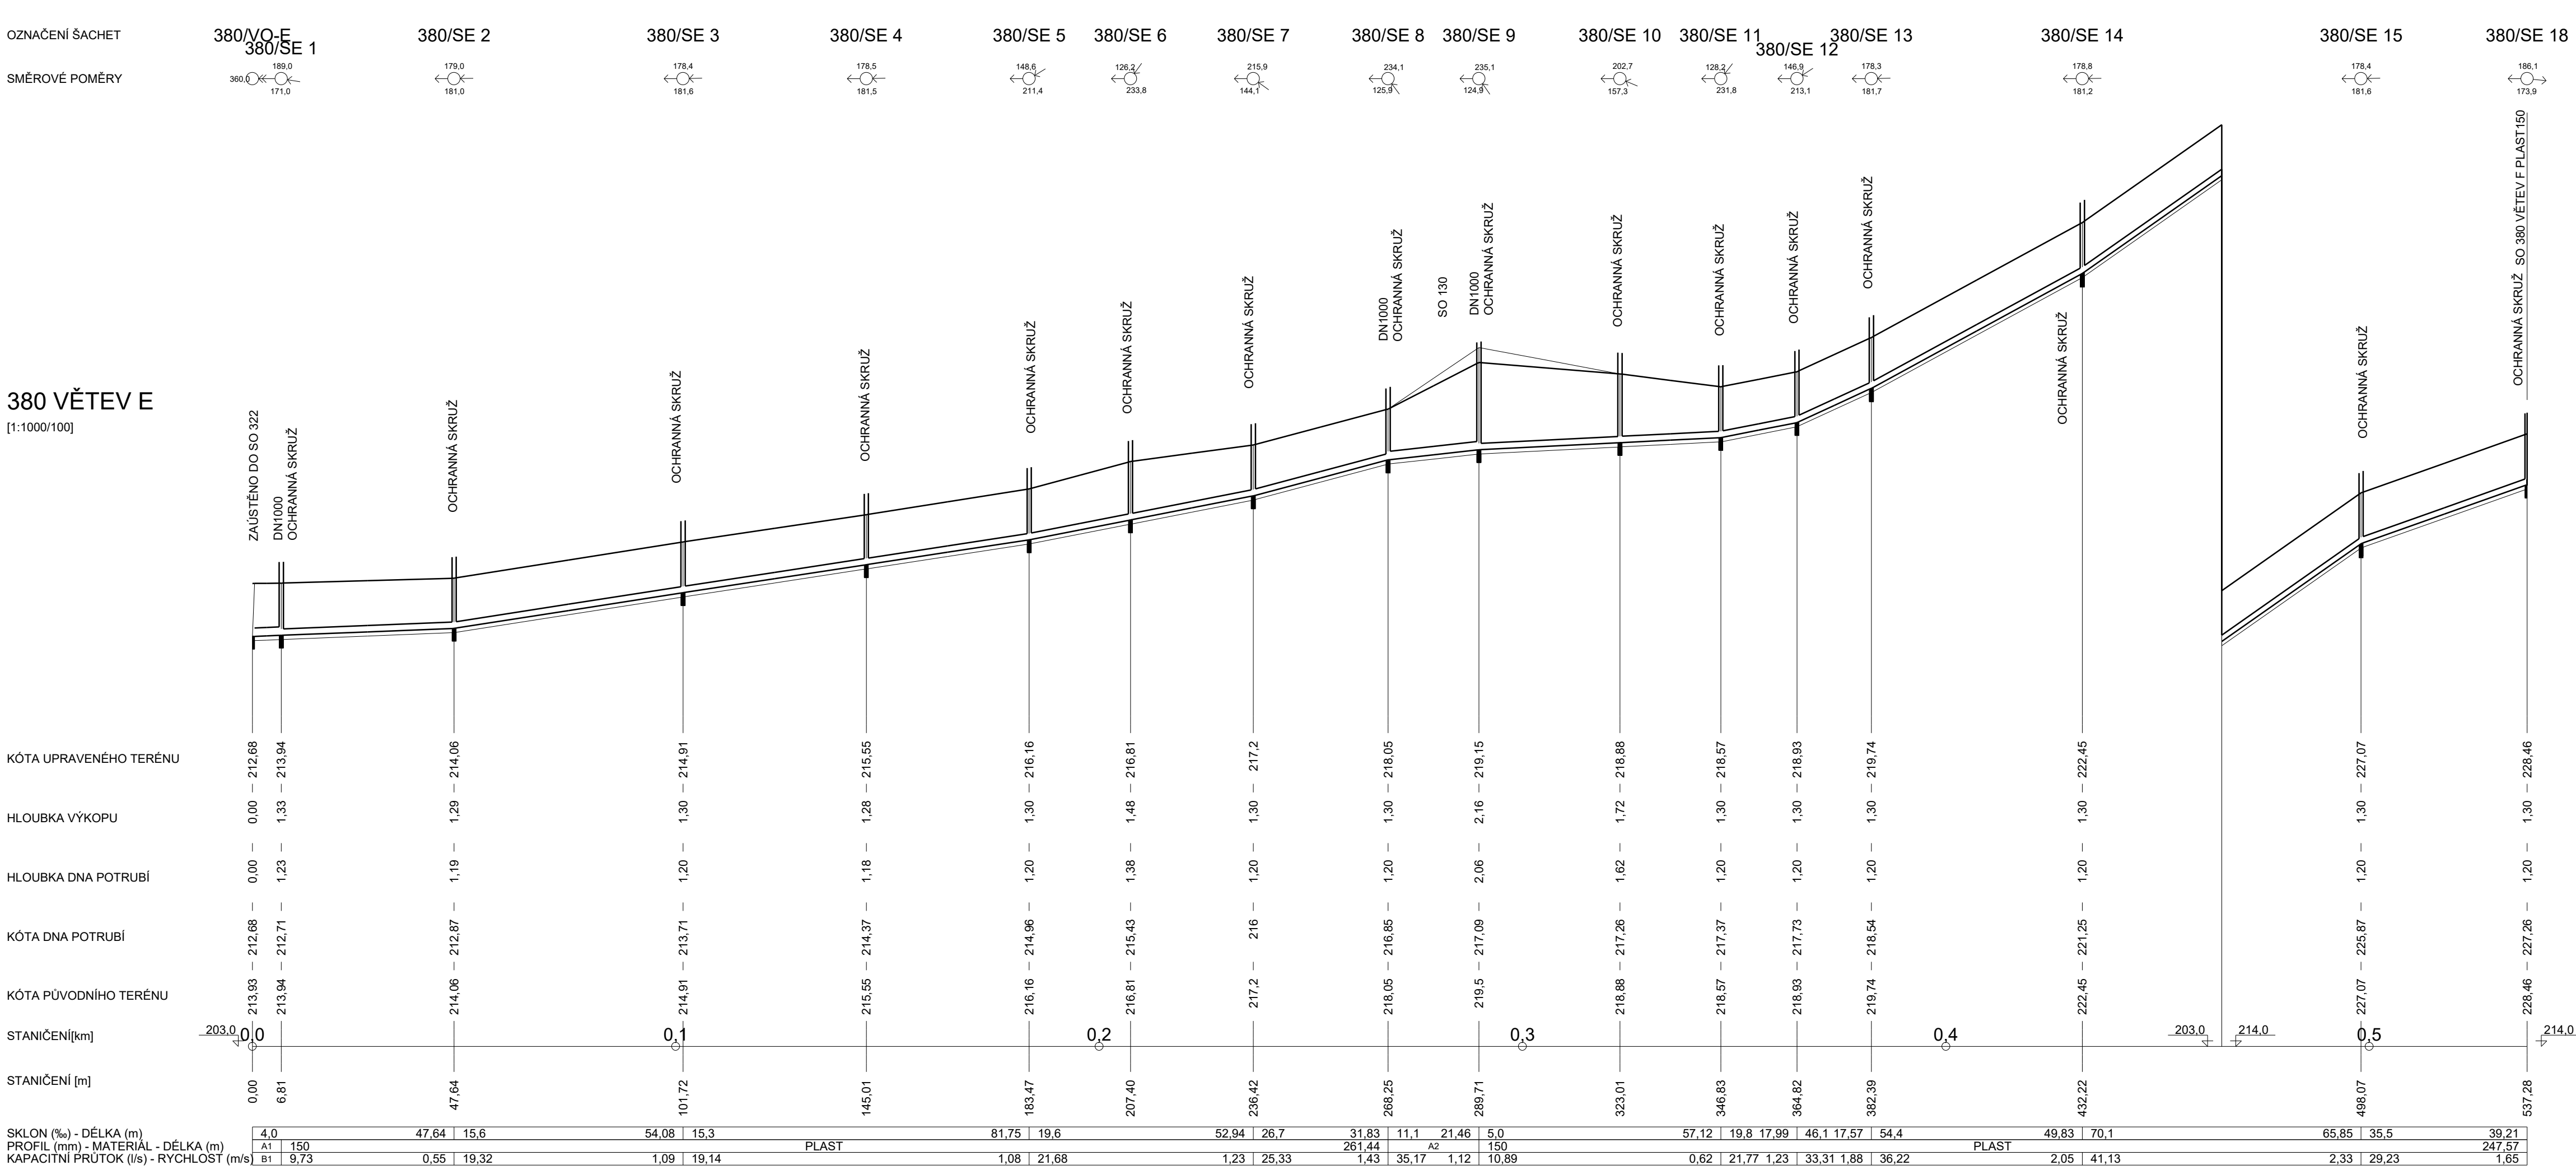

SKLON (‰) - DÉLKA (m)
A1 21,2, 3,46
PROFIL (mm) - MATERIÁL - DÉLKA (m)
B1 200, PLAST SN16, 13,17
B2 200, PLAST SN16, 15,89
KAPACITNÍ PRŮTOK (l/s) - RYCHLOST (m/s)
C1 20,99, 0,67
C2 22,54, 1,28
OZNAČENÍ ŠACHET
D1 380/SE1 21
D2 380/SE1 20

Souřadnicový systém: S-JTSK
Výškový systém: Bpv

SO 380 Úpravy meliorací

Objednatel:

Ředitelství silnic a dálnic s. p.
Čerčanská 2023/12, Krč, 140 00 Praha 4

Zhotovitel:

Valbek, spol. s r.o.
Vaňurova 505/17
460 07 Liberec 3

Valbek	Vypracoval	ING. J. VANCIL	Zak. číslo	21-LH3-001
	Zodp. projektant	ING. J. VANCIL	Datum	02/2025
	Tech. kontrola	ING. D. LANDA	Stupeň	PDPS
	Akce	I/16 MLADÁ BOLESLAV - MARTINOVICE		
Zhotovitel: Valbek, spol. s r.o. Vaňurova 505/17 460 07 Liberec 3	Příloha		Počet formátů	10 x A4
			Měřítko	1 : 1000/100
PODÉLNÝ PROFIL Č. 5 - VĚTEV E, E1		Paré		
		3.5		