


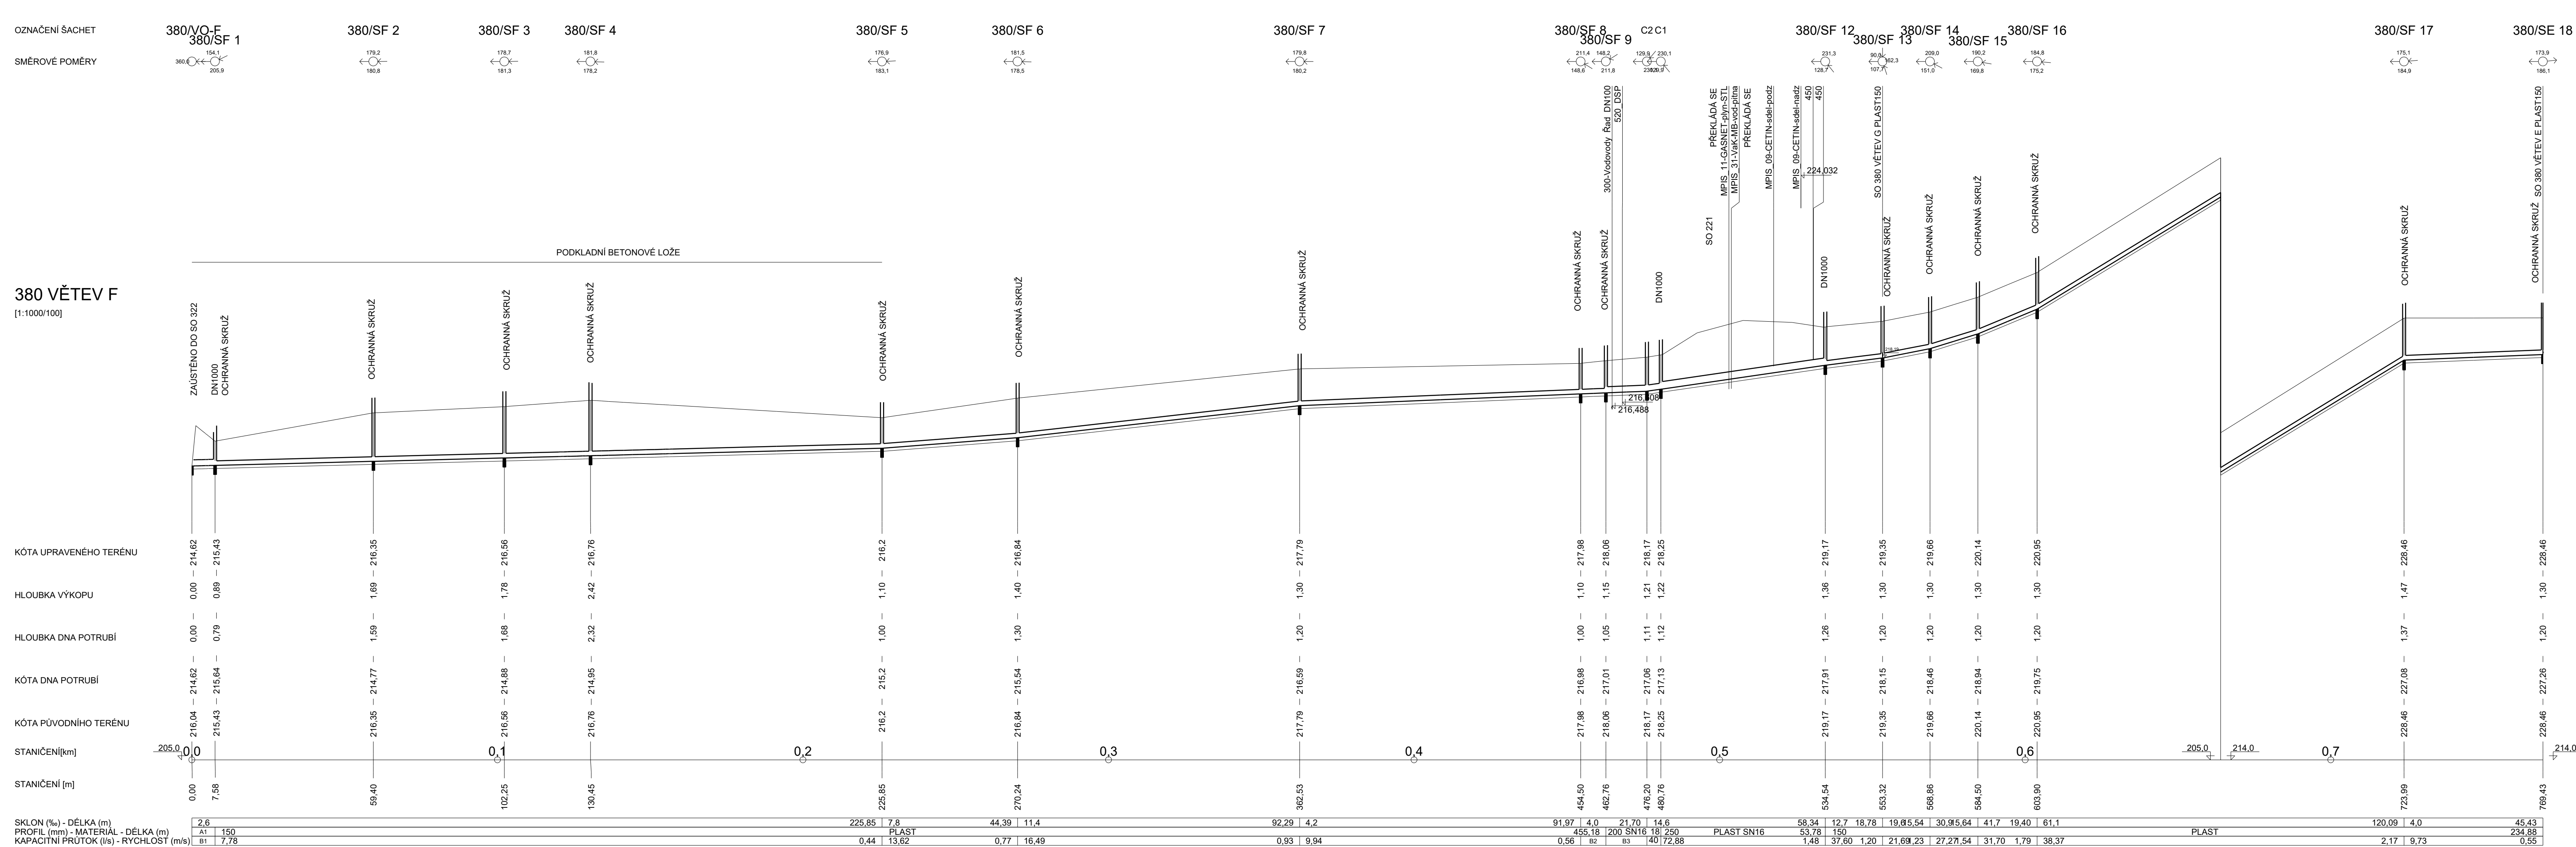

PROFIL (mm) - MATERIÁL - DĚLKA (m)	
A1	200, PLAST SN16, 7,58
KAPACITNÍ PRŮTOK (l/s) - RYCHLOST (m/s)	
B1	16,78, 0,53
B2	9,73, 0,55
B3	20,99, 0,67
OZNAČENÍ ŠACHET	
C1	380/SF 11
C2	380/SF 10

Souřadnicový systém: S-JTSK
Výškový systém: Bpv

SO 380 Úpravy meliorací



ŘEDITELSTVÍ SILNIC A DÁLNIC

Ředitelství silnic a dálnic s. p.

Čerčanská 2023/12, Krč, 140 00 Praha 4

**Valbek, spol. s r.o.**

Vaňurova 505/17
460 07 Liberec 3

	Vypracoval	ING. J. VANCL	<i>Jan Václav</i>	Zak. číslo	21-LI13-001	
	Zodp. projektant	ING. J. VANCL	<i>Jan Václav</i>	Datum	02/2025	
	Tech. kontrola	ING. D. LANDA	<i>David Landa</i>	Stupeň	PDPS	
	Akce	I/16 MLADÁ BOLESLAV - MARTINOVICE			Počet formátů	7 x A4
	Příloha				Měřítko	1 : 1000/100
Zhotovitel: Valbek, spol. s r.o. Vaňurova 505/17 460 07 Liberec 3				Č. přílohy	Paré	
				3.6		