
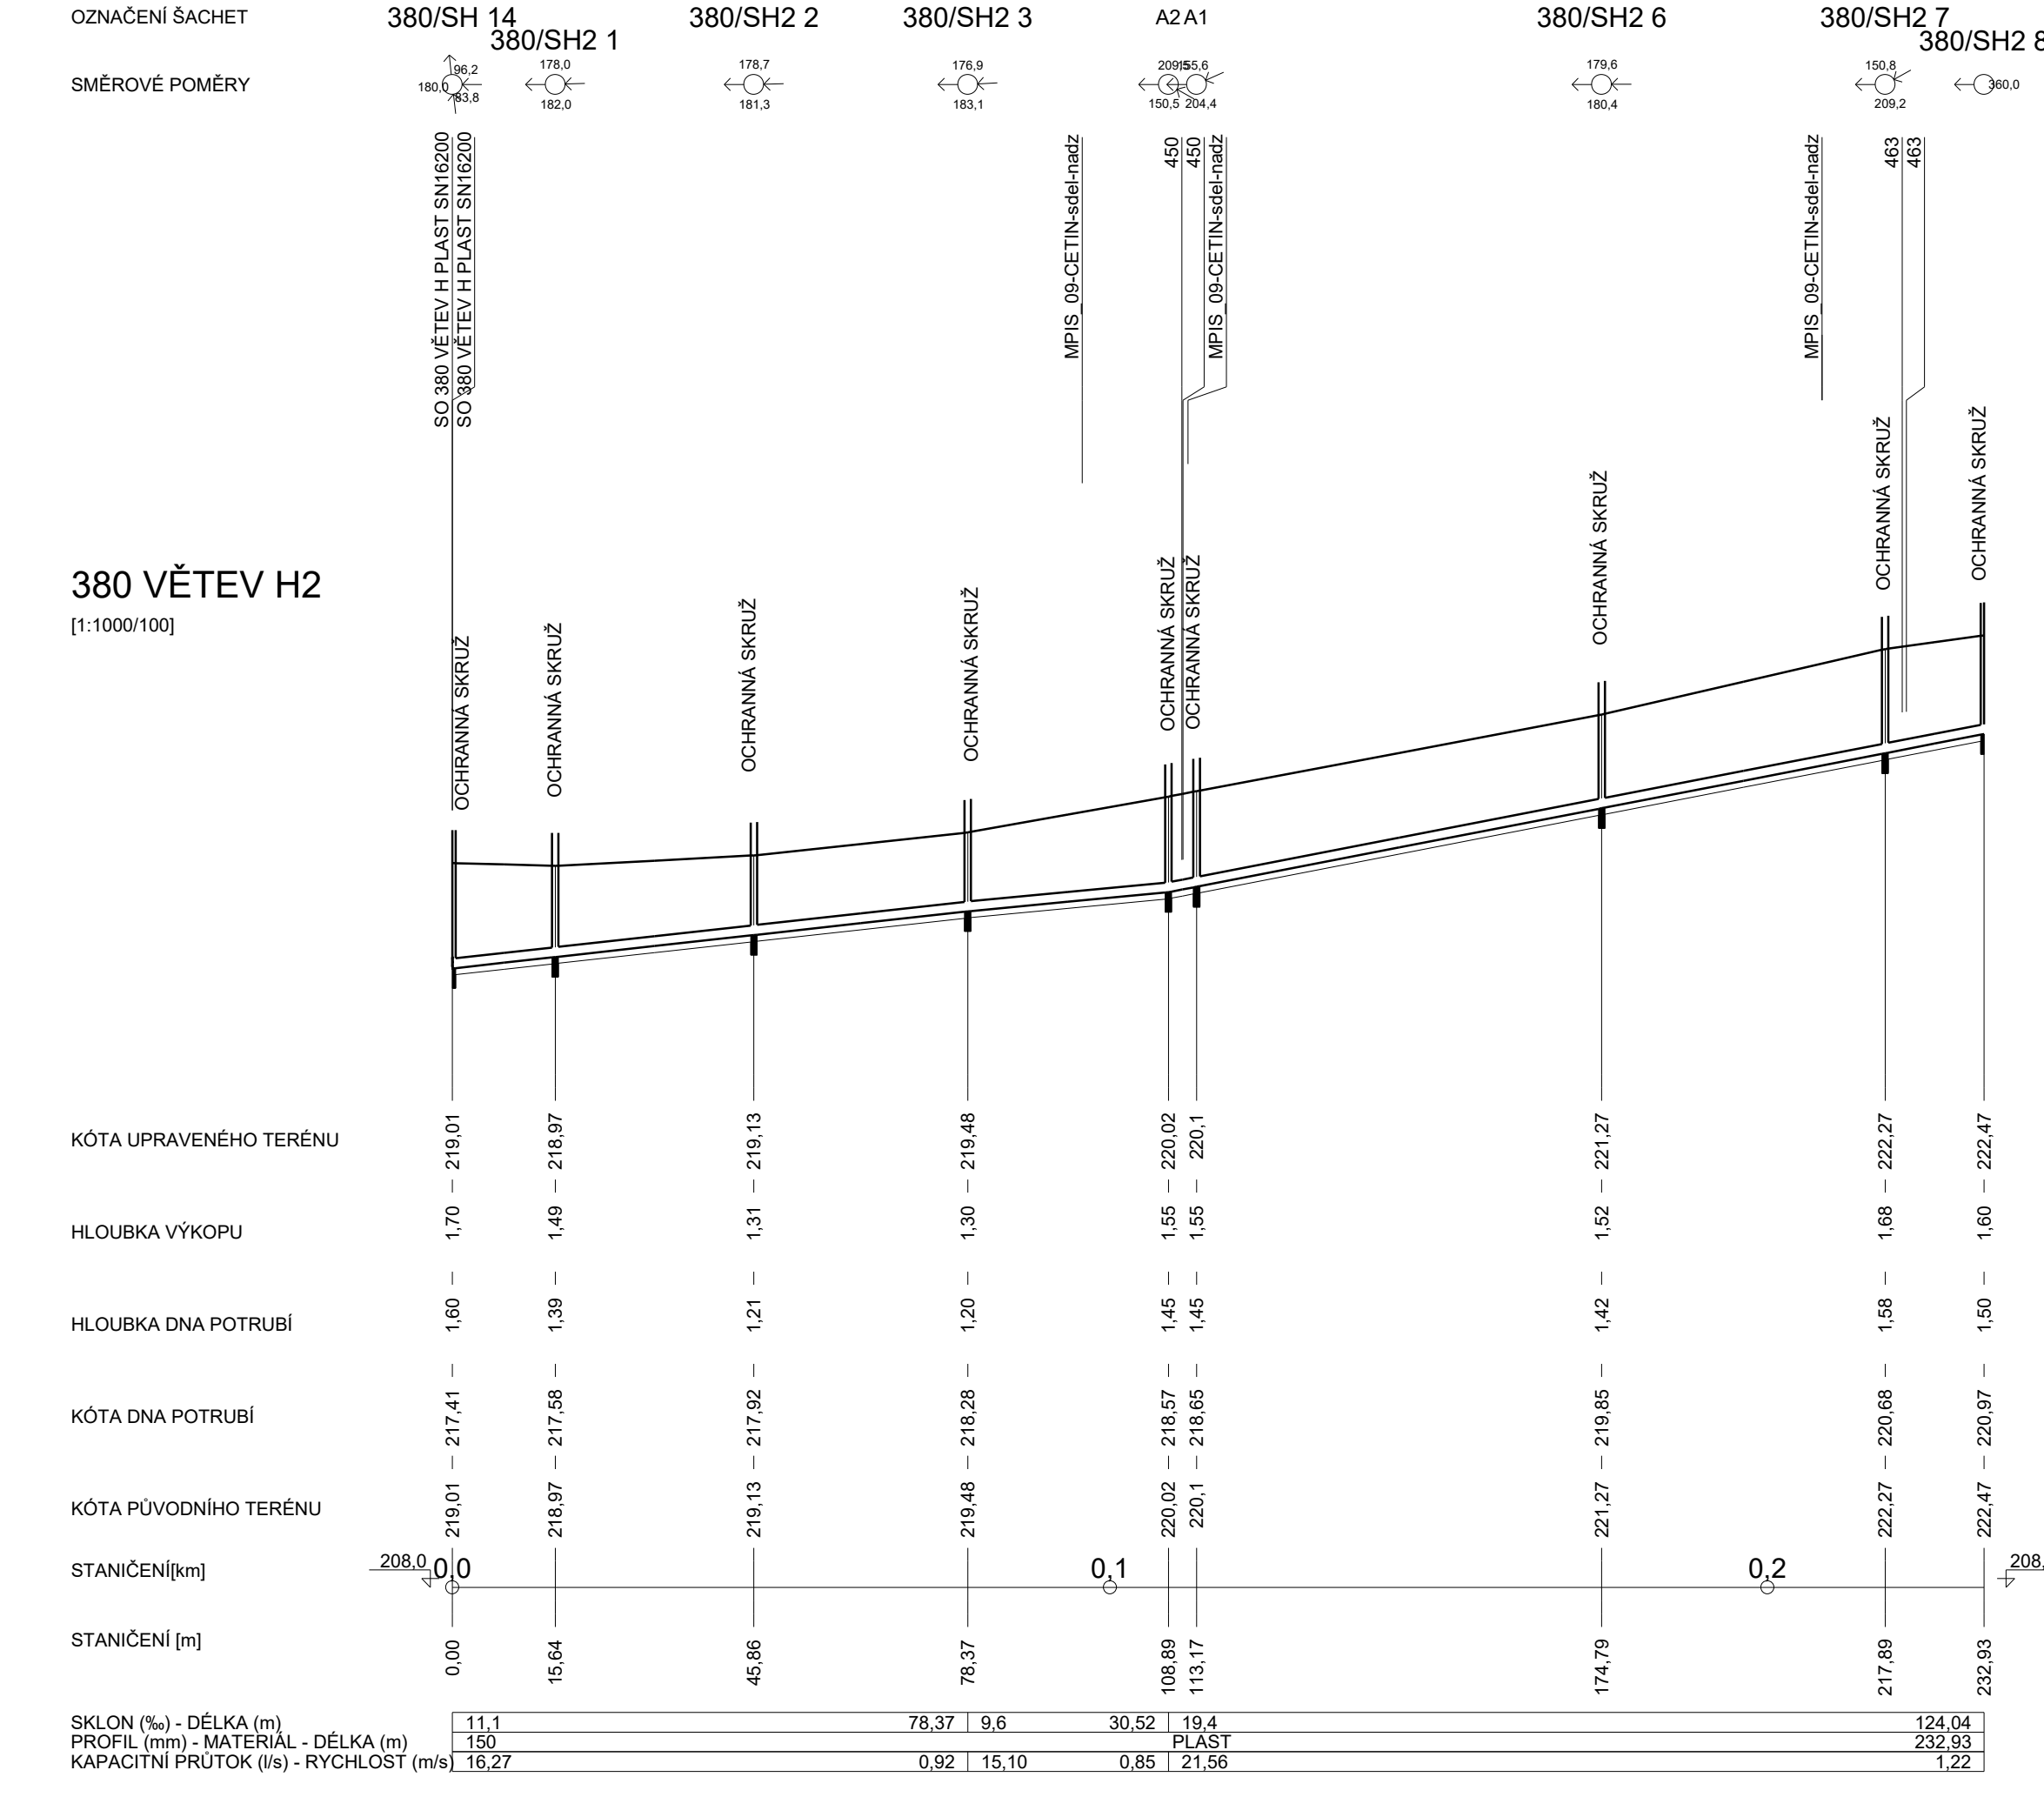
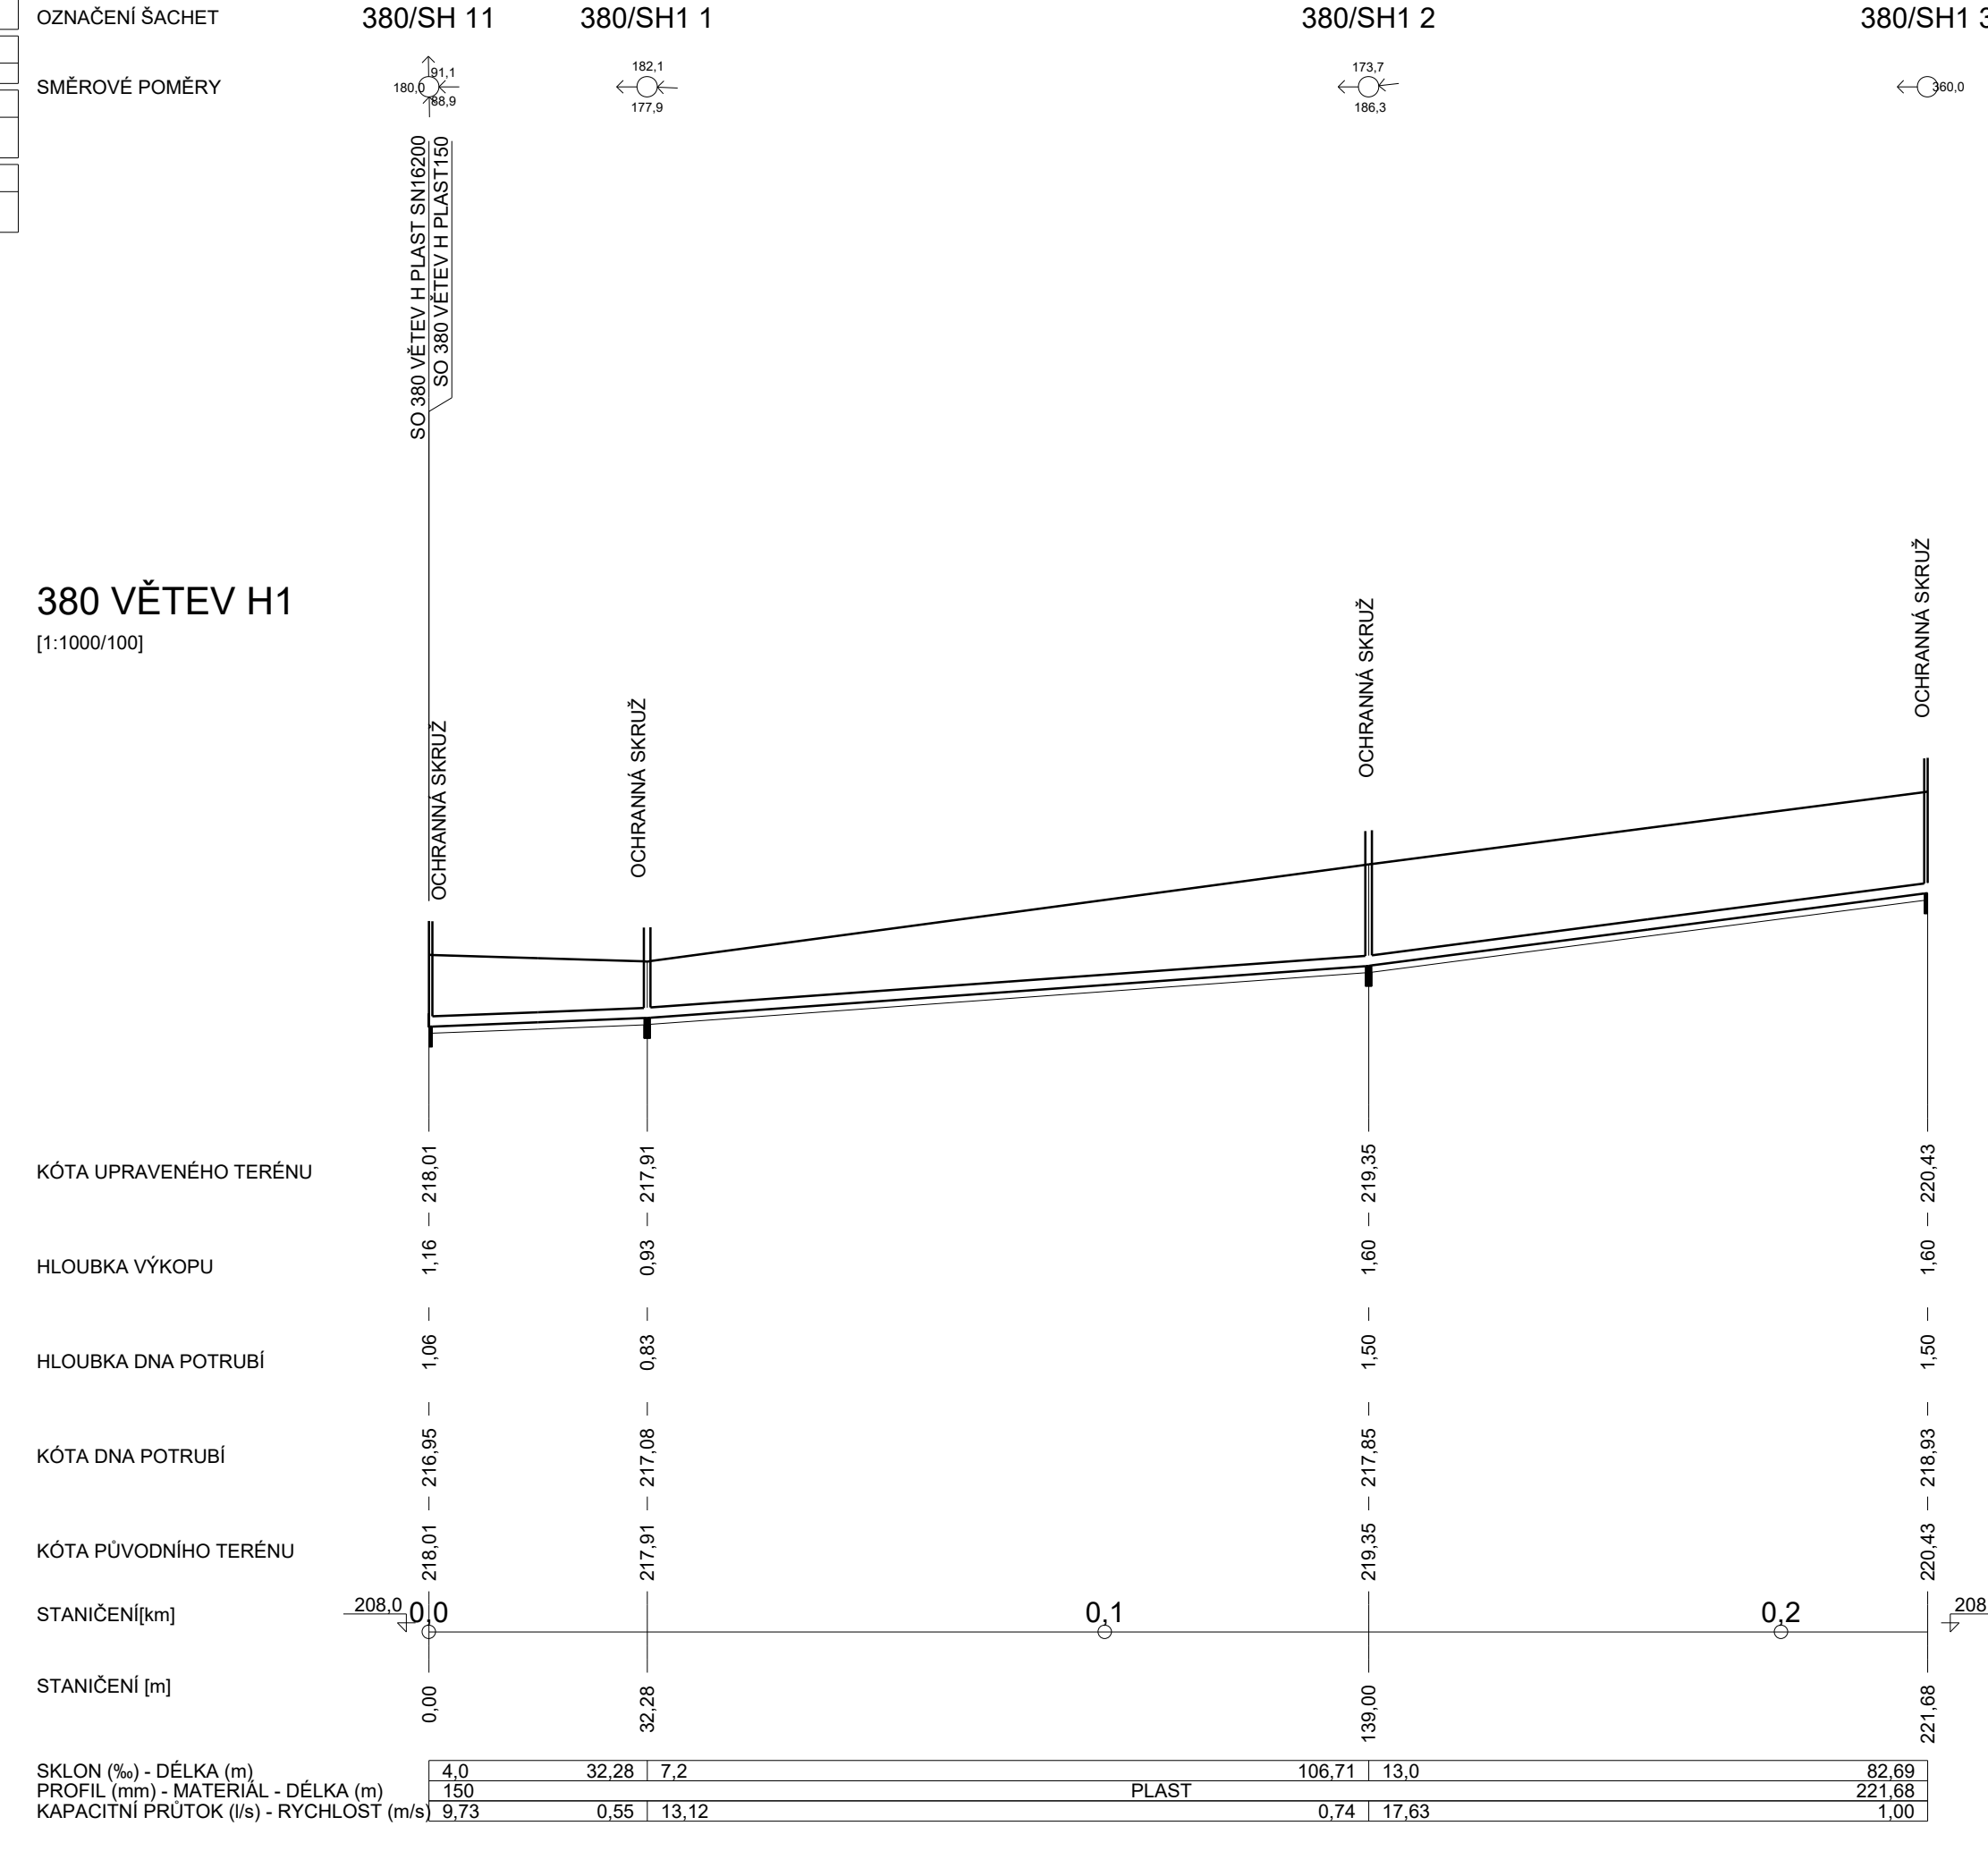


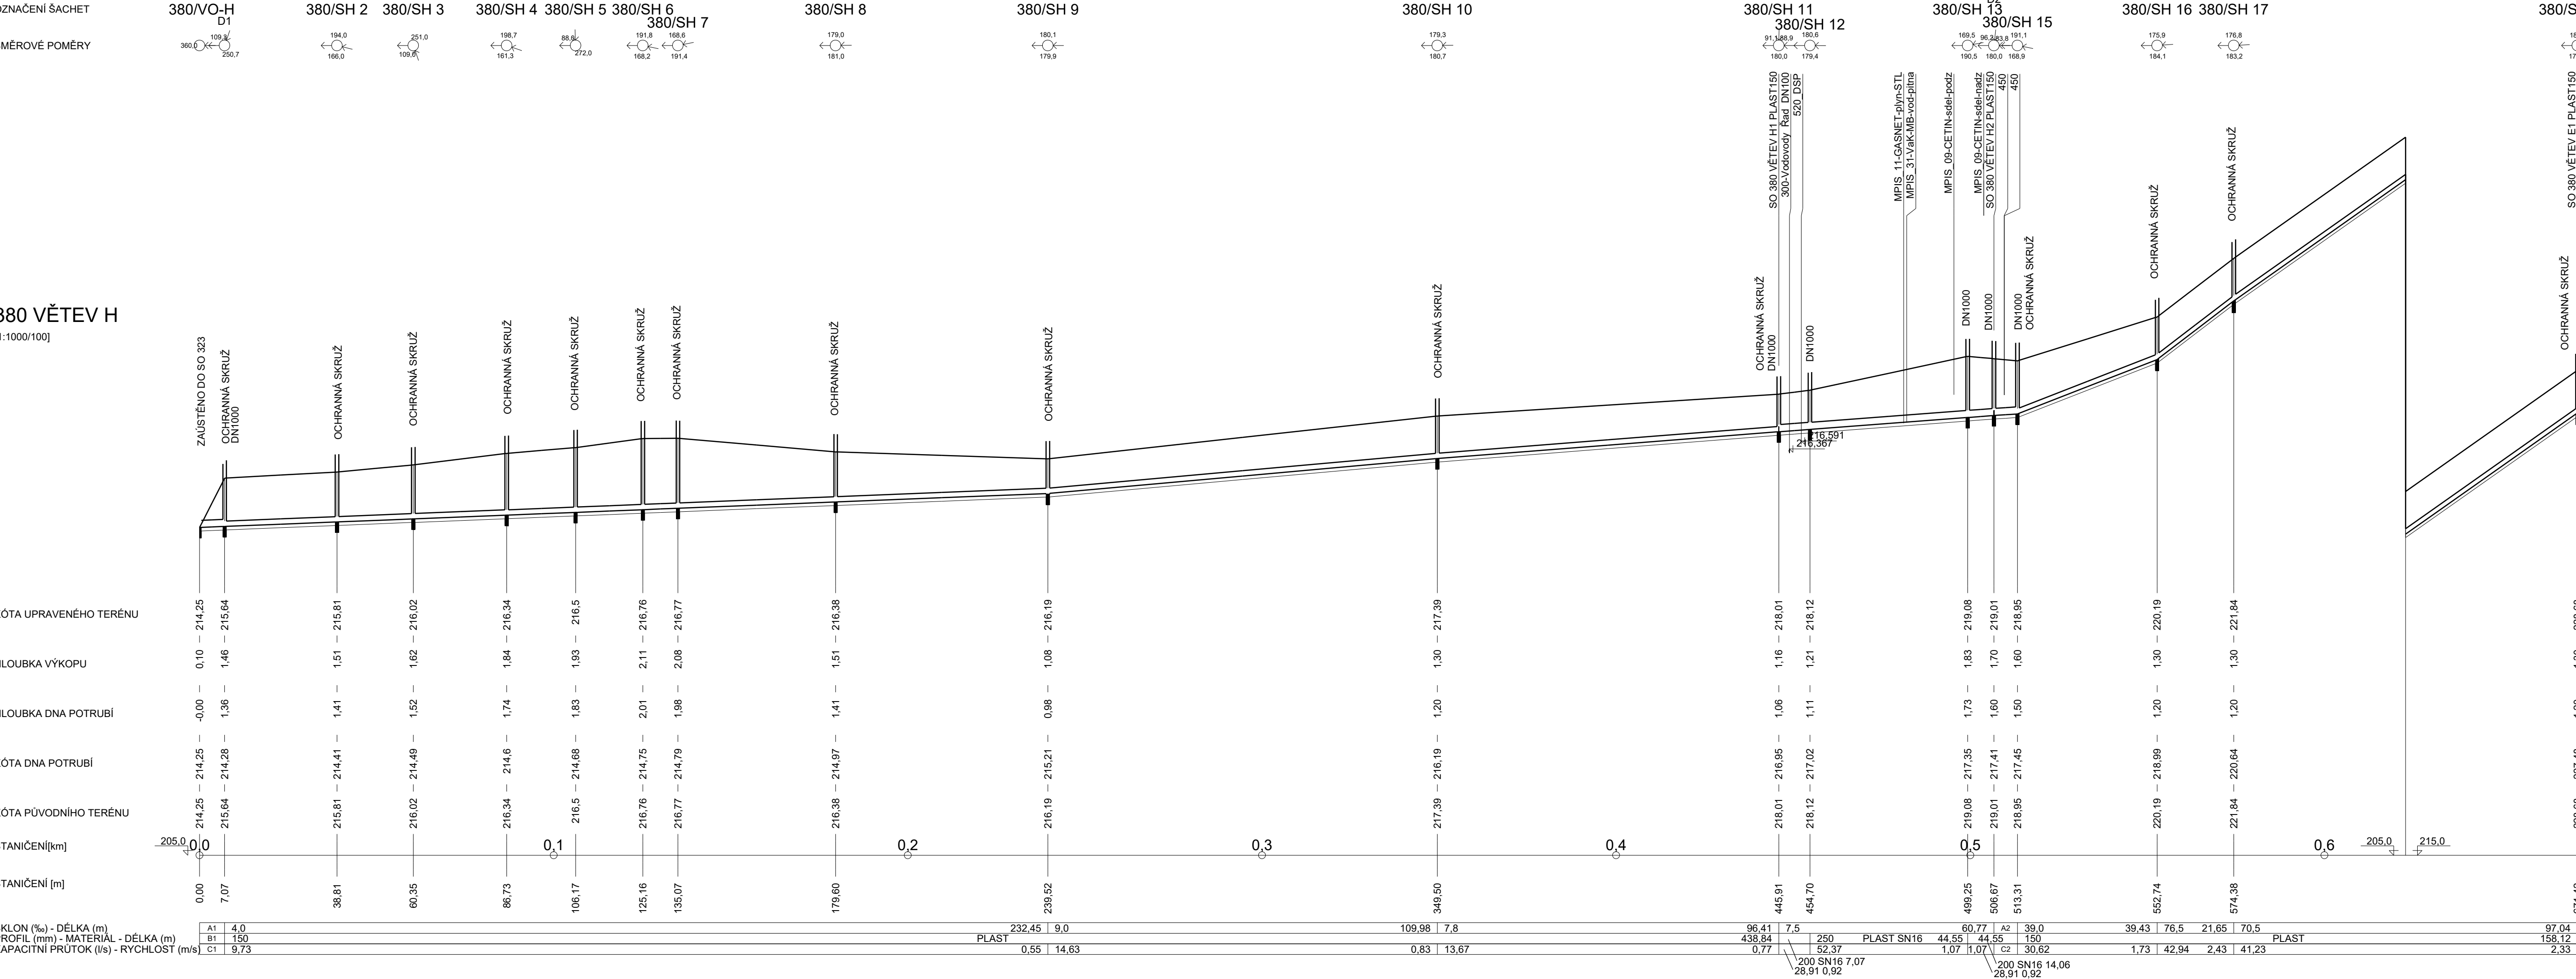

OZNAČENÍ ŠACHET

A1 380/SH 2 5 A2 380/SH 2 4

SO 380 Úpravy meliorací

Objednatel:

Ředitelství silnic a dálnic

Ředitelství silnic a dálnic s. p.

Čerčanská 2023/12, Krč, 140 00 Praha 4

Zhotovitel:

Valbek

Valbek, spol. s r.o.

Vaňurova 505/17

460 07 Liberec 3

Valbek

Ing. J. VANCL

Ing. J. VANCL

Ing. D. LANDA

I/16 MLADÁ BOLESLAV - MARTINOVICE

PODÉLNÝ PROFIL Č. 8 - VĚTEV H, H1, H2

3.8

Zak. číslo 21-Li13-001

Datum 02/2025

Stupeň PDPS

Počet formátů 9 x A4

Měřitko 1 : 1000/100

Č. přílohy Paré