




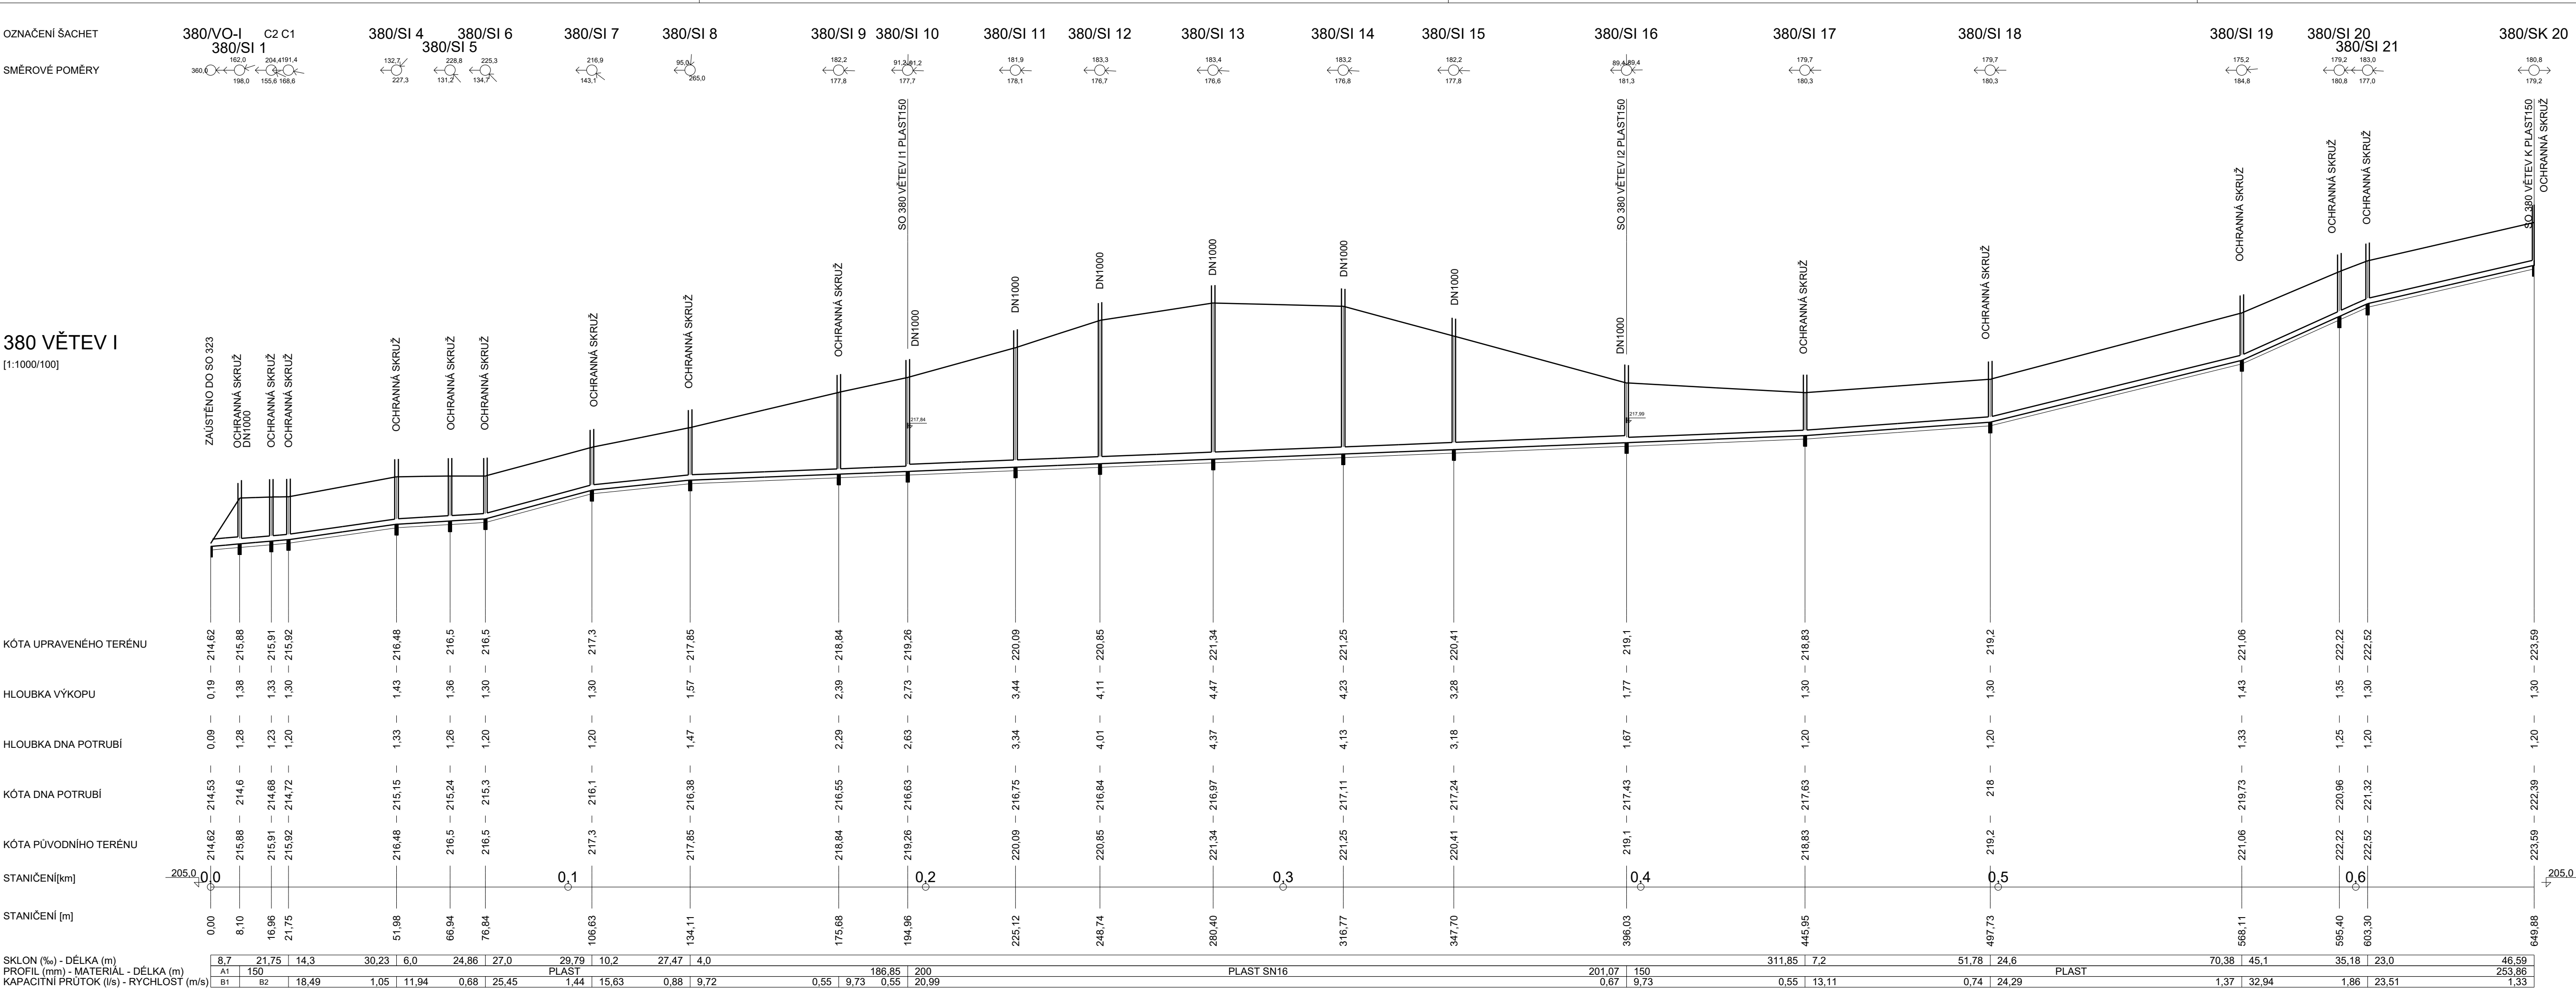

PROFIL (mm) - MATERIÁL - DÉLKA (m)
A1 200, PLAST SN16, 8,10
KAPACITNÍ PRŮTOK (l/s) - RYCHLOST (m/s)
B1 31,05, 0,99
B2 14,40, 0,81
OZNAČENÍ ŠACHET
C1 380/SI 3
C2 380/SI 2

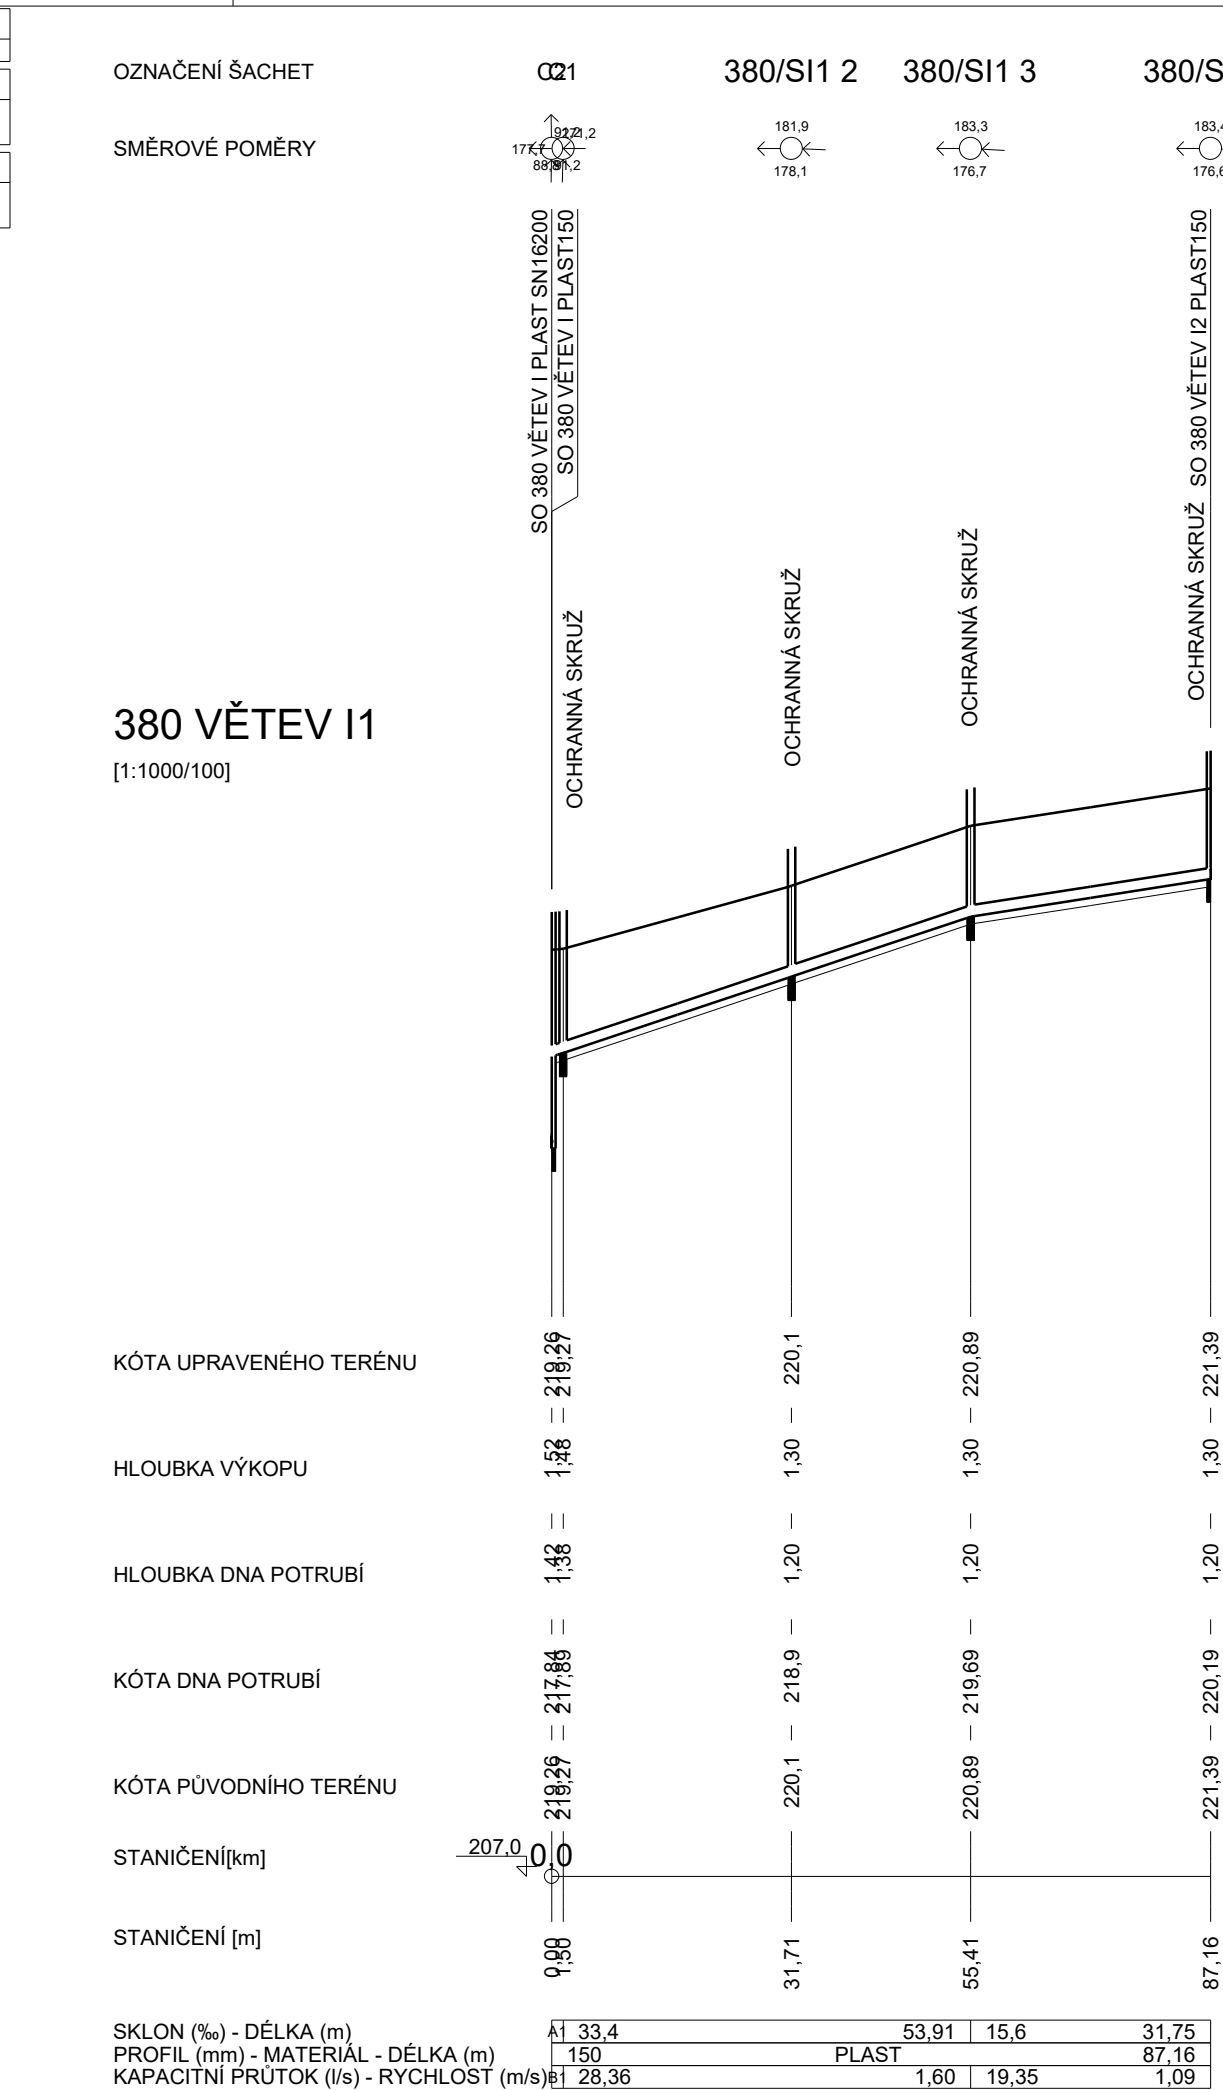

SKLON (‰) - DÉLKA (m)
A1 33,5, 1,50
KAPACITNÍ PRŮTOK (l/s) - RYCHLOST (m/s)
B1 28,37, 1,61
OZNAČENÍ ŠACHET
C1 380/SI1 1
C2 380/SI 10

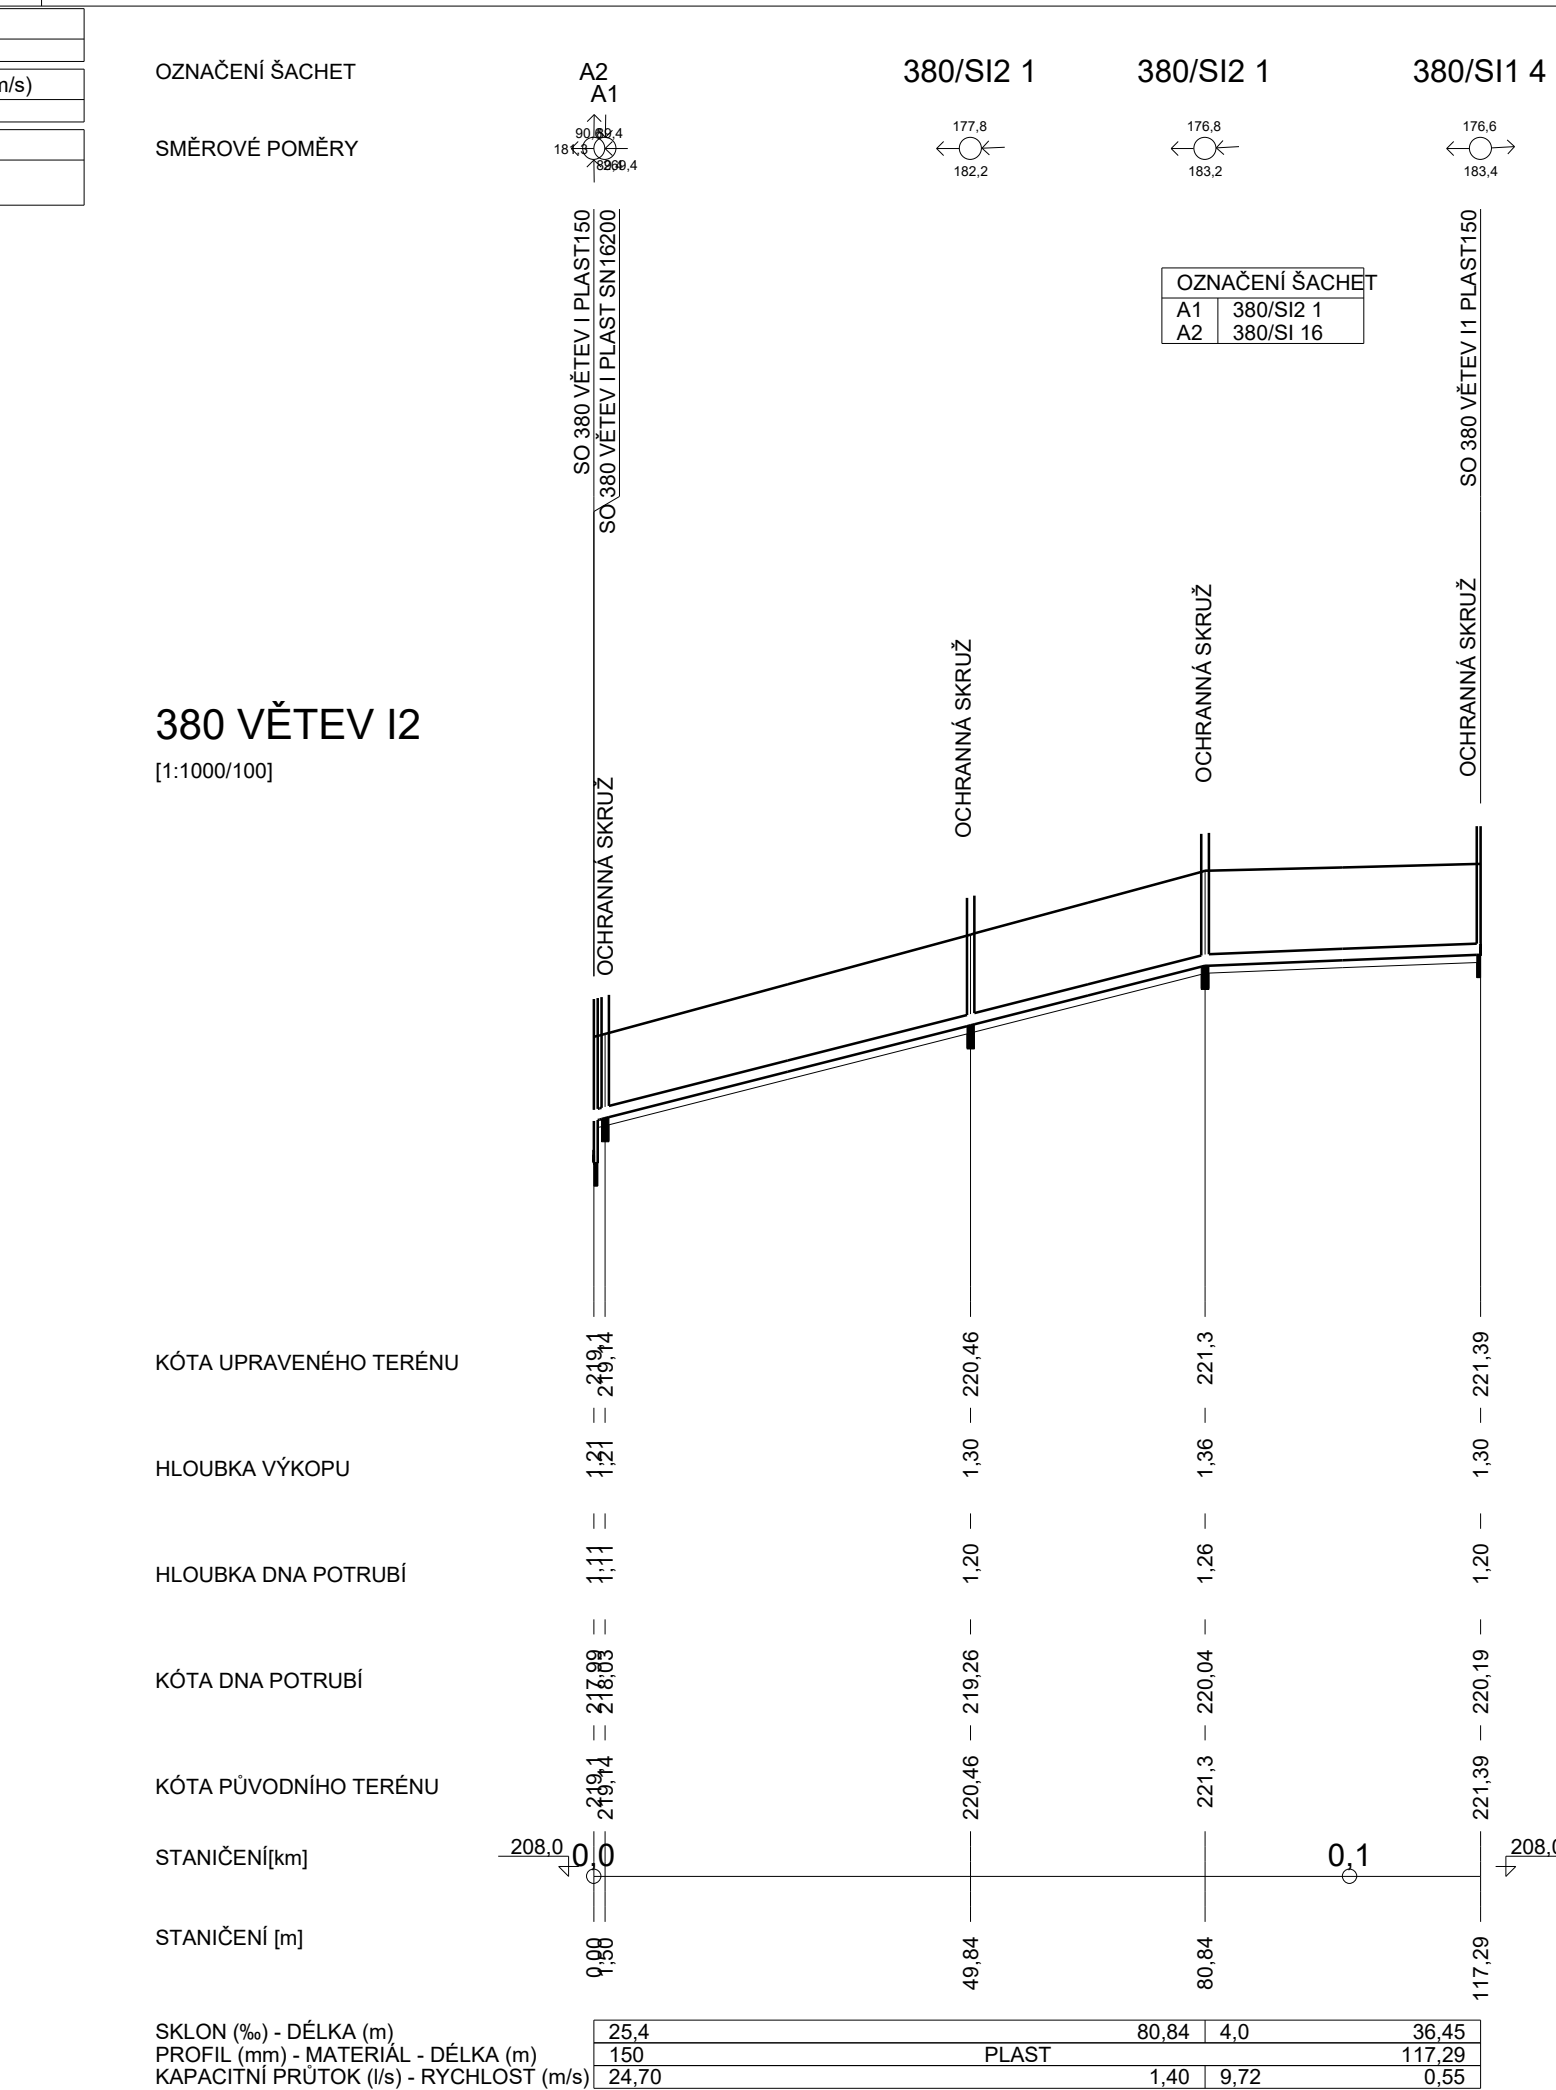

Souřadnicový systém: S-JTSK

Výškový systém: Bpv

SO 380 Úpravy meliorací

Objednatel:

Ředitelství silnic a dálnic

Ředitelství silnic a dálnic s. p.

Čerčanská 2023/12, Krč, 140 00 Praha 4

Zhotovitel:

Valbek, spol. s r.o.

Vaňurova 505/17

460 07 Liberec 3

Valbek

Vypracoval

ING. J. VANCL

Zodp. projektant

ING. J. VANCL

Tech. kontrola

ING. D. LANDA

Akce

I/16 MLADÁ BOLESLAV - MARTINOVICE

Příloha

PODÉLNÝ PROFIL Č. 9 - VĚTEV I, II, I2

Zak. číslo

21-L13-001

Datum

02/2025

Stupeň

PDPs

Počet formátů

8 x A4

Měřítka

1 : 1000/100

Č. přílohy

Paré

3.9

Zhotovitel:

Valbek, spol. s r.o.

Vaňurova 505/17

460 07 Liberec 3